


Для исполнений ЮНИТ-М300-ДЗТ2

Устройство резервирования отказа выключателя стороны ВН (УРОВ ВН) (ТРВВRF)

Устройство резервирования при отказе выключателя (УРОВ) (TPRBRF) RBRF1

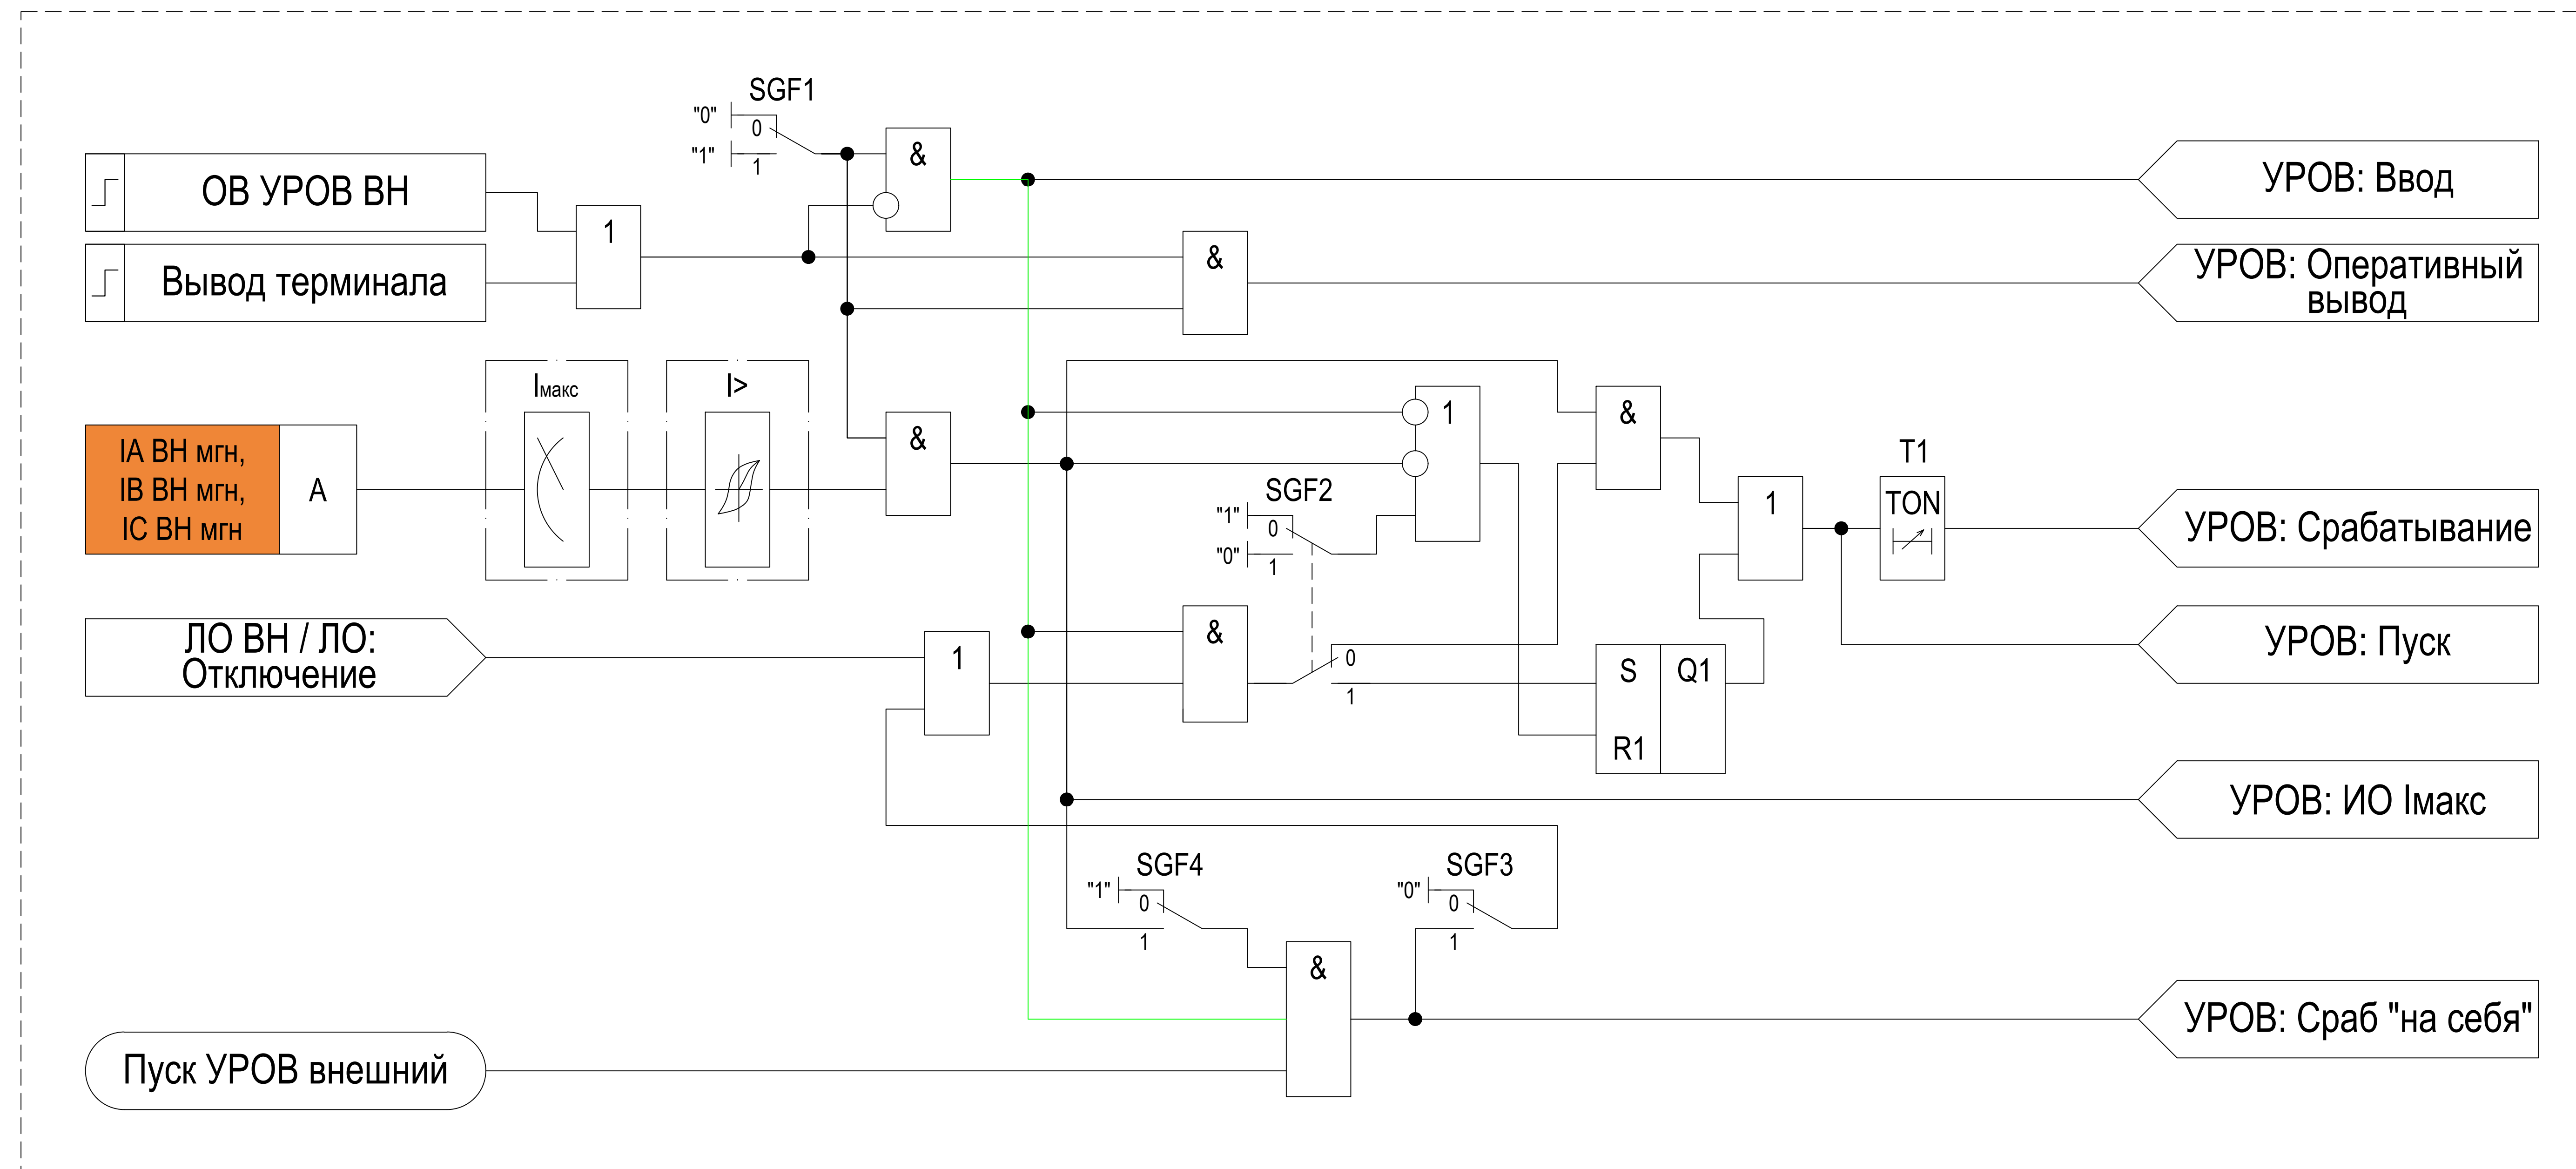

SGF1 - Ввод функции в работу (Не предусмотрено/ Предусмотрено)

SGF2 - УРОВ с подхватом по току (Не предусмотрено/ Предусмотрено)

SGF3 - Действие внешнего УРОВ на вышестоящий выключатель (Не предусмотрено/ Предусмотрено)

SGF4 - Контроль по току при действии "на себя" (Не предусмотрено/ Предусмотрено)