

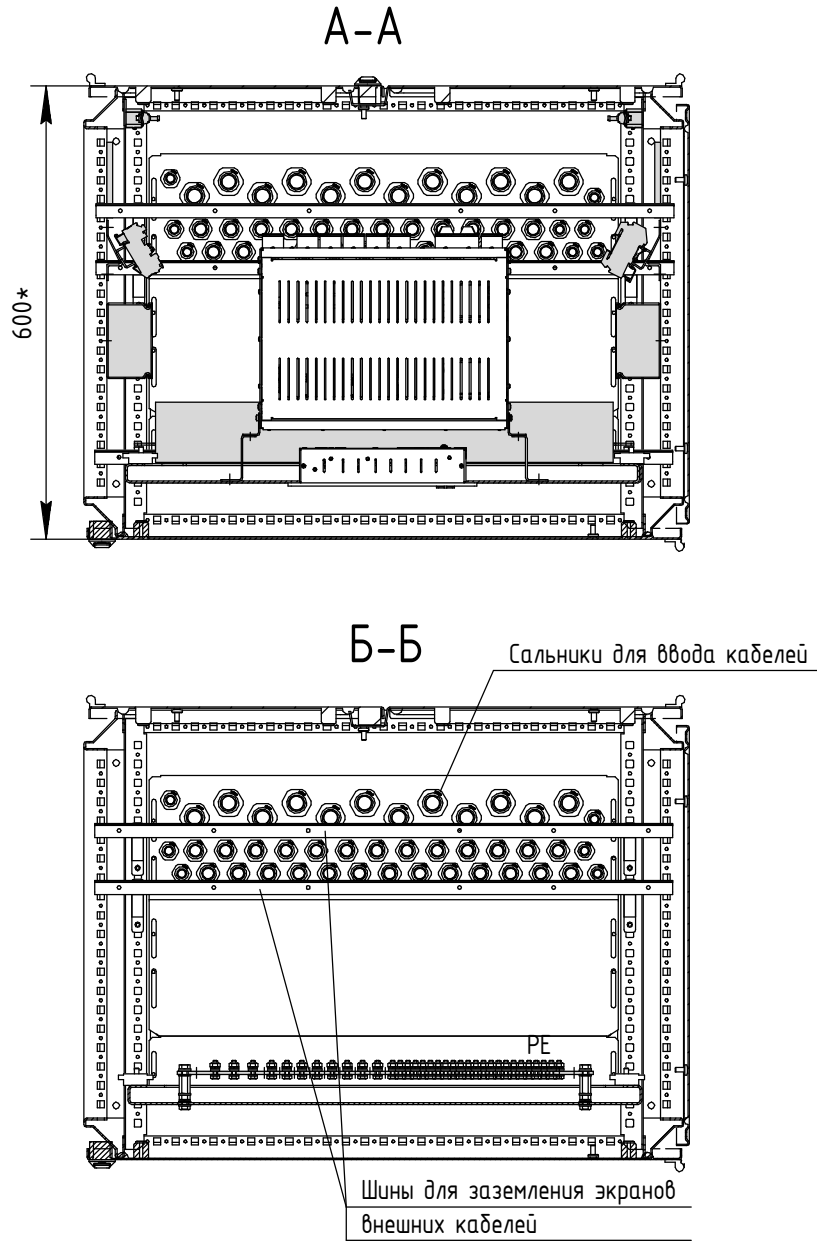


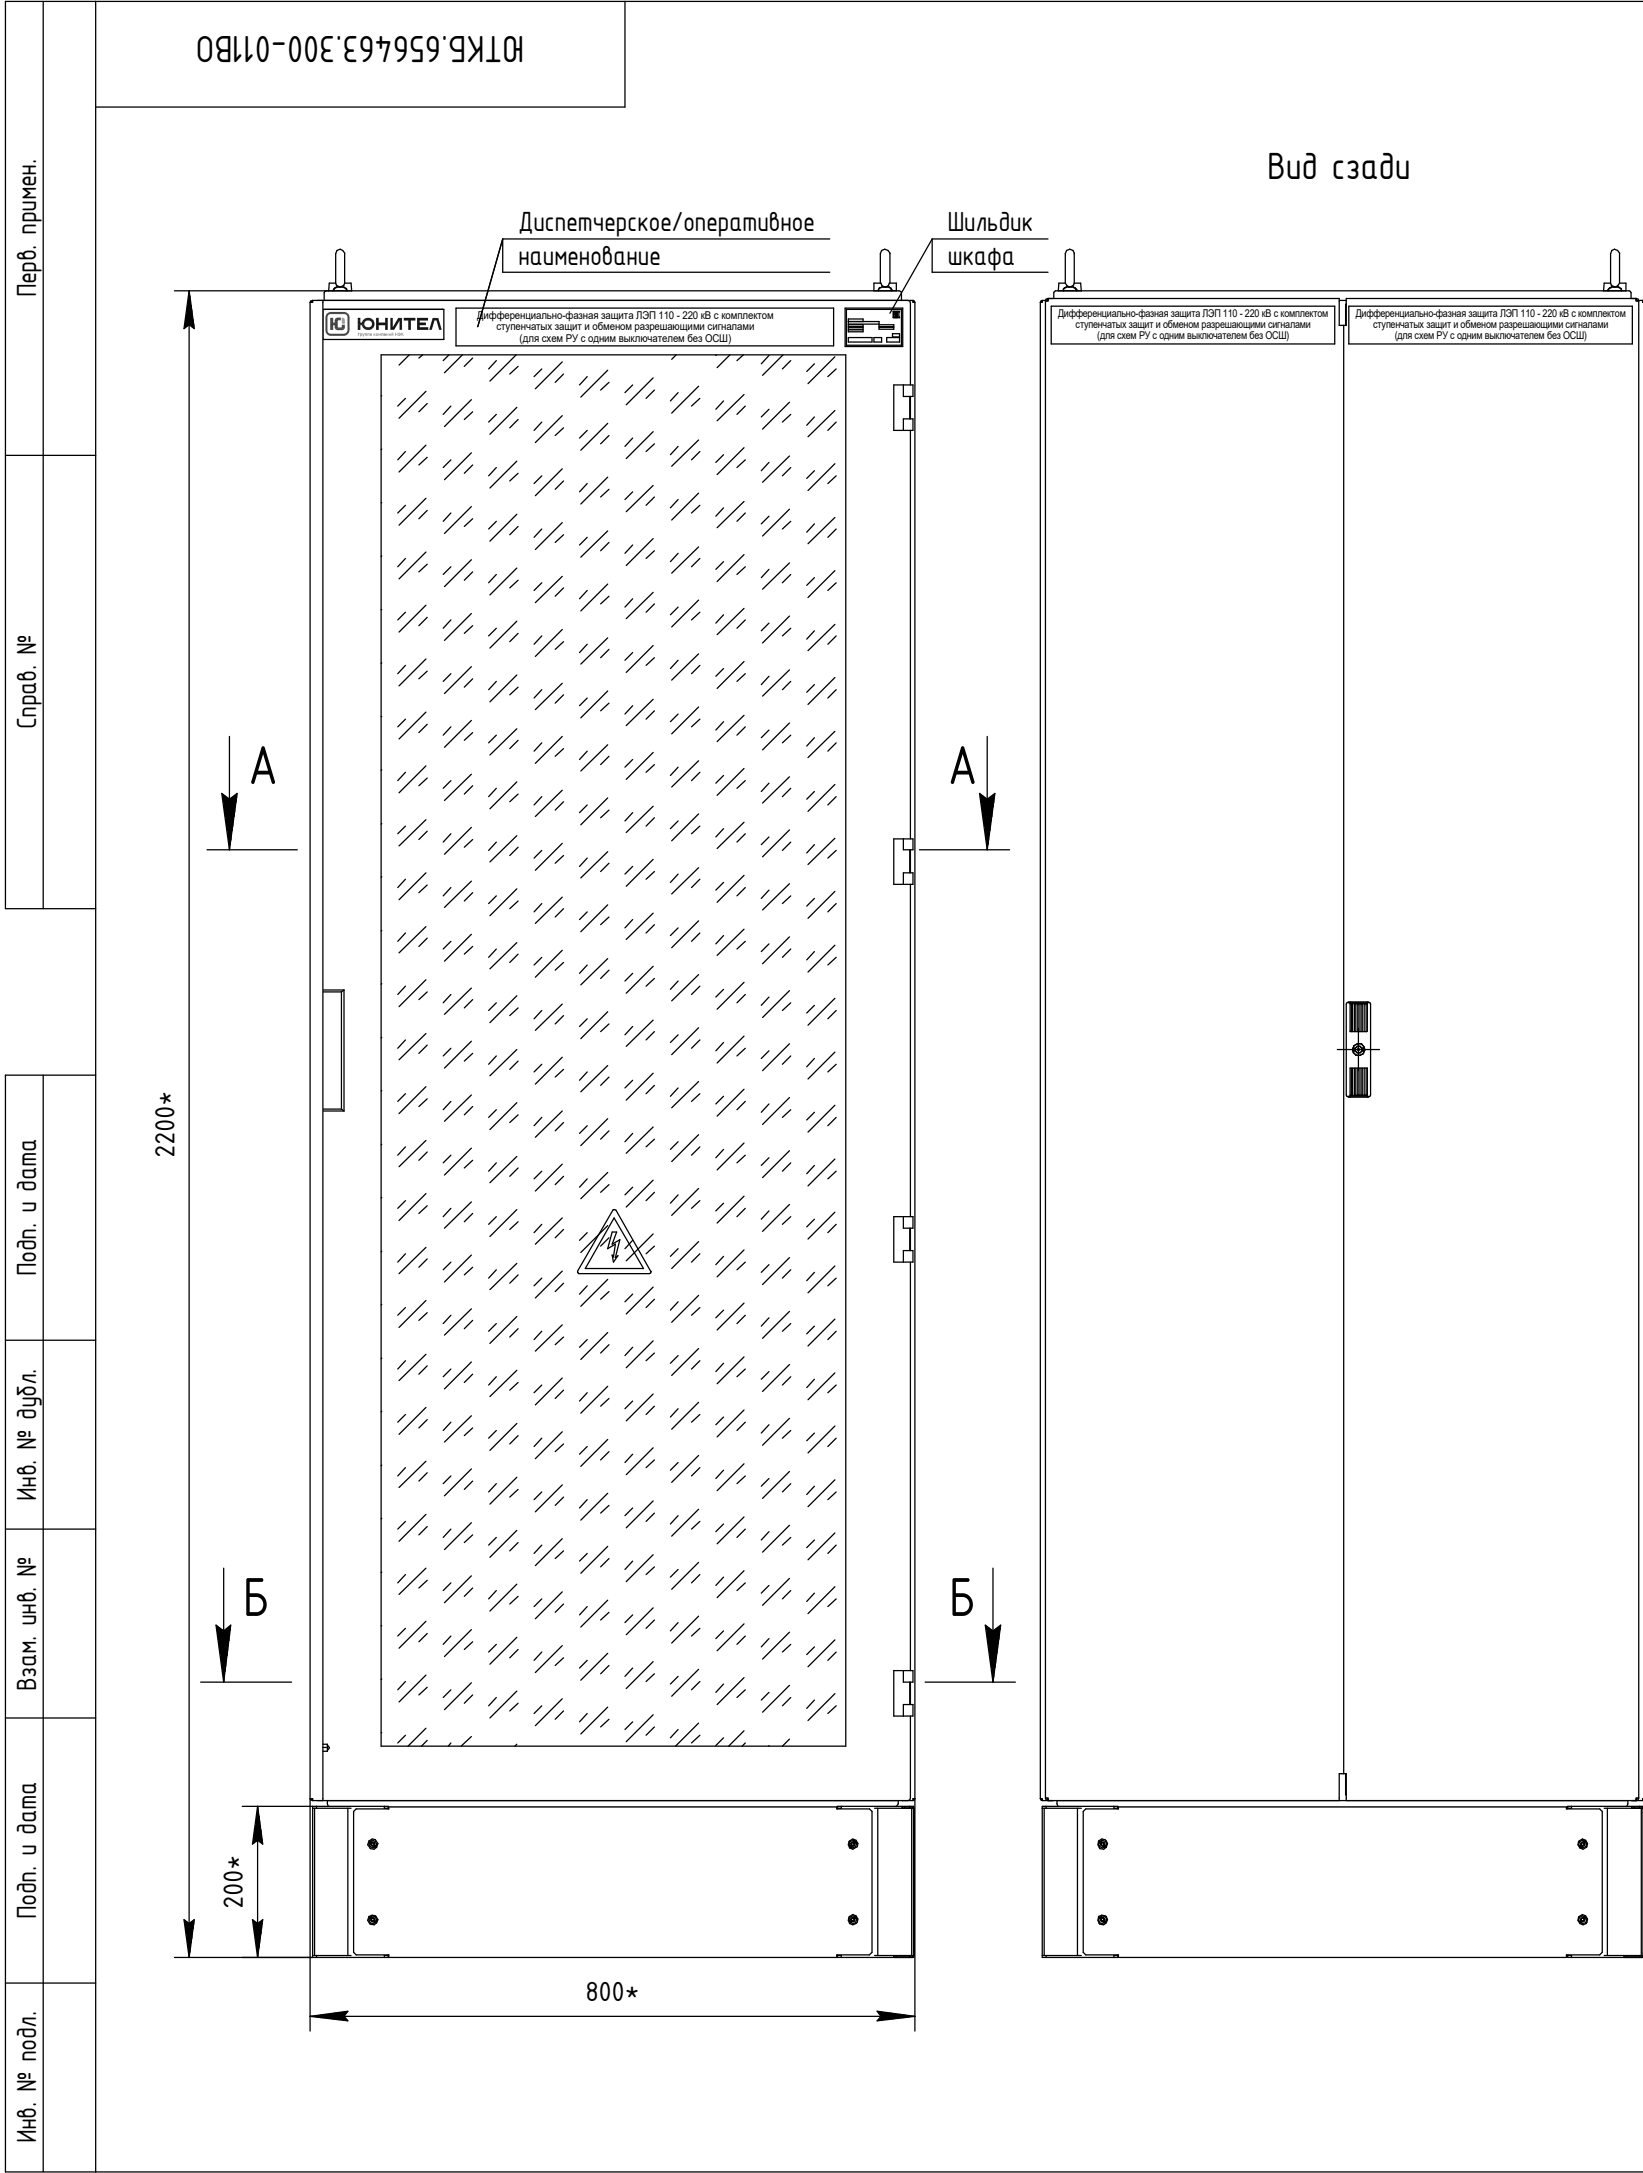


- 1 \* Указаны типовые габариты шкафов. Фактические размеры металлоконструкции могут отличаться в пределах +10 мм. Размеры даны без учета выступающих частей (ручек, петель и т.д.).
- 2 \*\* Указана расчетная масса изделия. Фактическая масса изделия определяется взвешиванием.
- 3 Общие допуски ± IT14/2 по ГОСТ 30893.1-2002.
- 4 Степень защиты шкафа IP54.
- 5 Подвод внешних кабелей снизу.
- 6 Монтаж оборудования в шкафу выполнить по нормам фирмы-изготовителя.
- 7 Позиционные обозначения аппаратов соответствуют перечню элементов ЮТКБ.656463.300-012ПЭЗ.

|          |              |          |       |            |   |        |          |         |
|----------|--------------|----------|-------|------------|---|--------|----------|---------|
|          |              |          |       |            | ЮТКБ.656463.300-011В0   |        |          |         |
|          |              |          |       |            | Шкаф дифференциально-фазной защиты ЛЭП 110 - 220 кВ с комплектом ступенчатых защит и обменом разрешающими сигналами (для схем РУ с одним выключателем без ОСШ)<br>ШЭТ 220.01-0-ЮИРЗ<br>Чертеж общего вида | Лист   | Масса    | Масштаб |
| Изм.     | Лист         | № докум. | Подп. | Дата       |   | 0      | 200**    | 1:10    |
| Разраб.  | Александрова |          |       | 19.05.2026 |   |        |          |         |
| Пров.    | Черемисова   |          |       | 19.05.2026 |   | Лист 1 | Листов 2 |         |
|          |              |          |       |            |   |        |          |         |
| Н.контр. |              |          |       |            |   |        |          |         |
| Утв.     | Ильин        |          |       | 19.05.2026 |   |        |          |         |


Вид спереди  
Дверь условно не показана

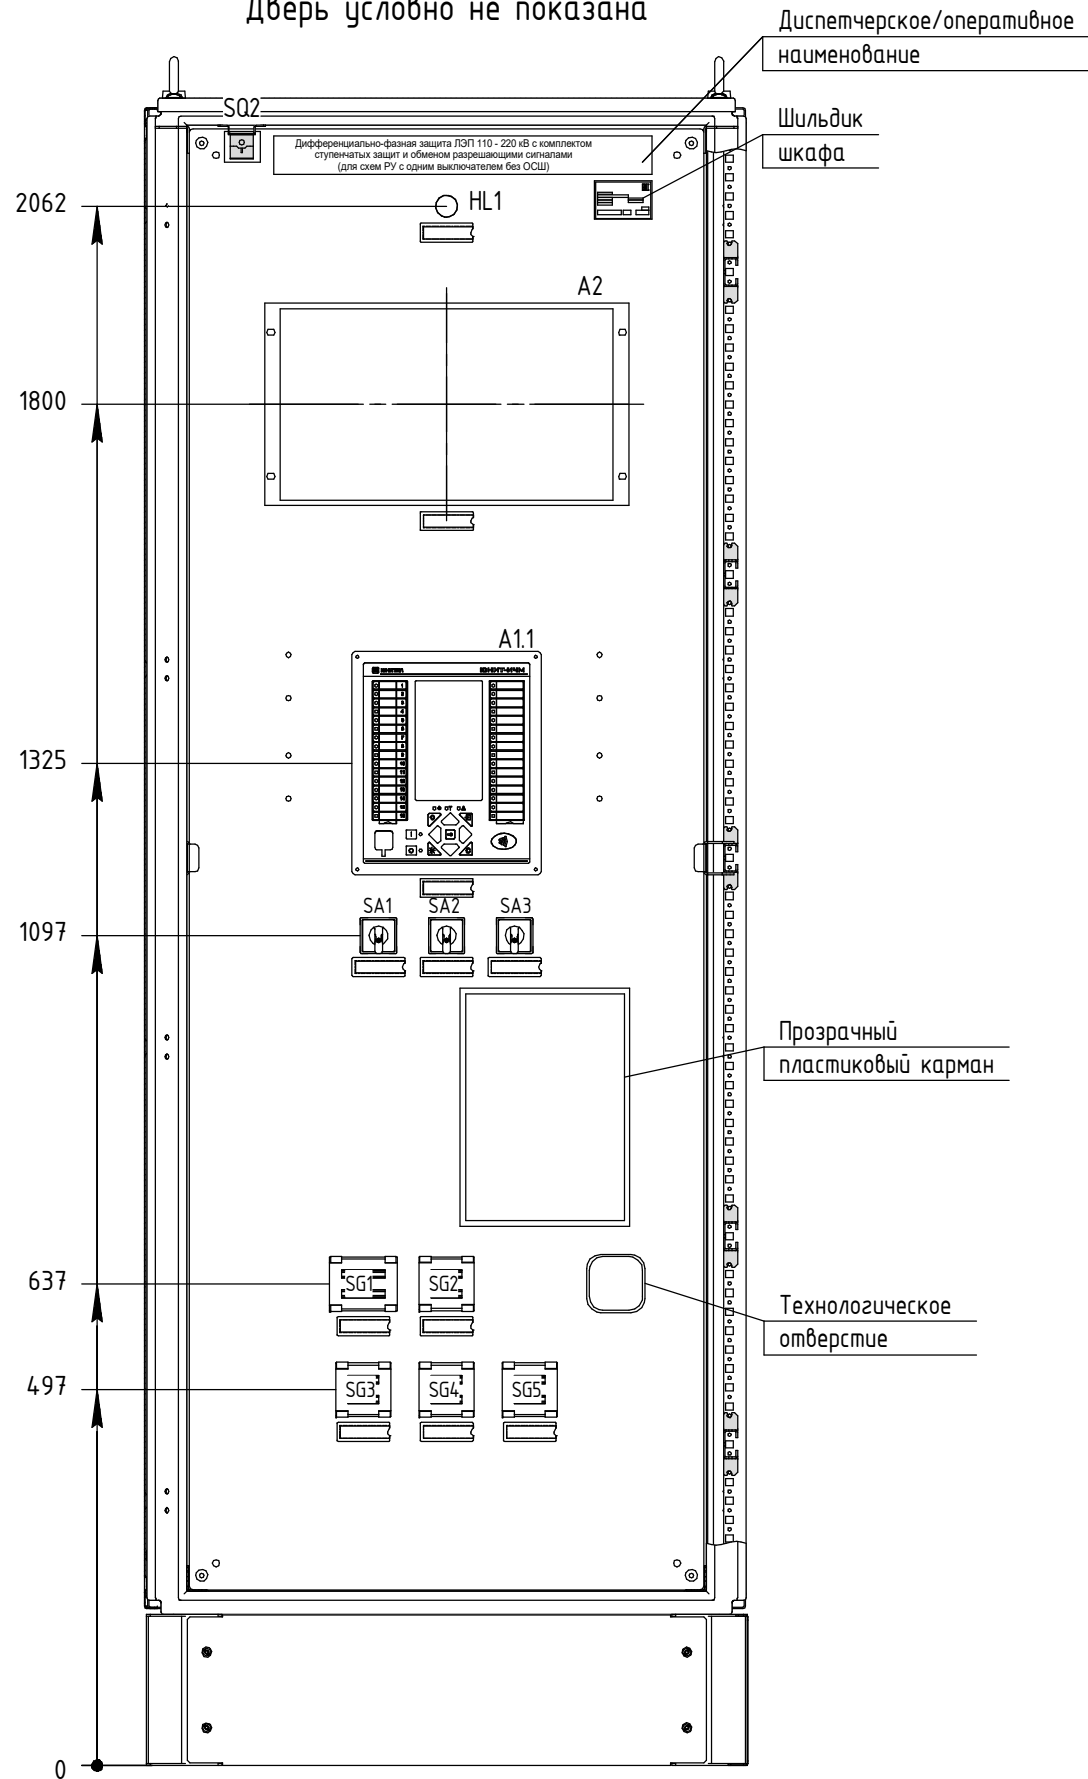


┌-┐

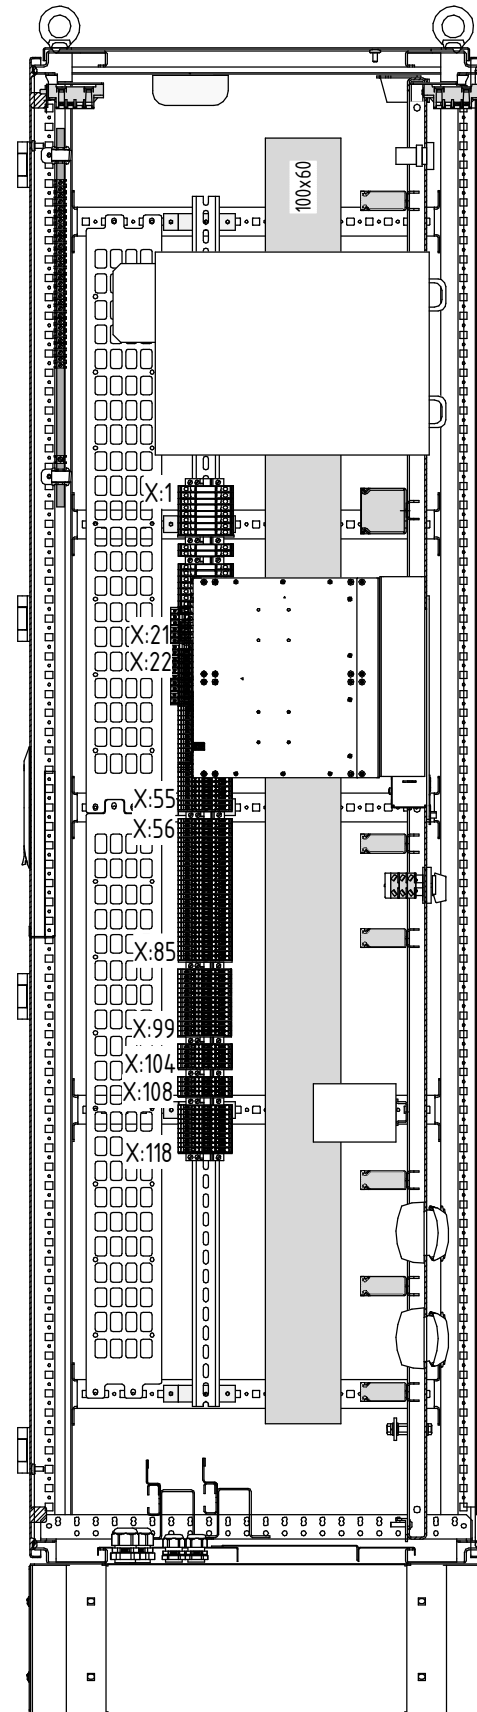

Вид сзади  
Дверь, ряды зажимов и вертикальные короба  
условно не показаны

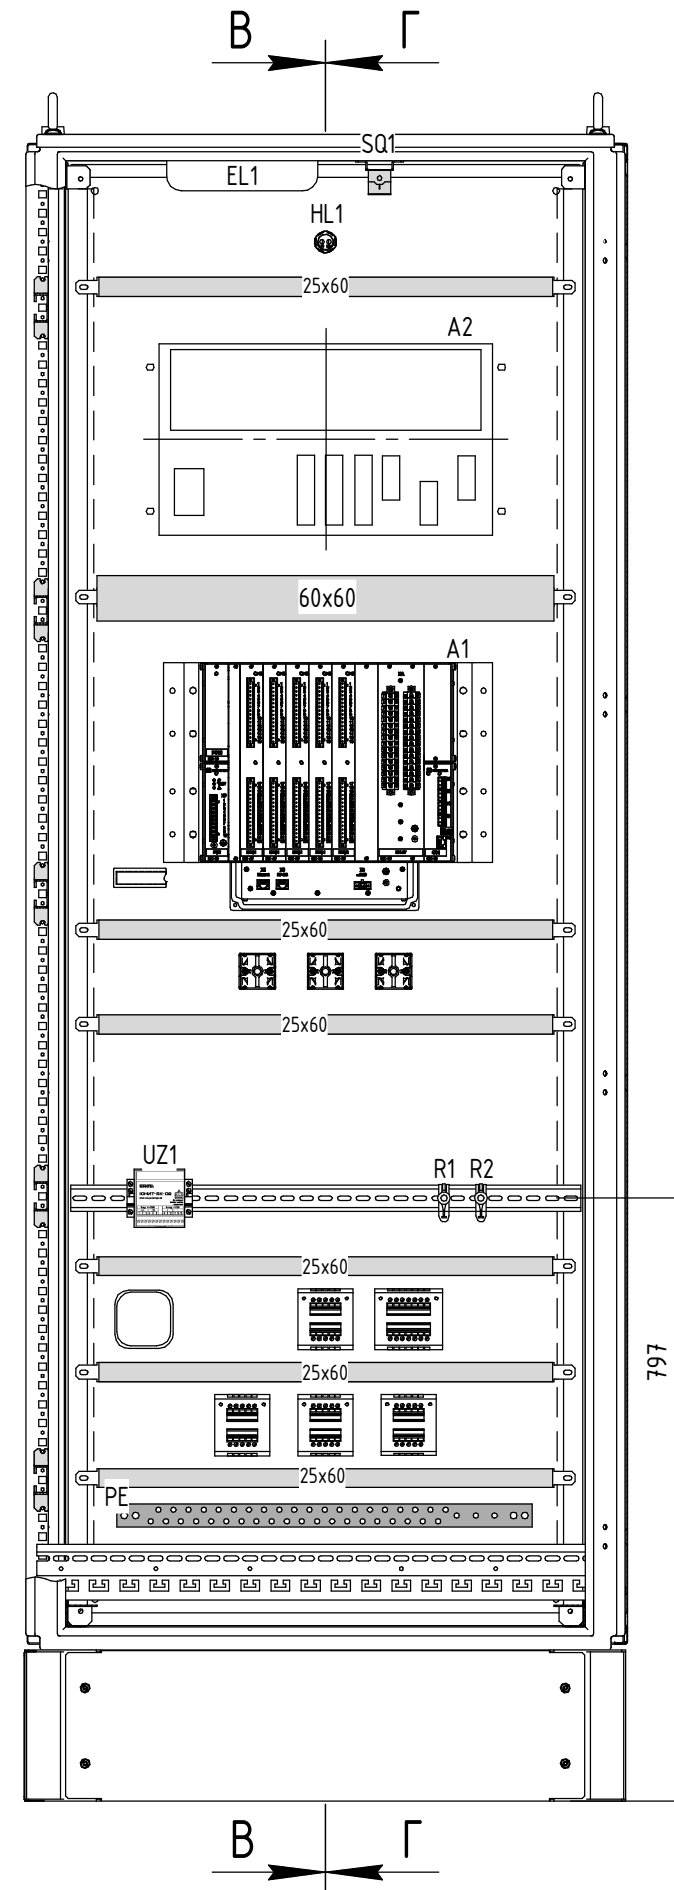

B-B

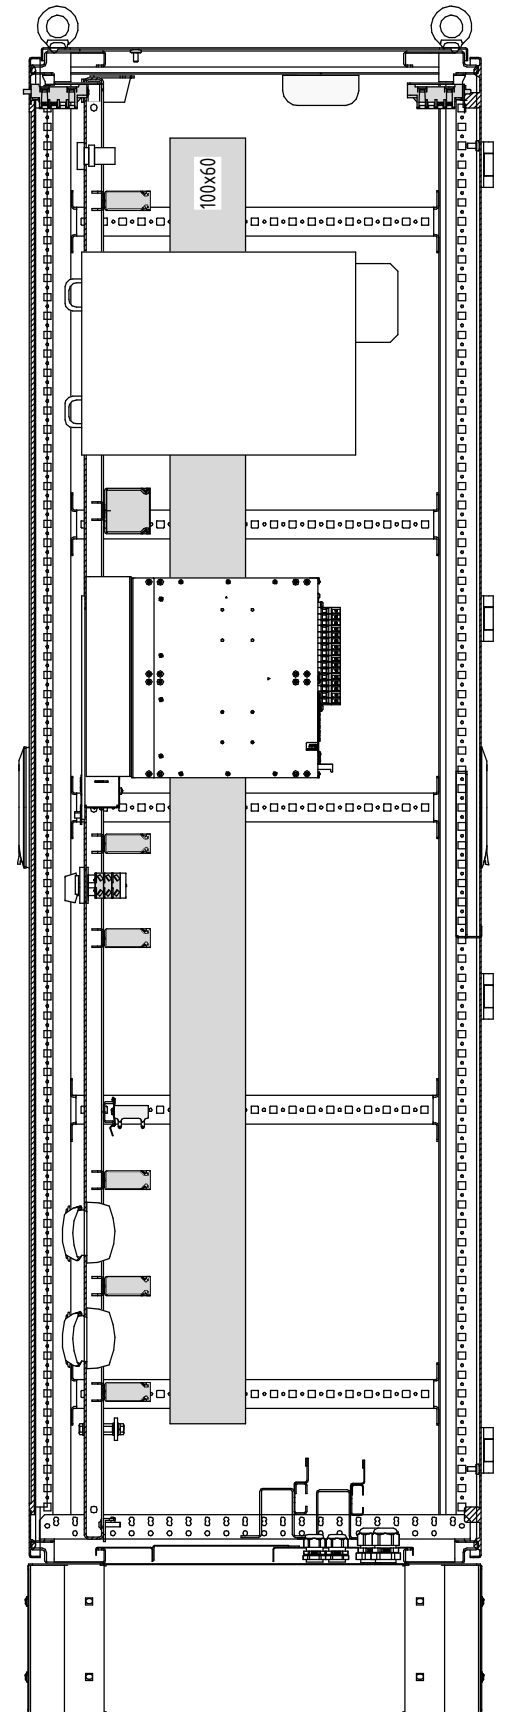

| Инв. № подл. | Подп. и дата | Взам. инв. № | Инв. № дубл. | Подп. и дата |
|--------------|--------------|--------------|--------------|--------------|
|              |              |              |              |              |

|      |      |          |       |     |
|------|------|----------|-------|-----|
| Изм. | Лист | № докум. | Подп. | Дат |
|------|------|----------|-------|-----|

ЮТКБ.656463.300-011В0

|      |
|------|
| Лист |
| 2    |