


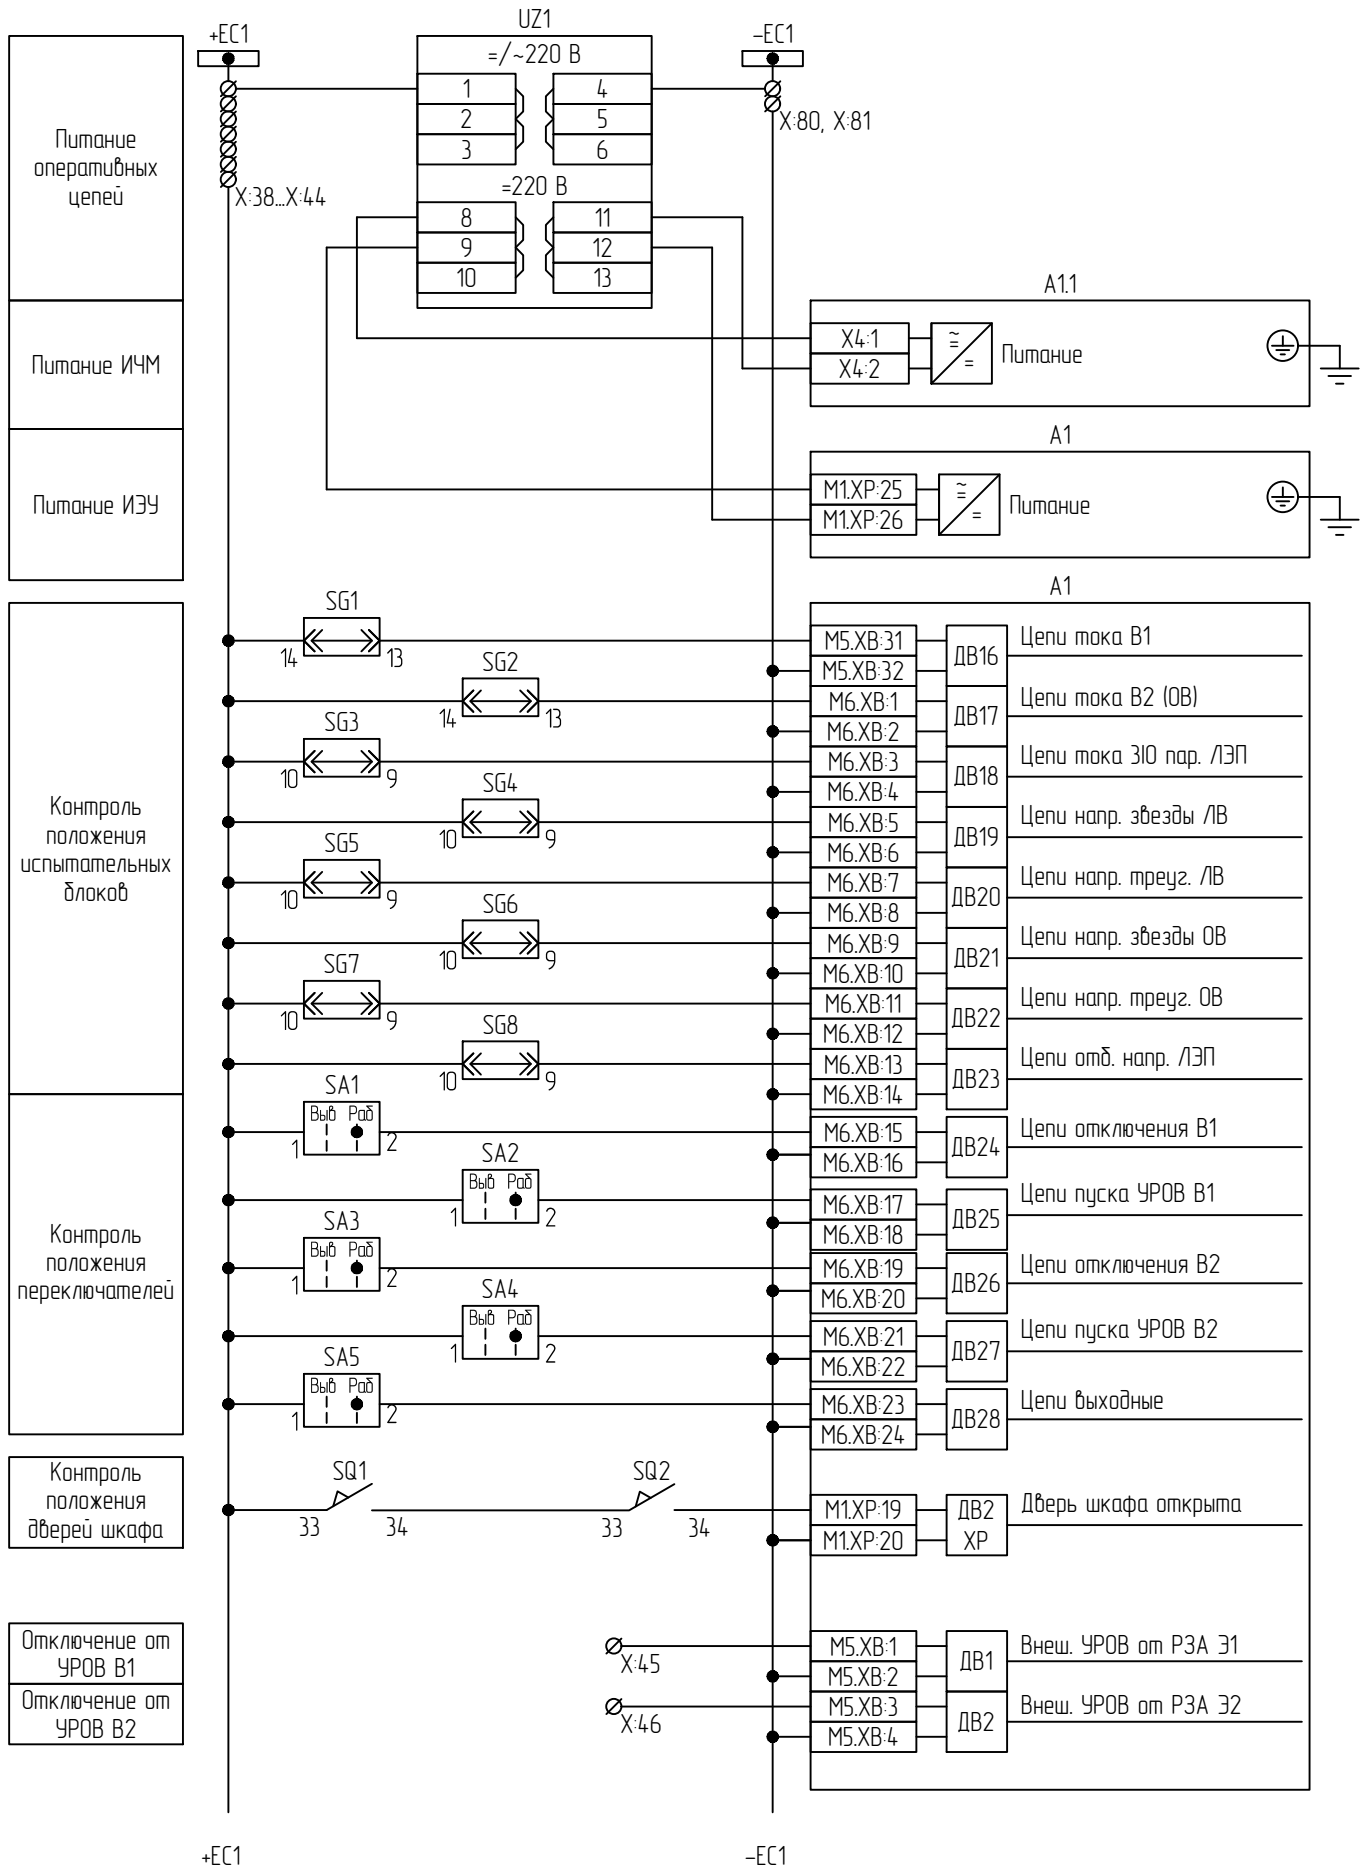

РПВ В1
РПО В1
ЗНФ В1
РПВ В2
РПО В2
ЗНФ В2
РПВ В3
Ускор. от защит парал. линии
РПВ ШСВ
Прием ТО
Прием ТУ ОТФ
Прием ТУ ДЗ
Прием ТУ ТНЗНП

