




Выходные цепи

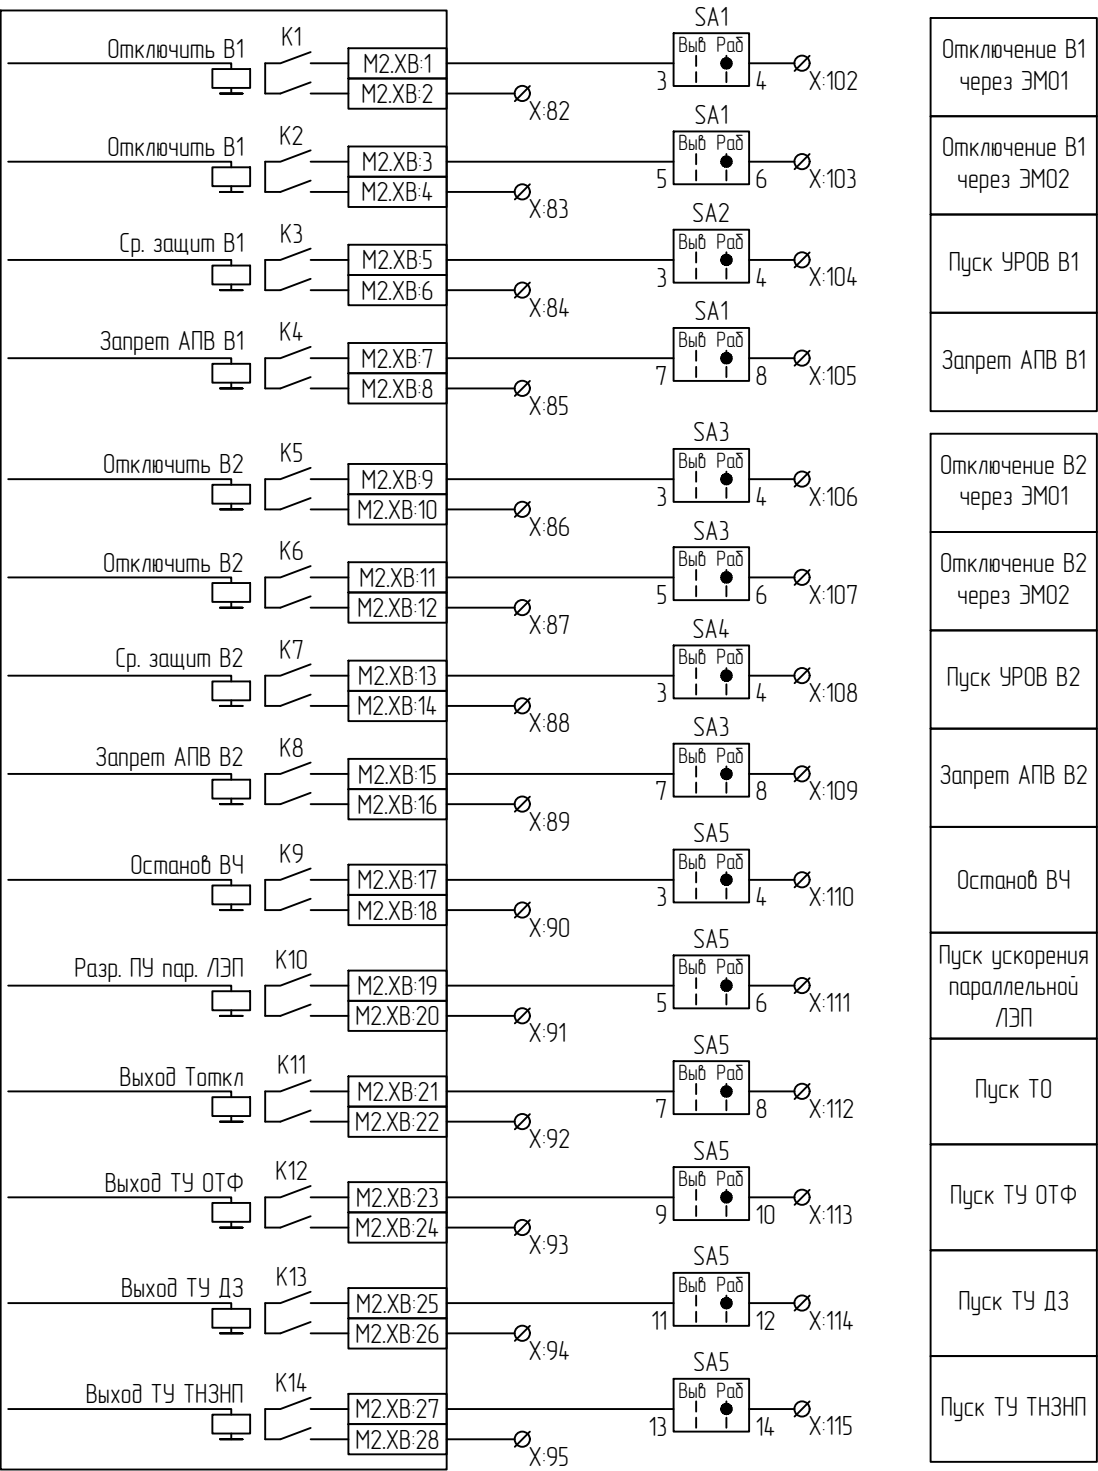


Цепи сигнализации

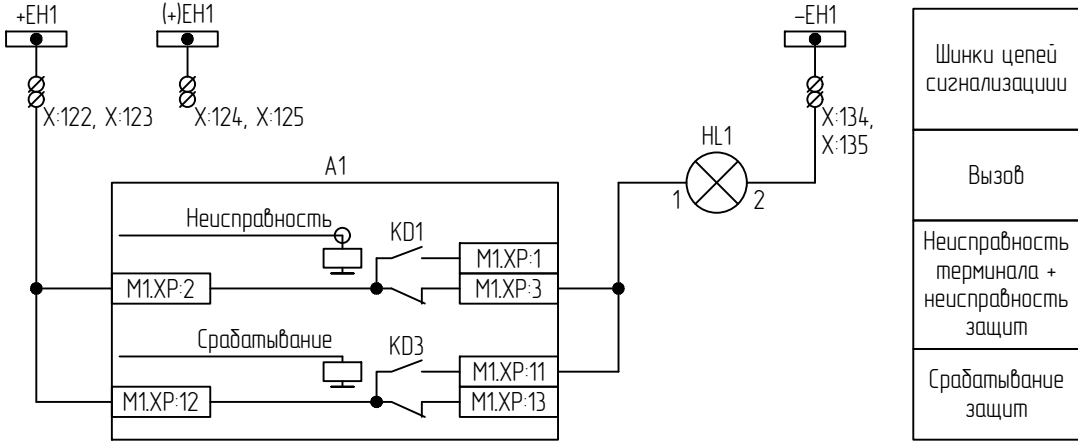


Цепи РАС

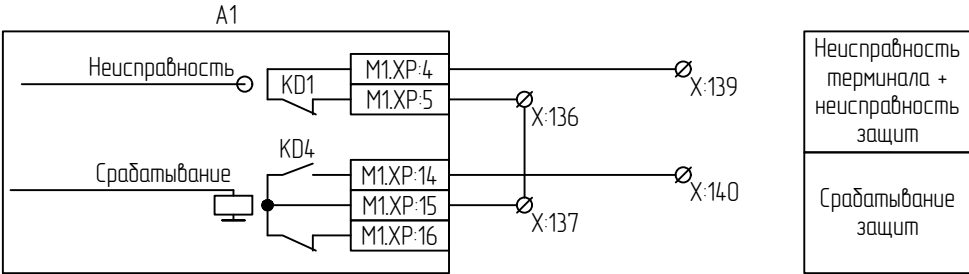

Цепи портов связи терминала

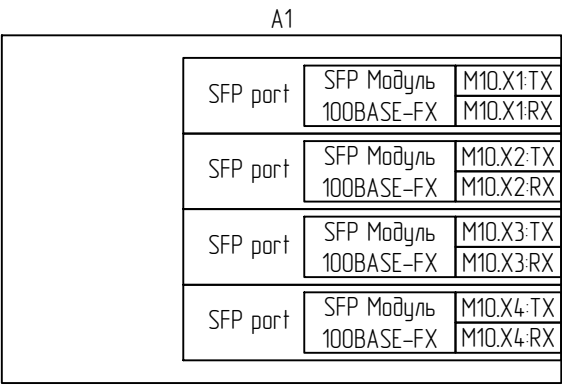

Цепи связи терминала с ИЧМ

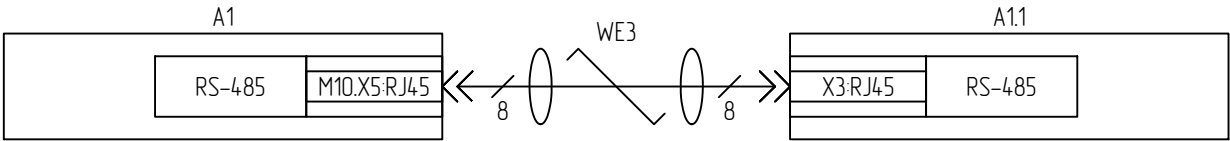

Цепи освещения шкафа

