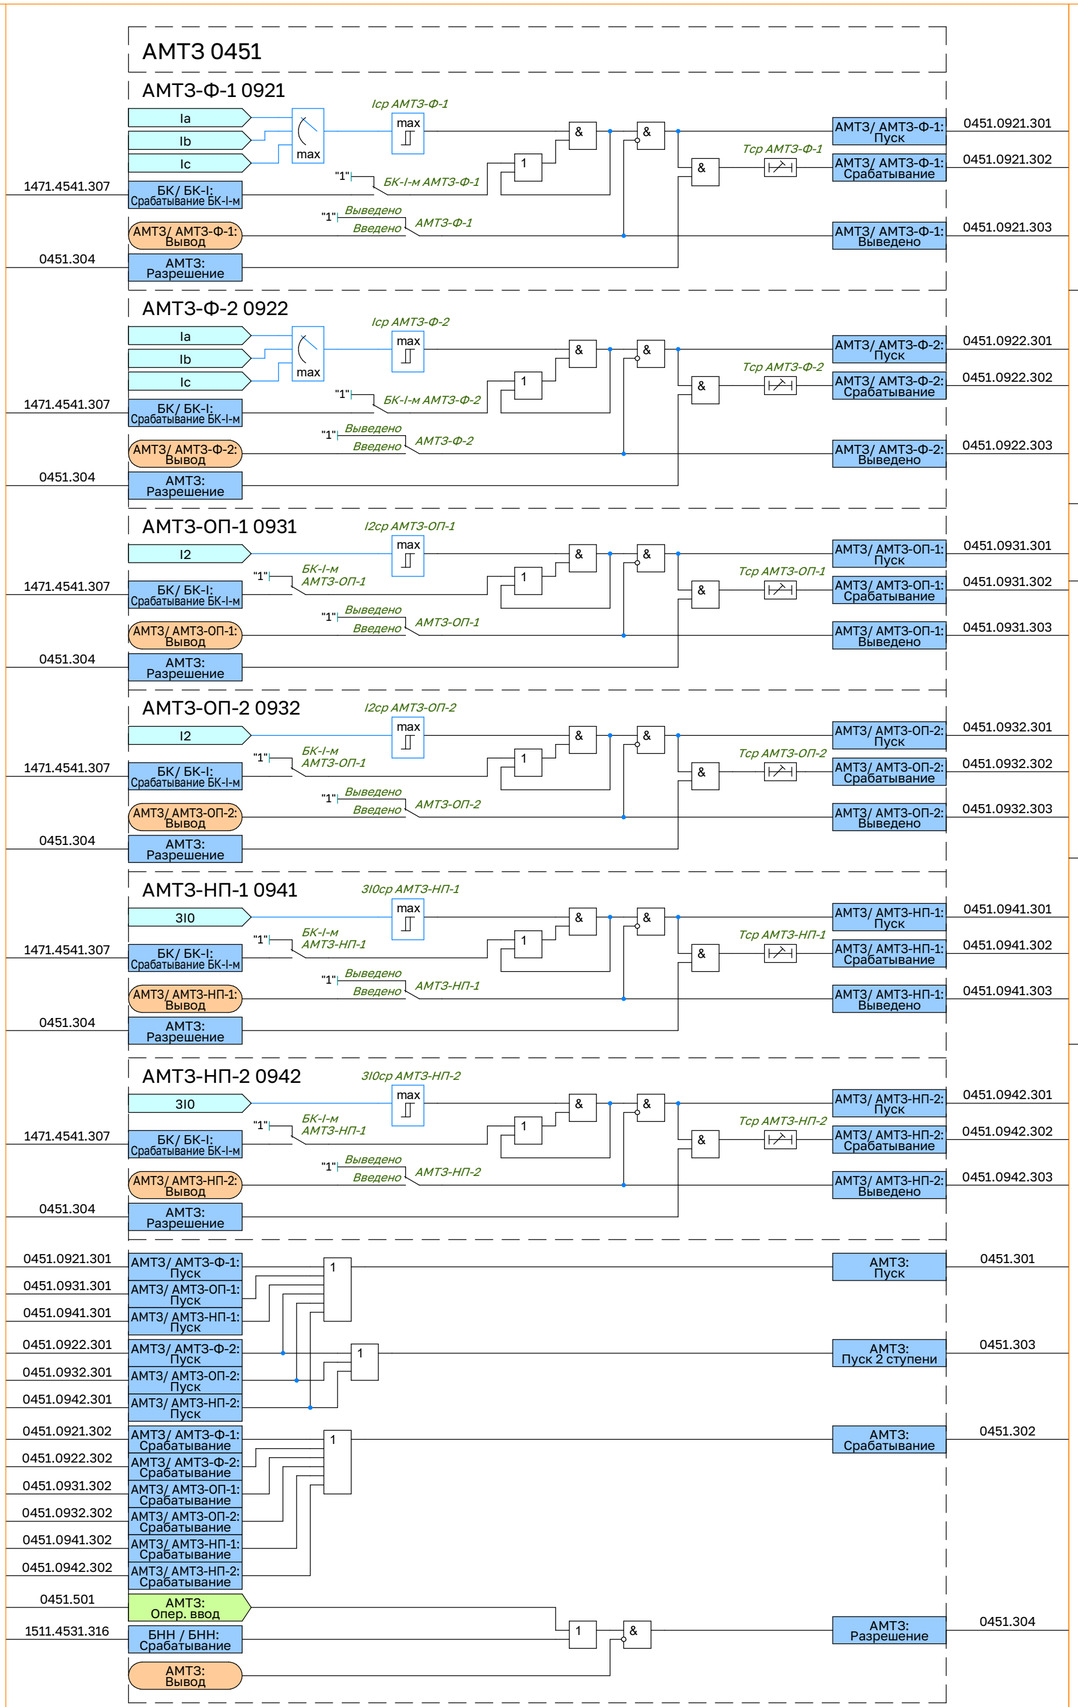
АМТЗ 0451
АМТЗ-Ф-1 0921
Ia
Ib
Ic
max
Iср АМТЗ-Ф-1
max
1471.4541.307
БК/ БК-I: Срабатывание БК-I-м
"1"
БК-I-м АМТЗ-Ф-1
1
&
&
&
Tср АМТЗ-Ф-1
АМТЗ/ АМТЗ-Ф-1: Пуск
0451.0921.301
АМТЗ/ АМТЗ-Ф-1: Срабатывание
0451.0921.302
"1"
Выведено
Введено
АМТЗ-Ф-1
АМТЗ/ АМТЗ-Ф-1: Вывод
АМТЗ/ АМТЗ-Ф-1: Выведено
0451.0921.303
0451.304
АМТЗ: Разрешение
АМТЗ-Ф-2 0922
Ia
Ib
Ic
max
Iср АМТЗ-Ф-2
max
1471.4541.307
БК/ БК-I: Срабатывание БК-I-м
"1"
БК-I-м АМТЗ-Ф-2
1
&
&
&
Tср АМТЗ-Ф-2
АМТЗ/ АМТЗ-Ф-2: Пуск
0451.0922.301
АМТЗ/ АМТЗ-Ф-2: Срабатывание
0451.0922.302
"1"
Выведено
Введено
АМТЗ-Ф-2
АМТЗ/ АМТЗ-Ф-2: Вывод
АМТЗ/ АМТЗ-Ф-2: Выведено
0451.0922.303
0451.304
АМТЗ: Разрешение
АМТЗ-ОП-1 0931
I2
max
I2ср АМТЗ-ОП-1
max
1471.4541.307
БК/ БК-I: Срабатывание БК-I-м
"1"
БК-I-м АМТЗ-ОП-1
1
&
&
&
Tср АМТЗ-ОП-1
АМТЗ/ АМТЗ-ОП-1: Пуск
0451.0931.301
АМТЗ/ АМТЗ-ОП-1: Срабатывание
0451.0931.302
"1"
Выведено
Введено
АМТЗ-ОП-1
АМТЗ/ АМТЗ-ОП-1: Вывод
АМТЗ/ АМТЗ-ОП-1: Выведено
0451.0931.303
0451.304
АМТЗ: Разрешение
АМТЗ-ОП-2 0932
I2
max
I2ср АМТЗ-ОП-2
max
1471.4541.307
БК/ БК-I: Срабатывание БК-I-м
"1"
БК-I-м АМТЗ-ОП-1
1
&
&
&
Tср АМТЗ-ОП-2
АМТЗ/ АМТЗ-ОП-2: Пуск
0451.0932.301
АМТЗ/ АМТЗ-ОП-2: Срабатывание
0451.0932.302
"1"
Выведено
Введено
АМТЗ-ОП-2
АМТЗ/ АМТЗ-ОП-2: Вывод
АМТЗ/ АМТЗ-ОП-2: Выведено
0451.0932.303
0451.304
АМТЗ: Разрешение
АМТЗ-НП-1 0941
3I0
max
3I0ср АМТЗ-НП-1
max
1471.4541.307
БК/ БК-I: Срабатывание БК-I-м
"1"
БК-I-м АМТЗ-НП-1
1
&
&
&
Tср АМТЗ-НП-1
АМТЗ/ АМТЗ-НП-1: Пуск
0451.0941.301
АМТЗ/ АМТЗ-НП-1: Срабатывание
0451.0941.302
"1"
Выведено
Введено
АМТЗ-НП-1
АМТЗ/ АМТЗ-НП-1: Вывод
АМТЗ/ АМТЗ-НП-1: Выведено
0451.0941.303
0451.304
АМТЗ: Разрешение
АМТЗ-НП-2 0942
3I0
max
3I0ср АМТЗ-НП-2
max
1471.4541.307
БК/ БК-I: Срабатывание БК-I-м
"1"
БК-I-м АМТЗ-НП-1
1
&
&
&
Tср АМТЗ-НП-2
АМТЗ/ АМТЗ-НП-2: Пуск
0451.0942.301
АМТЗ/ АМТЗ-НП-2: Срабатывание
0451.0942.302
"1"
Выведено
Введено
АМТЗ-НП-2
АМТЗ/ АМТЗ-НП-2: Вывод
АМТЗ/ АМТЗ-НП-2: Выведено
0451.0942.303
0451.304
АМТЗ: Разрешение
0451.0921.301
АМТЗ/ АМТЗ-Ф-1: Пуск
0451.0931.301
АМТЗ/ АМТЗ-ОП-1: Пуск
0451.0941.301
АМТЗ/ АМТЗ-НП-1: Пуск
1
АМТЗ: Пуск
0451.301
0451.0922.301
АМТЗ/ АМТЗ-Ф-2: Пуск
0451.0932.301
АМТЗ/ АМТЗ-ОП-2: Пуск
0451.0942.301
АМТЗ/ АМТЗ-НП-2: Пуск
1
АМТЗ: Пуск 2 ступени
0451.303
0451.0921.302
АМТЗ/ АМТЗ-Ф-1: Срабатывание
0451.0922.302
АМТЗ/ АМТЗ-Ф-2: Срабатывание
0451.0931.302
АМТЗ/ АМТЗ-ОП-1: Срабатывание
0451.0932.302
АМТЗ/ АМТЗ-ОП-2: Срабатывание
0451.0941.302
АМТЗ/ АМТЗ-НП-1: Срабатывание
0451.0942.302
АМТЗ/ АМТЗ-НП-2: Срабатывание
1
АМТЗ: Срабатывание
0451.302
0451.501
АМТЗ: Опер. ввод
1511.4531.316
БНН / БНН: Срабатывание
1
&
АМТЗ: Разрешение
0451.304
АМТЗ: Вывод
КПОН 0541
КПОН СШ 0811
U2
max
U2 КПОН СШ
max
Тип КПОН СШ
Umin, U2
Umin
1
&
1
&
КПОН/ КПОН СШ: Пуск
0541.0811.301
КПОН/ КПОН СШ: Срабатывание
0541.0811.302
Uab
Ubc
Uca
min
Ul КПОН СШ
min
КПОН/ КПОН СШ: Вывод
"1"
Выведено
Введено
КПОН СШ
КПОН/ КПОН СШ: Выведено
0541.0811.302
1511.4531.316
БНН СШ/ БНН: Срабатывание
Неиспр ТН СШ
Выведено
Пуск КПОН
Блок КПОН
КПОН НН 0771
U2 НН
max
U2 КПОН НН
max
Тип КПОН НН
Umin, U2
Umin
Внеш
1
&
1
&
КПОН/ КПОН НН: Пуск
0541.0771.301
КПОН/ КПОН НН: Срабатывание
0541.0771.302
Uab НН
Ubc НН
min
Ul КПОН НН
min
0541.0771.501
КПОН/ КПОН НН: Внешний КПОН
КПОН/ КПОН НН: Вывод
"1"
Выведено
Введено
КПОН НН
КПОН/ КПОН НН: Выведено
0541.0771.303
1961.5121.304
КЦН НН/ КЦН: Срабатывание
Неиспр ТН НН
Выведено
Пуск КПОН
Блок КПОН
КОН 1951
КОН СШ 5221
Uab
Ubc
Uca
min
Ucр КОН СШ
min
&
&
КОН/ КОН СШ: Срабатывание
1951.5221.301
КОН/ КОН СШ: Выведено
1951.5221.302
КОН/ КОН СШ: Вывод
"1"
Выведено
Введено
КОН СШ
1511.4531.316
БНН СШ/ БНН: Срабатывание
КОН НН 5371
Uab НН
Ubc НН
min
Ucр КОН НН
min
&
&
КОН/ КОН НН: Срабатывание
1951.5371.301
КОН/ КОН НН: Выведено
1951.5371.302
КОН/ КОН НН: Вывод
"1"
Выведено
Введено
КОН НН
1961.5121.304
КЦН НН/ КЦН: Срабатывание