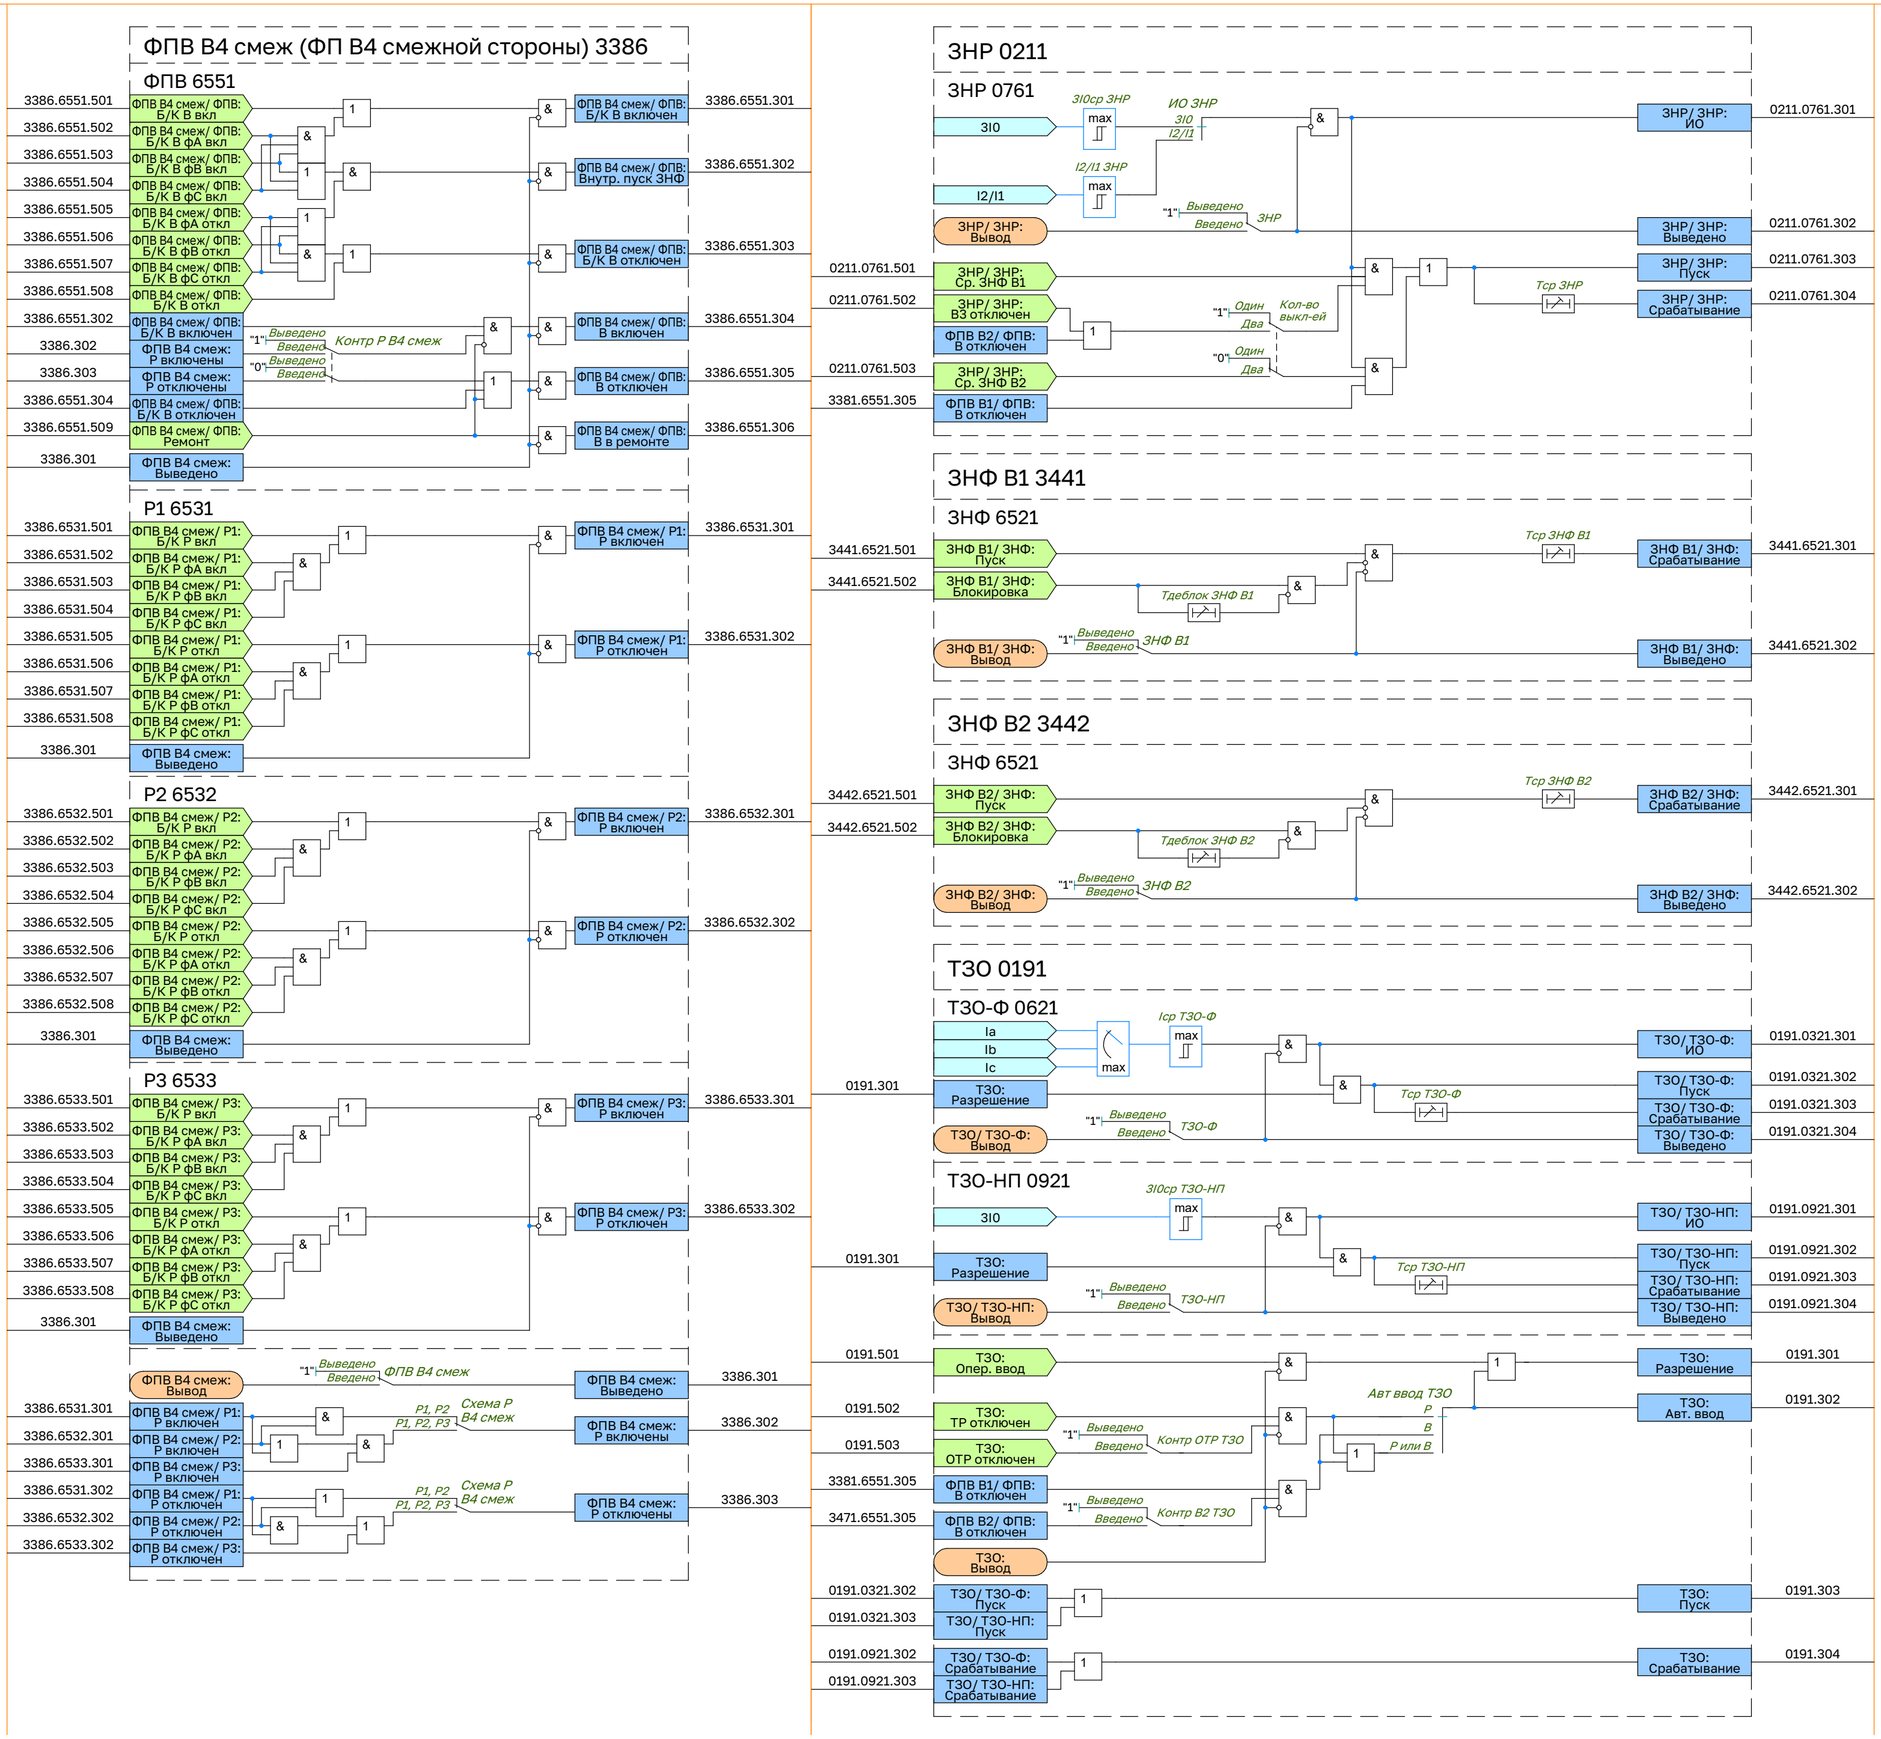
ФПВ В4 смеж (ФП В4 смежной стороны) 3386
ФПВ 6551
3386.6551.501
ФПВ В4 смеж/ ФПВ: Б/К В вкл
3386.6551.502
ФПВ В4 смеж/ ФПВ: Б/К В фА вкл
3386.6551.503
ФПВ В4 смеж/ ФПВ: Б/К В фВ вкл
3386.6551.504
ФПВ В4 смеж/ ФПВ: Б/К В фС вкл
3386.6551.505
ФПВ В4 смеж/ ФПВ: Б/К В фА откл
3386.6551.506
ФПВ В4 смеж/ ФПВ: Б/К В фВ откл
3386.6551.507
ФПВ В4 смеж/ ФПВ: Б/К В фС откл
3386.6551.508
ФПВ В4 смеж/ ФПВ: Б/К В откл
3386.6551.302
ФПВ В4 смеж/ ФПВ: Б/К В включен
3386.302
ФПВ В4 смеж: Р включены
3386.303
ФПВ В4 смеж: Р отключены
3386.6551.304
ФПВ В4 смеж/ ФПВ: Б/К В отключен
3386.6551.509
ФПВ В4 смеж/ ФПВ: Ремонт
3386.301
ФПВ В4 смеж: Выведено
"1"
Выведено
Введено
"0"
Выведено
Введено
Контр Р В4 смеж
ФПВ В4 смеж/ ФПВ: Б/К В включен
ФПВ В4 смеж/ ФПВ: Внутр. пуск ЗНФ
ФПВ В4 смеж/ ФПВ: Б/К В отключен
ФПВ В4 смеж/ ФПВ: В включен
ФПВ В4 смеж/ ФПВ: В отключен
ФПВ В4 смеж/ ФПВ: В в ремонте
3386.6551.301
3386.6551.302
3386.6551.303
3386.6551.304
3386.6551.305
3386.6551.306
Р1 6531
3386.6531.501
ФПВ В4 смеж/ Р1: Б/К Р вкл
3386.6531.502
ФПВ В4 смеж/ Р1: Б/К Р фА вкл
3386.6531.503
ФПВ В4 смеж/ Р1: Б/К Р фВ вкл
3386.6531.504
ФПВ В4 смеж/ Р1: Б/К Р фС вкл
3386.6531.505
ФПВ В4 смеж/ Р1: Б/К Р откл
3386.6531.506
ФПВ В4 смеж/ Р1: Б/К Р фА откл
3386.6531.507
ФПВ В4 смеж/ Р1: Б/К Р фВ откл
3386.6531.508
ФПВ В4 смеж/ Р1: Б/К Р фС откл
3386.301
ФПВ В4 смеж: Выведено
ФПВ В4 смеж/ Р1: Р включен
ФПВ В4 смеж/ Р1: Р отключен
3386.6531.301
3386.6531.302
Р2 6532
3386.6532.501
ФПВ В4 смеж/ Р2: Б/К Р вкл
3386.6532.502
ФПВ В4 смеж/ Р2: Б/К Р фА вкл
3386.6532.503
ФПВ В4 смеж/ Р2: Б/К Р фВ вкл
3386.6532.504
ФПВ В4 смеж/ Р2: Б/К Р фС вкл
3386.6532.505
ФПВ В4 смеж/ Р2: Б/К Р откл
3386.6532.506
ФПВ В4 смеж/ Р2: Б/К Р фА откл
3386.6532.507
ФПВ В4 смеж/ Р2: Б/К Р фВ откл
3386.6532.508
ФПВ В4 смеж/ Р2: Б/К Р фС откл
3386.301
ФПВ В4 смеж: Выведено
ФПВ В4 смеж/ Р2: Р включен
ФПВ В4 смеж/ Р2: Р отключен
3386.6532.301
3386.6532.302
Р3 6533
3386.6533.501
ФПВ В4 смеж/ Р3: Б/К Р вкл
3386.6533.502
ФПВ В4 смеж/ Р3: Б/К Р фА вкл
3386.6533.503
ФПВ В4 смеж/ Р3: Б/К Р фВ вкл
3386.6533.504
ФПВ В4 смеж/ Р3: Б/К Р фС вкл
3386.6533.505
ФПВ В4 смеж/ Р3: Б/К Р откл
3386.6533.506
ФПВ В4 смеж/ Р3: Б/К Р фА откл
3386.6533.507
ФПВ В4 смеж/ Р3: Б/К Р фВ откл
3386.6533.508
ФПВ В4 смеж/ Р3: Б/К Р фС откл
3386.301
ФПВ В4 смеж: Выведено
ФПВ В4 смеж/ Р3: Р включен
ФПВ В4 смеж/ Р3: Р отключен
3386.6533.301
3386.6533.302
ФПВ В4 смеж: Вывод
"1"
Выведено
Введено
ФПВ В4 смеж
ФПВ В4 смеж: Выведено
3386.301
3386.6531.301
ФПВ В4 смеж/ Р1: Р включен
3386.6532.301
ФПВ В4 смеж/ Р2: Р включен
3386.6533.301
ФПВ В4 смеж/ Р3: Р включен
3386.6531.302
ФПВ В4 смеж/ Р1: Р отключен
3386.6532.302
ФПВ В4 смеж/ Р2: Р отключен
3386.6533.302
ФПВ В4 смеж/ Р3: Р отключен
Р1, Р2
Р1, Р2, Р3
Схема Р В4 смеж
ФПВ В4 смеж: Р включены
3386.302
ФПВ В4 смеж: Р отключены
3386.303
ЗНР 0211
ЗНР 0761
3I0ср ЗНР
ИО ЗНР
3I0
I2/I1
max
I2/I1 ЗНР
I2/I1
ЗНР/ ЗНР: Вывод
"1"
Выведено
Введено
ЗНР
ЗНР/ ЗНР: ИО
ЗНР/ ЗНР: Выведено
ЗНР/ ЗНР: Пуск
ЗНР/ ЗНР: Срабатывание
0211.0761.301
0211.0761.302
0211.0761.303
0211.0761.304
0211.0761.501
ЗНР/ ЗНР: Ср. ЗНФ В1
0211.0761.502
ЗНР/ ЗНР: В3 отключен
ФПВ В2/ ФПВ: В отключен
0211.0761.503
ЗНР/ ЗНР: Ср. ЗНФ В2
3381.6551.305
ФПВ В1/ ФПВ: В отключен
Один
Два
Кол-во выкл-ей
Тср ЗНР
ЗНФ В1 3441
ЗНФ 6521
3441.6521.501
ЗНФ В1/ ЗНФ: Пуск
3441.6521.502
ЗНФ В1/ ЗНФ: Блокировка
ЗНФ В1/ ЗНФ: Вывод
Тдеблок ЗНФ В1
ЗНФ В1
Тср ЗНФ В1
ЗНФ В1/ ЗНФ: Срабатывание
ЗНФ В1/ ЗНФ: Выведено
3441.6521.301
3441.6521.302
ЗНФ В2 3442
ЗНФ 6521
3442.6521.501
ЗНФ В2/ ЗНФ: Пуск
3442.6521.502
ЗНФ В2/ ЗНФ: Блокировка
ЗНФ В2/ ЗНФ: Вывод
Тдеблок ЗНФ В2
ЗНФ В2
Тср ЗНФ В2
ЗНФ В2/ ЗНФ: Срабатывание
ЗНФ В2/ ЗНФ: Выведено
3442.6521.301
3442.6521.302
ТЗО 0191
ТЗО-Ф 0621
Ia
Ib
Ic
max
Iср ТЗО-Ф
0191.301
ТЗО: Разрешение
ТЗО/ ТЗО-Ф: Вывод
ТЗО-Ф
Тср ТЗО-Ф
ТЗО/ ТЗО-Ф: ИО
ТЗО/ ТЗО-Ф: Пуск
ТЗО/ ТЗО-Ф: Срабатывание
ТЗО/ ТЗО-Ф: Выведено
0191.0321.301
0191.0321.302
0191.0321.303
0191.0321.304
ТЗО-НП 0921
3I0ср ТЗО-НП
3I0
0191.301
ТЗО: Разрешение
ТЗО/ ТЗО-НП: Вывод
ТЗО-НП
Тср ТЗО-НП
ТЗО/ ТЗО-НП: ИО
ТЗО/ ТЗО-НП: Пуск
ТЗО/ ТЗО-НП: Срабатывание
ТЗО/ ТЗО-НП: Выведено
0191.0921.301
0191.0921.302
0191.0921.303
0191.0921.304
0191.501
ТЗО: Опер. ввод
0191.502
ТЗО: ТР отключен
0191.503
ТЗО: ОТР отключен
3381.6551.305
ФПВ В1/ ФПВ: В отключен
3471.6551.305
ФПВ В2/ ФПВ: В отключен
ТЗО: Вывод
Контр ОТР ТЗО
Контр В2 ТЗО
Авт ввод ТЗО
Р
В
Р или В
ТЗО: Разрешение
ТЗО: Авт. ввод
0191.301
0191.302
0191.0321.302
ТЗО/ ТЗО-Ф: Пуск
0191.0321.303
ТЗО/ ТЗО-НП: Пуск
0191.0921.302
ТЗО/ ТЗО-Ф: Срабатывание
0191.0921.303
ТЗО/ ТЗО-НП: Срабатывание
ТЗО: Пуск
ТЗО: Срабатывание
0191.303
0191.304