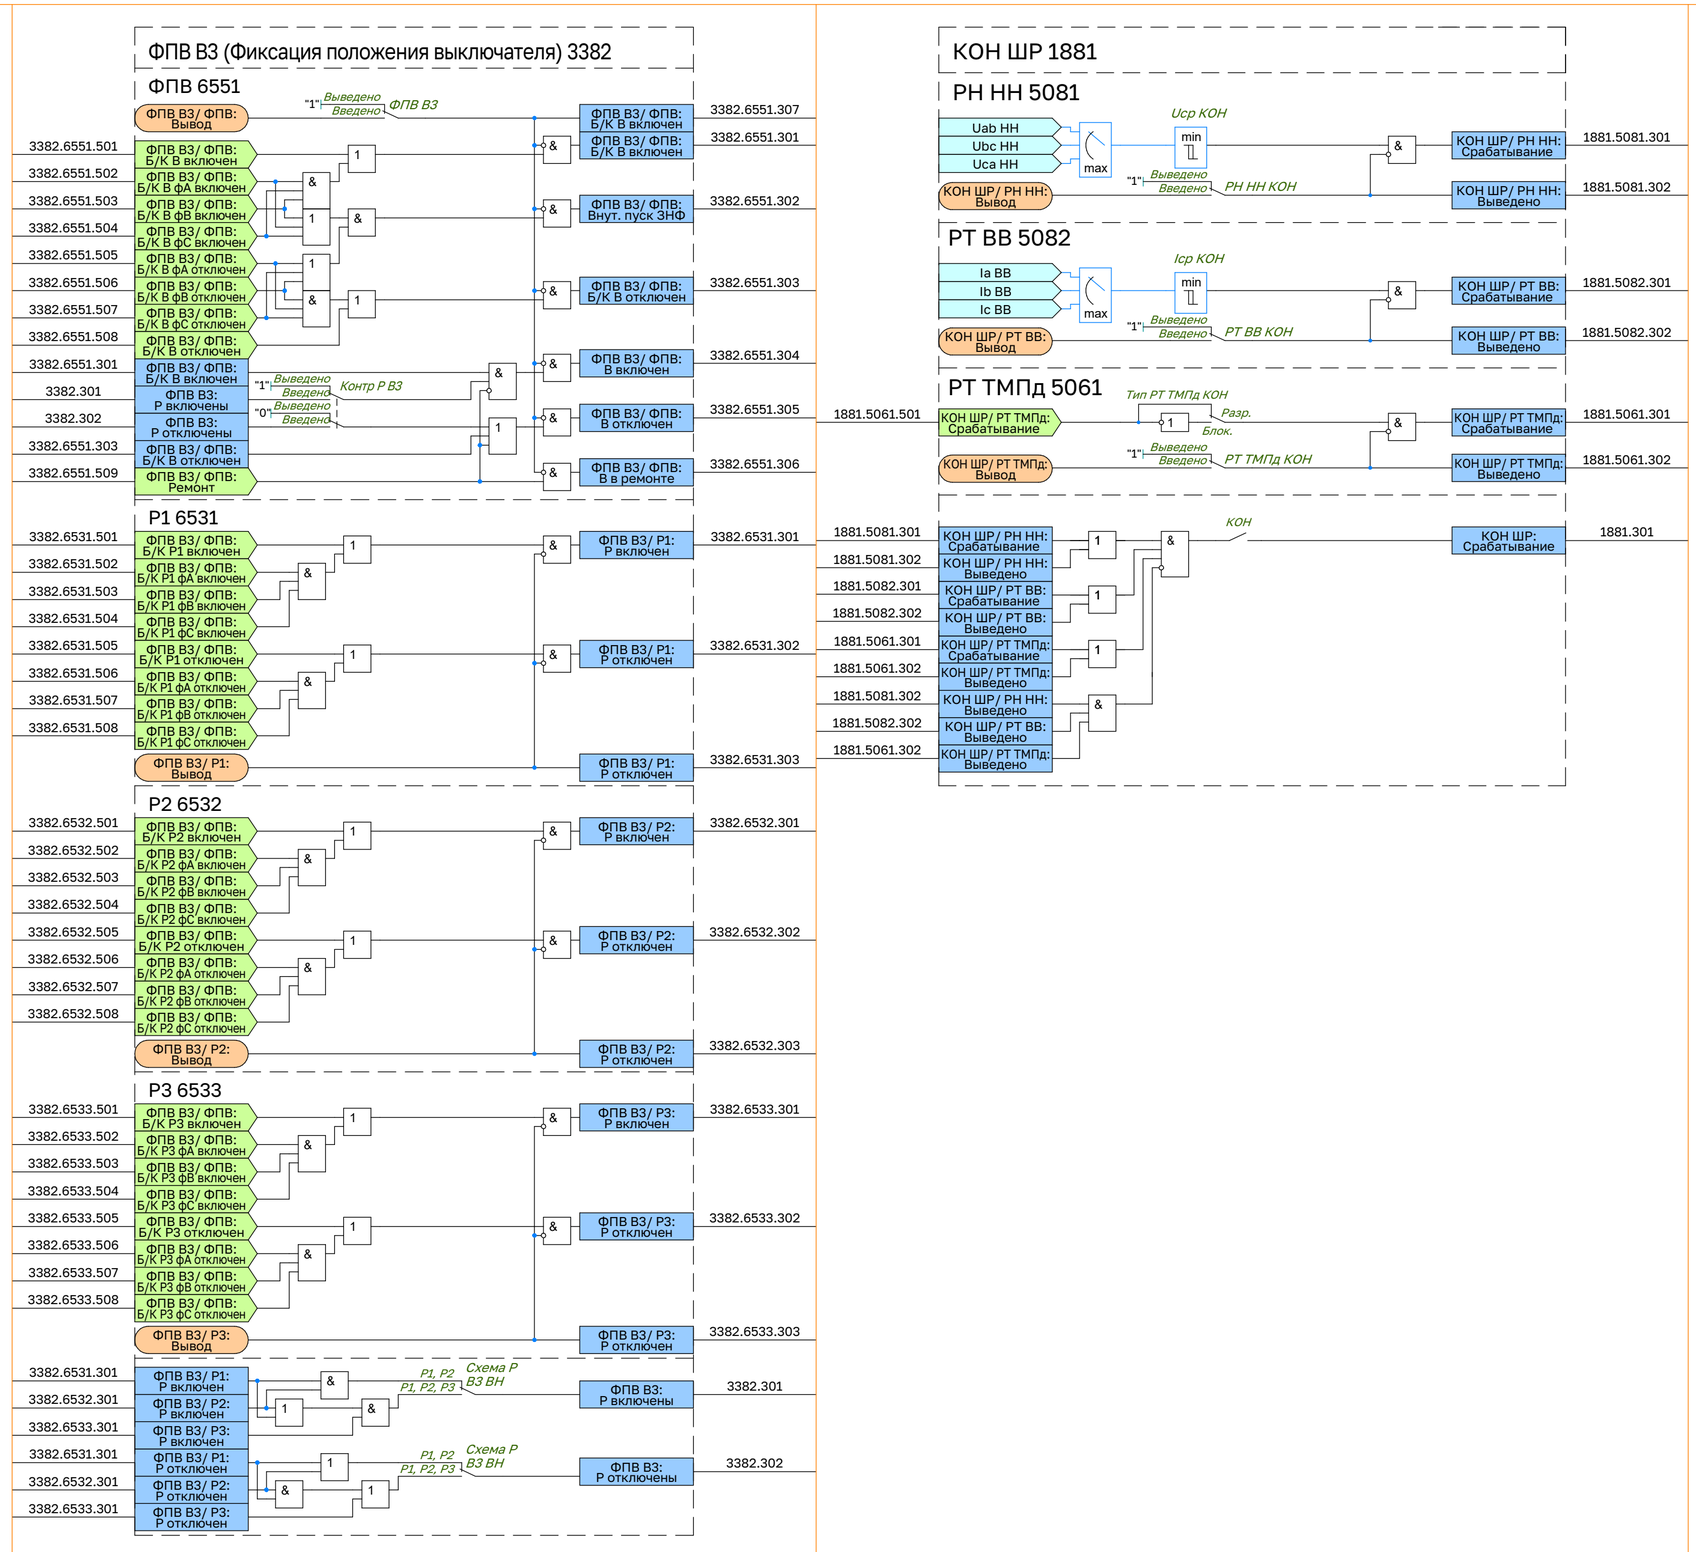

ФПВ ВЗ (Фиксация положения выключателя) 3382
ФПВ 6551
ФПВ ВЗ/ ФПВ: Вывод
"1" Выведено Введено ФПВ ВЗ
ФПВ ВЗ/ ФПВ: Б/К В включен
ФПВ ВЗ/ ФПВ: Б/К В фА включен
ФПВ ВЗ/ ФПВ: Б/К В фВ включен
ФПВ ВЗ/ ФПВ: Б/К В фС включен
ФПВ ВЗ/ ФПВ: Б/К В фА отключен
ФПВ ВЗ/ ФПВ: Б/К В фВ отключен
ФПВ ВЗ/ ФПВ: Б/К В фС отключен
ФПВ ВЗ/ ФПВ: Б/К В отключен
ФПВ ВЗ/ ФПВ: Б/К В включен
ФПВ ВЗ: Р включены
ФПВ ВЗ: Р отключены
ФПВ ВЗ/ ФПВ: Б/К В отключен
ФПВ ВЗ/ ФПВ: Ремонт
"1" Выведено Введено Контр Р ВЗ
"0" Выведено Введено
3382.6551.501
3382.6551.502
3382.6551.503
3382.6551.504
3382.6551.505
3382.6551.506
3382.6551.507
3382.6551.508
3382.6551.301
3382.301
3382.302
3382.6551.303
3382.6551.509
ФПВ ВЗ/ ФПВ: Б/К В включен
ФПВ ВЗ/ ФПВ: Внут. пуск ЗНФ
ФПВ ВЗ/ ФПВ: Б/К В отключен
ФПВ ВЗ/ ФПВ: В включен
ФПВ ВЗ/ ФПВ: В отключен
ФПВ ВЗ/ ФПВ: В в ремонте
3382.6551.307
3382.6551.301
3382.6551.302
3382.6551.303
3382.6551.304
3382.6551.305
3382.6551.306
Р1 6531
ФПВ ВЗ/ ФПВ: Б/К Р1 включен
ФПВ ВЗ/ ФПВ: Б/К Р1 фА включен
ФПВ ВЗ/ ФПВ: Б/К Р1 фВ включен
ФПВ ВЗ/ ФПВ: Б/К Р1 фС включен
ФПВ ВЗ/ ФПВ: Б/К Р1 отключен
ФПВ ВЗ/ ФПВ: Б/К Р1 фА отключен
ФПВ ВЗ/ ФПВ: Б/К Р1 фВ отключен
ФПВ ВЗ/ ФПВ: Б/К Р1 фС отключен
ФПВ ВЗ/ Р1: Вывод
3382.6531.501
3382.6531.502
3382.6531.503
3382.6531.504
3382.6531.505
3382.6531.506
3382.6531.507
3382.6531.508
ФПВ ВЗ/ Р1: Р включен
ФПВ ВЗ/ Р1: Р отключен
ФПВ ВЗ/ Р1: Р отключен
3382.6531.301
3382.6531.302
3382.6531.303
Р2 6532
ФПВ ВЗ/ ФПВ: Б/К Р2 включен
ФПВ ВЗ/ ФПВ: Б/К Р2 фА включен
ФПВ ВЗ/ ФПВ: Б/К Р2 фВ включен
ФПВ ВЗ/ ФПВ: Б/К Р2 фС включен
ФПВ ВЗ/ ФПВ: Б/К Р2 отключен
ФПВ ВЗ/ ФПВ: Б/К Р2 фА отключен
ФПВ ВЗ/ ФПВ: Б/К Р2 фВ отключен
ФПВ ВЗ/ ФПВ: Б/К Р2 фС отключен
ФПВ ВЗ/ Р2: Вывод
3382.6532.501
3382.6532.502
3382.6532.503
3382.6532.504
3382.6532.505
3382.6532.506
3382.6532.507
3382.6532.508
ФПВ ВЗ/ Р2: Р включен
ФПВ ВЗ/ Р2: Р отключен
ФПВ ВЗ/ Р2: Р отключен
3382.6532.301
3382.6532.302
3382.6532.303
Р3 6533
ФПВ ВЗ/ ФПВ: Б/К Р3 включен
ФПВ ВЗ/ ФПВ: Б/К Р3 фА включен
ФПВ ВЗ/ ФПВ: Б/К Р3 фВ включен
ФПВ ВЗ/ ФПВ: Б/К Р3 фС включен
ФПВ ВЗ/ ФПВ: Б/К Р3 отключен
ФПВ ВЗ/ ФПВ: Б/К Р3 фА отключен
ФПВ ВЗ/ ФПВ: Б/К Р3 фВ отключен
ФПВ ВЗ/ ФПВ: Б/К Р3 фС отключен
ФПВ ВЗ/ Р3: Вывод
3382.6533.501
3382.6533.502
3382.6533.503
3382.6533.504
3382.6533.505
3382.6533.506
3382.6533.507
3382.6533.508
ФПВ ВЗ/ Р3: Р включен
ФПВ ВЗ/ Р3: Р отключен
ФПВ ВЗ/ Р3: Р отключен
3382.6533.301
3382.6533.302
3382.6533.303
ФПВ ВЗ/ Р1: Р включен
ФПВ ВЗ/ Р2: Р включен
ФПВ ВЗ/ Р3: Р включен
ФПВ ВЗ/ Р1: Р отключен
ФПВ ВЗ/ Р2: Р отключен
ФПВ ВЗ/ Р3: Р отключен
3382.6531.301
3382.6532.301
3382.6533.301
3382.6531.301
3382.6532.301
3382.6533.301
P1, P2
P1, P2, P3
Схема Р ВЗ ВН
ФПВ ВЗ: Р включены
ФПВ ВЗ: Р отключены
3382.301
3382.302
КОН ШР 1881
РН НН 5081
Uab HH
Ubc HH
Uca HH
max
Ucp KOH
min
КОН ШР/ РН НН: Вывод
"1" Выведено Введено РН НН КОН
КОН ШР/ РН НН: Срабатывание
КОН ШР/ РН НН: Выведено
1881.5081.301
1881.5081.302
РТ ВВ 5082
Ia BB
Ib BB
Ic BB
Icp KOH
КОН ШР/ РТ ВВ: Вывод
РТ ВВ КОН
КОН ШР/ РТ ВВ: Срабатывание
КОН ШР/ РТ ВВ: Выведено
1881.5082.301
1881.5082.302
РТ ТМПд 5061
1881.5061.501
КОН ШР/ РТ ТМПд: Срабатывание
Тип РТ ТМПд КОН
Разр.
Блок.
КОН ШР/ РТ ТМПд: Вывод
РТ ТМПд КОН
КОН ШР/ РТ ТМПд: Срабатывание
КОН ШР/ РТ ТМПд: Выведено
1881.5061.301
1881.5061.302
1881.5081.301
1881.5081.302
1881.5082.301
1881.5082.302
1881.5061.301
1881.5061.302
1881.5081.302
1881.5082.302
1881.5061.302
КОН
КОН ШР: Срабатывание
1881.301