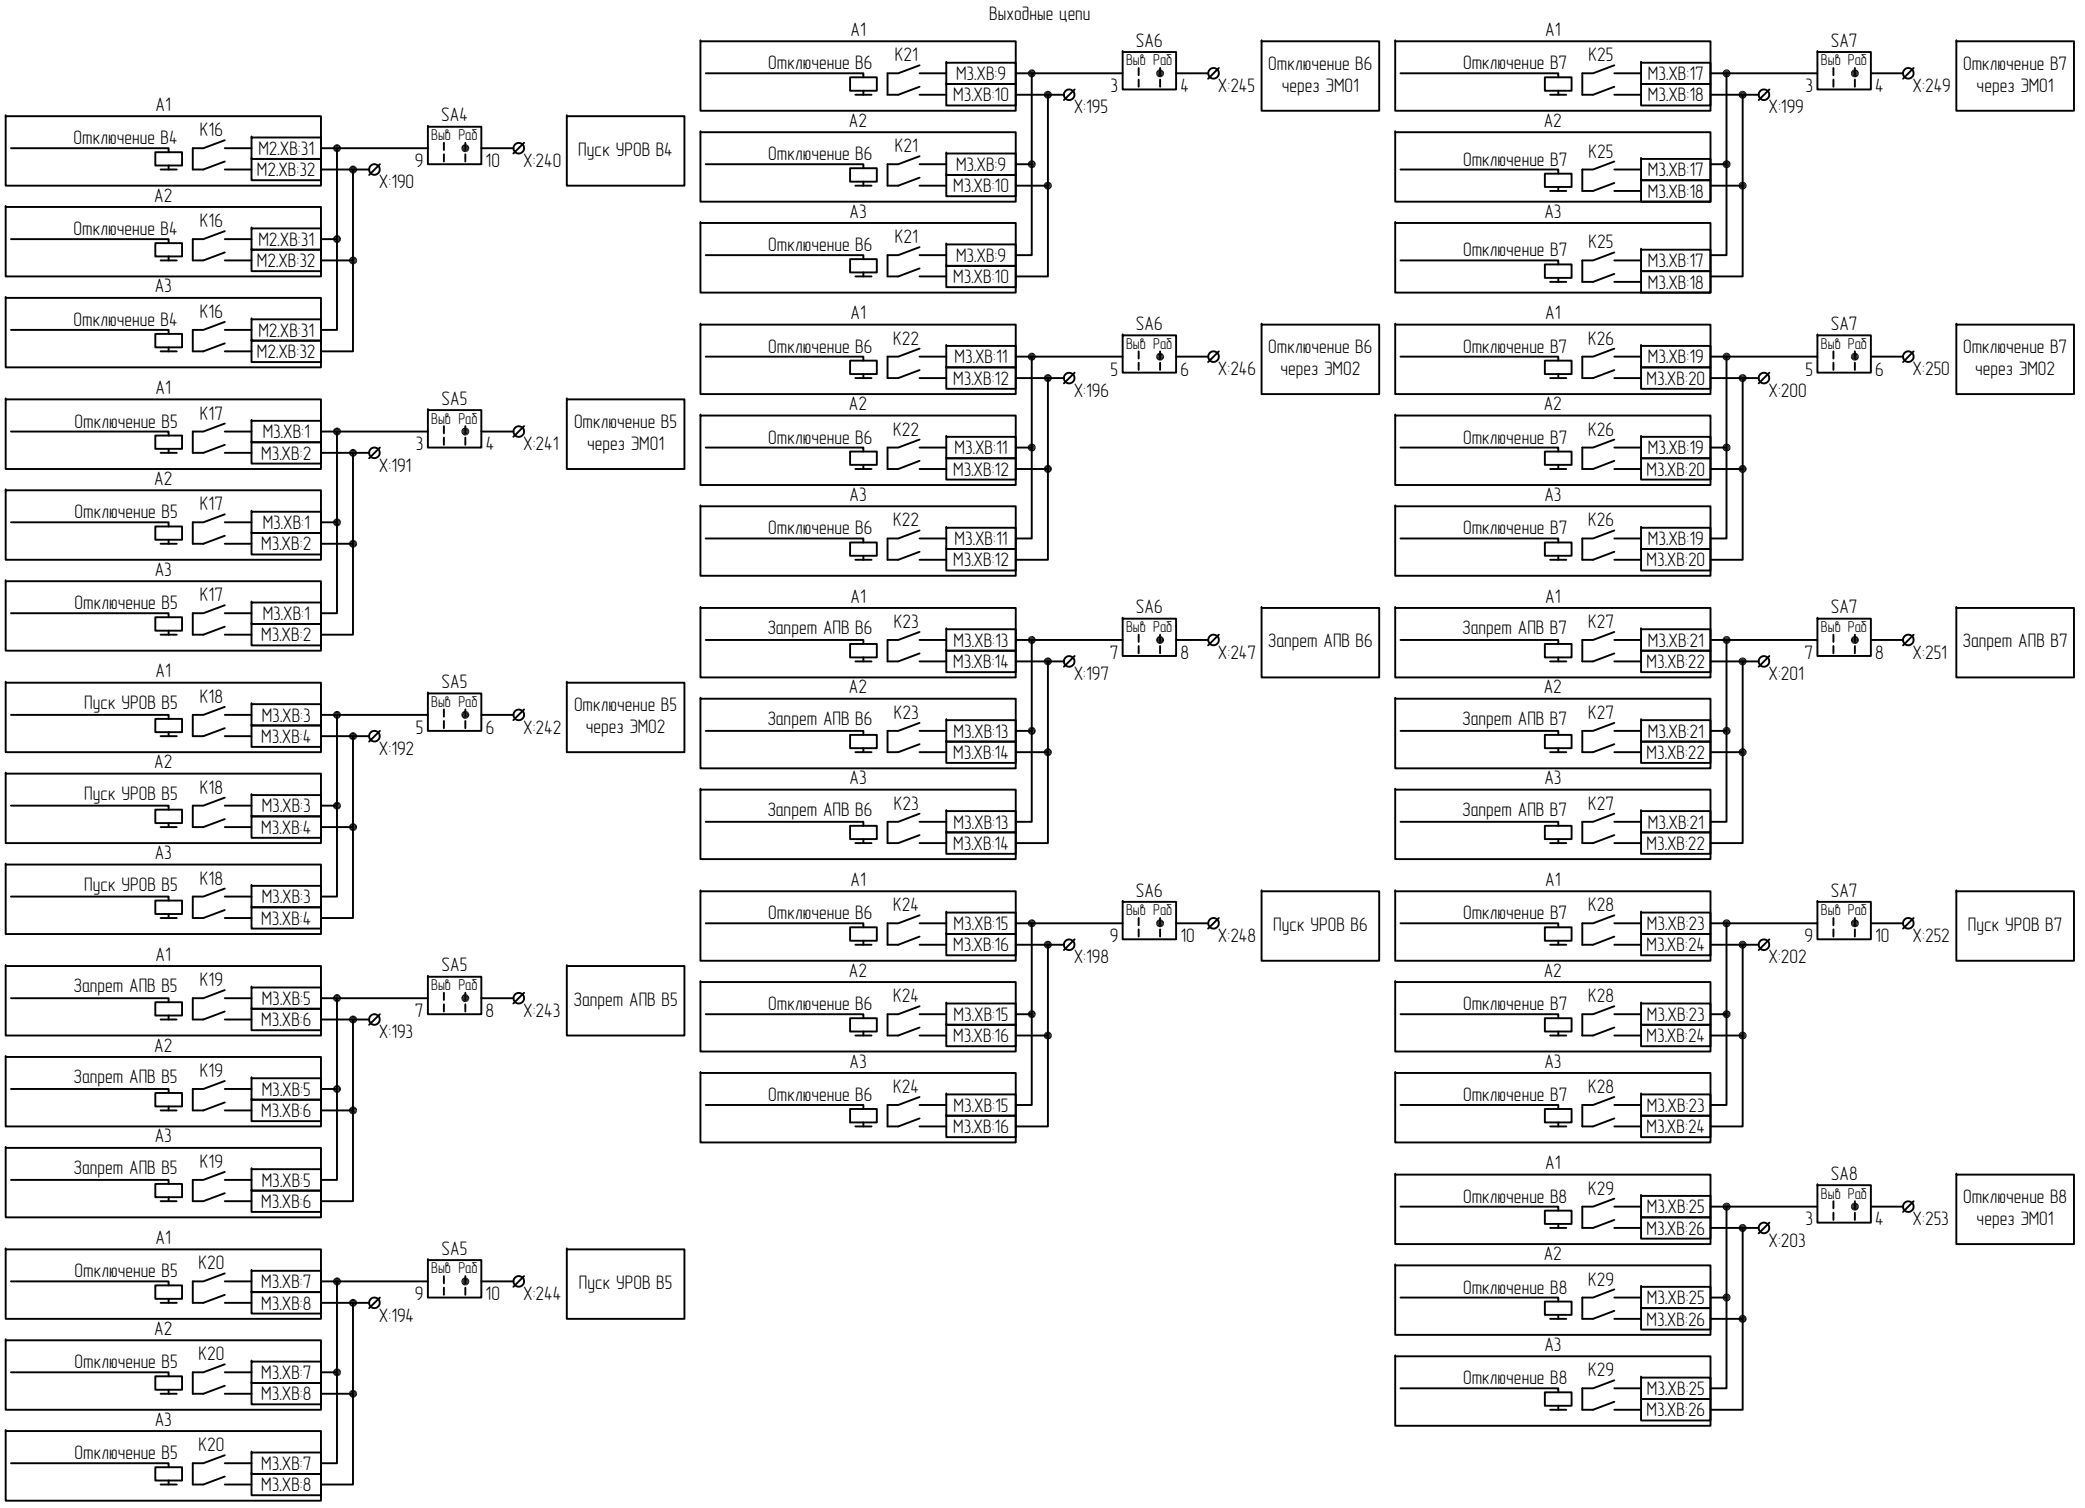

Выходные цепи
A1
Отключение В4
K16
M2.XB:31
M2.XB:32
A2
Отключение В4
K16
M2.XB:31
M2.XB:32
A3
Отключение В4
K16
M2.XB:31
M2.XB:32
SA4
Вып Раб
9
10
X:190
X:240
Пуск УРОВ В4
A1
Отключение В5
K17
M3.XB:1
M3.XB:2
A2
Отключение В5
K17
M3.XB:1
M3.XB:2
A3
Отключение В5
K17
M3.XB:1
M3.XB:2
SA5
Вып Раб
3
4
X:191
X:241
Отключение В5 через ЭМ01
A1
Пуск УРОВ В5
K18
M3.XB:3
M3.XB:4
A2
Пуск УРОВ В5
K18
M3.XB:3
M3.XB:4
A3
Пуск УРОВ В5
K18
M3.XB:3
M3.XB:4
SA5
Вып Раб
5
6
X:192
X:242
Отключение В5 через ЭМ02
A1
Запрет АПВ В5
K19
M3.XB:5
M3.XB:6
A2
Запрет АПВ В5
K19
M3.XB:5
M3.XB:6
A3
Запрет АПВ В5
K19
M3.XB:5
M3.XB:6
SA5
Вып Раб
7
8
X:193
X:243
Запрет АПВ В5
A1
Отключение В5
K20
M3.XB:7
M3.XB:8
A2
Отключение В5
K20
M3.XB:7
M3.XB:8
A3
Отключение В5
K20
M3.XB:7
M3.XB:8
SA5
Вып Раб
9
10
X:194
X:244
Пуск УРОВ В5
A1
Отключение В6
K21
M3.XB:9
M3.XB:10
A2
Отключение В6
K21
M3.XB:9
M3.XB:10
A3
Отключение В6
K21
M3.XB:9
M3.XB:10
SA6
Вып Раб
3
4
X:195
X:245
Отключение В6 через ЭМ01
A1
Отключение В6
K22
M3.XB:11
M3.XB:12
A2
Отключение В6
K22
M3.XB:11
M3.XB:12
A3
Отключение В6
K22
M3.XB:11
M3.XB:12
SA6
Вып Раб
5
6
X:196
X:246
Отключение В6 через ЭМ02
A1
Запрет АПВ В6
K23
M3.XB:13
M3.XB:14
A2
Запрет АПВ В6
K23
M3.XB:13
M3.XB:14
A3
Запрет АПВ В6
K23
M3.XB:13
M3.XB:14
SA6
Вып Раб
7
8
X:197
X:247
Запрет АПВ В6
A1
Отключение В6
K24
M3.XB:15
M3.XB:16
A2
Отключение В6
K24
M3.XB:15
M3.XB:16
A3
Отключение В6
K24
M3.XB:15
M3.XB:16
SA6
Вып Раб
9
10
X:198
X:248
Пуск УРОВ В6
A1
Отключение В7
K25
M3.XB:17
M3.XB:18
A2
Отключение В7
K25
M3.XB:17
M3.XB:18
A3
Отключение В7
K25
M3.XB:17
M3.XB:18
SA7
Вып Раб
3
4
X:199
X:249
Отключение В7 через ЭМ01
A1
Отключение В7
K26
M3.XB:19
M3.XB:20
A2
Отключение В7
K26
M3.XB:19
M3.XB:20
A3
Отключение В7
K26
M3.XB:19
M3.XB:20
SA7
Вып Раб
5
6
X:200
X:250
Отключение В7 через ЭМ02
A1
Запрет АПВ В7
K27
M3.XB:21
M3.XB:22
A2
Запрет АПВ В7
K27
M3.XB:21
M3.XB:22
A3
Запрет АПВ В7
K27
M3.XB:21
M3.XB:22
SA7
Вып Раб
7
8
X:201
X:251
Запрет АПВ В7
A1
Отключение В7
K28
M3.XB:23
M3.XB:24
A2
Отключение В7
K28
M3.XB:23
M3.XB:24
A3
Отключение В7
K28
M3.XB:23
M3.XB:24
SA7
Вып Раб
9
10
X:202
X:252
Пуск УРОВ В7
A1
Отключение В8
K29
M3.XB:25
M3.XB:26
A2
Отключение В8
K29
M3.XB:25
M3.XB:26
A3
Отключение В8
K29
M3.XB:25
M3.XB:26
SA8
Вып Раб
3
4
X:203
X:253
Отключение В8 через ЭМ01