

ЦОС.ХХ

ХА:Х	Ia BB*
ХА:Х	Ia BB
ХА:Х	Ib BB*
ХА:Х	Ib BB
ХА:Х	Ic BB*
ХА:Х	Ic BB
ХА:Х	Ia НВ*
ХА:Х	Ia НВ
ХА:Х	Ib НВ*
ХА:Х	Ib НВ
ХА:Х	Ic НВ*
ХА:Х	Ic НВ
ХА:Х	Ia СП*
ХА:Х	Ia СП
ХА:Х	Ib СП*
ХА:Х	Ib СП
ХА:Х	Ic СП*
ХА:Х	Ic СП
ХА:Х	Iнейтр*
ХА:Х	Iнейтр
ХА:Х	---
ХА:Х	----
ХА:Х	----
ХА:Х	----

Iдиф.а ДТЗ (1г)	
Iгорм ДЗТ	
Iдиф.б ДТЗ (1г)	
Iдиф.с ДТЗ (1г)	
Iад2г/Iад1г ВН	
Iбд2г/Iбд1г ВН	
Iсд2г/Iсд1г ВН	
Iад5г/Iад1г ВН	
Iбд5г/Iбд1г ВН	
Iсд5г/Iсд1г ВН	
Iдиф ДТЗ НП	
Iгорм ДТЗ НП	
ЗЮ ВВ*	
Iнейтр*	
Ia_нб	
Ib_нб	
Ic_нб	
Ua	
Uab	
Ub	
Ubc	
Uc	
Uca	
Ia ВВ	
Ib ВВ	
Ic ВВ	
Iab ВВ	
Ibc ВВ	
Ica ВВ	
ЗЮ ВВ	
Iнейтр	
I2 ВВ	
Ia2r/Ia1r ВВ	
Iab2r/Iab1r ВВ	
Ib2r/Ib1r ВВ	
Ibc2r/Ibc1r ВВ	
Ic2r/Ic1r ВВ	
Ica2r/Ica1r ВВ	
Ia_скз ВВ	
Ib_скз ВВ	
Ic_скз ВВ	
dU1	
dI1	
U1	
I1	
Ua	
Ub	
Uc	
I2/I1	
U2/U1	
U2	
ЗЮ/I1	
ЗЮ0 звезда	
Uбнн	
Уни	
Уиф	
Уфж	
Убнн фА	
Убнн-фВ	
Убнн фС	
ЗЮ	

Вывод терминала	90.004
БИ ток ВН	90.501
БИ ток нейтрал	90.502
БИ ток. Ср. Пер.	90.503
БИ ток. в цепи ЗН	90.504
БИ напр. ВН(ав.)	90.505
БИ напр. ВН (тр.)	90.506
Действие на В1 введено	90.507
Действие на В2 введено	90.508
Действие на В3 введено	90.509
Вых. цепи разобраны	90.510
ЗНФ В1	0161.0221.0881.500
ЗНФ В2	0161.0221.0881.502
Автомат ТН	261.1461.0011.501
Фикс. неиспр. ЦН	261.1461.0011.500
Низк.ур.изол.ТТ ВВ	91.500
Низк.ур.изол.ТТ Нб	91.501
Низк.ур.изол.ТТ НВ	91.502
Низк.ур.изол.ТТ нейтр	91.503
Авар.ур.изол.ТТ ВВ	91.504
Авар.ур.изол.ТТ Нб	91.505
Авар.ур.изол.ТТ НВ	91.506
Авар.ур.изол.ТТ нейтр	91.507
Контр. ОТ терм.	91.508


Контр. ЭМО1 В1(ЛВ)	761.3371.6571.501
Контр. ЭМО1 В1(ЛВ) ф.А	761.3371.6571.511
Контр. ЭМО1 В1(ЛВ) ф.В	761.3371.6571.521
Контр. ЭМО1 В1(ЛВ) ф.С	761.3371.6571.531
Контр. ЭМО2 В1(ЛВ)	761.3371.6571.502
Контр. ЭМО2 В1(ЛВ) ф.А	761.3371.6571.512
Контр. ЭМО2 В1(ЛВ) ф.В	761.3371.6571.522
Контр. ЭМО2 В1(ЛВ) ф.С	761.3371.6571.532
Контр. ЭМВ В1(ЛВ)	761.3371.6571.503
Контр. ЭМВ В1(ЛВ) ф.А	761.3371.6571.513
Контр. ЭМВ В1(ЛВ) ф.В	761.3371.6571.523
Контр. ЭМВ В1(ЛВ) ф.С	761.3371.6571.533
Низк. давл. SF6 В1(ЛВ)	761.3371.6571.504
Низк. давл. SF6 В1(ЛВ) ф.А	761.3371.6571.514
Низк. давл. SF6 В1(ЛВ) ф.В	761.3371.6571.524
Низк. давл. SF6 В1(ЛВ) ф.С	761.3371.6571.534
Авар. давл. SF6 В1(ЛВ)	761.3371.6571.505
Авар. давл. SF6 В1(ЛВ) ф.А	761.3371.6571.515
Авар. давл. SF6 В1(ЛВ) ф.В	761.3371.6571.525
Авар. давл. SF6 В1(ЛВ) ф.С	761.3371.6571.535
Пруж. не заведены В1(ЛВ)	761.3371.6571.506
Пруж. не заведены В1(ЛВ) ф.А	761.3371.6571.516
Пруж. не заведены В1(ЛВ) ф.В	761.3371.6571.526
Пруж. не заведены В1(ЛВ) ф.С	761.3371.6571.536
Неиспр. обогр. В1(ЛВ)	761.3371.6571.507
Автомат ШП В1(ЛВ)	761.3371.6571.508
Контр. опертока ЭМВ/ЭМО1 В1(ЛВ)	761.3371.6591.500
Контр. опертока ЭМО2 В1(ЛВ)	761.3371.6591.501
Контр. опертока сигн. В1(ЛВ)	761.3371.6591.502
Внеш. блок. откл. В1(ЛВ)	761.3371.6611.500
Внеш. блок. упр. В1(ЛВ)	761.3371.6611.501
Внеш. блок. вкл. В1(ЛВ)	761.3371.6611.502
Работа ЭМВ В1(ЛВ)	761.3371.6601.503
Работа ЭМВ В1(ЛВ) ф.А	761.3371.6601.513
Работа ЭМВ В1(ЛВ) ф.В	761.3371.6601.523
Работа ЭМВ В1(ЛВ) ф.А	761.3371.6601.533
Работа ЭМО1 В1(ЛВ)	761.3371.6601.501
Работа ЭМО1 В1(ЛВ) ф.А	761.3371.6601.511
Работа ЭМО1 В1(ЛВ) ф.В	761.3371.6601.521
Работа ЭМО1 В1(ЛВ) ф.А	761.3371.6601.531
Работа ЭМО2 В1(ЛВ)	761.3371.6601.502
Работа ЭМО2 В1(ЛВ) ф.А	761.3371.6601.512
Работа ЭМО2 В1(ЛВ) ф.В	761.3371.6601.522
Работа ЭМО2 В1(ЛВ) ф.А	761.3371.6601.532
Низк. давл. SF6 ТТ В1(ЛВ)	761.3371.6581.501
Низк. давл. SF6 ТТ В1(ЛВ) ф.А	761.3371.6581.511
Низк. давл. SF6 ТТ В1(ЛВ) ф.В	761.3371.6581.521
Низк. давл. SF6 ТТ В1(ЛВ) ф.С	761.3371.6581.531
Авар. давл. SF6 ТТ В1(ЛВ)	761.3371.6581.502
Авар. давл. SF6 ТТ В1(ЛВ) ф.А	761.3371.6581.512
Авар. давл. SF6 ТТ В1(ЛВ) ф.В	761.3371.6581.522
Авар. давл. SF6 ТТ В1(ЛВ) ф.С	761.3371.6581.532
Неиспр. обогр. ТТ В1(ЛВ)	761.3371.6581.500

Б/К В1(ЛВ) вкл	761.3471.6551.501
Б/К В1(ЛВ) фА вкл	761.3471.6551.511
Б/К В1(ЛВ) фВ вкл	761.3471.6551.521
Б/К В1(ЛВ) фС вкл	761.3471.6551.531
Б/К В1(ЛВ) фА откл	761.3471.6551.512
Б/К В1(ЛВ) фВ откл	761.3471.6551.522
Б/К В1(ЛВ) фС откл	761.3471.6551.532
Б/К В1(ЛВ) откл	761.3471.6551.502
Б/К Р1 В1(ЛВ) вкл	761.3471.6531.501
Б/К Р1 В1(ЛВ) фА вкл	761.3471.6531.511
Б/К Р1 В1(ЛВ) фВ вкл	761.3471.6531.521
Б/К Р1 В1(ЛВ) фС вкл	761.3471.6531.531
Б/К Р1 В1(ЛВ) откл	761.3471.6531.502
Б/К Р1 В1(ЛВ) фА откл	761.3471.6531.512
Б/К Р1 В1(ЛВ) фВ откл	761.3471.6531.522
Б/К Р1 В1(ЛВ) фС откл	761.3471.6531.532
Б/К Р2 В1(ЛВ) вкл	761.3471.6532.501
Б/К Р2 В1(ЛВ) фА вкл	761.3471.6532.511
Б/К Р2 В1(ЛВ) фВ вкл	761.3471.6532.521
Б/К Р2 В1(ЛВ) фС вкл	761.3471.6532.531
Б/К Р2 В1(ЛВ) откл	761.3471.6532.502
Б/К Р2 В1(ЛВ) фА откл	761.3471.6532.512
Б/К Р2 В1(ЛВ) фВ откл	761.3471.6532.522
Б/К Р2 В1(ЛВ) фС откл	761.3471.6532.532
Б/К Р3 В1 вкл	761.3471.6533.501
Б/К Р3 В1(ЛВ) фА вкл	761.3471.6533.511
Б/К Р3 В1(ЛВ) фВ вкл	761.3471.6533.521
Б/К Р3 В1(ЛВ) фС вкл	761.3471.6533.531
Б/К Р3 В1(ЛВ) откл	761.3471.6533.502
Б/К Р3 В1(ЛВ) фА откл	761.3471.6533.512
Б/К Р3 В1(ЛВ) фВ откл	761.3471.6533.522
Б/К Р3 В1(ЛВ) фС откл	761.3471.6533.532
Б/К В2(ОВ) вкл	762.3471.6551.501
Б/К В2(ОВ) фА вкл	762.3471.6551.511
Б/К В2(ОВ) фВ вкл	762.3471.6551.521
Б/К В2(ОВ) фС вкл	762.3471.6551.531
Б/К В2(ОВ) фА откл	762.3471.6551.512
Б/К В2(ОВ) фВ откл	762.3471.6551.522
Б/К В2(ОВ) фС откл	762.3471.6551.532
Б/К В2(ОВ) откл	762.3471.6551.502
Ремонт В2(ОВ)	762.3471.6551.500
Б/К Р1 В2(ОВ) вкл	762.3471.6531.501
Б/К Р1 В2(ОВ) фА вкл	762.3471.6531.511
Б/К Р1 В2(ОВ) фВ вкл	762.3471.6531.521
Б/К Р1 В2(ОВ) фС вкл	762.3471.6531.531
Б/К Р1 В2(ОВ) откл	762.3471.6531.502
Б/К Р1 В2(ОВ) фА откл	762.3471.6531.512
Б/К Р1 В2(ОВ) фВ откл	762.3471.6531.522
Б/К Р1 В2(ОВ) фС откл	762.3471.6531.532
Б/К Р2 В2(ОВ) вкл	762.3471.6532.501
Б/К Р2 В2(ОВ) фА вкл	762.3471.6532.511
Б/К Р2 В2(ОВ) фВ вкл	762.3471.6532.521
Б/К Р2 В2(ОВ) фС вкл	762.3471.6532.531
Б/К Р2 В2(ОВ) откл	762.3471.6532.502
Б/К Р2 В2(ОВ) фА откл	762.3471.6532.512
Б/К Р2 В2(ОВ) фВ откл	762.3471.6532.522
Б/К Р2 В2(ОВ) фС откл	762.3471.6532.532
Б/К Р3 В2 вкл	762.3471.6533.501
Б/К Р3 В2(ОВ) фА вкл	762.3471.6533.511
Б/К Р3 В2(ОВ) фВ вкл	762.3471.6533.521
Б/К Р3 В2(ОВ) фС вкл	762.3471.6533.531
Б/К Р3 В2(ОВ) откл	762.3471.6533.502
Б/К Р3 В2(ОВ) фА откл	762.3471.6533.512
Б/К Р3 В2(ОВ) фВ откл	762.3471.6533.522
Б/К Р3 В2(ОВ) фС откл	762.3471.6533.532
Б/К В3 вкл	763.3471.6551.501
Б/К В3 фА вкл	763.3471.6551.511
Б/К В3 фВ вкл	763.3471.6551.521
Б/К В3 фС вкл	763.3471.6551.531
Б/К В3 фА откл	763.3471.6551.512
Б/К В3 фВ откл	763.3471.6551.522

Б/К В3 фС откл	763.3471.6551.532
Б/К В3 откл	763.3471.6551.502
Ремонт В3	763.3471.6551.500
Б/К Р1 В3 вкл	763.3471.6531.501
Б/К Р1 В3 фА вкл	763.3471.6531.511
Б/К Р1 В3 фВ вкл	763.3471.6531.521
Б/К Р1 В3 фС вкл	763.3471.6531.531
Б/К Р1 В3 откл	763.3471.6531.502
Б/К Р1 В3 фА откл	763.3471.6531.512
Б/К Р1 В3 фВ откл	763.3471.6531.522
Б/К Р1 В3 фС откл	763.3471.6531.532
Б/К Р2 В3 вкл	763.3471.6532.501
Б/К Р2 В3 фА вкл	763.3471.6532.511
Б/К Р2 В3 фВ вкл	763.3471.6532.521
Б/К Р2 В3 фС вкл	763.3471.6532.531
Б/К Р2 В3 откл	763.3471.6532.502
Б/К Р2 В3 фА откл	763.3471.6532.512
Б/К Р2 В3 фВ откл	763.3471.6532.522
Б/К Р2 В3 фС откл	763.3471.6532.532
Б/К Р3 В3 вкл	763.3471.6533.501
Б/К Р3 В3 фА вкл	763.3471.6533.511
Б/К Р3 В3 фВ вкл	763.3471.6533.521
Б/К Р3 В3 фС вкл	763.3471.6533.531
Б/К Р3 В3 откл	763.3471.6533.502
Б/К Р3 В3 фА откл	763.3471.6533.512
Б/К Р3 В3 фВ откл	763.3471.6533.522
Б/К Р3 В3 фС откл	763.3471.6533.532


ДТЗ Введена	261.0611.1521.303
Вывод ДТЗ НП	261.0621.1631.004
Вывод ЗВП	261.0611.0011.004
Вывод ЗН	261.0861.0011.004
Вывод МТЗ ВВ	271.0281.0011.004
Вывод ТЗНП ВВ	271.0241.0011.004
Вывод ТЗНП НВ	272.0251.0011.004
Вывод ТЗОП ВВ	271.0291.0011.004
Вывод ЗНР	261.0221.0881.004
Вывод ЗПВГ	261.381.821.004
Вывод УРОВ В1(ЛВ)	761.3341.5231.004
Вывод БНН	261.1461.0011.004
Вывод ФПВ В1(ЛВ)	761.3471.0011.004
Вывод ФПВ В2(ОВ)	762.3471.0011.004
Вывод ФПВ В3	763.3471.0011.004
Вывод УВ В1(ЛВ)	761.3391.0011.004
Вывод ЛО В1(ЛВ)	761.9901.9901.500
Вывод ЦО В1(ЛВ)	761.9901.9901.501
Вывод ЗАПВ В1(ЛВ)	761.9901.9901.502
Вывод ЛО В2(ОВ)	762.9901.9901.500
Вывод ЦО В2(ОВ)	762.9901.9901.501
Вывод ЗАПВ В2(ОВ)	762.9901.9901.502

Вкл. В1(ЛВ) от КП	761.3431.6661.514
Вкл. В1(ЛВ) от ПА	761.3431.6661.515
РФ В1(ЛВ)	761.3371.6621.300
Вкл. В1(ЛВ) от КУ	761.3431.6661.511
Откл. В1(ЛВ) от КУ	761.3431.6661.521
Местное управление	90.316
Вкл. В1(ЛВ) от ФК	761.3431.6661.512
Откл. В1(ЛВ) от ФК	761.3431.6661.522
Вкл. В1(ЛВ) от АСУ ТП	761.3431.6661.513
Откл. В1(ЛВ) от АСУ ТП	761.3431.6661.523
Разреш. АСУ ТП	90.317
Отмена команды	90.318
Выполнение команды	90.319
Откл. В1(ЛВ) от КП	761.3431.6661.524
Откл. В1(ЛВ) от ПА	761.3431.6661.525

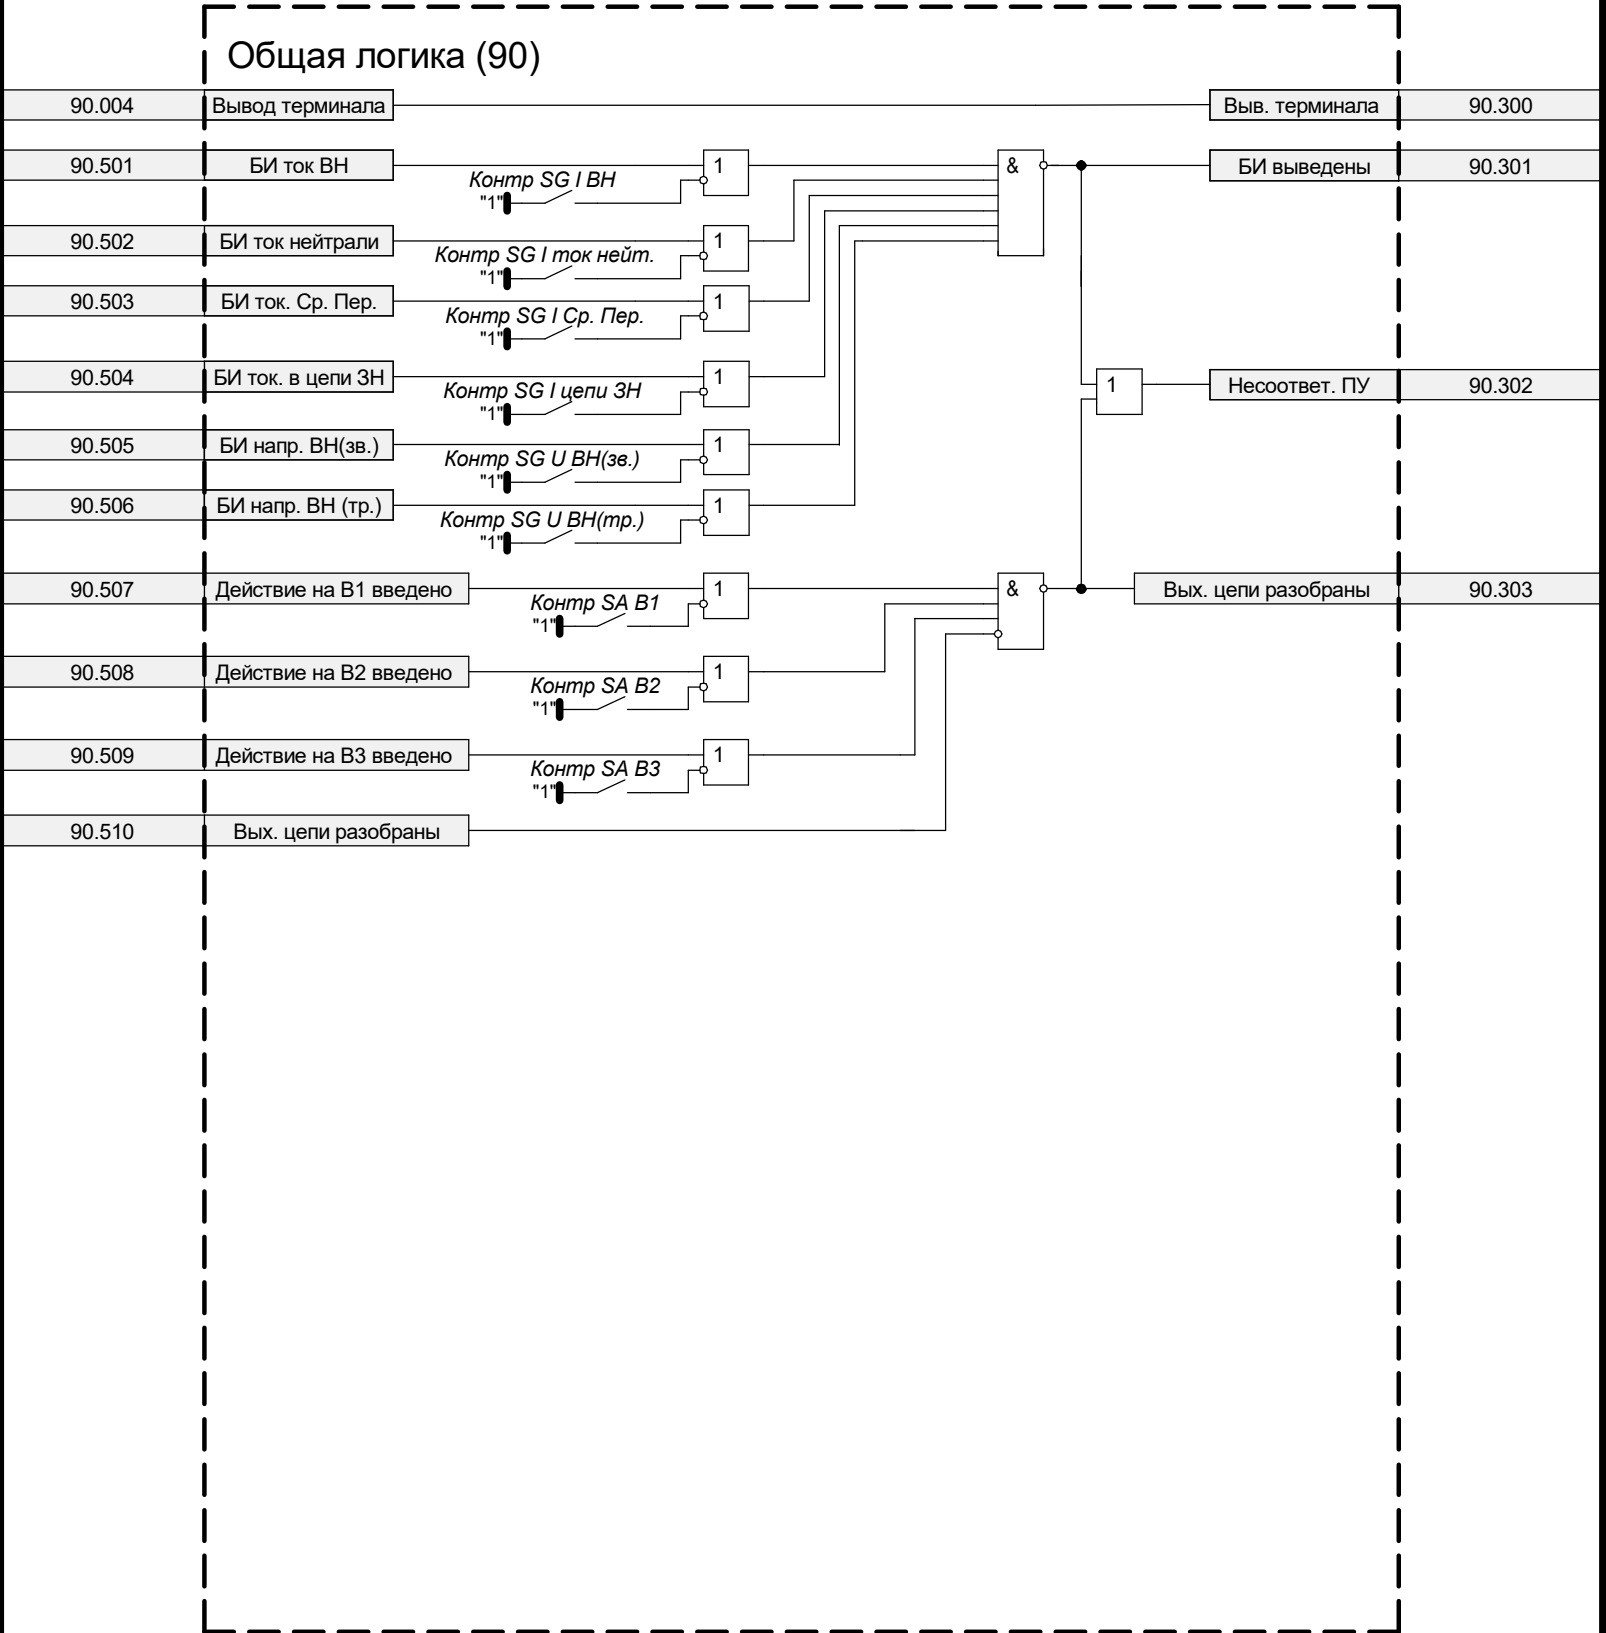


ДТЗ (261.0611)


ДТЗт (1521)

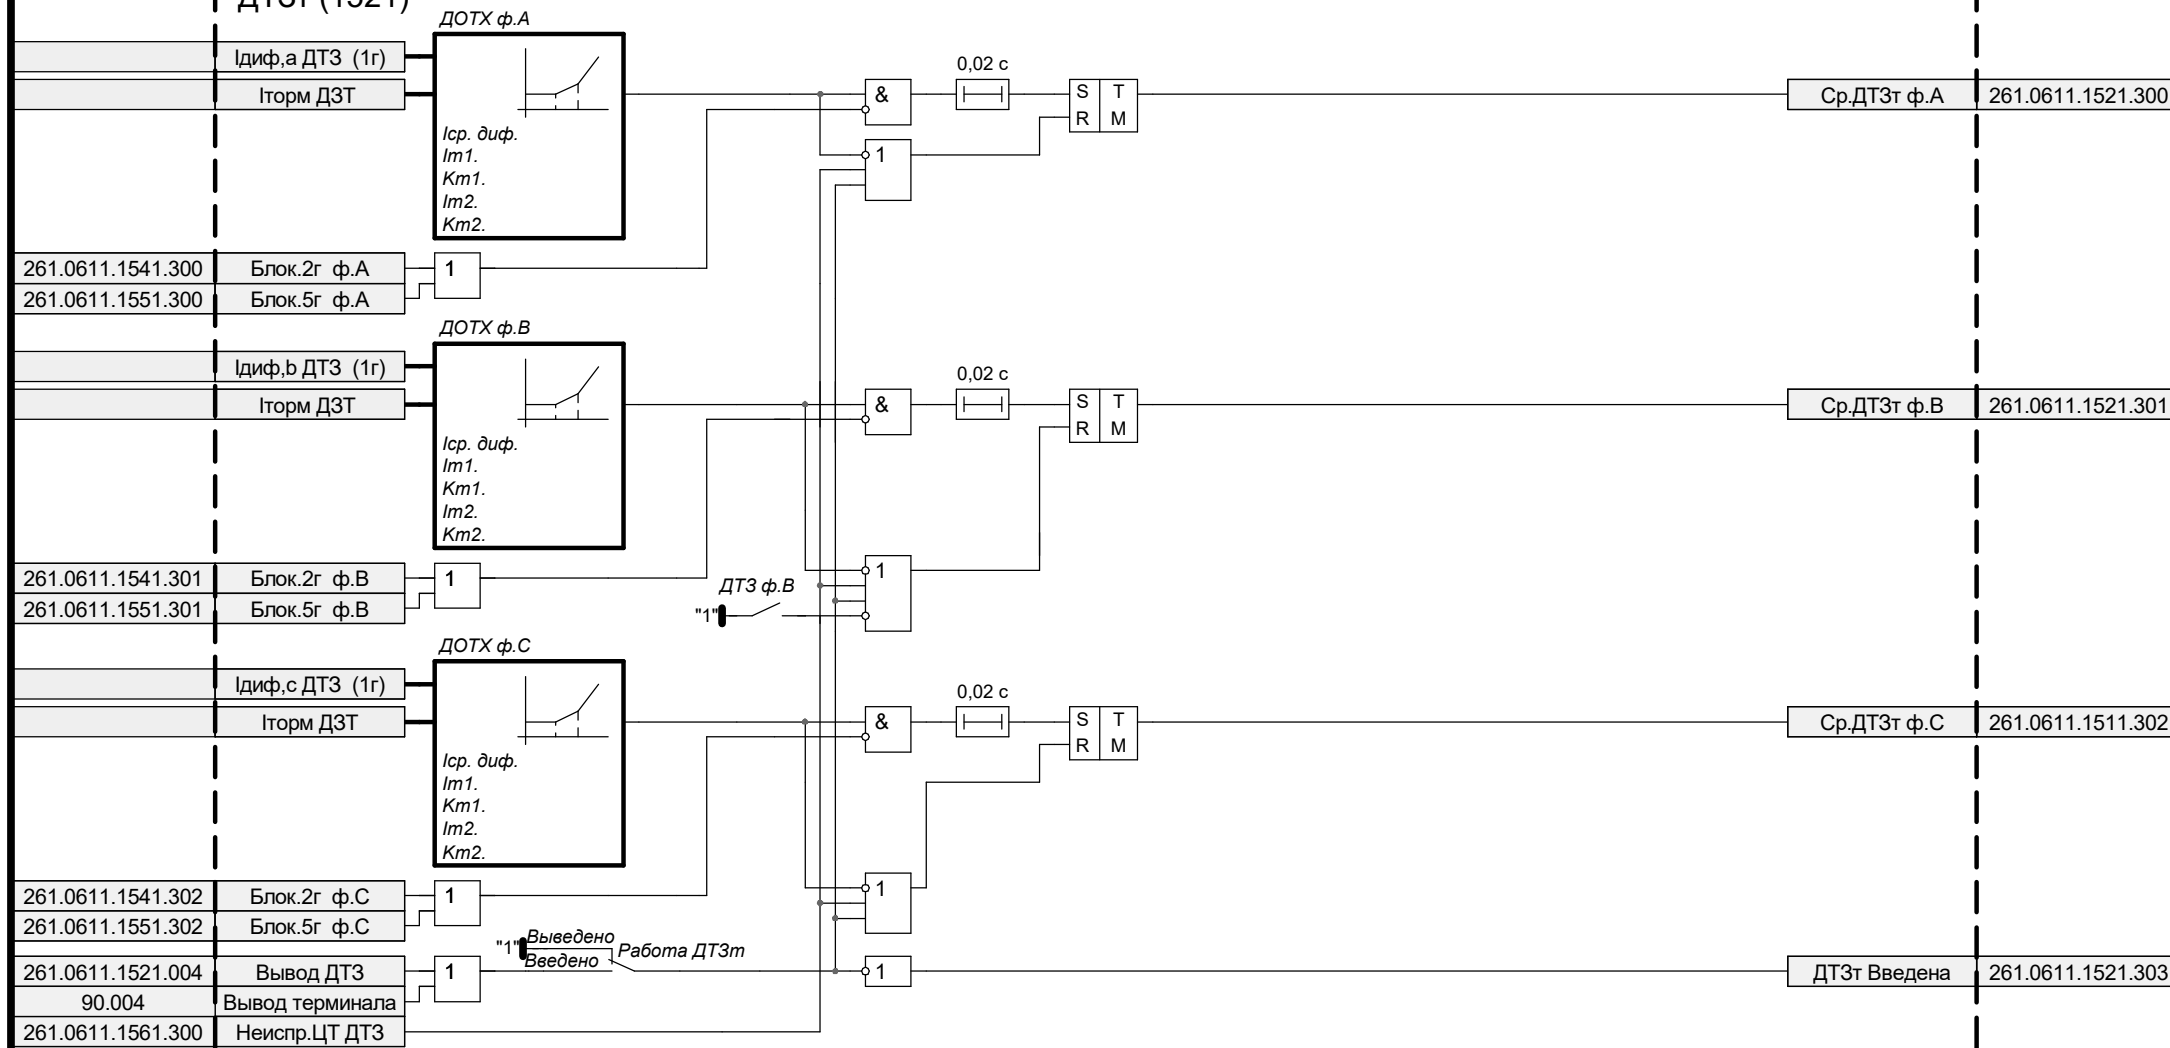

Д2г (1541)

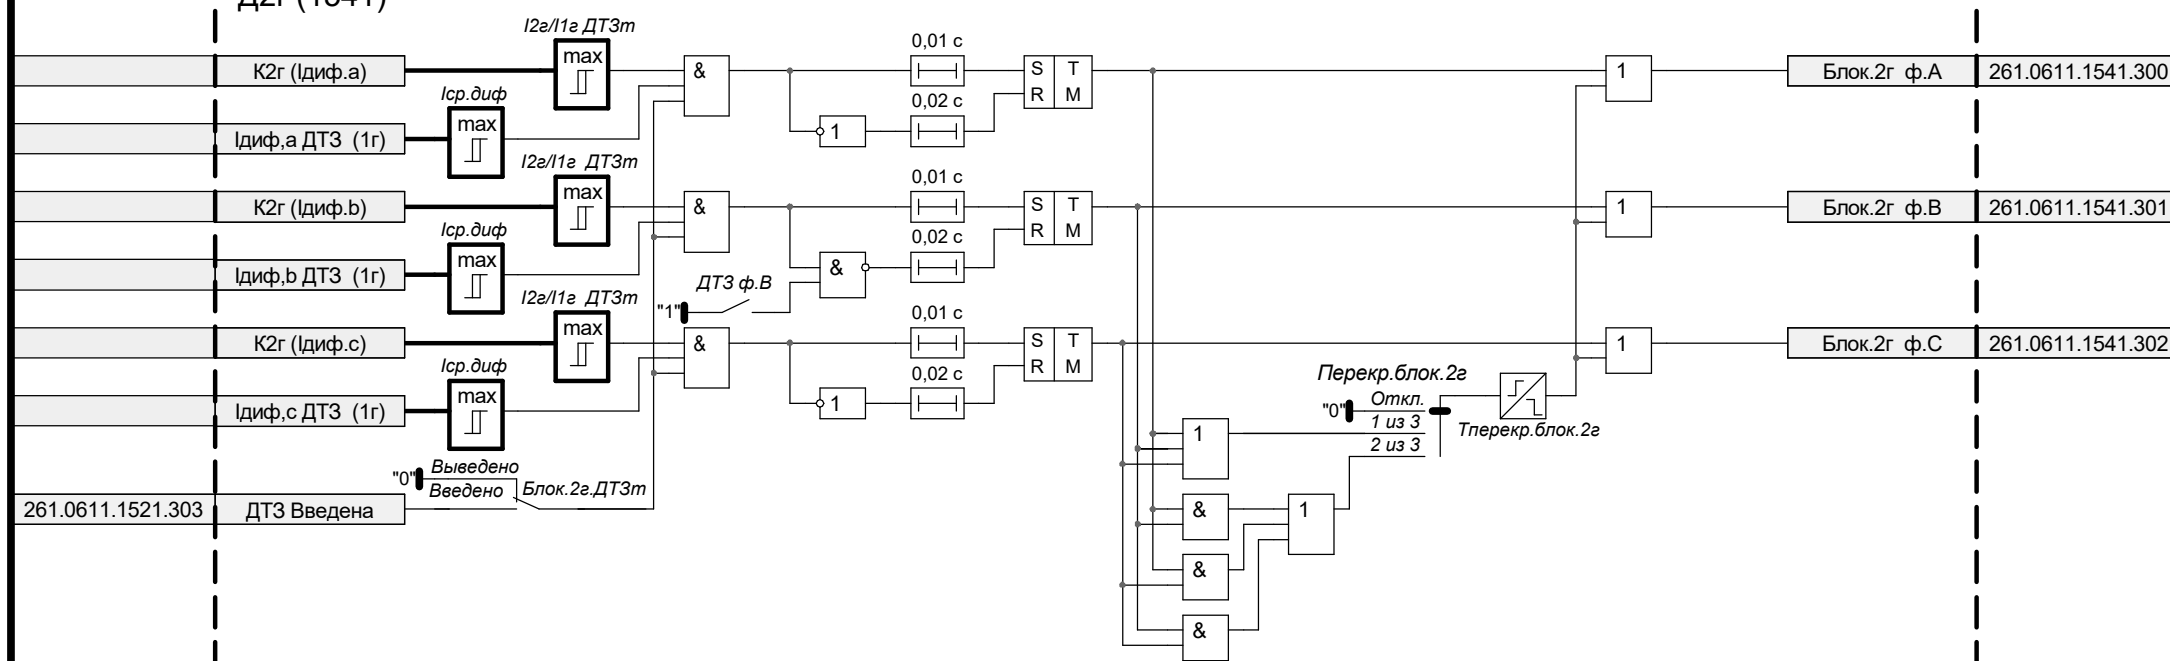


Д5г (1551)

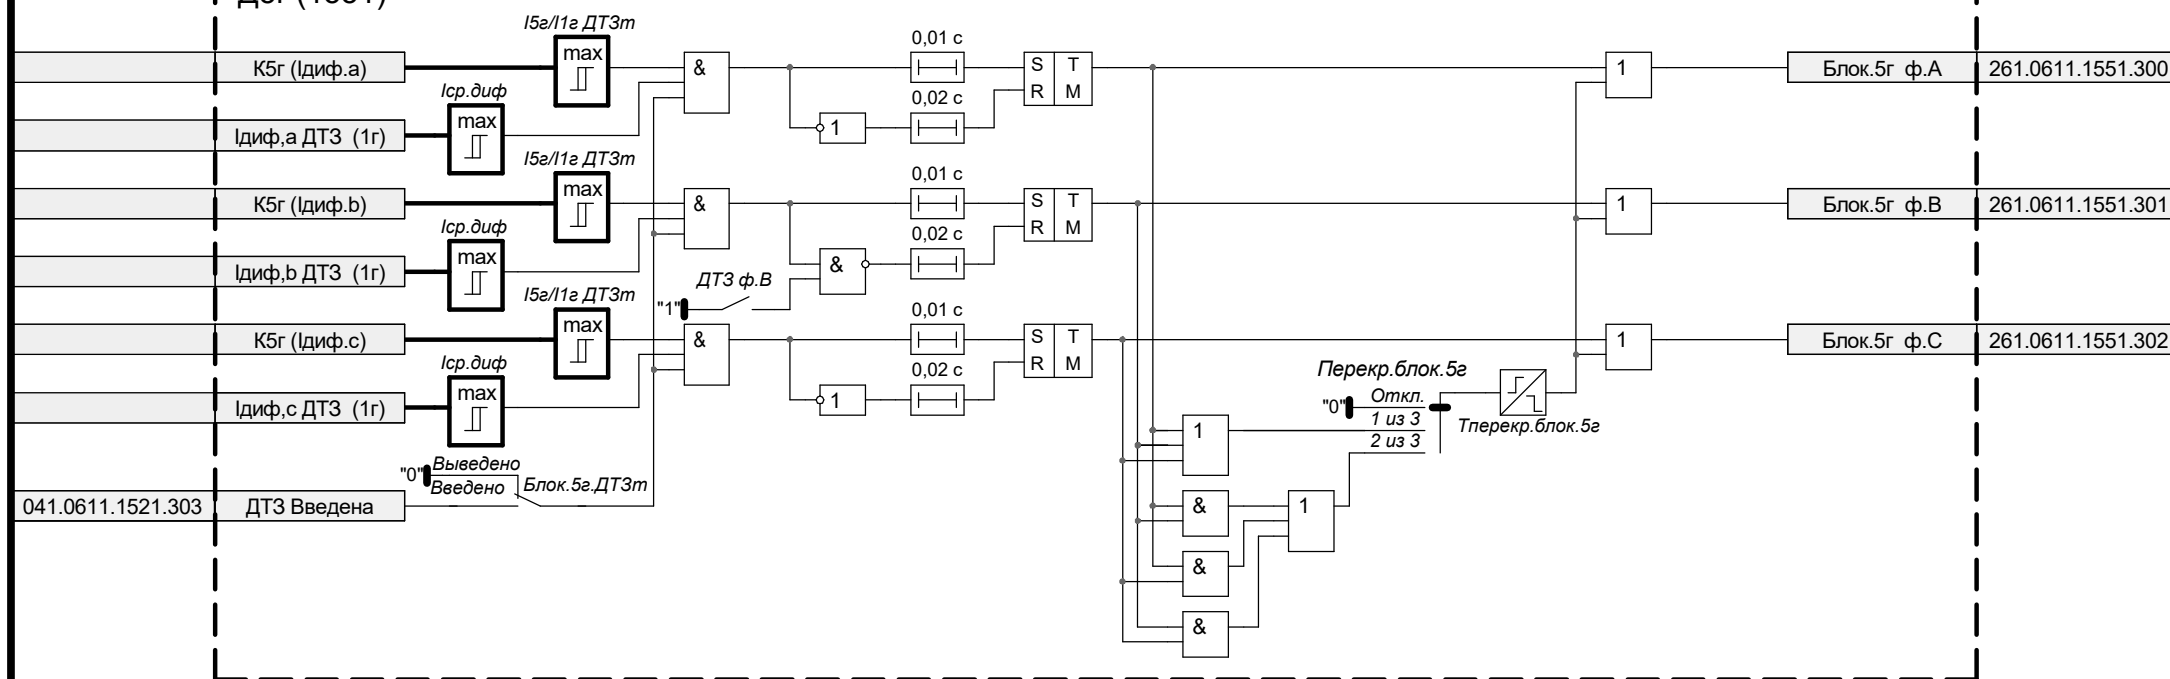


ДТЗ (261.0611)


ДТО (1511)

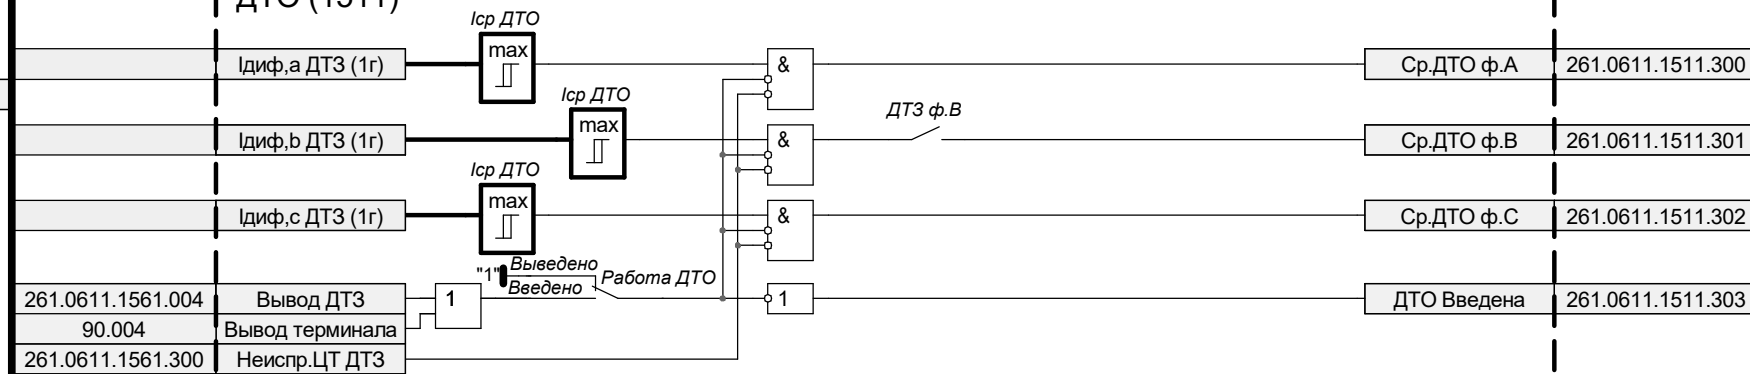

КЦТ (1561)

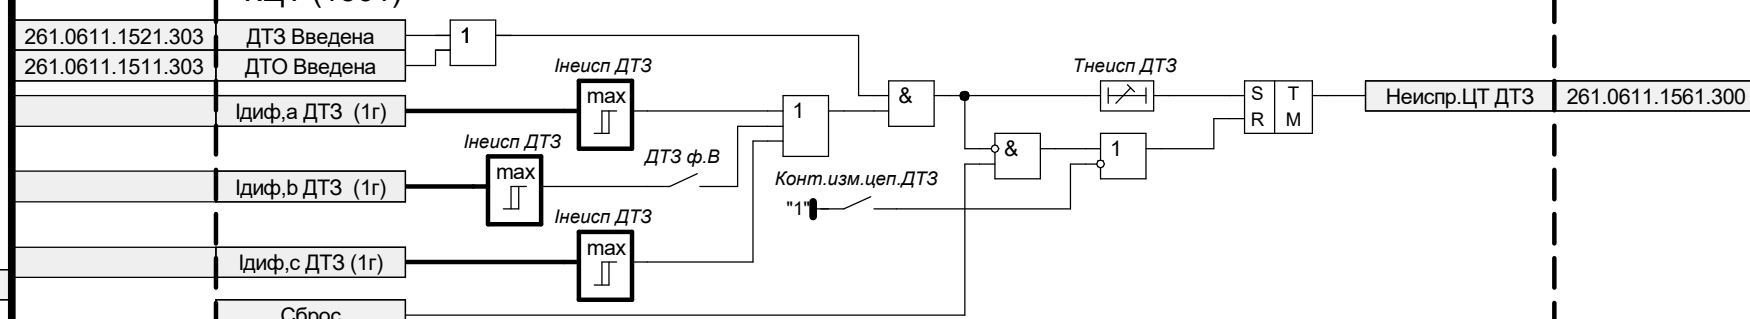


Общая логика (0011)

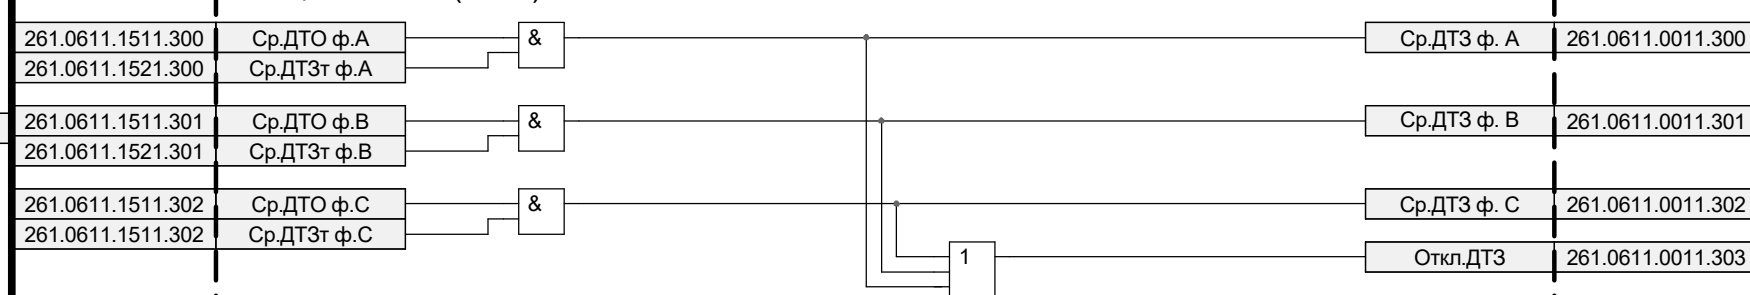


ДТЗ НП (261.0621)

ДТЗ НП (1631)

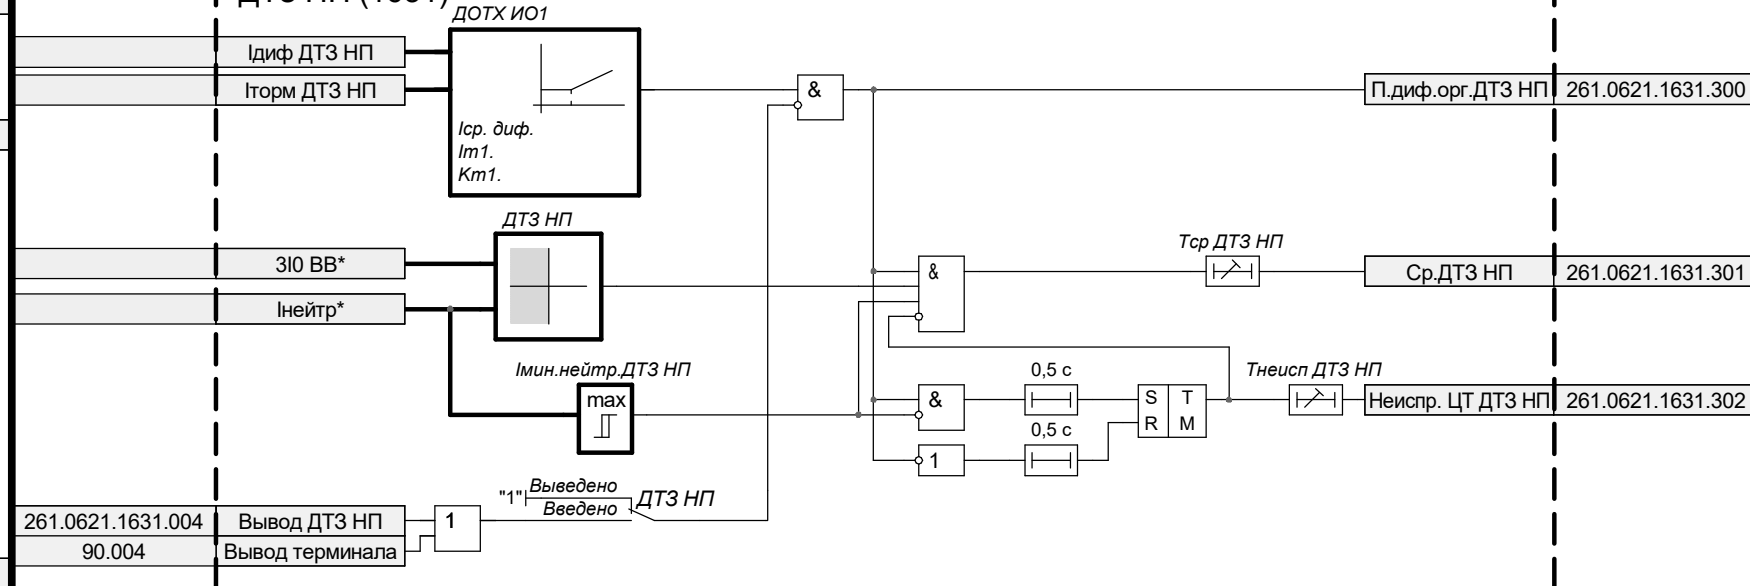


ТЗОП ВВ (271.0291)

ИО ТЗОП ВВ (0611)

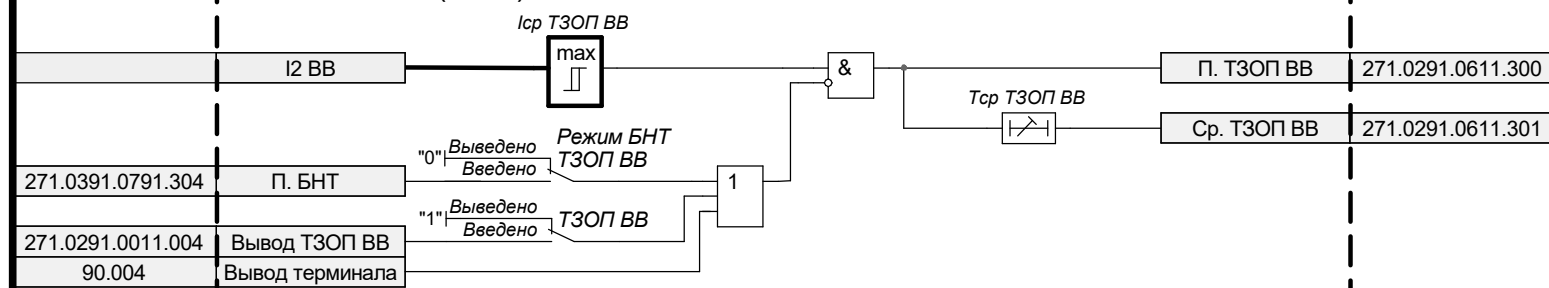


ОВ БНТ ВВ (271.0391)

ОВ БНТ (0791)

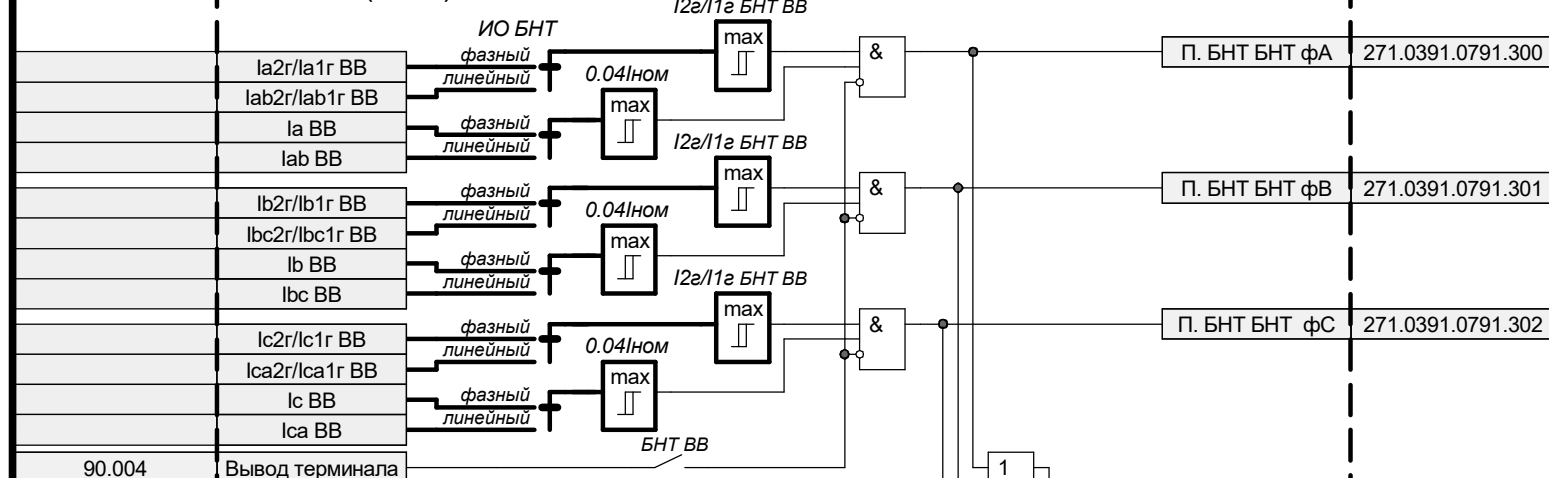


ЗНР (0271.0221)

ЗНР (0881)

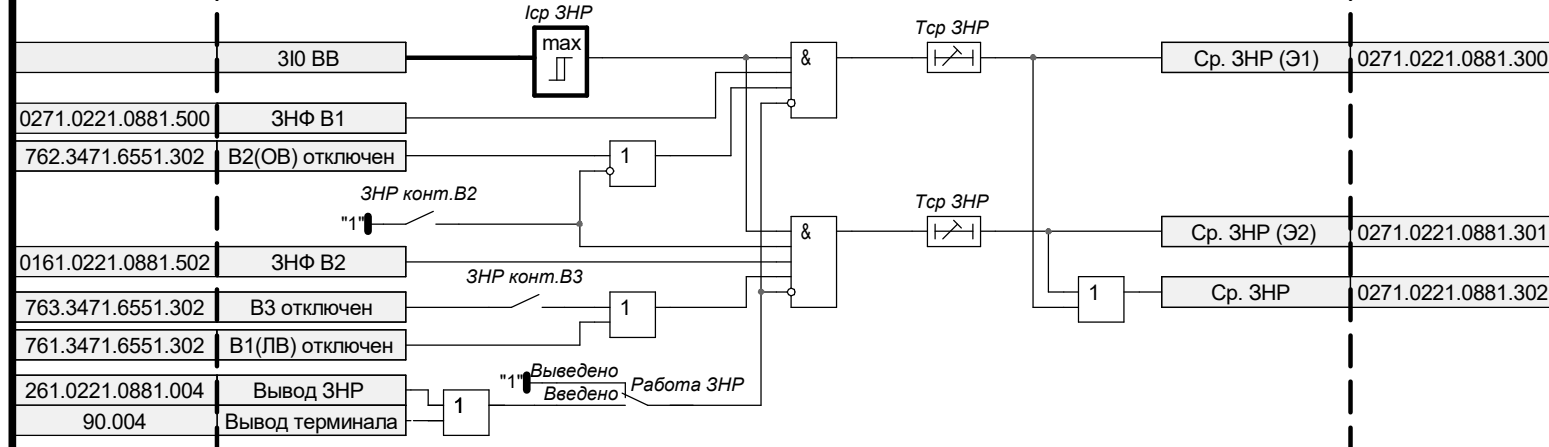


ЗПВГ (0261.0381)

ЗПВГ сигнальная ступень (0821)

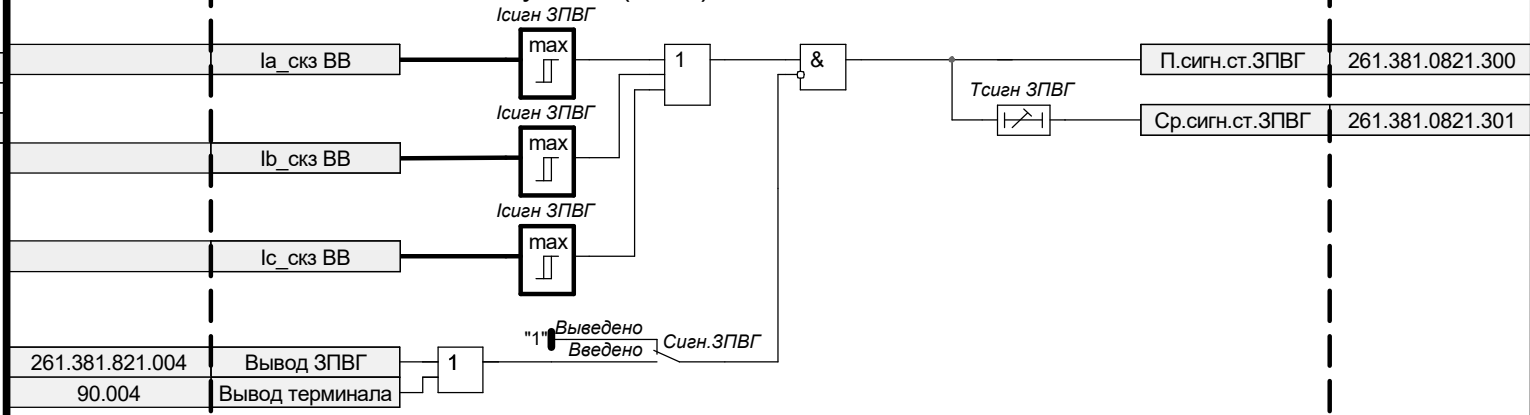


ЗПВГ отключающая ступень (0822)

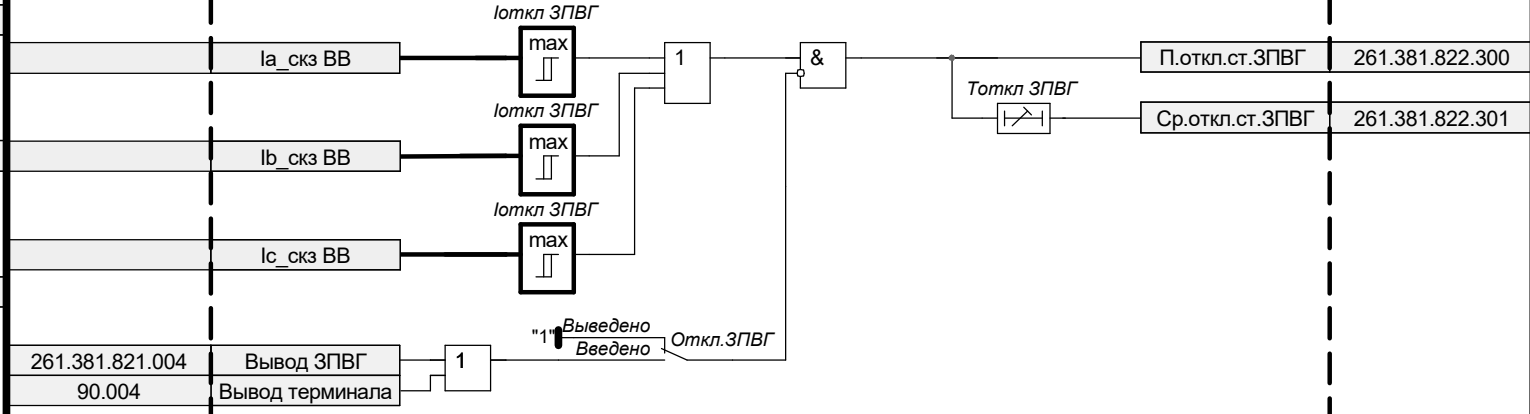


УРОВ В1(ЛВ) (761.3341)


УРОВ (5231)

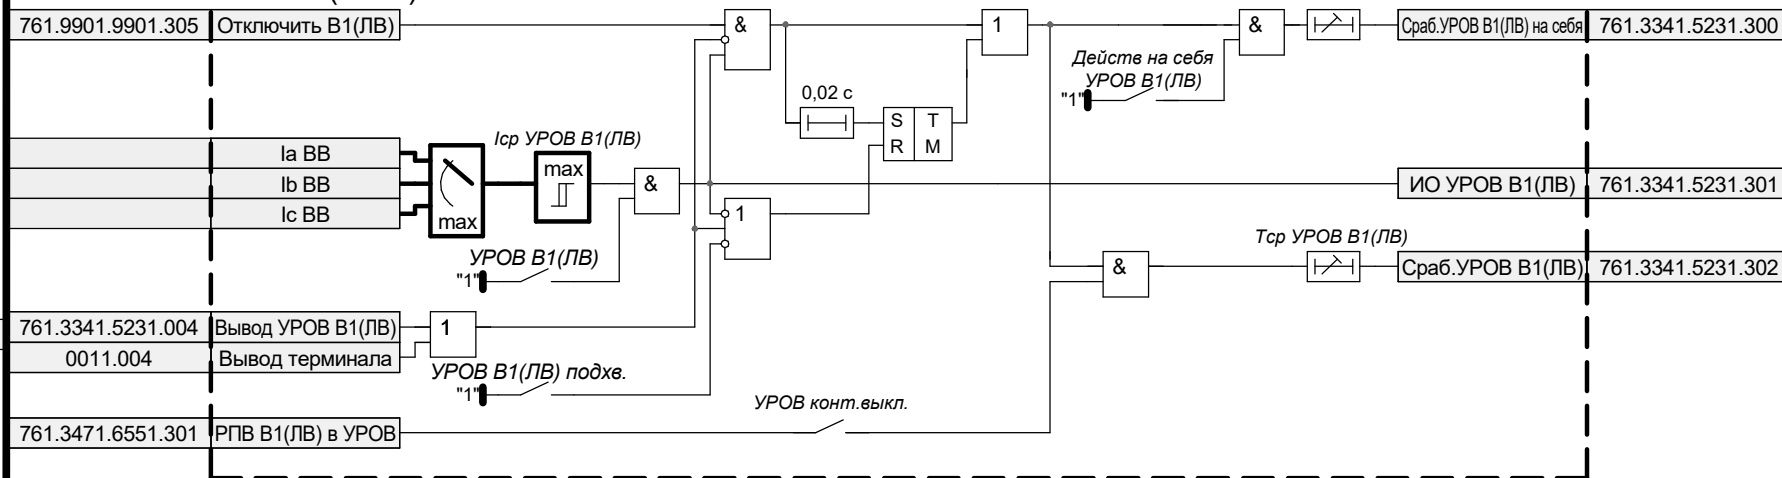

Блокировка при неисправности цепей напряжения (261.1461)

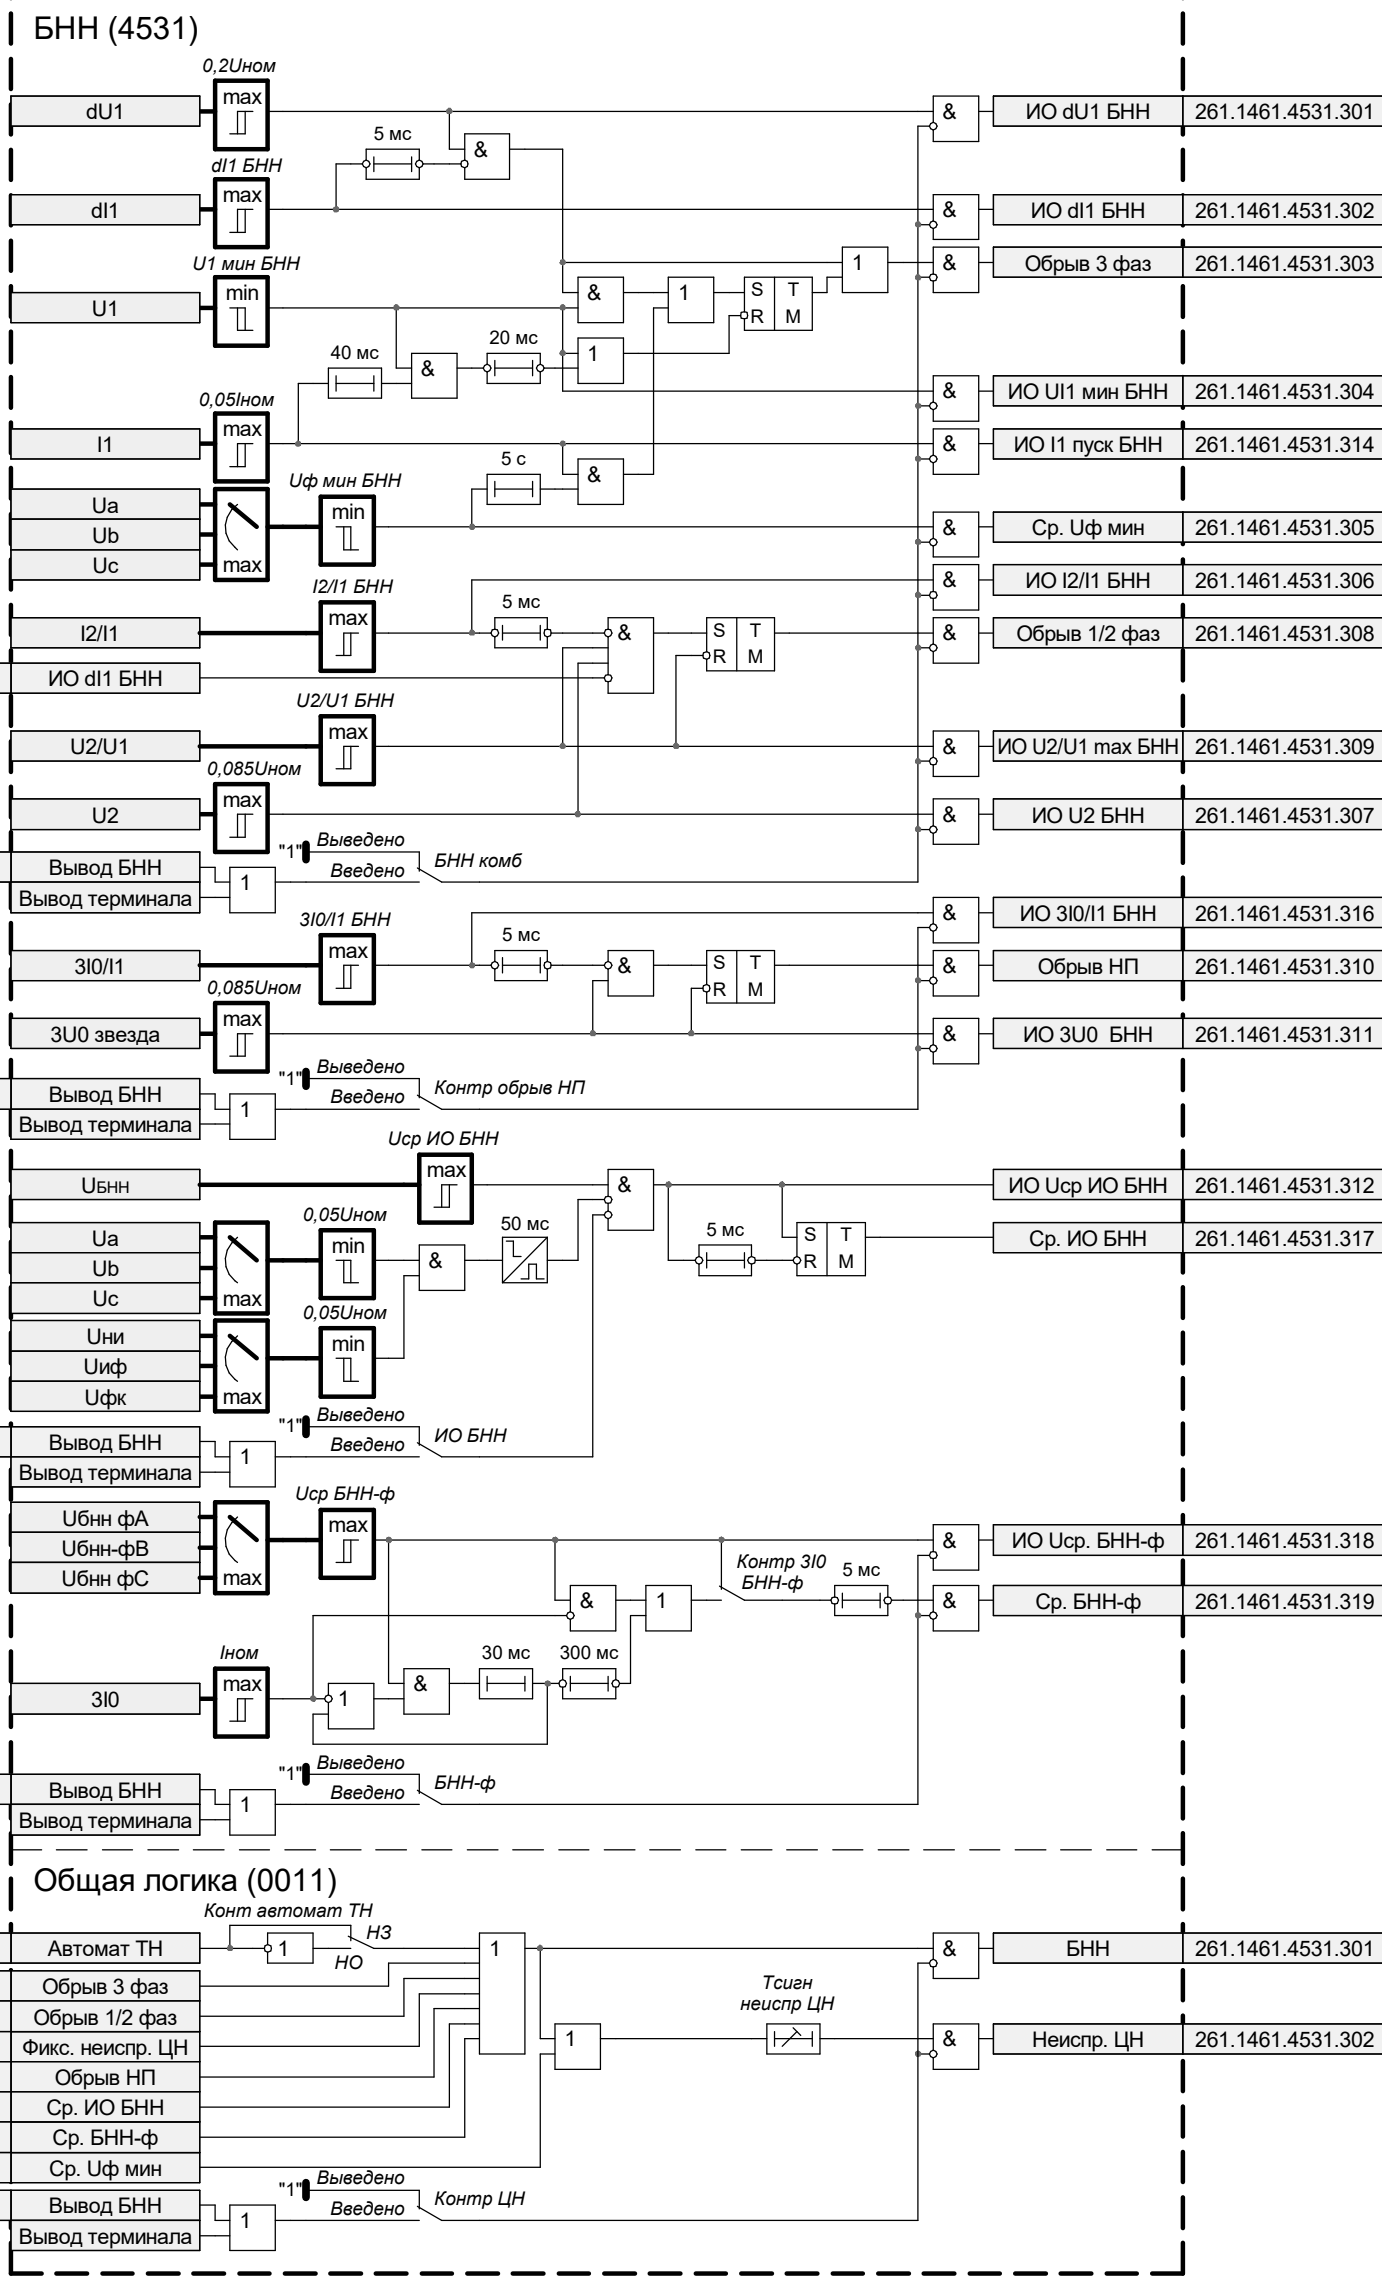


Логика сигнализации (91)

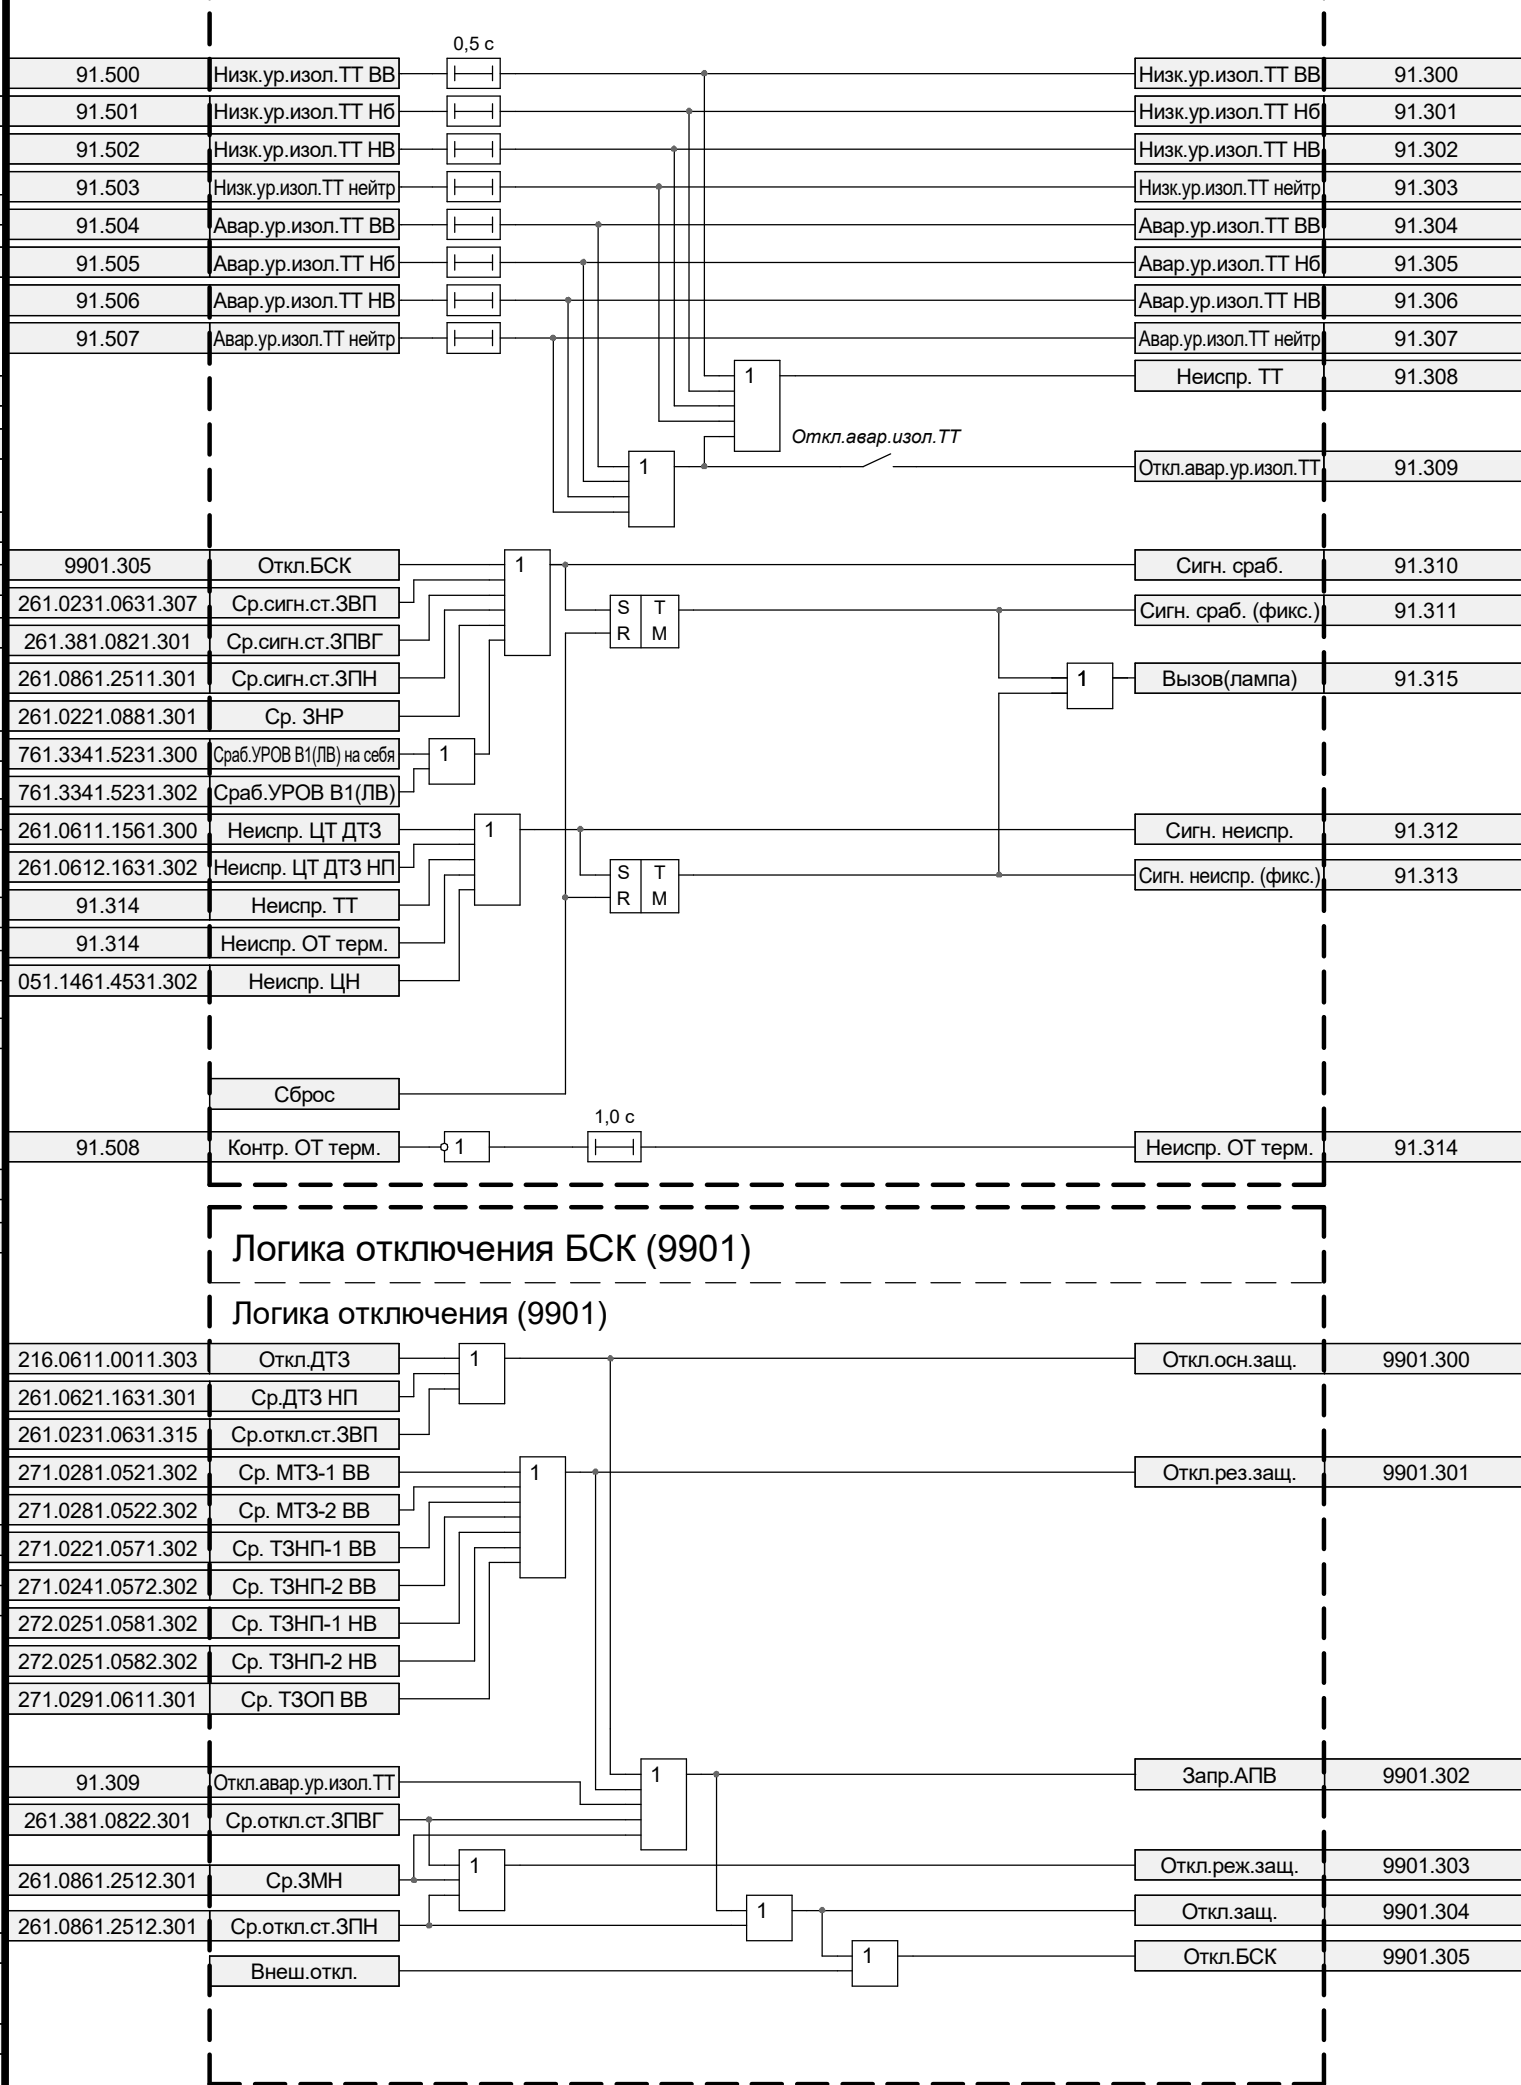


КСВ В1(ЛВ) (761.3371)


Контроль В1(ЛВ) (6571)

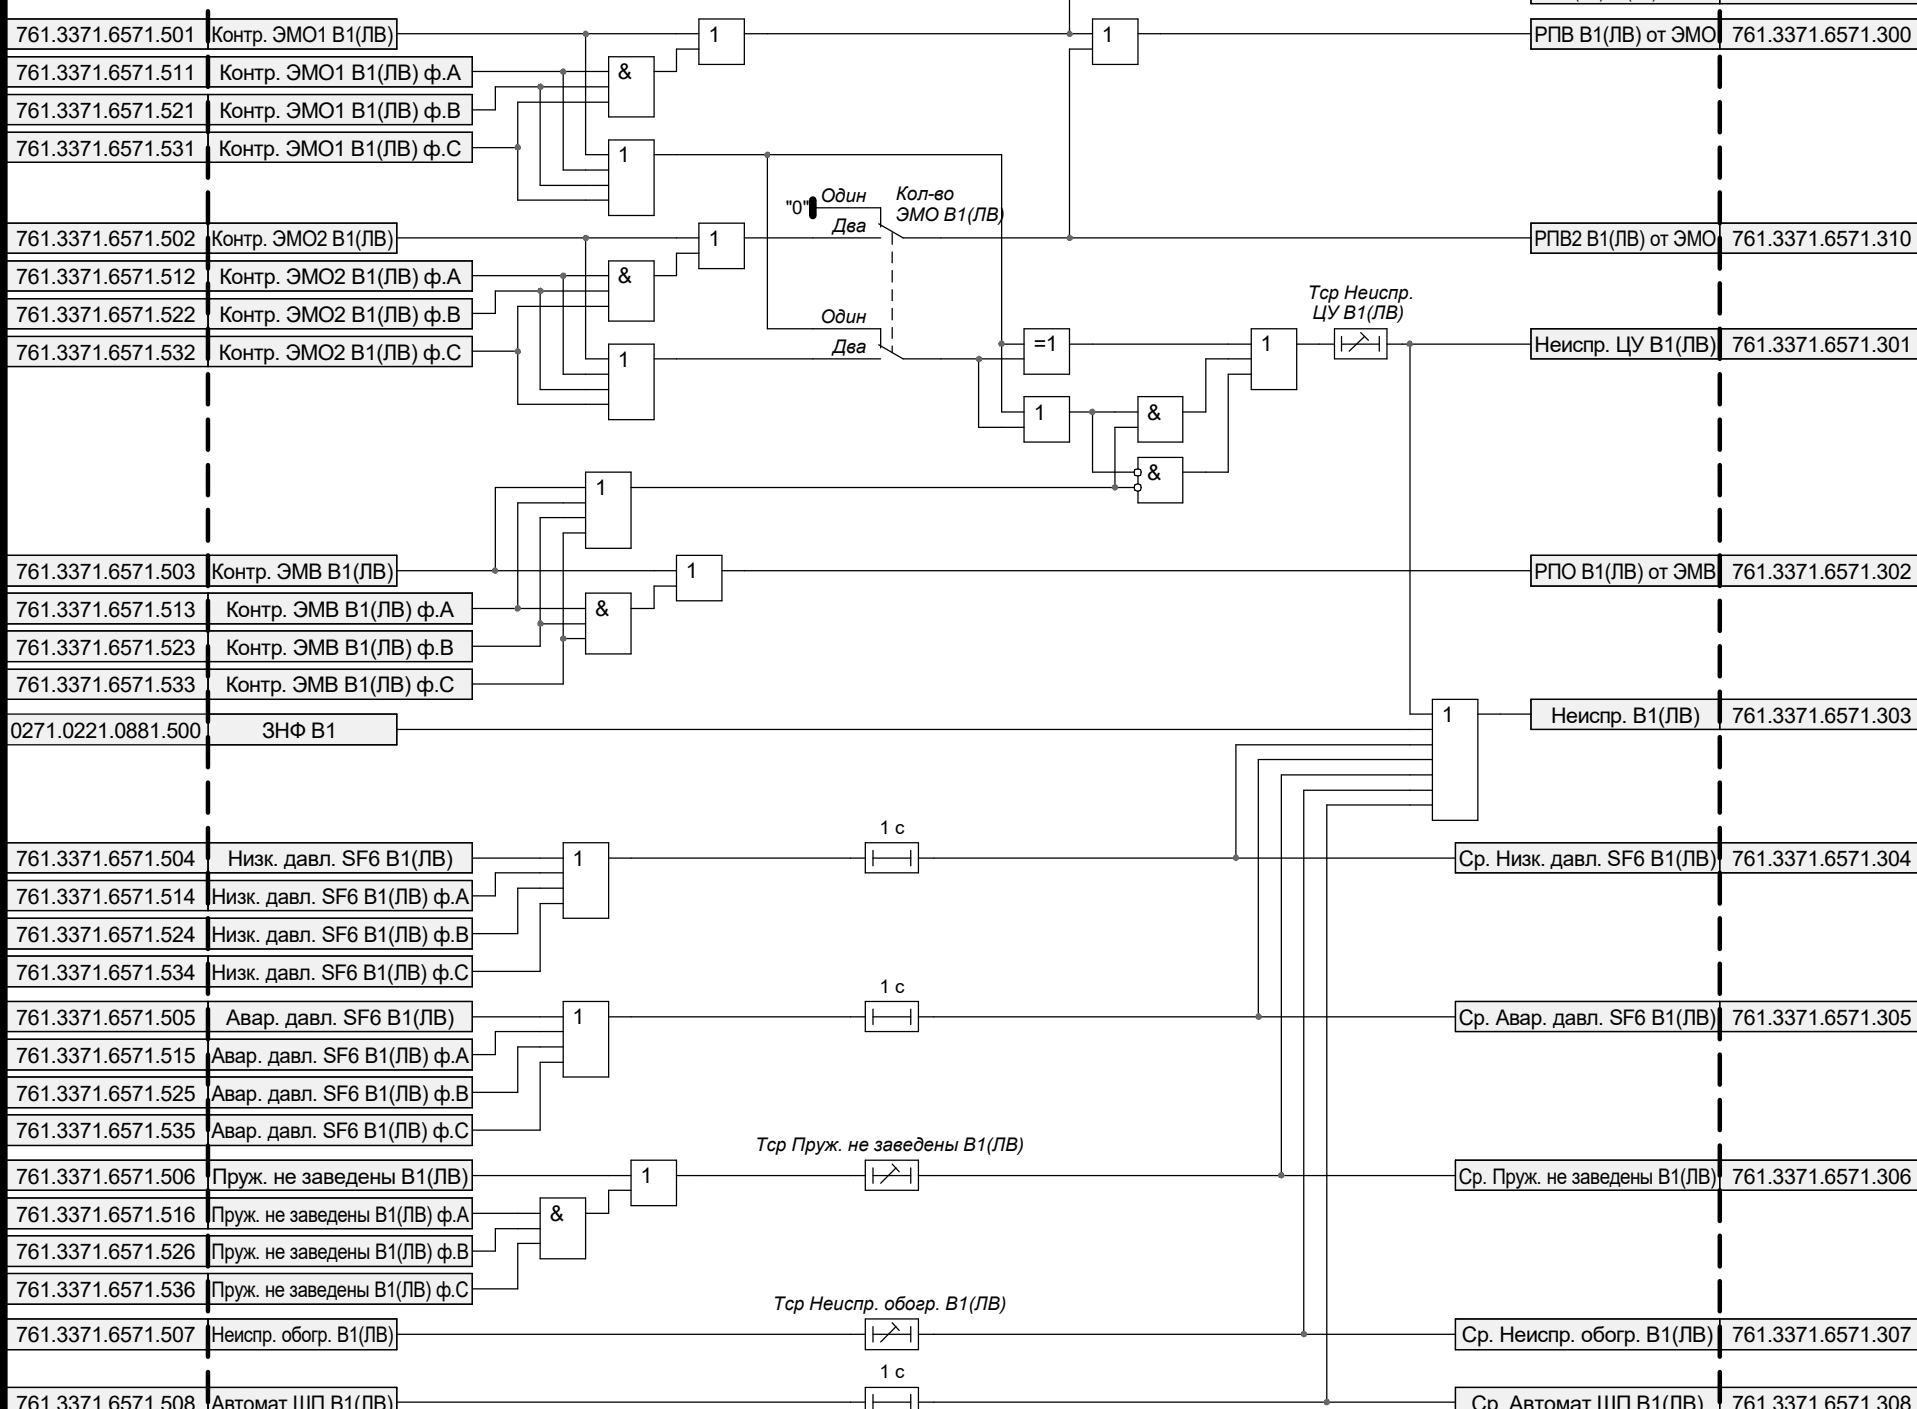


Контроль опертока В1(ЛВ) (6591)

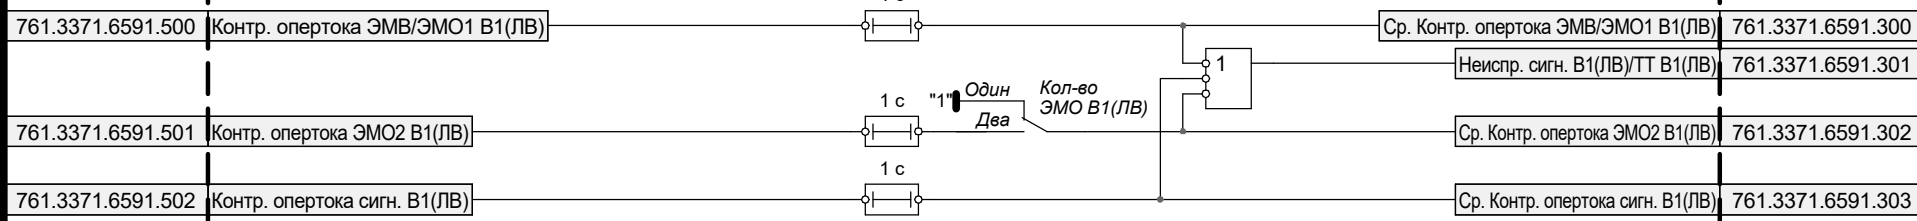

Блокировка управления В1(ЛВ) (6611)

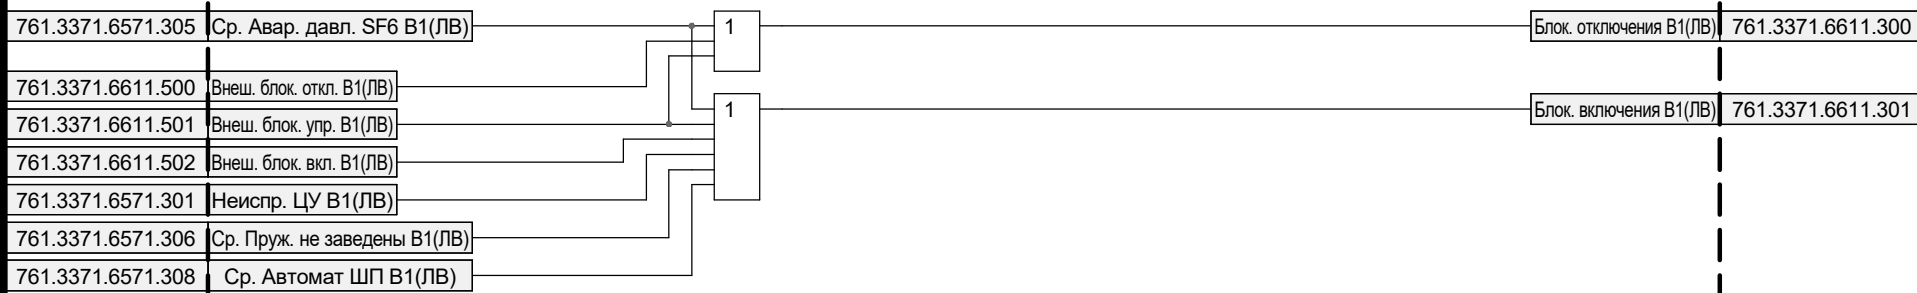


Защита ЭМУ В1(ЛВ) (6601)

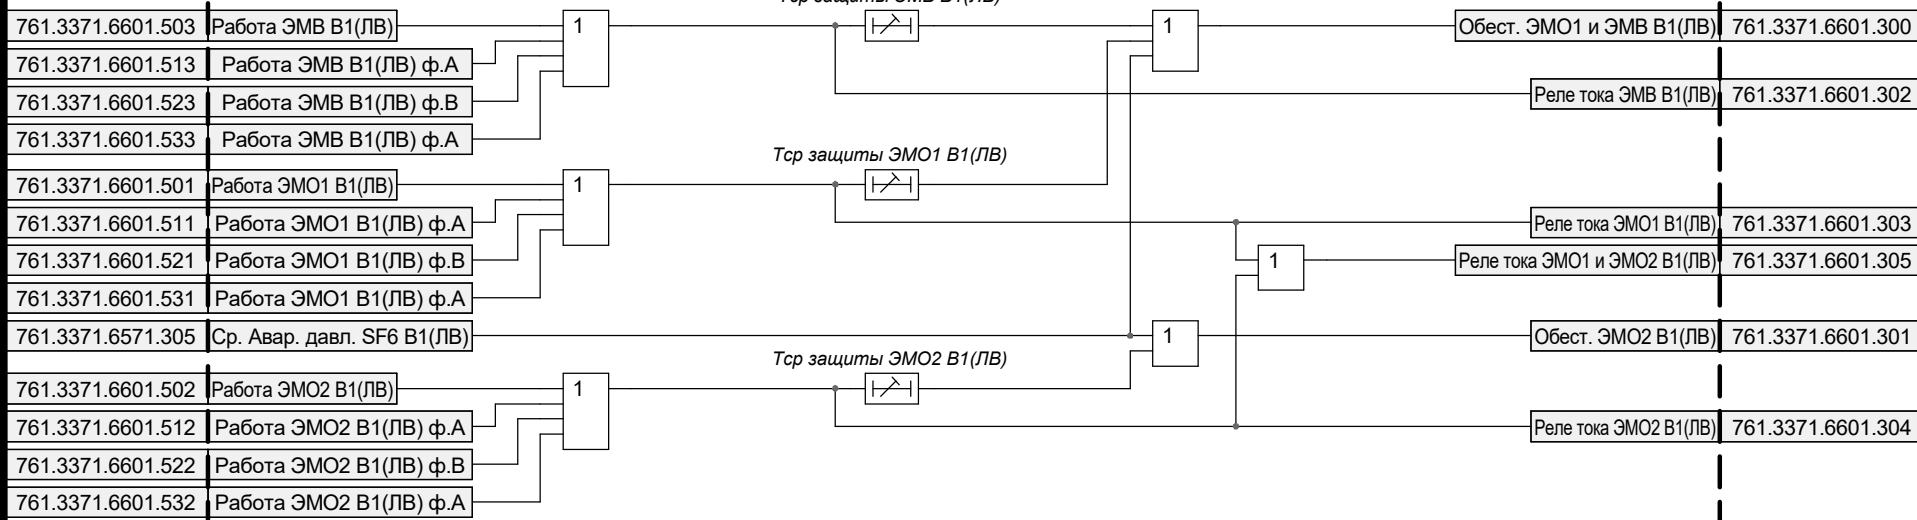


КСВ В1(ЛВ) (761.3371)

Контроль ТТ В1(ЛВ) (6581)

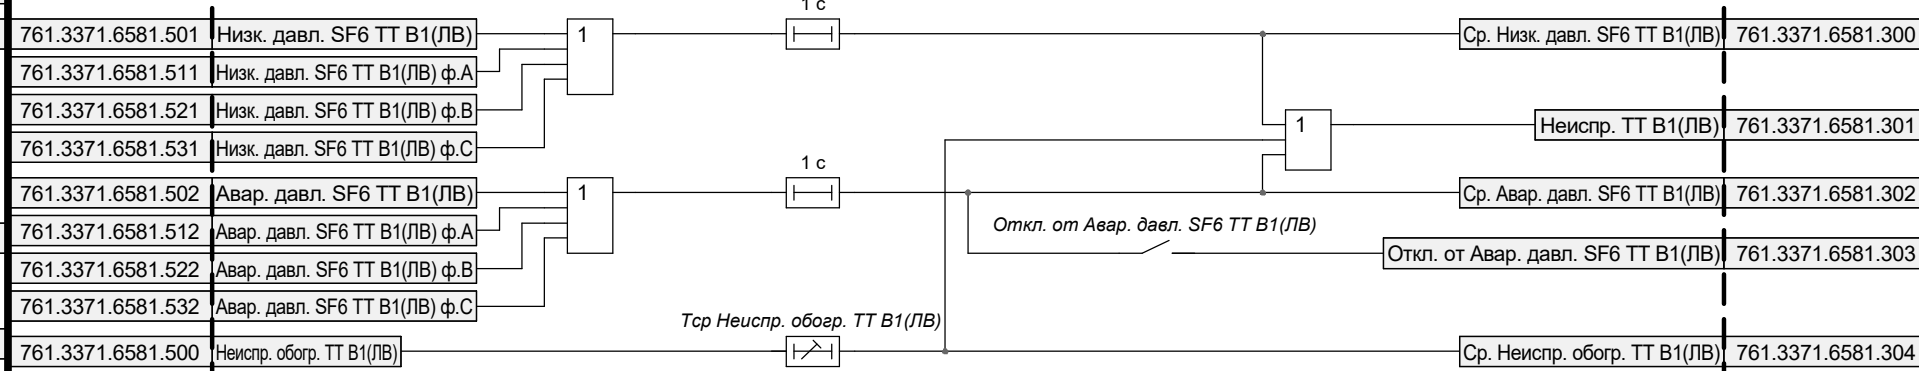


Реле фиксации В1(ЛВ) (6621)

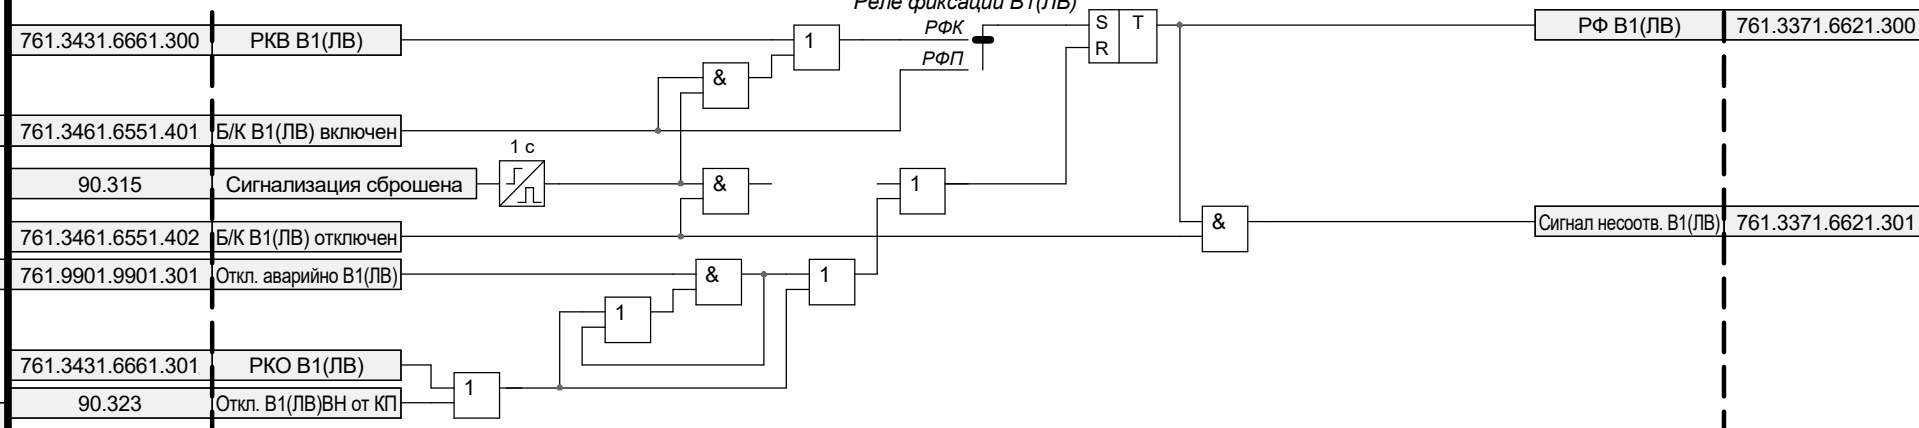

Управление выключателем В1(ЛВ) (761.3391)

Управление выключателем (6651)

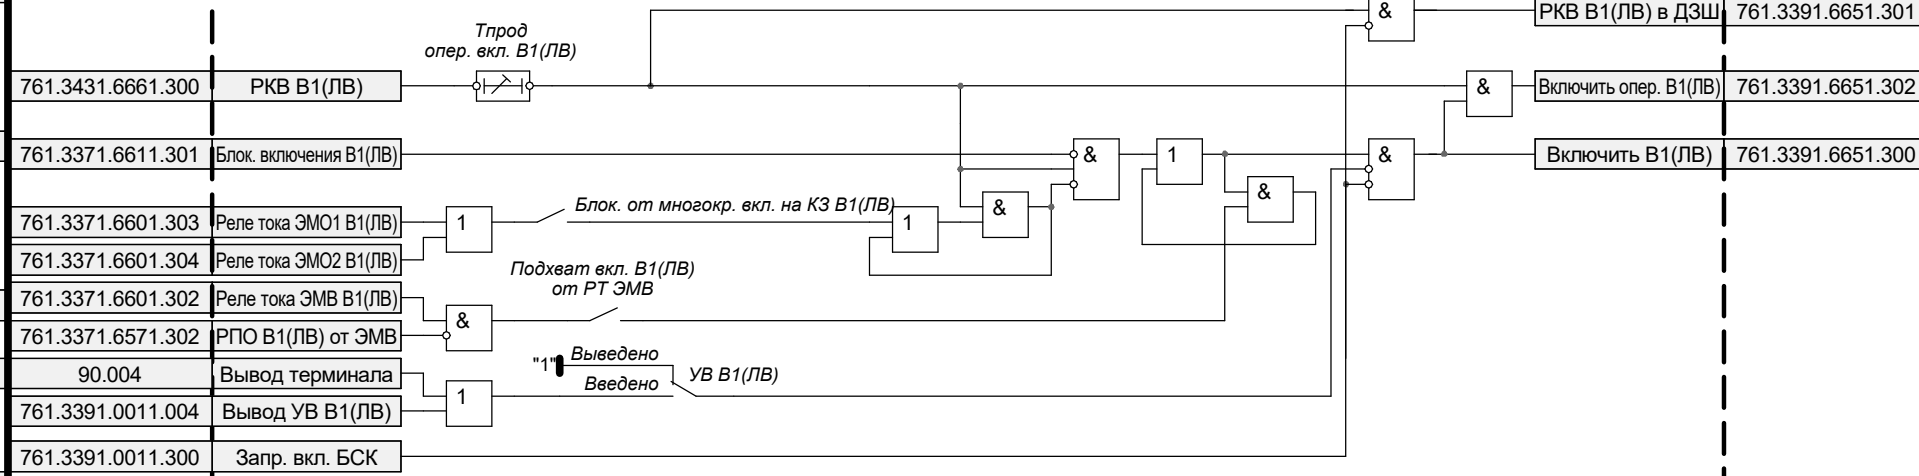

Общая логика (0011)

