


Питание оперативных цепей
Питание ИЧМ
Питание ИЗУ
Контроль положения испытательных блоков
Контроль положения переключателей
Контроль положения дверей шкафа
Внешнее отключение
Положение В1
ЗНФ В1
Положение В2
ЗНФ В2
Положение В3

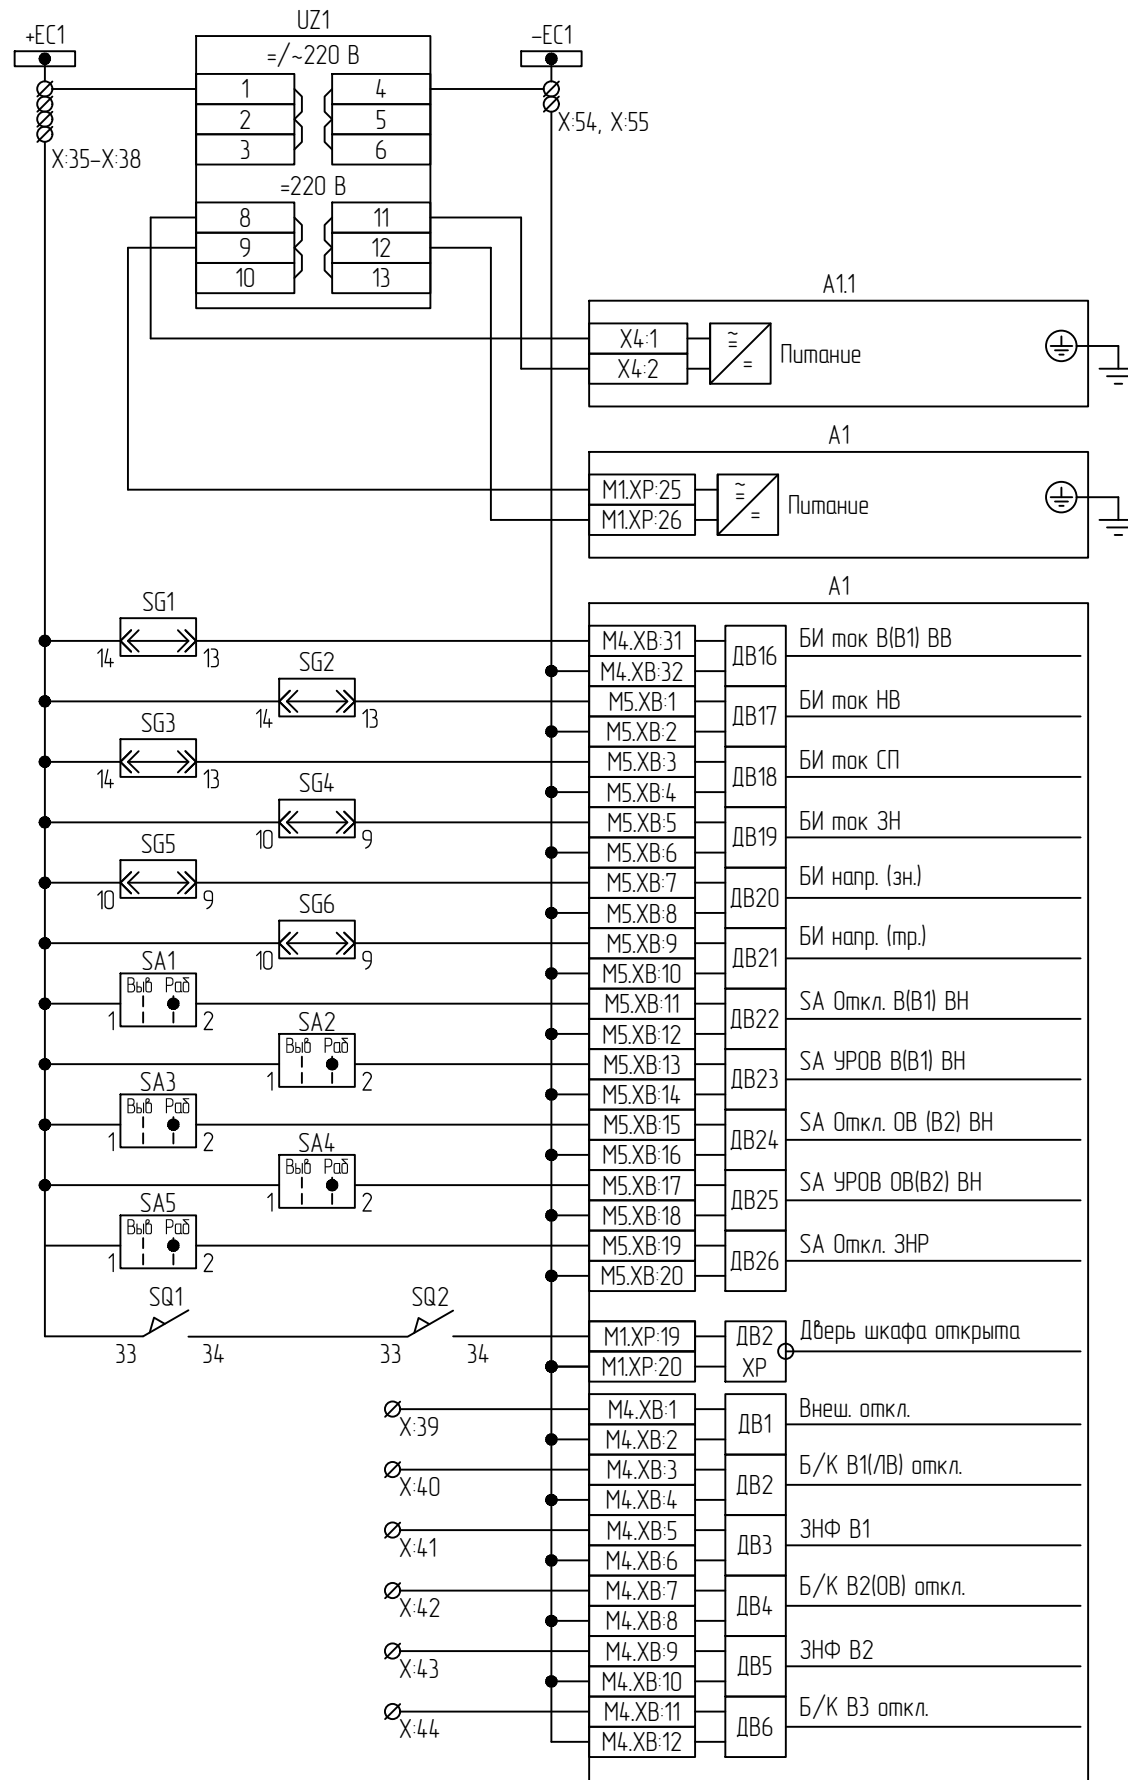

Контроль оперттока технологической сигнализацции
Аварийный уровень изоляции ТТ ВН БСК
Низкий уровень изоляции ТТ ВН БСК
Аварийный уровень изоляции ТТ средней перемычки
Низкий уровень изоляции ТТ средней перемычки
Аварийный уровень изоляции фазных ТТ нейтрал
Низкий уровень изоляции фазных ТТ нейтрал
Аварийный уровень изоляции ТТ нейтрал
Низкий уровень изоляции ТТ нейтрал

