




Цепи оперативного тока

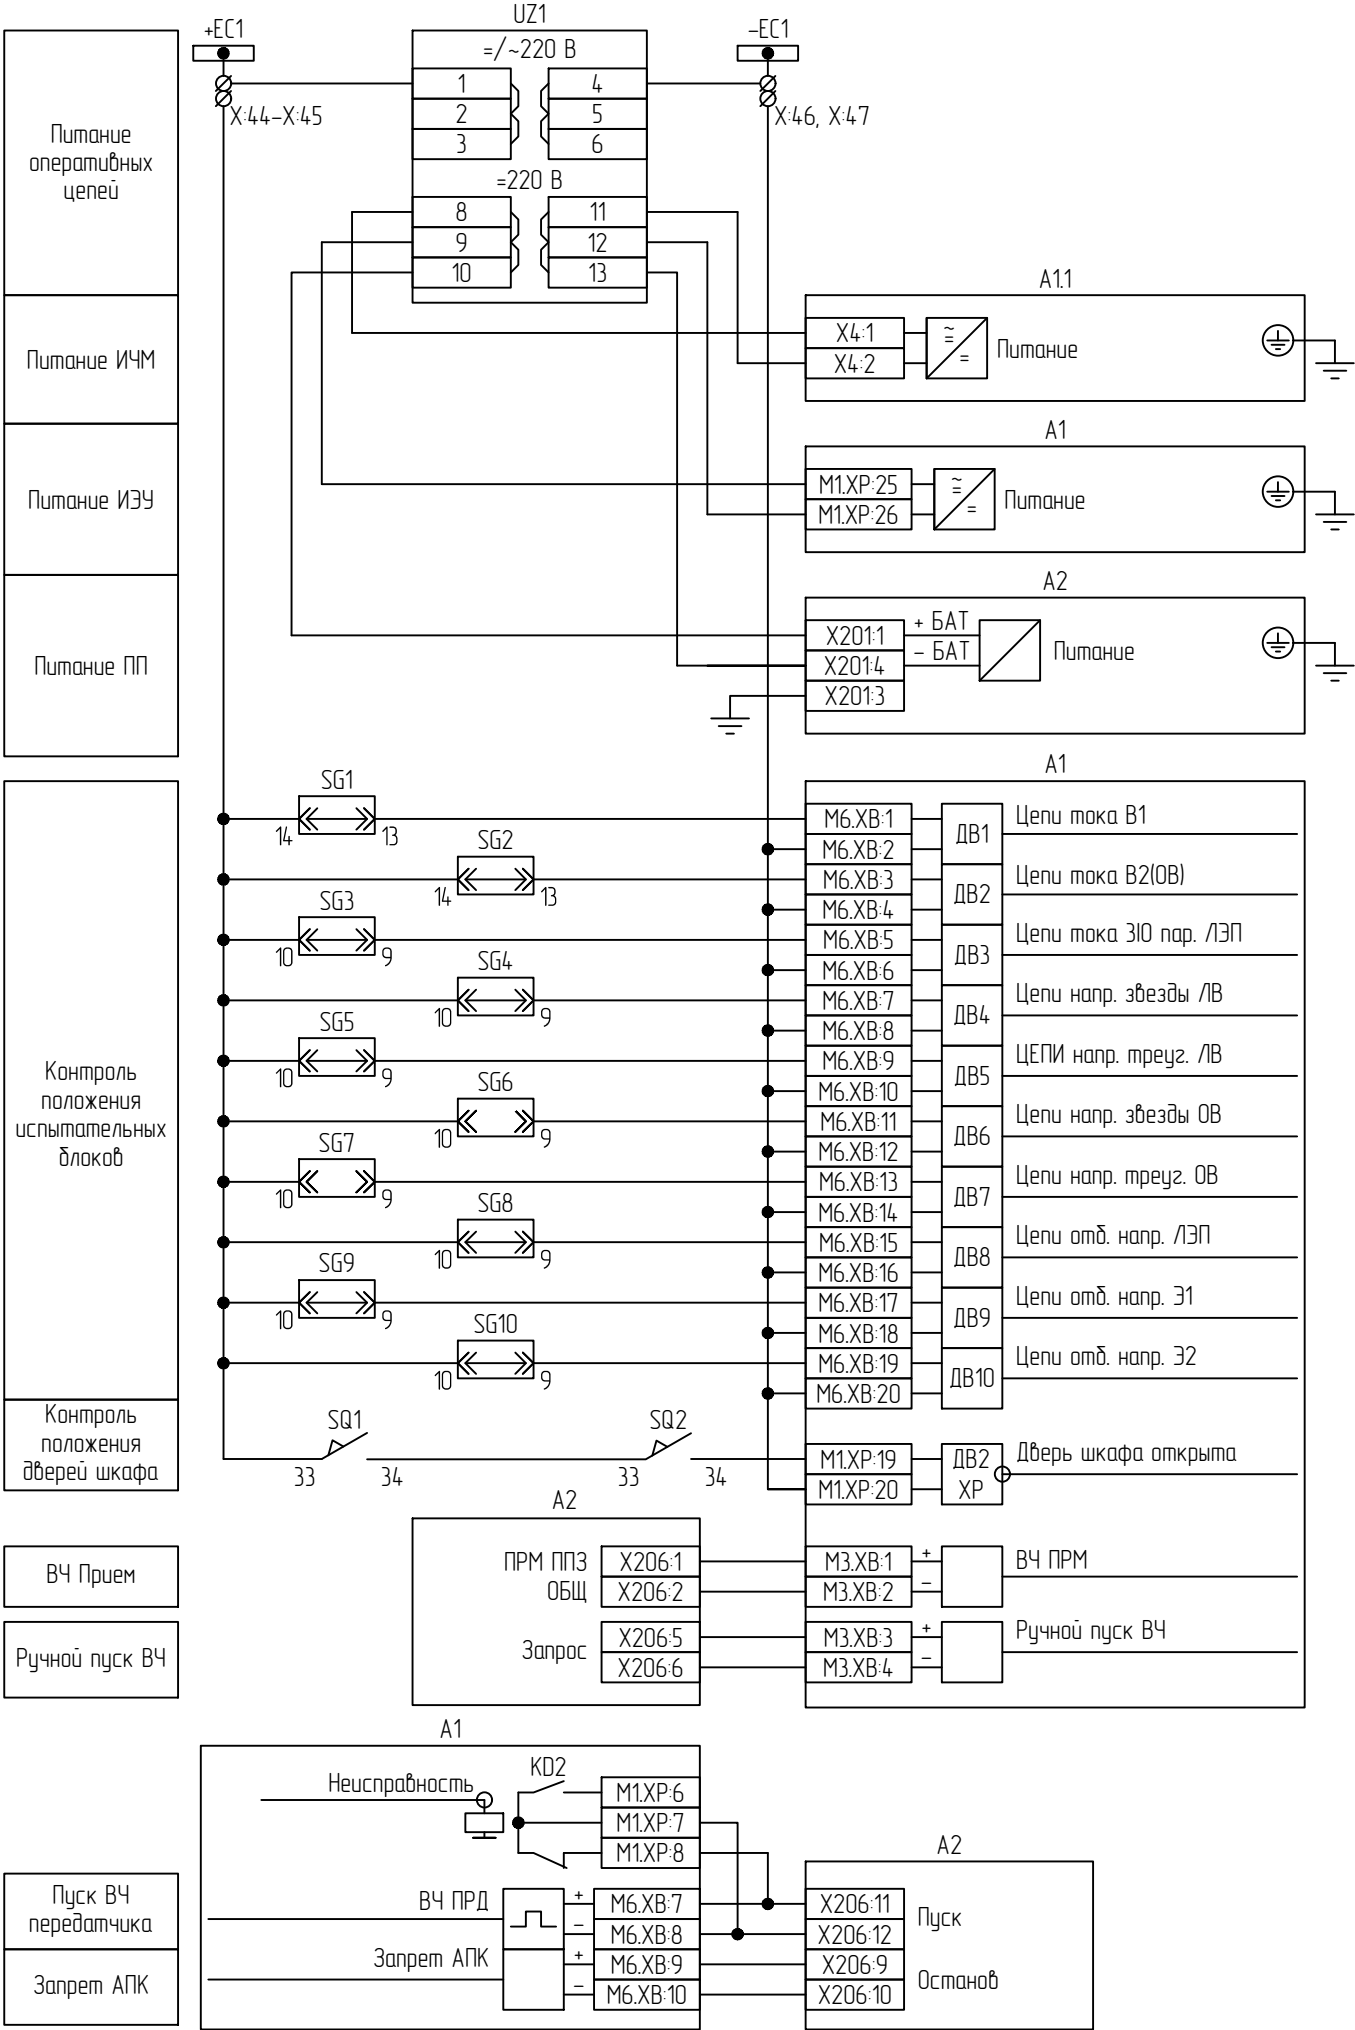


Цепи сигнализации

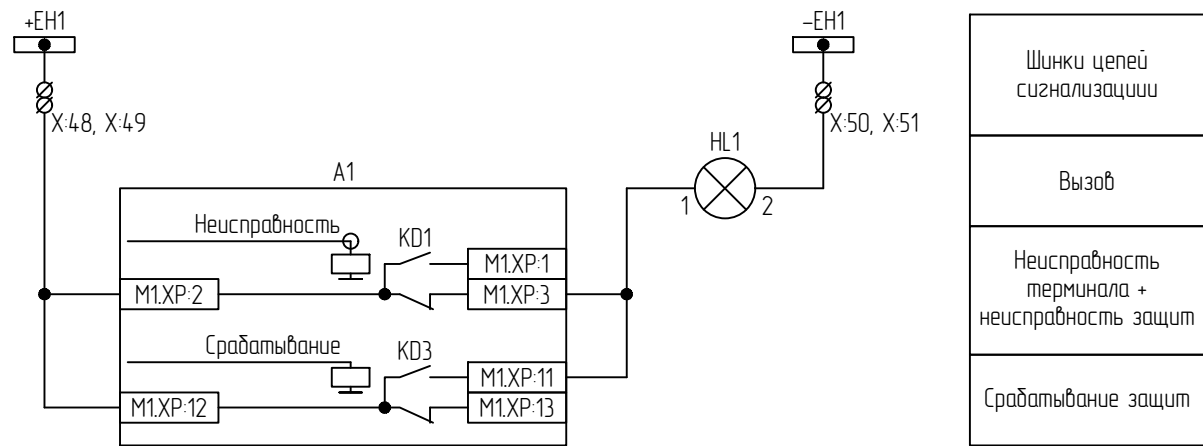

Цепи портов связи терминала

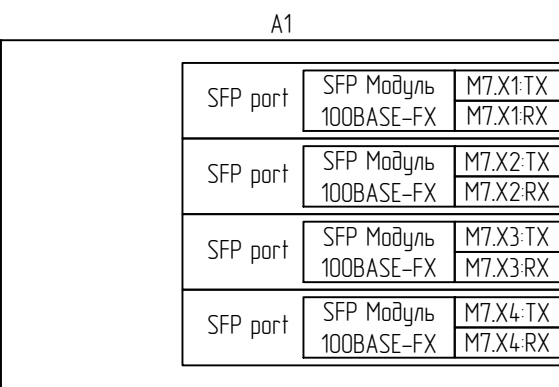

Цепи связи терминала с ИЧМ

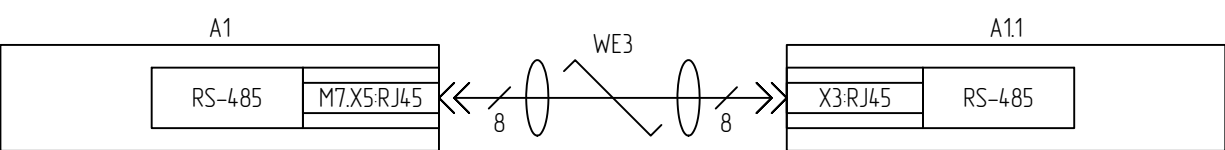

Цепи освещения шкафа

