

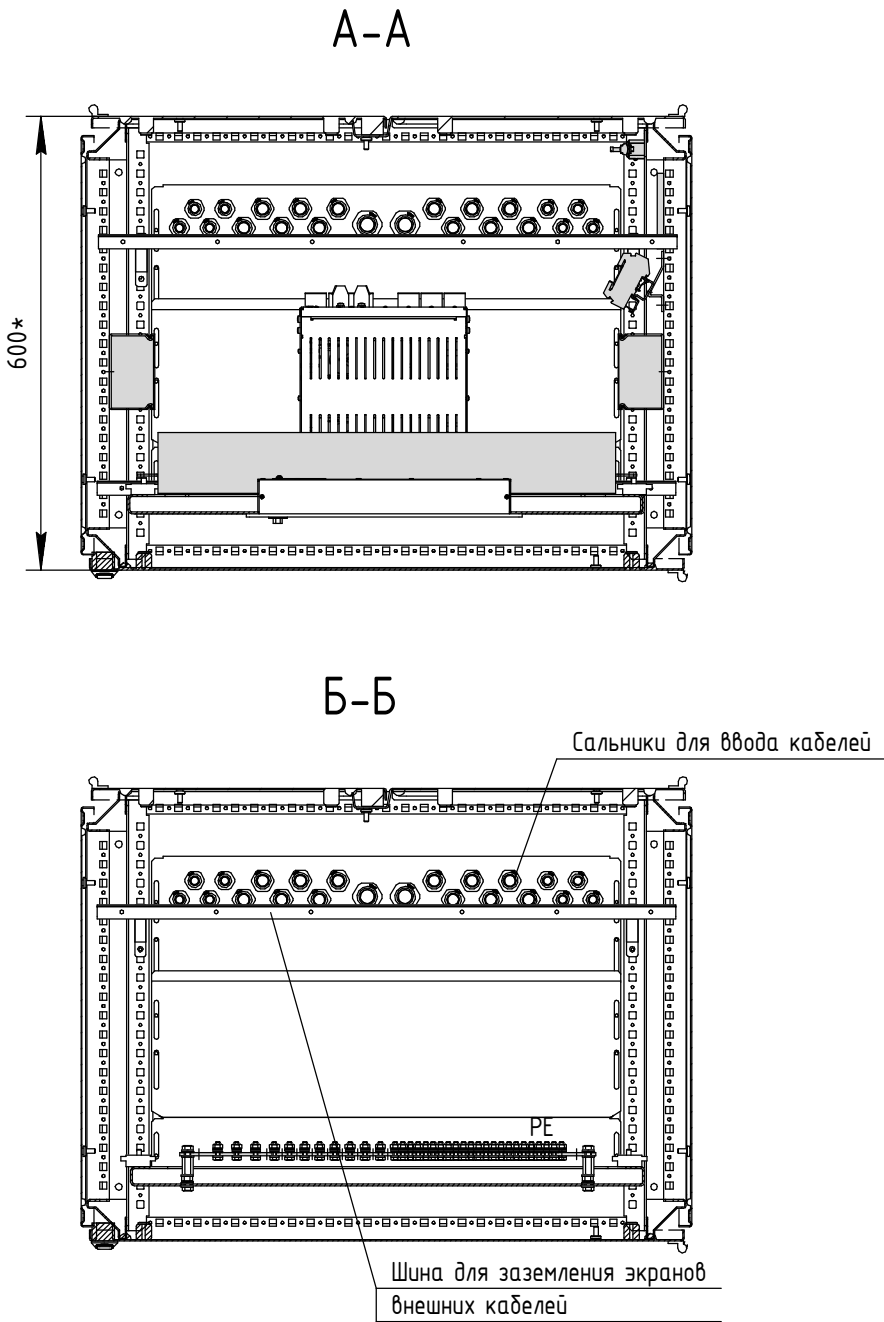


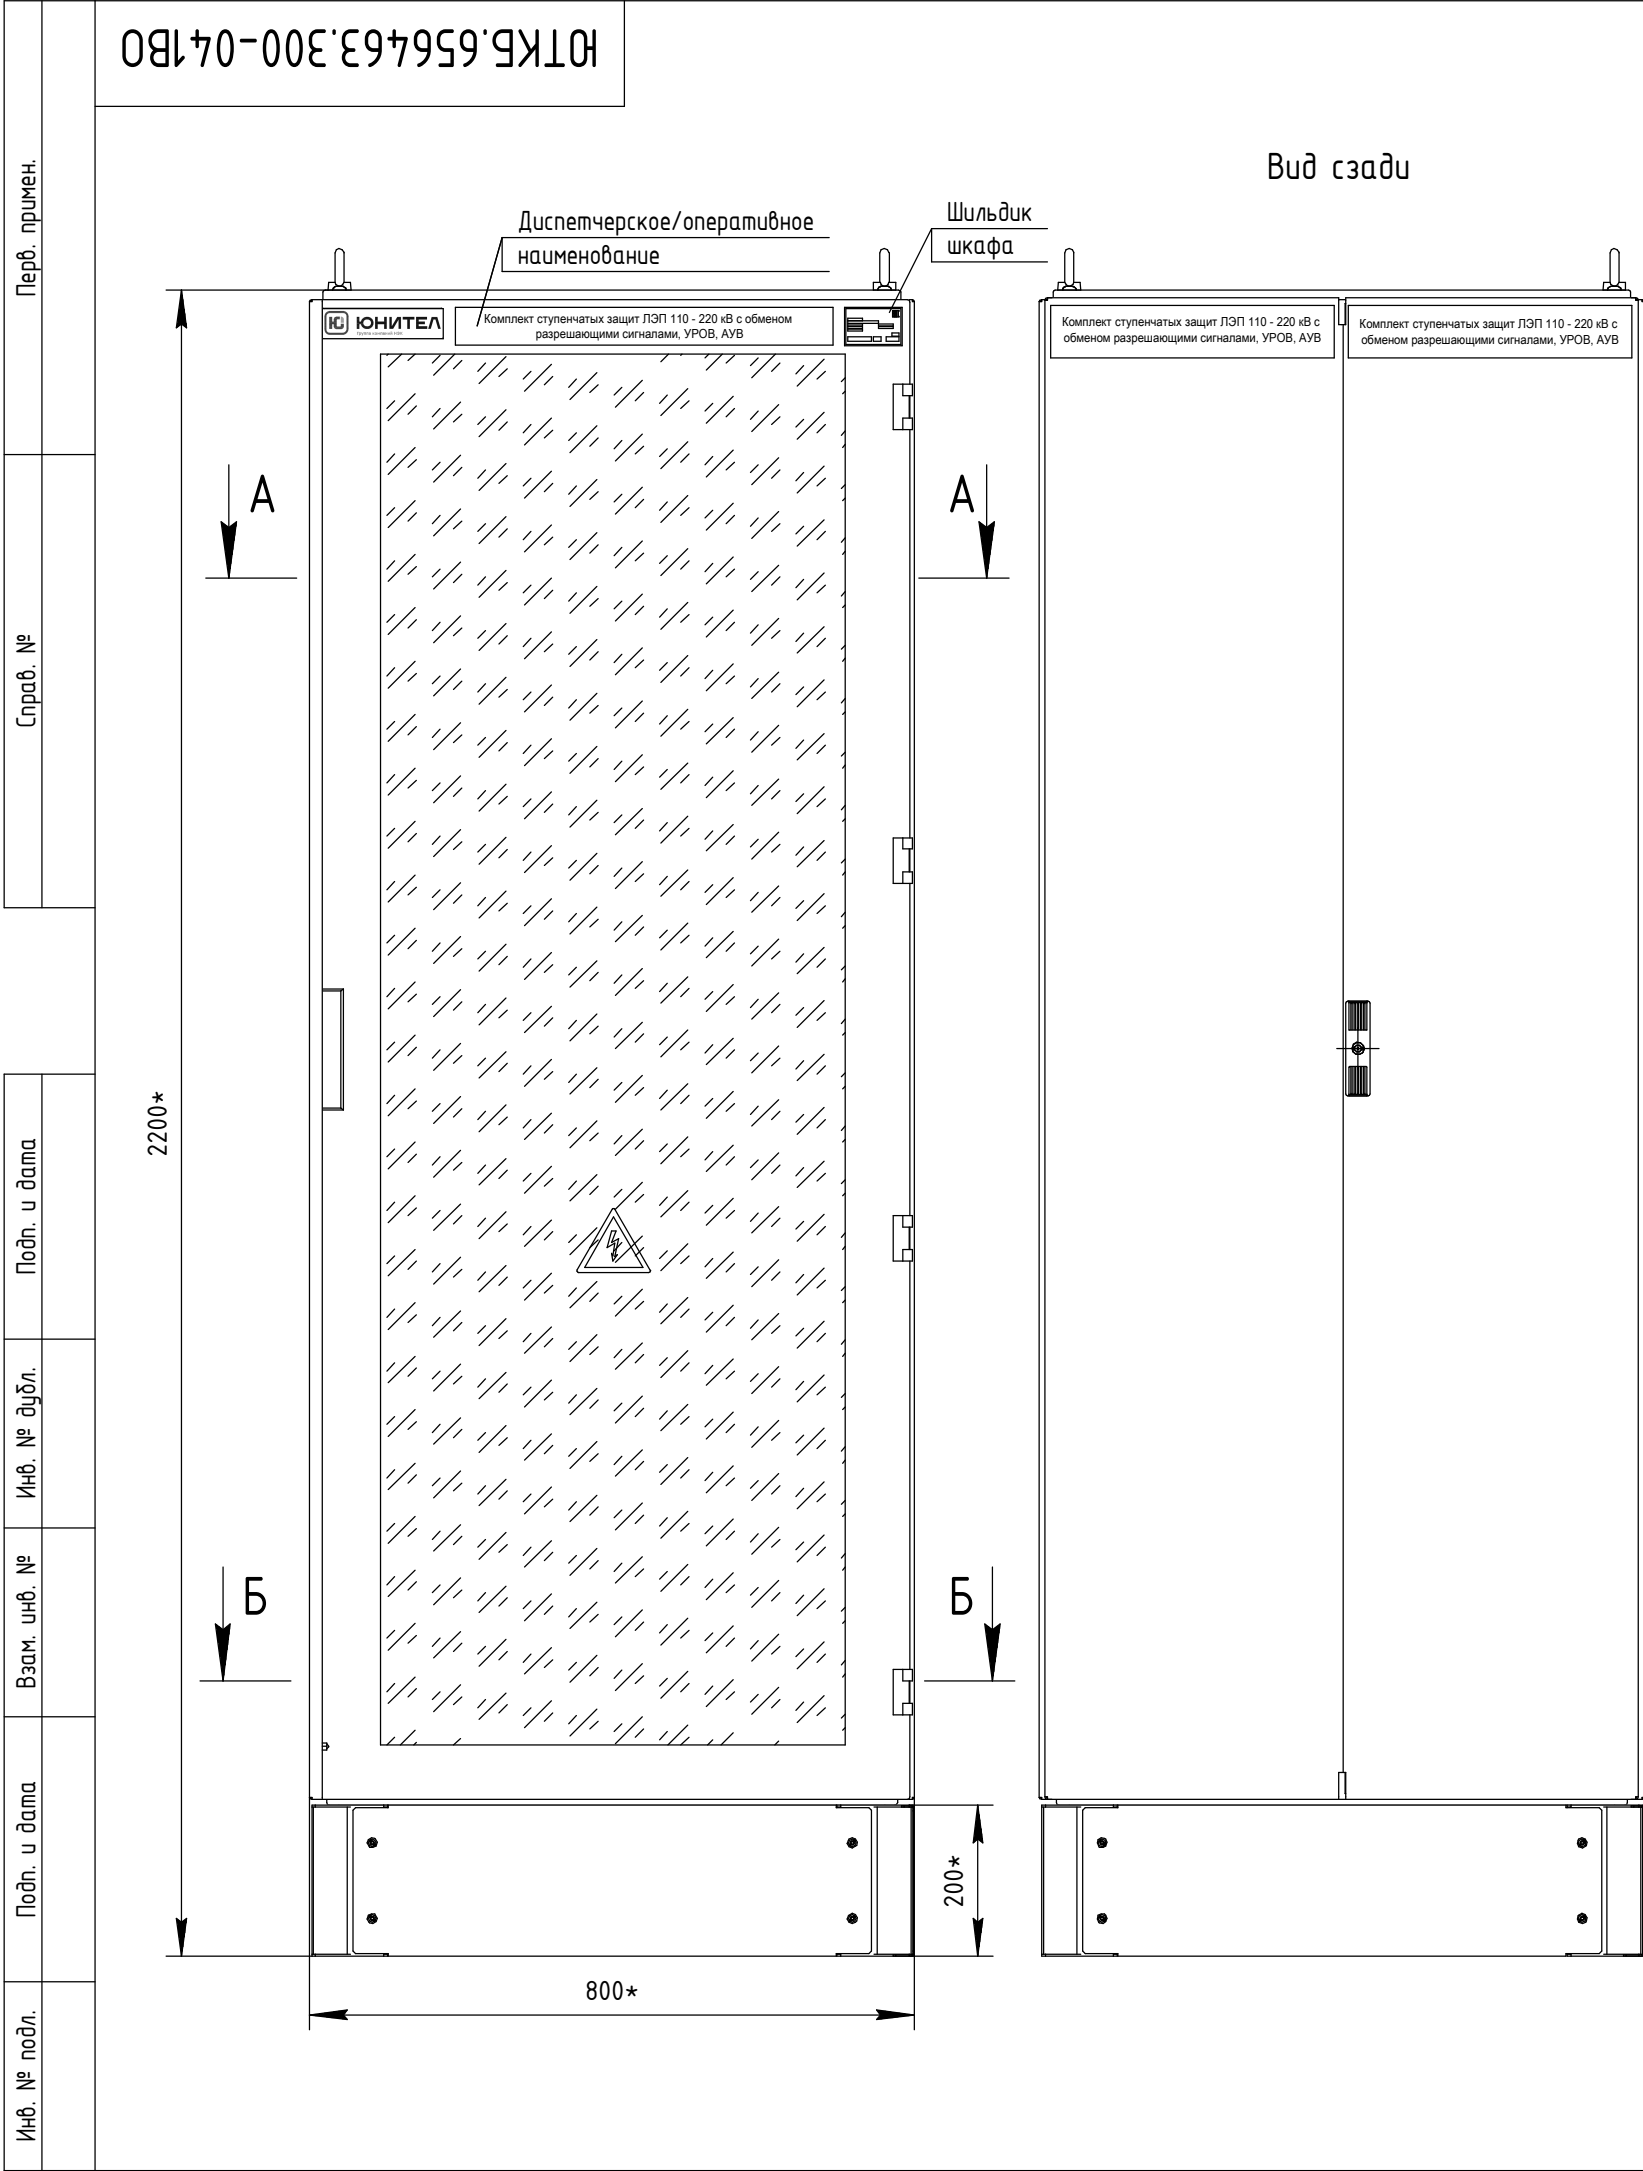


- 1 * Указаны типовые габариты шкафов. Фактические размеры металлоконструкции могут отличаться в пределах +10 мм. Размеры даны без учета выступающих частей (ручек, петель и т.д.).
- 2 ** Указана расчетная масса изделия. Фактическая масса изделия определяется взвешиванием.
- 3 Общие допуски ± IT14/2 по ГОСТ 30893.1-2002.
- 4 Степень защиты шкафа IP54.
- 5 Подвод внешних кабелей снизу.
- 6 Монтаж оборудования в шкафу выполнить по нормам фирмы-изготовителя.
- 7 Позиционные обозначения аппаратов соответствуют перечню элементов ЮТКБ.656463.300-041ПЭЗ.

					ЮТКБ.656463.300-041В0			
					Шкаф ступенчатых защит ЛЭП 110 - 220 кВ с обменом разрешающими сигналами, УРОВ, АУВ ШЭТ 221.04-1-ЮИРЗ Чертеж общего вида	Лист	Масса	Масштаб
Изм.	Лист	№ докум.	Подп.	Дата		0	180**	1:10
Разраб.	Юдина			18.08.2026				
Пров.	Черемисова			18.08.2026				
Т. контр.						Лист	1	Листов 2
Н. контр.								
Утв.	Ильин			18.08.2026				

Вид спереди
Дверь условно не показана

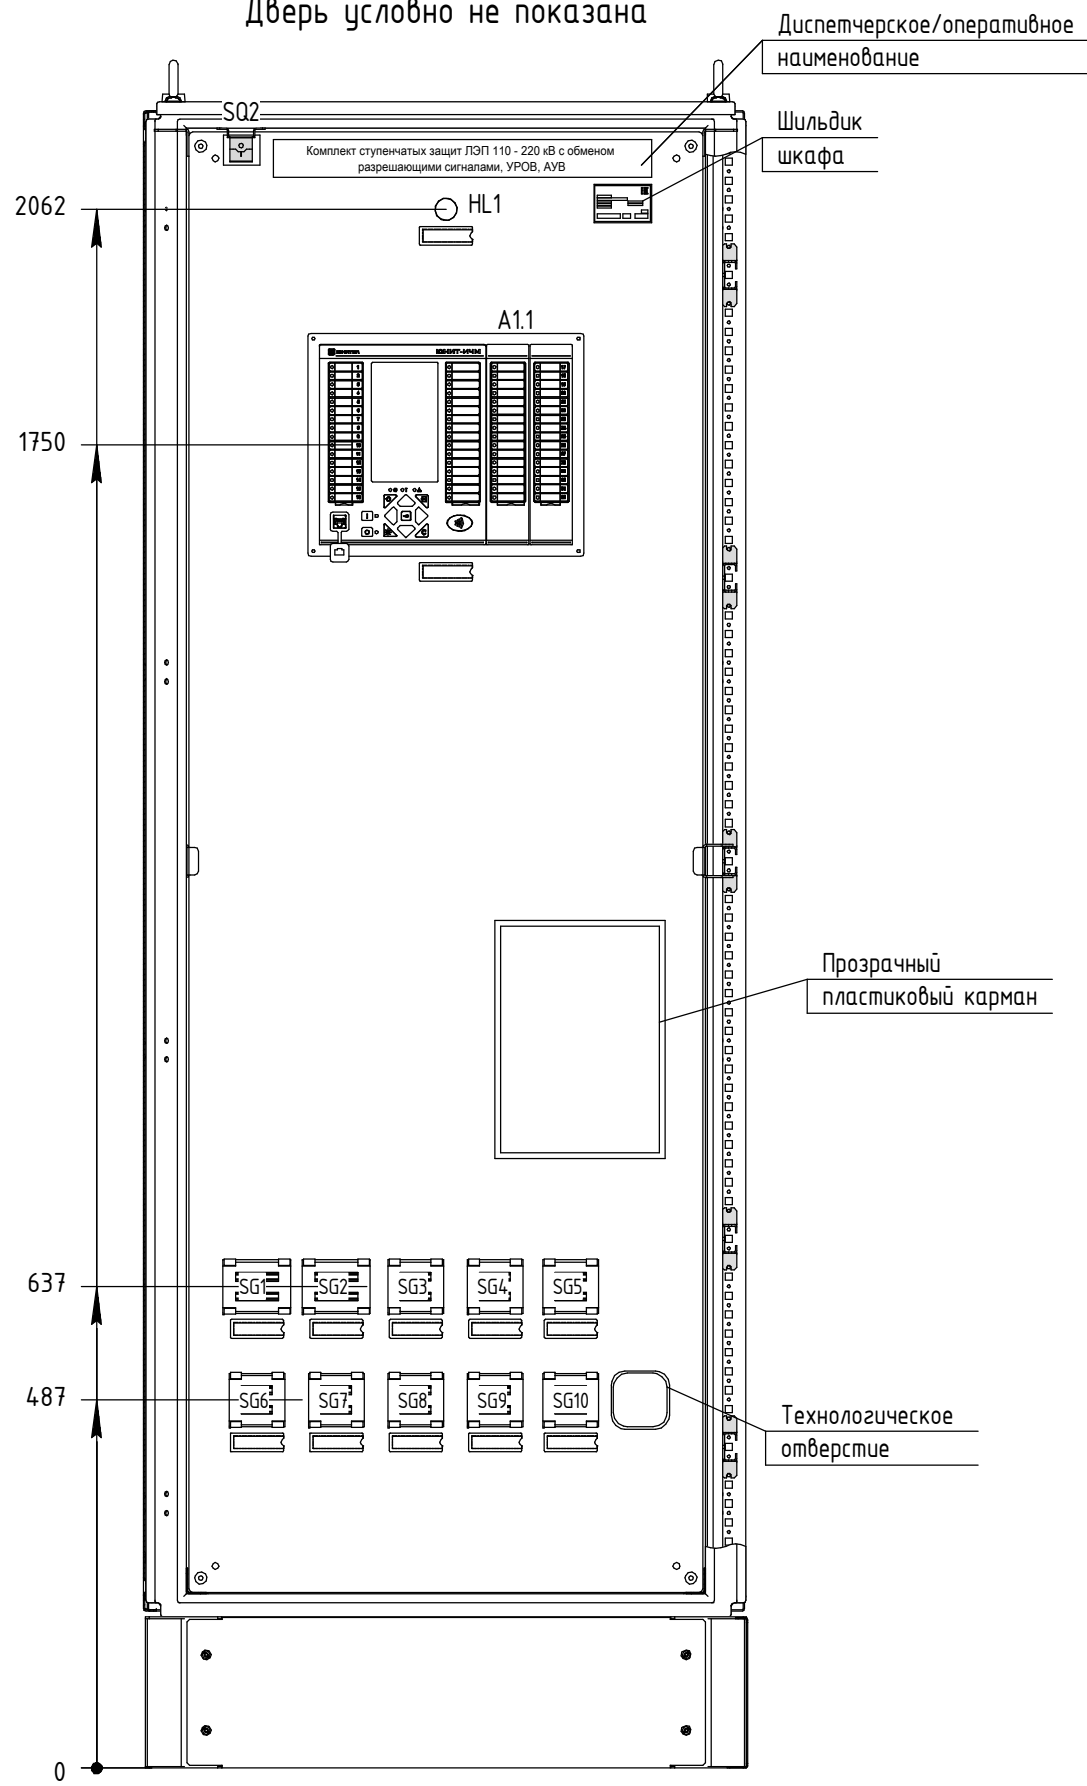


Г-Г

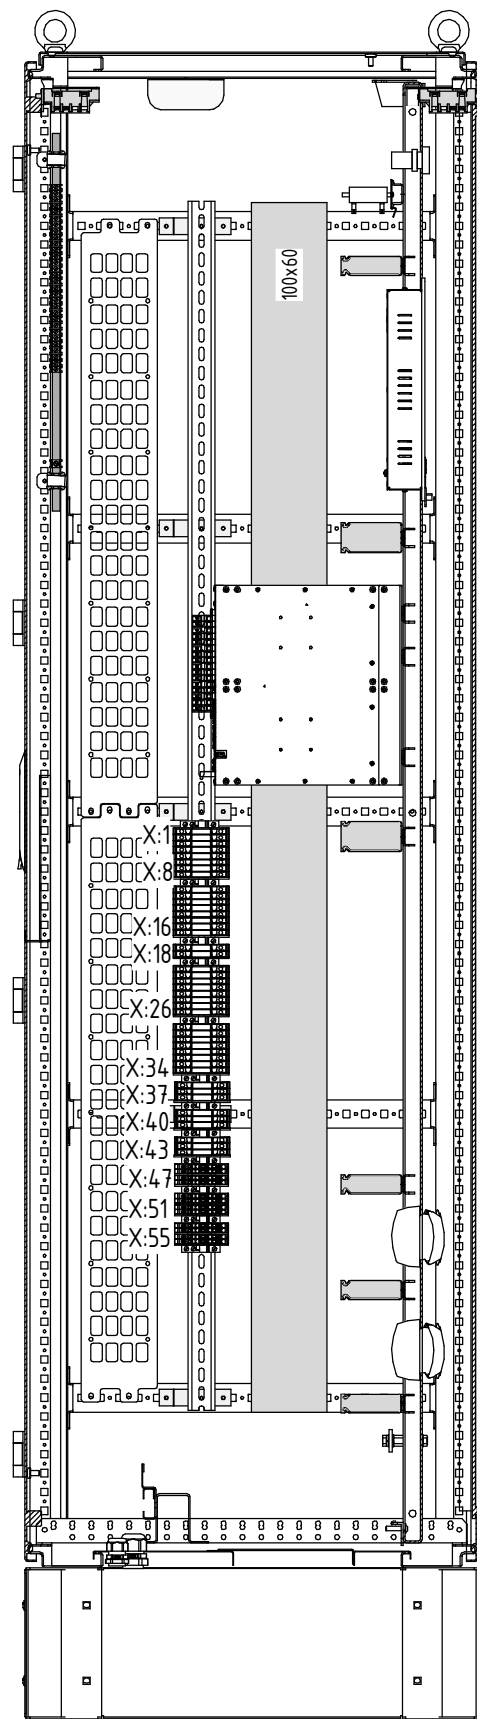


Вид сзади
Дверь, ряды зажимов и вертикальные короба
условно не показаны

В Г

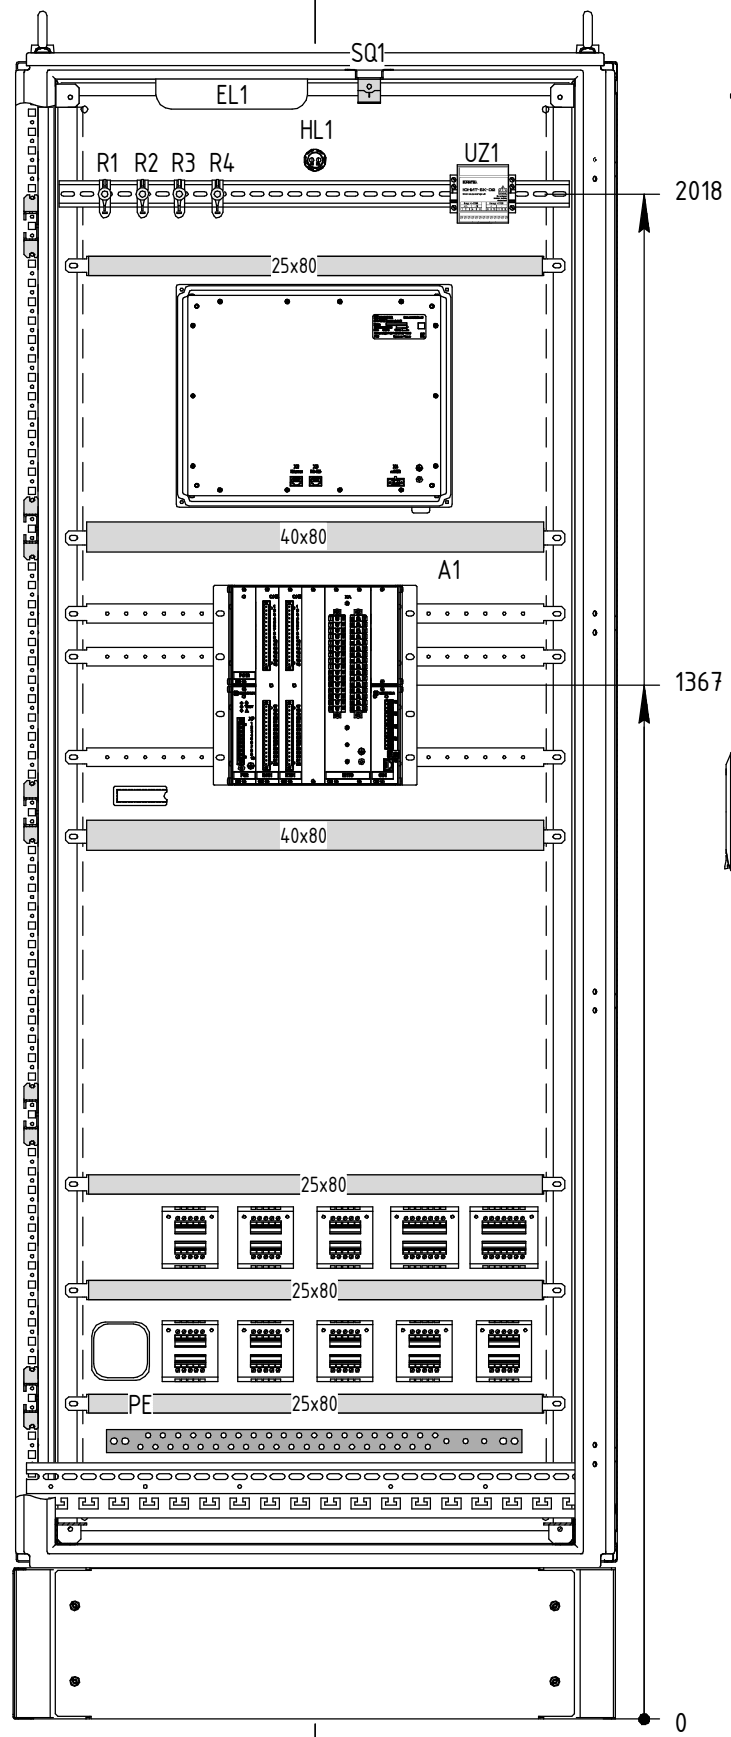

В-В

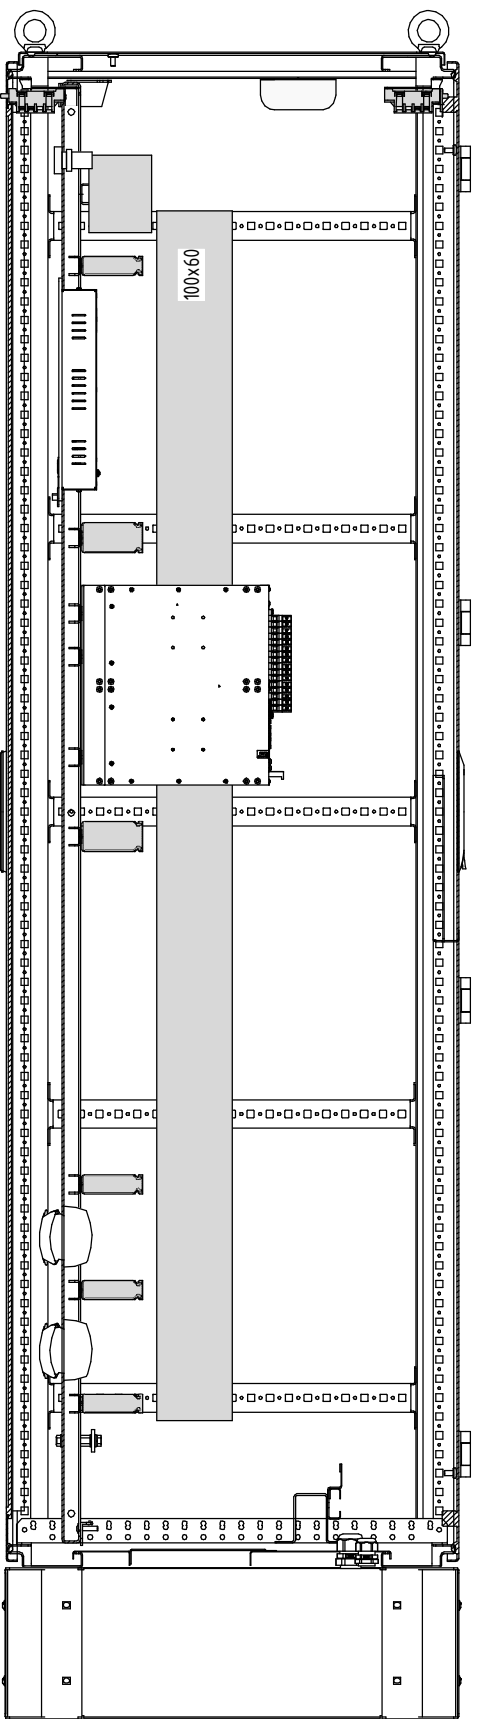

Инв. № подл.	Подп. и дата	Взам. инв. №	Инв. № дубл.	Подп. и дата

Изм.	Лист	№ докум.	Подп.	Дата