



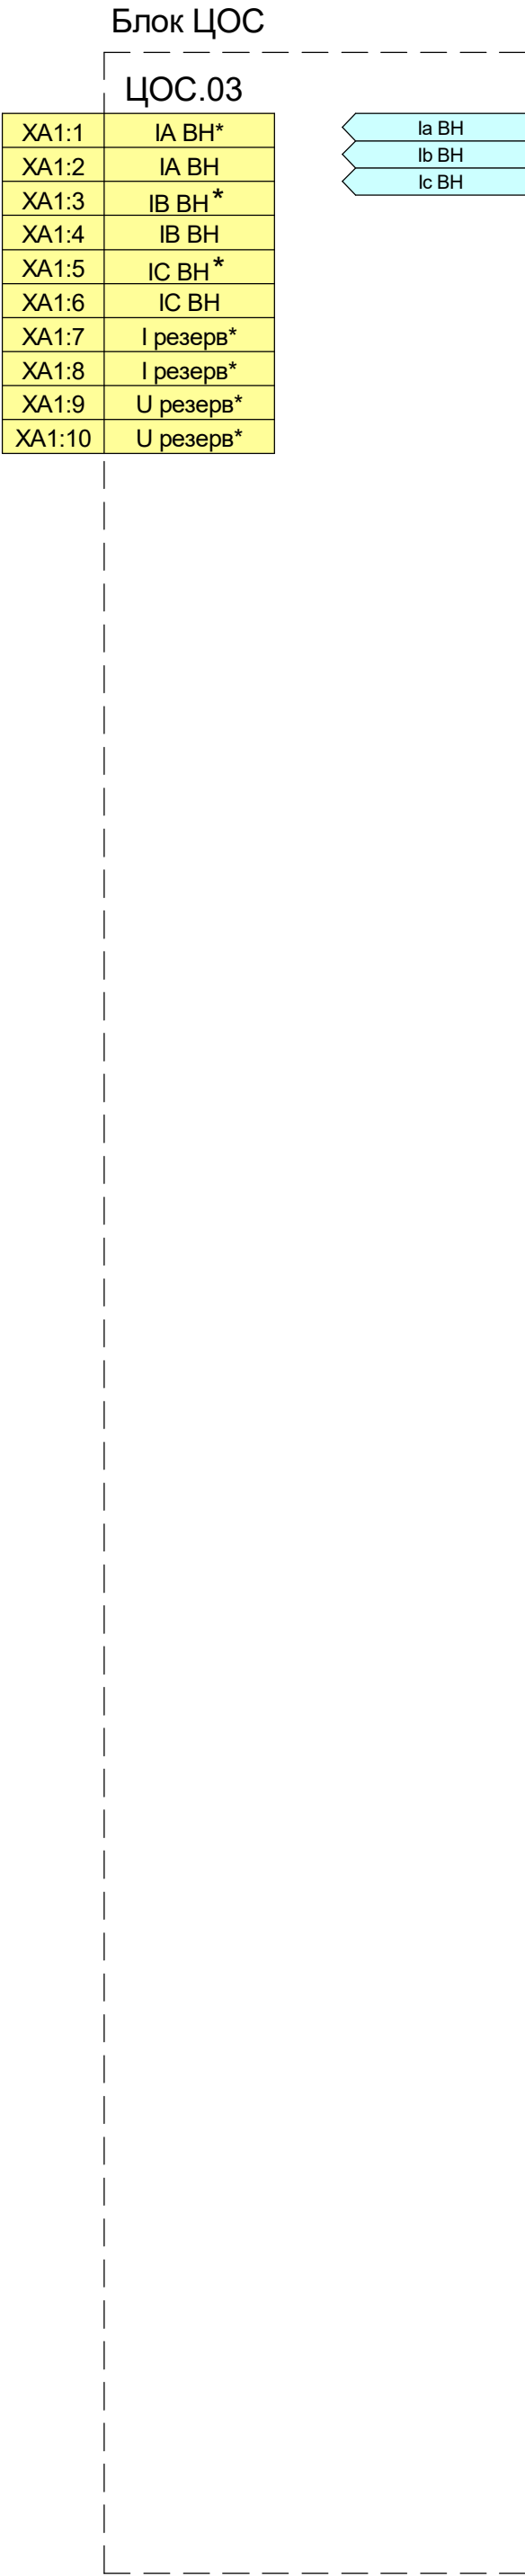


Входы ФСУ		
	Общая логика: Контр. ОТ терм	90.501
	Общая логика: БИ ток В	90.502
	Общая логика: SA Упр. В	90.503
	Общая логика: SA Упр. УПНКП	90.504
	Общая логика: SA Откл. УРОВ1	90.505
	Общая логика: SA Откл. УРОВ2	90.506
	Общая логика: SA Упр. КР	90.507
	Общая логика: SA Уск. ОАПВ	90.508
	Общая логика: SA Шунт. КОР	90.509
	Общая логика: Вых. цепи разобраны	90.510
	УРОВ В1(ЛВ) ВН/ УРОВ: Пуск УРОВ	3321.6821.501
	ФПВ/ ФПВ: Б/К В фА включен	501
	ФПВ/ ФПВ: Б/К В фВ включен	502
	ФПВ/ ФПВ: Б/К В фС включен	503
	ФПВ/ ФПВ: Б/К В фА отключен	504
	ФПВ/ ФПВ: Б/К В фВ отключен	505
	ФПВ/ ФПВ: Б/К В фС отключен	506
	ЗНФ: Пуск ЗНФ	3541.6701.501
	ЗНФ: Цикл ОАПВ	3541.6701.502
	ФПВ/ ФПВ: Б/К В вкл	3461.6551.501
	ФПВ/ ФПВ: Б/К В вкл ф.А	3461.6551.502
	ФПВ/ ФПВ: Б/К В вкл ф.В	3461.6551.503
	ФПВ/ ФПВ: Б/К В вкл ф.С	3461.6551.504
	ФПВ/ ФПВ: Б/К В откл ф.А	3461.6551.505
	ФПВ/ ФПВ: Б/К В откл ф.В	3461.6551.506
	ФПВ/ ФПВ: Б/К В откл ф.С	3461.6551.507
	ФПВ/ ФПВ: Б/К В откл	3461.6551.508
	ФПВ/ ФПВ: Ремонт	507
	ФПВ/ Р1: Б/К Р вкл	3461.6531.501
	ФПВ/ Р1: Б/К Р вкл ф.А	3461.6531.502
	ФПВ/ Р1: Б/К Р вкл ф.В	3461.6531.503
	ФПВ/ Р1: Б/К Р вкл ф.С	3461.6531.504
	ФПВ/ Р1: Б/К Р откл	3461.6531.505
	ФПВ/ Р1: Б/К Р откл ф.А	3461.6531.506
	ФПВ/ Р1: Б/К Р откл ф.В	3461.6531.507
	ФПВ/ Р1: Б/К Р откл ф.С	3461.6531.508
	ФПВ/ Р2: Б/К Р вкл	3461.6532.501
	ФПВ/ Р2: Б/К Р вкл ф.А	3461.6532.502
	ФПВ/ Р2: Б/К Р вкл ф.В	3461.6532.503
	ФПВ/ Р2: Б/К Р вкл ф.С	3461.6532.504
	ФПВ/ Р2: Б/К Р откл	3461.6532.505
	ФПВ/ Р2: Б/К Р откл ф.А	3461.6532.506
	ФПВ/ Р2: Б/К Р откл ф.В	3461.6532.507
	ФПВ/ Р2: Б/К Р откл ф.С	3461.6532.508
	Контр. ЭМО1	508
	Контр. ЭМО1 ф.А	522
	Контр. ЭМО1 ф.В	525
	Контр. ЭМО1 ф.С	528
	Контр. ЭМВ	513
	Контр. ЭМВ ф.А	524
	Контр. ЭМВ ф.В	527
	Контр. ЭМВ ф.С	528
	Контр. ЭМО2	509
	Контр. ЭМО2 ф.А	523
	Контр. ЭМО2 ф.В	526
	Контр. ЭМО2 ф.С	529
	КСВ/ Контроль В: Неиспр. обогр.	3071.6861.513
	КСВ/ Контроль В: Автомат ШП	3071.6861.514

Входы ФСУ		
	КСВ/ Контроль В: Низк. давл. SF6	3071.6861.515
	КСВ/ Контроль В: Низк. давл. SF6 ф.А	3071.6861.516
	КСВ/ Контроль В: Низк. давл. SF6 ф.В	3071.6861.517
	КСВ/ Контроль В: Низк. давл. SF6 ф.С	3071.6861.518
	КСВ/ Контроль В: Авар. давл. SF6	3071.6861.519
	КСВ/ Контроль В: Авар. давл. SF6 ф.А	3071.6861.520
	КСВ/ Контроль В: Авар. давл. SF6 ф.В	3071.6861.521
	КСВ/ Контроль В: Авар. давл. SF6 ф.С	3071.6861.522
	КСВ/ Контроль В: Пруж. не заведены	3071.6861.523
	КСВ/ Контроль В: Пруж. не заведены ф.А	3071.6861.524
	КСВ/ Контроль В: Пруж. не заведены ф.В	3071.6861.525
	КСВ/ Контроль В: Пруж. не заведены ф.С	3071.6861.526
	КСВ/ Контроль В: Контр. ОТ ЭМВ/ЭМО1	3071.6861.527
	КСВ/ Контроль В: Контр. ОТ ЭМО2	3071.6861.528
	КСВ/ Контроль ТТ Низк. давл. SF6 ТТ	3071.6581.501
	КСВ/ Контроль ТТ Низк. давл. SF6 ТТ ф.А	3071.6581.502
	КСВ/ Контроль ТТ Низк. давл. SF6 ТТ ф.В	3071.6581.503
	КСВ/ Контроль ТТ Низк. давл. SF6 ТТ ф.С	3071.6581.504
	КСВ/ Контроль ТТ Авар. давл. SF6 ТТ	3071.6581.505
	КСВ/ Контроль ТТ Авар. давл. SF6 ТТ ф.А	3071.6581.506
	КСВ/ Контроль ТТ Авар. давл. SF6 ТТ ф.В	3071.6581.507
	КСВ/ Контроль ТТ Авар. давл. SF6 ТТ ф.С	3071.6581.508
	КСВ/ Контроль ТТ Неиспр. обогр. ТТ	3071.6581.509
	Работа ЭМВ	510
	Работа ЭМВ ф.А	516
	Работа ЭМВ ф.В	519
	Работа ЭМВ ф.С	522
	Работа ЭМО1	511
	Работа ЭМО1 ф.А	514
	Работа ЭМО1 ф.В	517
	Работа ЭМО1 ф.С	520
	Работа ЭМО2	512
	Работа ЭМО2 ф.А	515
	Работа ЭМО2 ф.В	518
	Работа ЭМО2 ф.С	521
	БКУ/ БКУ : Ком. опер. вкл.	3431.6661.501
	БКУ/ БКУ : Ком. опер. откл.	3431.6661.502
	БКУ/ БКУ : Ком. вкл. СКРМ	3432.6661.501
	БКУ/ БКУ Ав.СКРМ: Ком. откл.	3432.6661.502
	ФПВ/ ФПВ: Ремонт	507
	КСВ/ Блокировка управления: Пруж. не заведены	3071.6901.502
	КСВ/ Блокировка управления: Внеш. блок. вкл.	3071.6901.503
	КСВ/ Блокировка управления: Авар. давл. SF6	3071.6901.504
	КСВ/ Блокировка управления: Внеш. блок. упр.	3071.6901.505
	КСВ/ Блокировка управления: Пруж. не заведены ф.А	3071.6901.506
	КСВ/ Блокировка управления: Внеш. блок. вкл. ф.А	3071.6901.507
	КСВ/ Блокировка управления: Авар. давл. SF6 ф.А	3071.6901.508
	КСВ/ Блокировка управления: Внеш. блок. упр. ф.А	3071.6901.509
	КСВ/ Блокировка управления: Пруж. не заведены ф.В	3071.6901.510
	КСВ/ Блокировка управления: Внеш. блок. вкл. ф.В	3071.6901.511
	КСВ/ Блокировка управления: Авар. давл. SF6 ф.В	3071.6901.512
	КСВ/ Блокировка управления: Внеш. блок. упр. ф.В	3071.6901.513
	КСВ/ Блокировка управления: Пруж. не заведены ф.С	3071.6901.514
	КСВ/ Блокировка управления: Внеш. блок. вкл. ф.С	3071.6901.515
	КСВ/ Блокировка управления: Авар. давл. SF6 ф.С	3071.6901.516
	КСВ/ Блокировка управления: Внеш. блок. упр. ф.С	3071.6901.517
	ЗН БСК:	3071.501
	В. отключены	3071.502
	КСВ: Ср. РЗ ШР(БСК)	


Входы ФСУ		
	КСВ: Ср. РЗ КР	3071.503
	КСВ: Сброс	3071.504
	КСВ: Разр. вкл. САУ	3071.505
	УВ УПНКП/ УВ УПНКП: Вкл. АПВ	3081.6911.501
	УВ УПНКП/ УВ УПНКП: УВ УПНКП	3081.6911.502
	УВ/ УВ: Ср. РЗ ШР(БСК)	3091.6921.501
	УВ/ УВ: Ср. РЗ КР	3091.6921.502
	УВ/ УВ: Ср. РЗ ЛЭП	3091.6921.503
	Работа ЭМО1	511
	Контр. ЭМО1	508
	Работа ЭМО2	512
	Контр. ЭМО2	509
	УВ/ УВ: Вкл. АПВ	3091.6921.504
	Работа ЭМВ	510
	Контр. ЭМВ	513
	Работа ЭМО1 ф.А	514
	Контр. ЭМО1 ф.А	522
	Работа ЭМО2 ф.А	515
	Контр. ЭМО2 ф.А	523
	Работа ЭМВ ф.А	516
	Контр. ЭМВ ф.А	524
	Работа ЭМО1 ф.В	517
	Контр. ЭМО1 ф.В	525
	Работа ЭМО2 ф.В	518
	Контр. ЭМО2 ф.В	526
	Работа ЭМВ ф.В	519
	Контр. ЭМВ ф.В	527
	Работа ЭМО1 ф.С	520
	Контр. ЭМО1 ф.С	528
	Работа ЭМО2 ф.С	521
	Контр. ЭМО2 ф.С	529
	Работа ЭМВ ф.С	522
	Контр. ЭМВ ф.С	528
	УВ/ УВ: УВ УПНКП	3091.6921.505

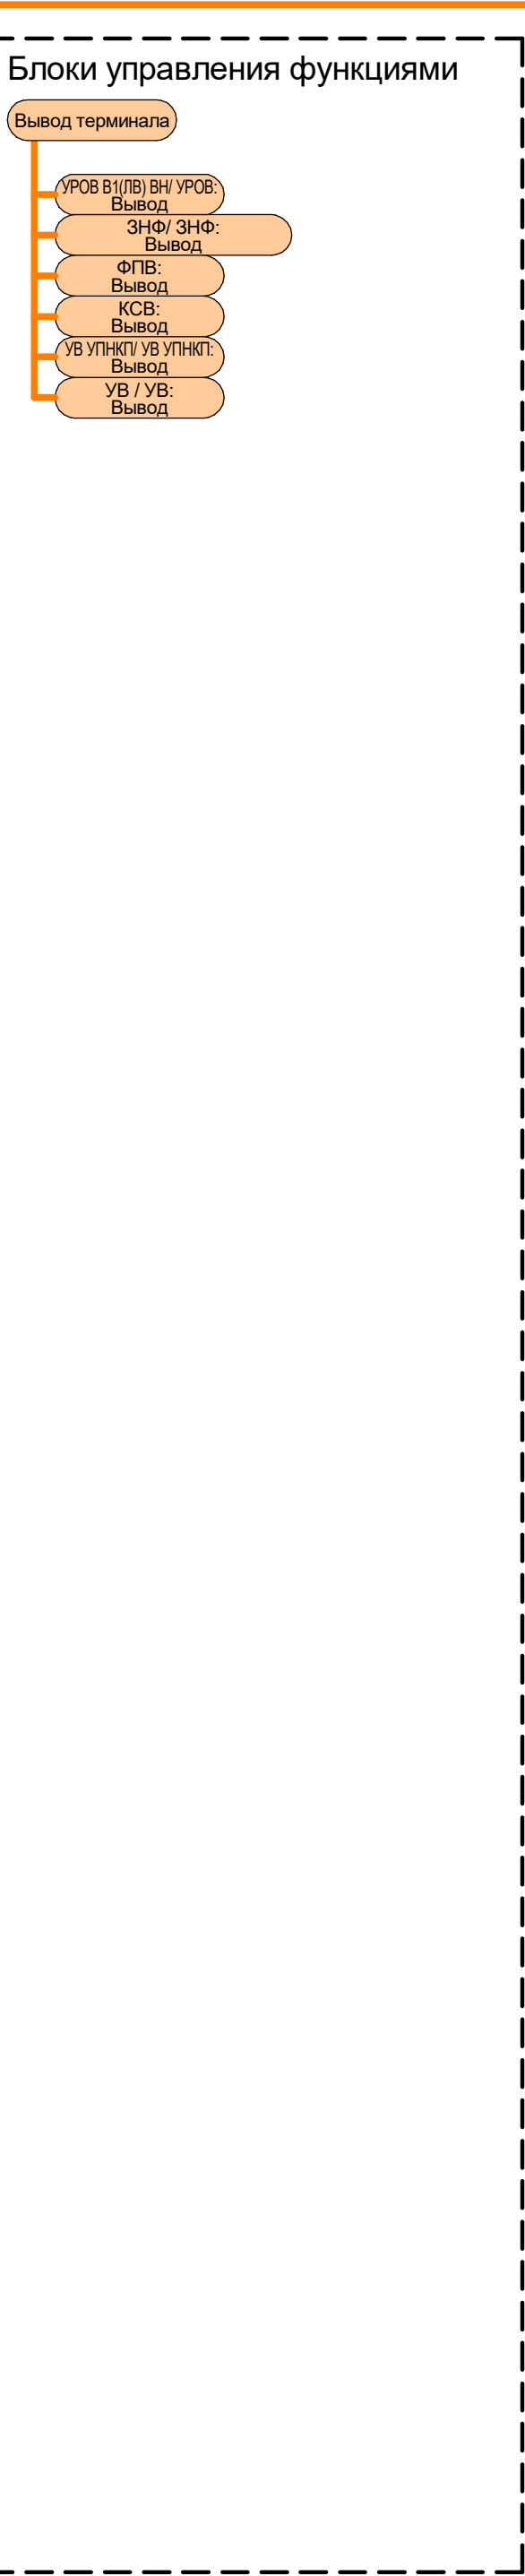

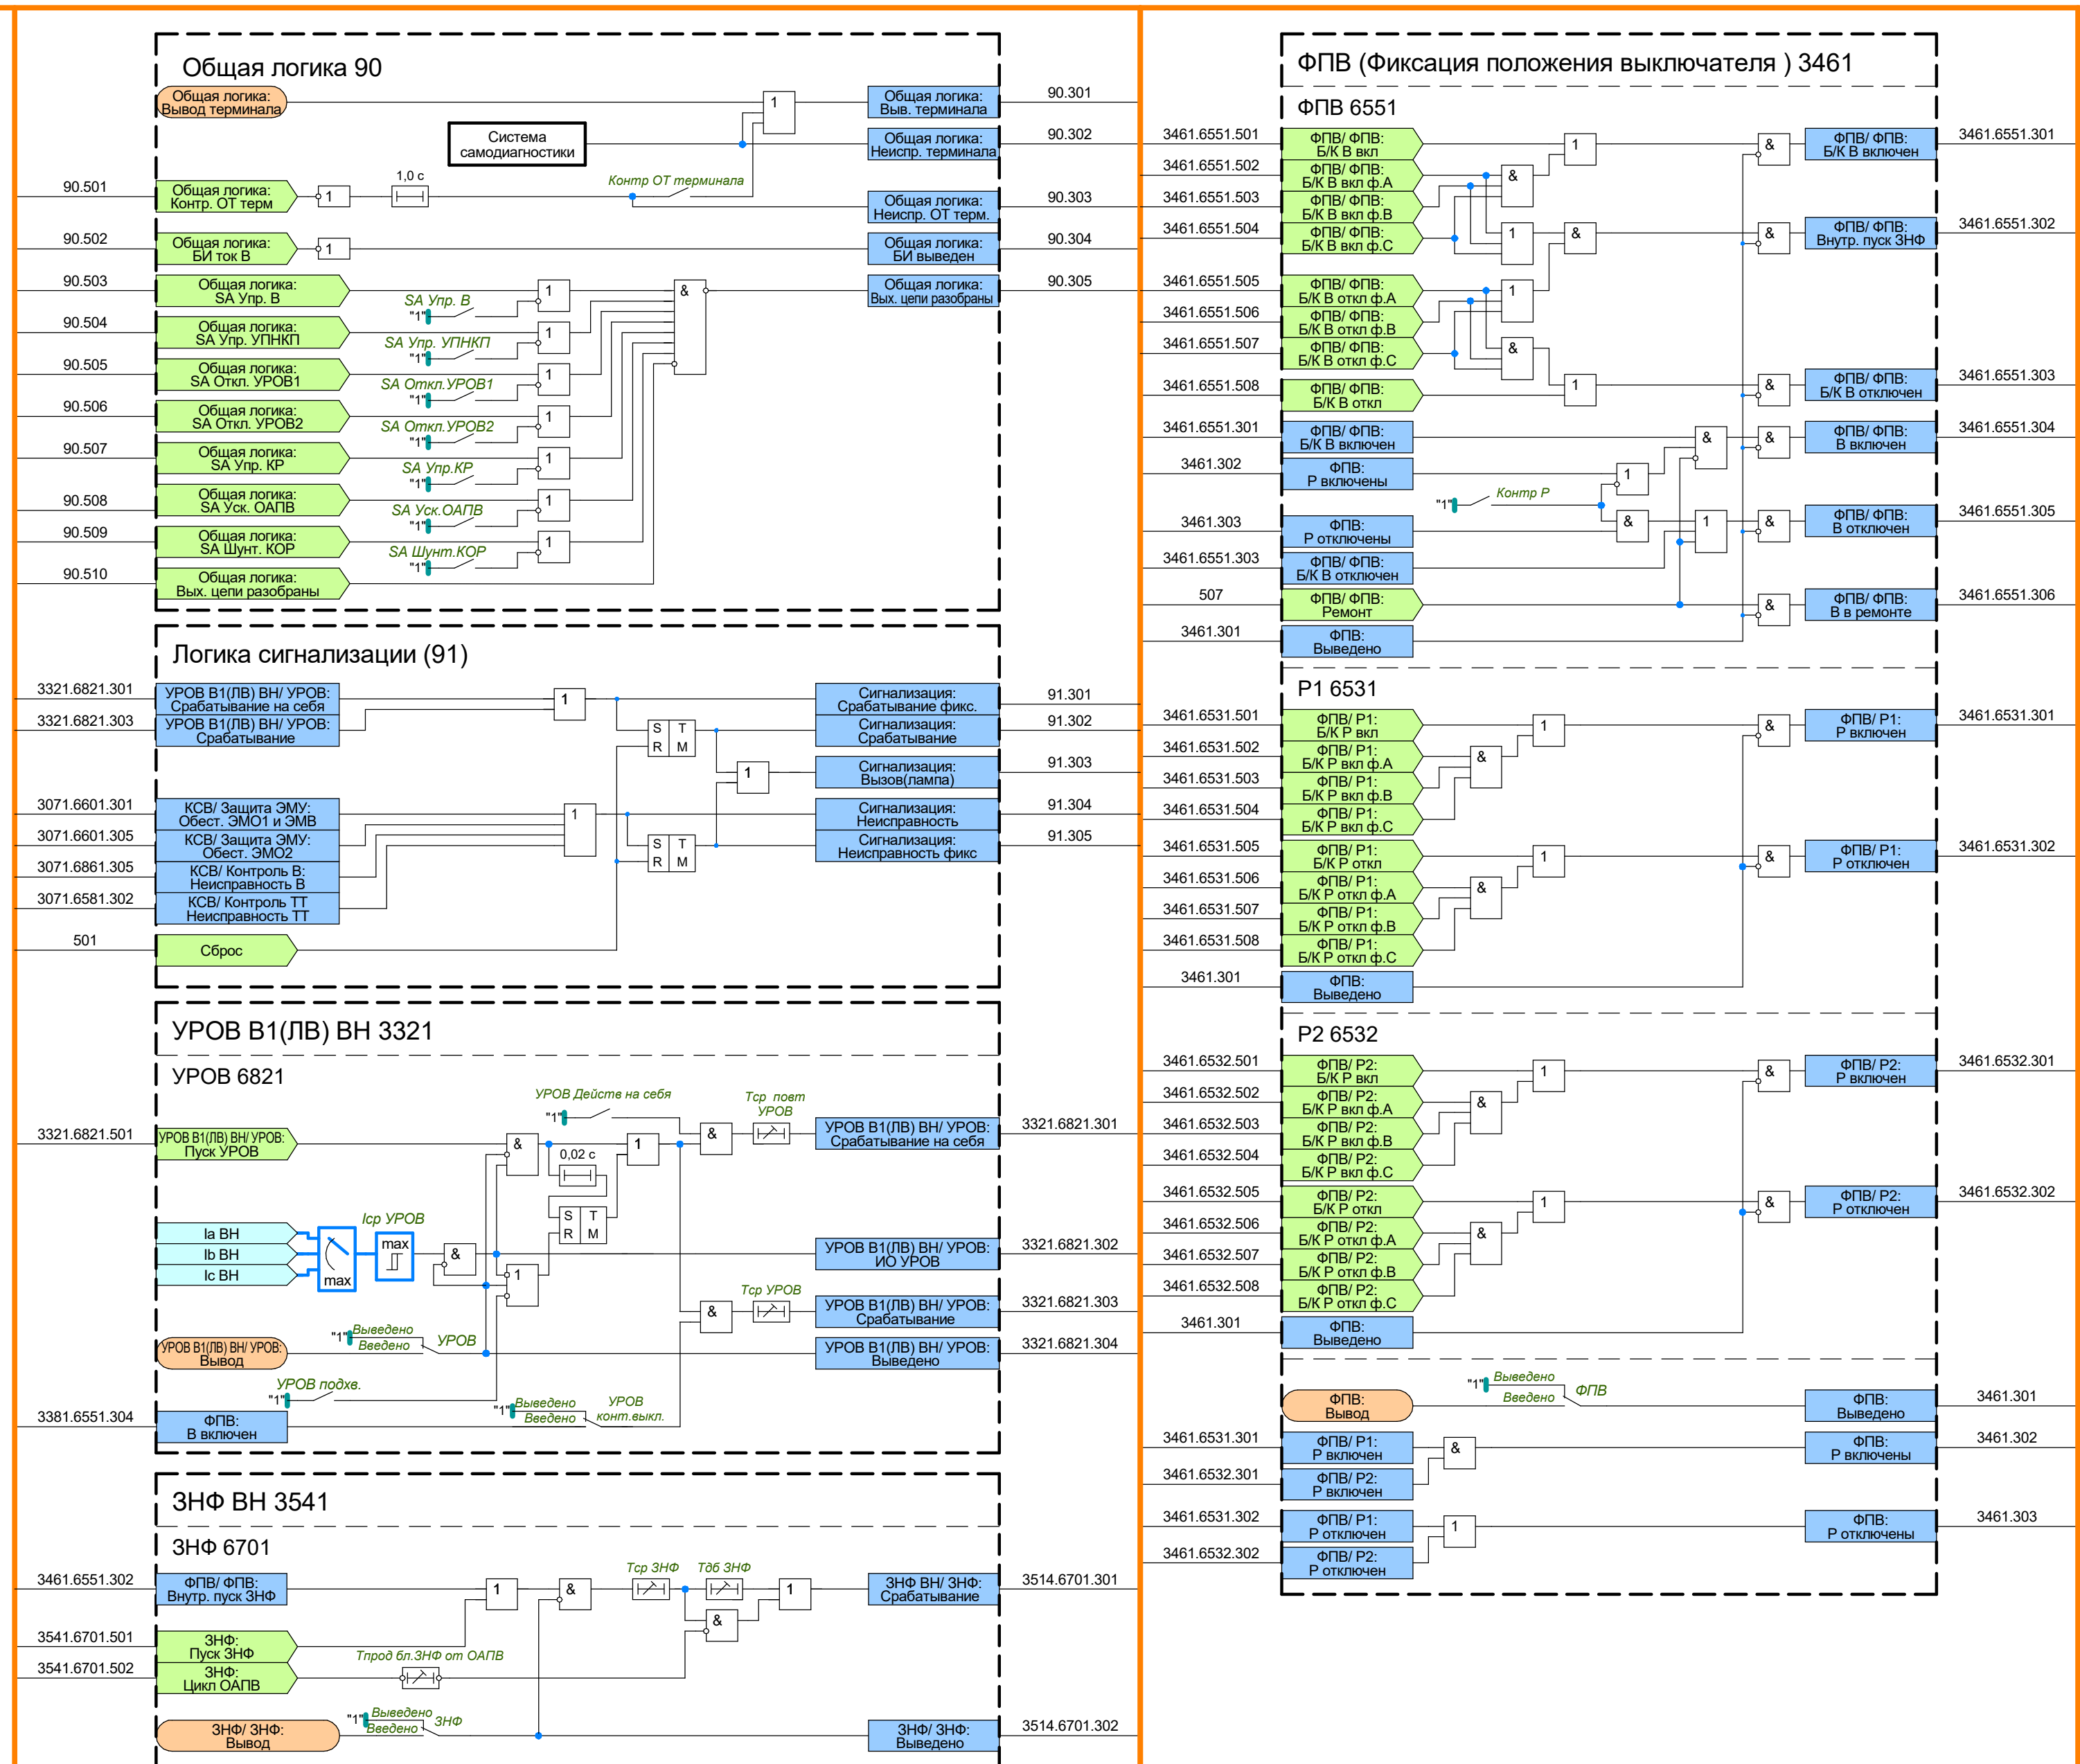


КСВ (Контроль силового выключателя) 3071

Контроль В 6861

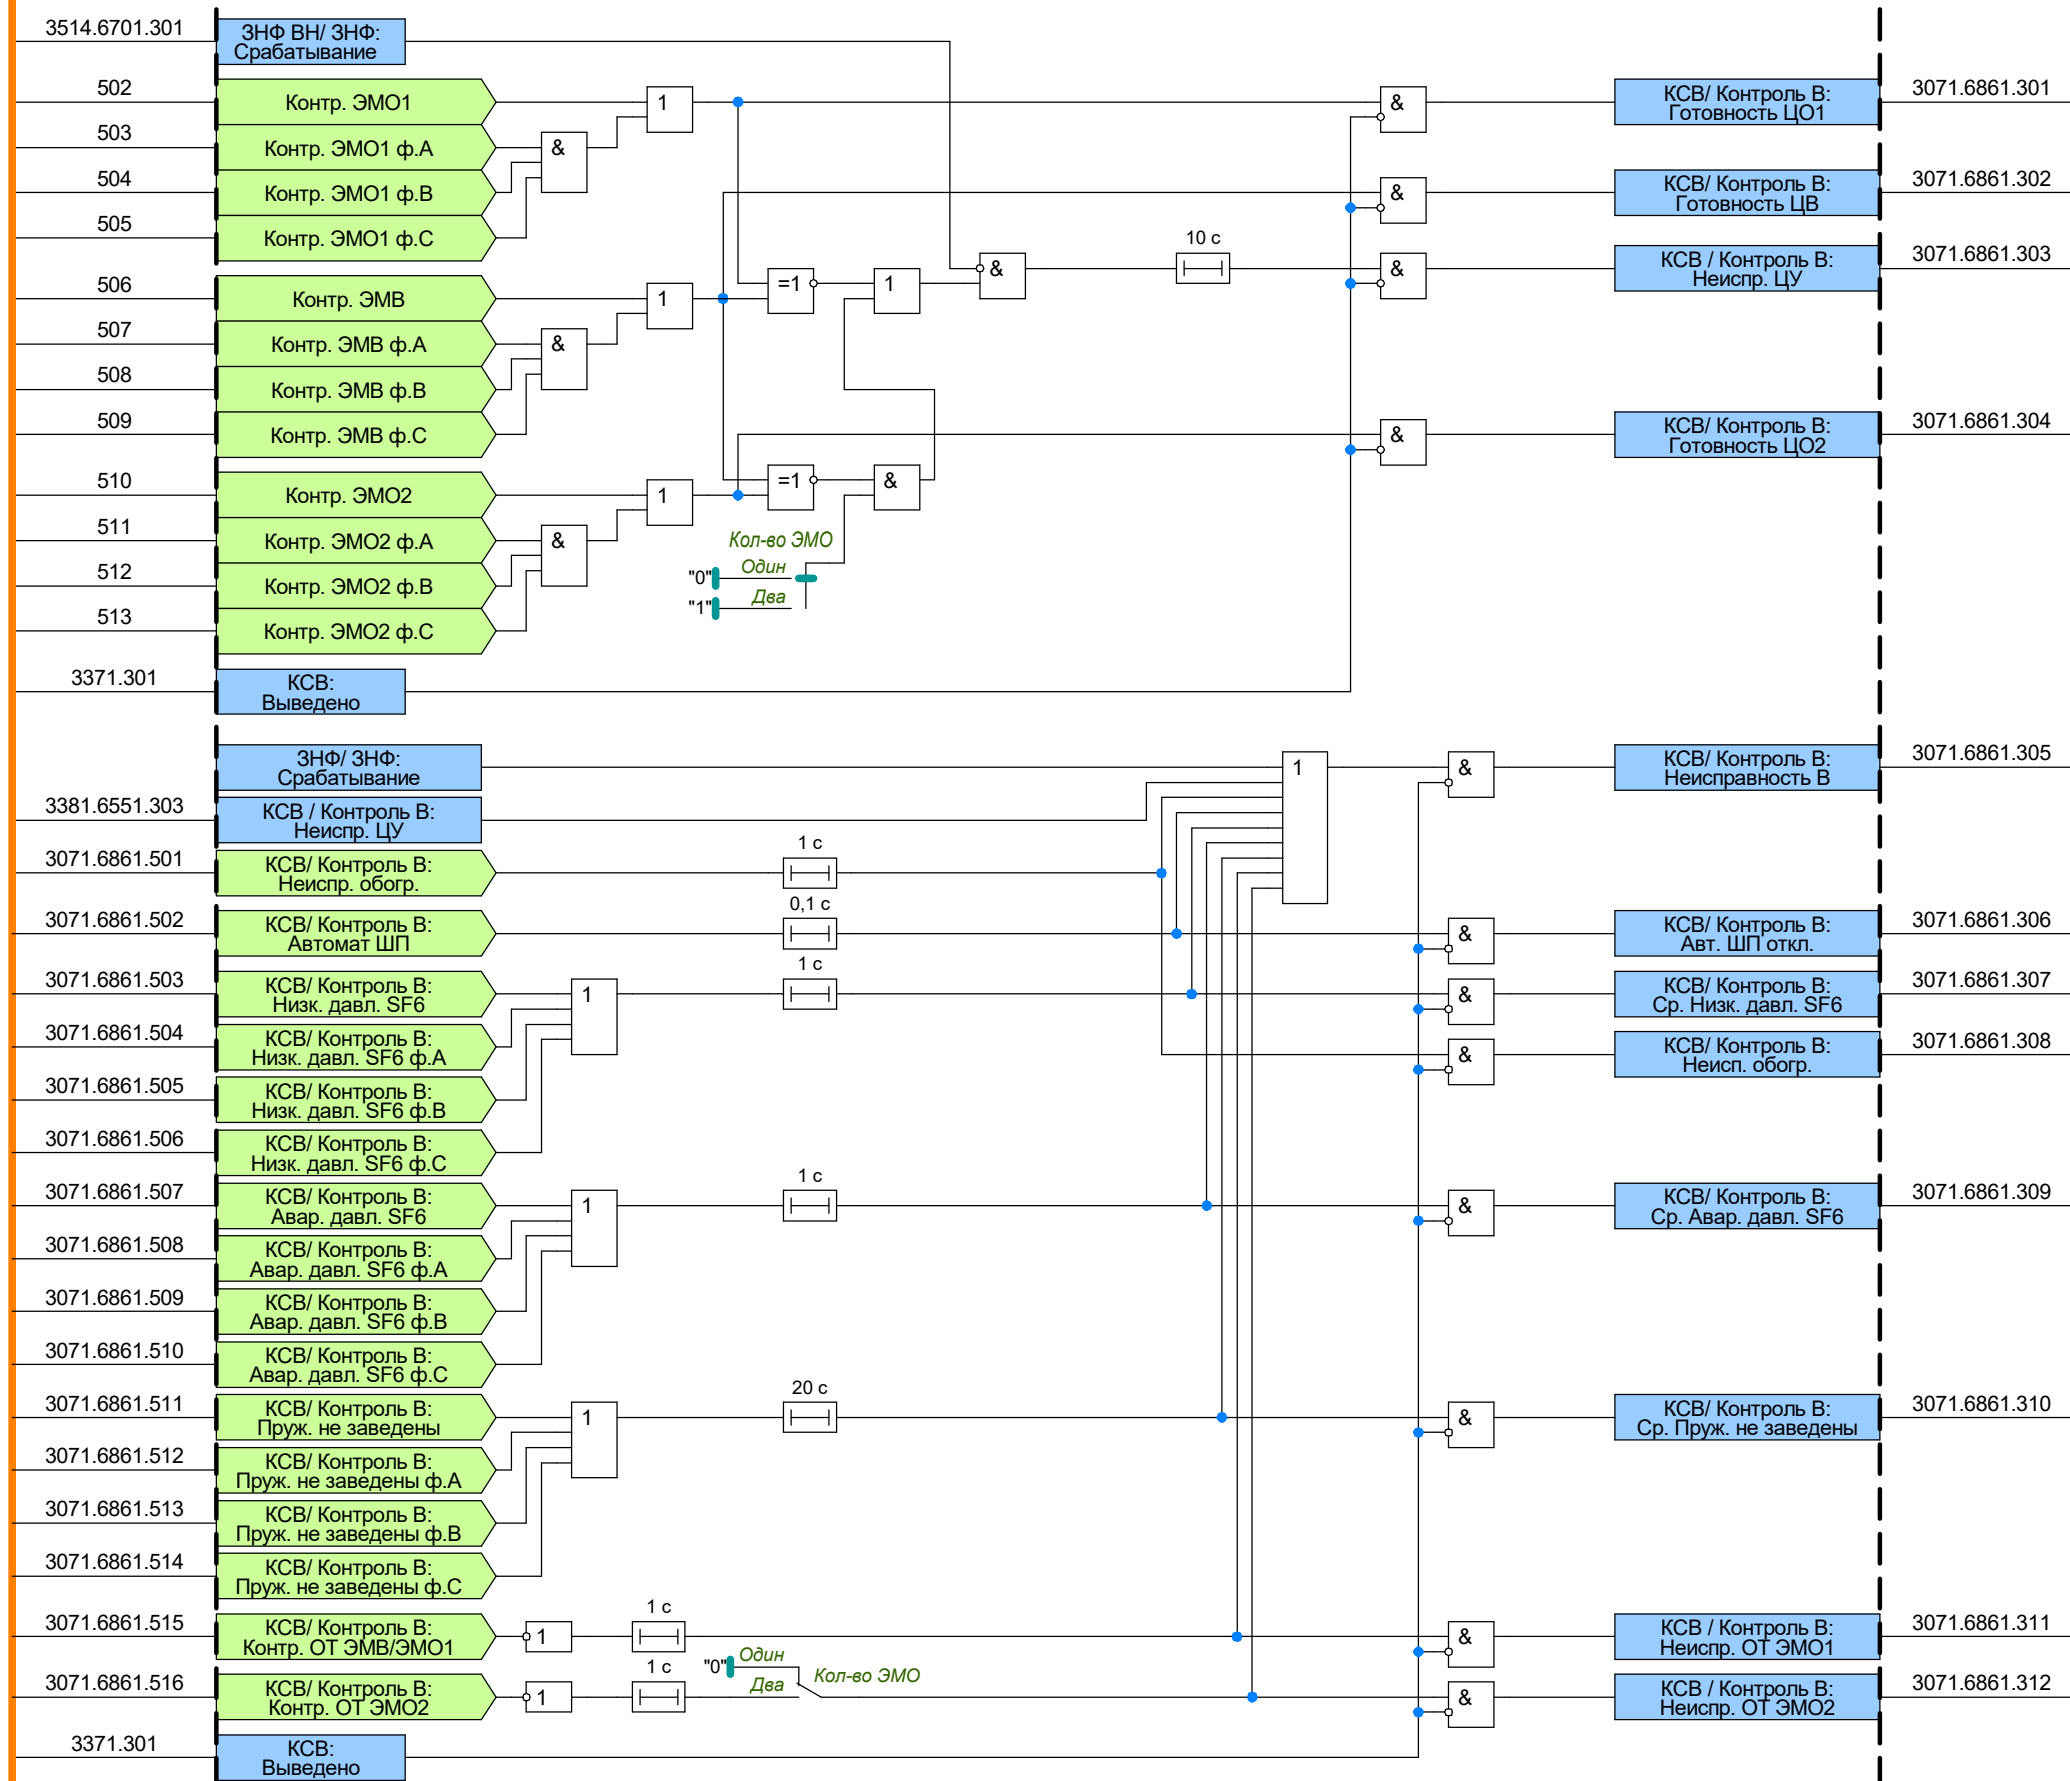


КСВ (Контроль силового выключателя) 3071


Контроль ТТ 6581

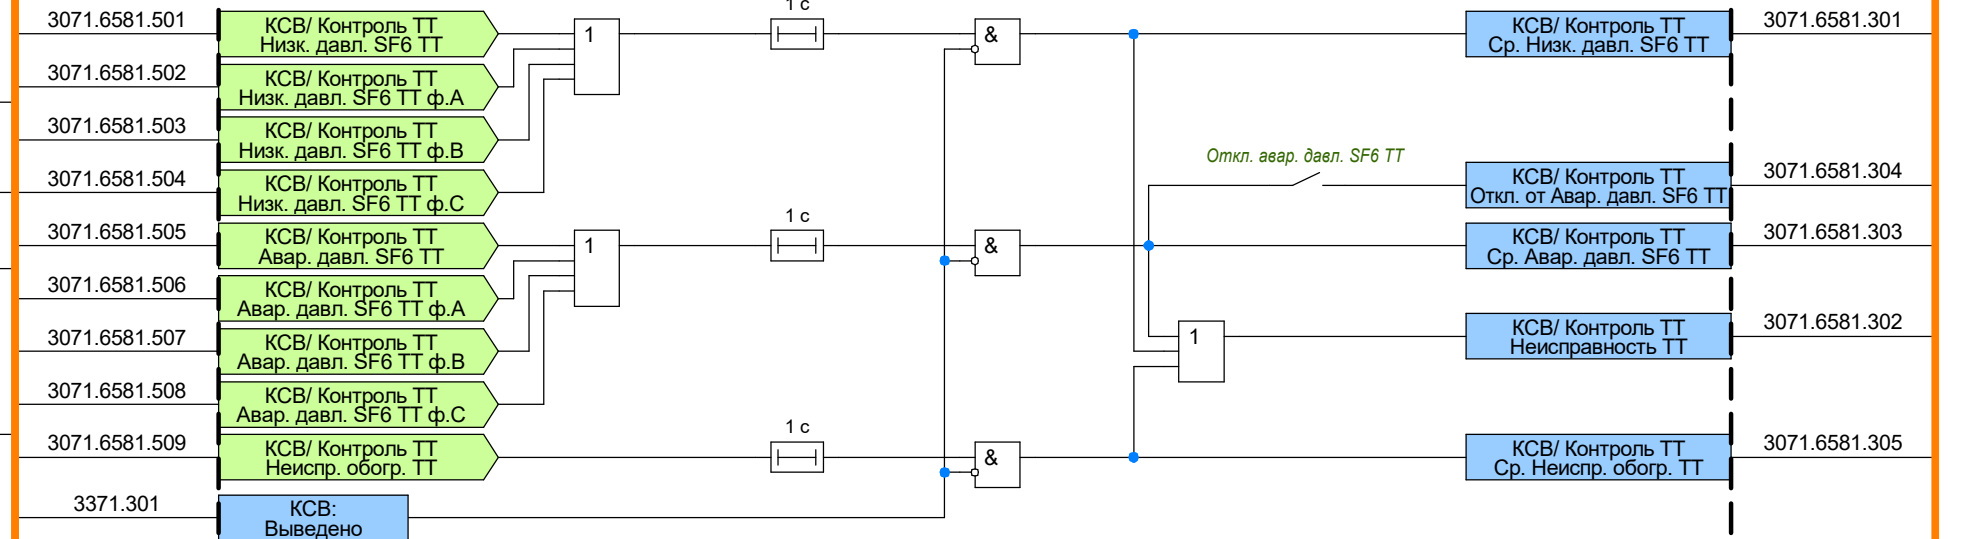

Защита ЭМУ 6601

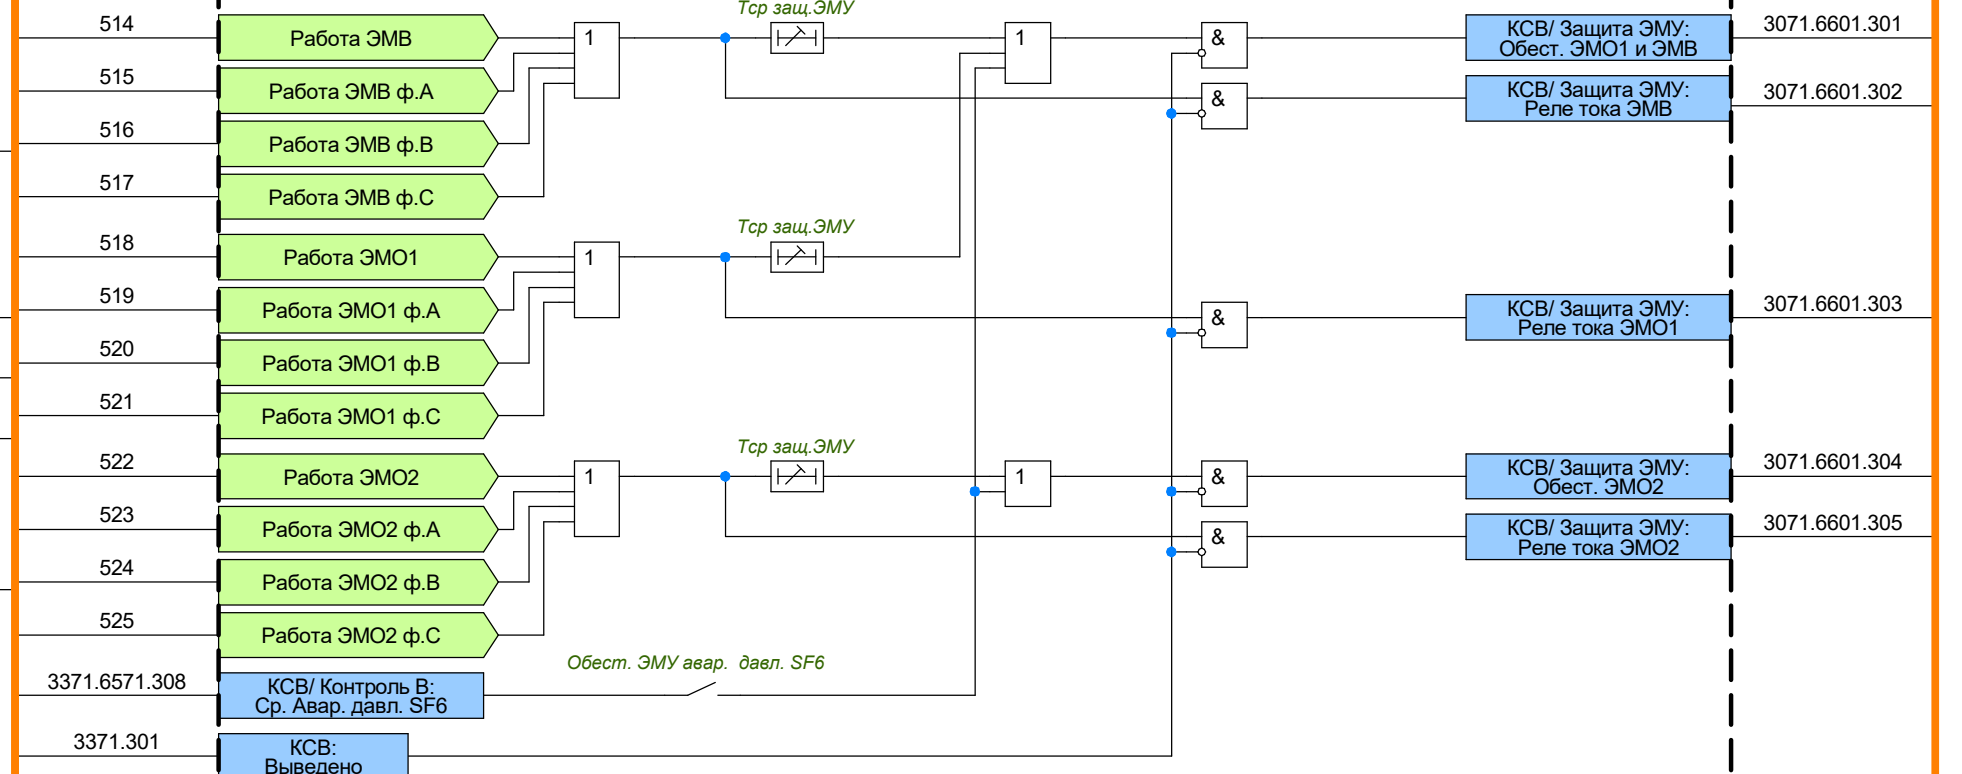


РФ (Реле фиксации) 6591

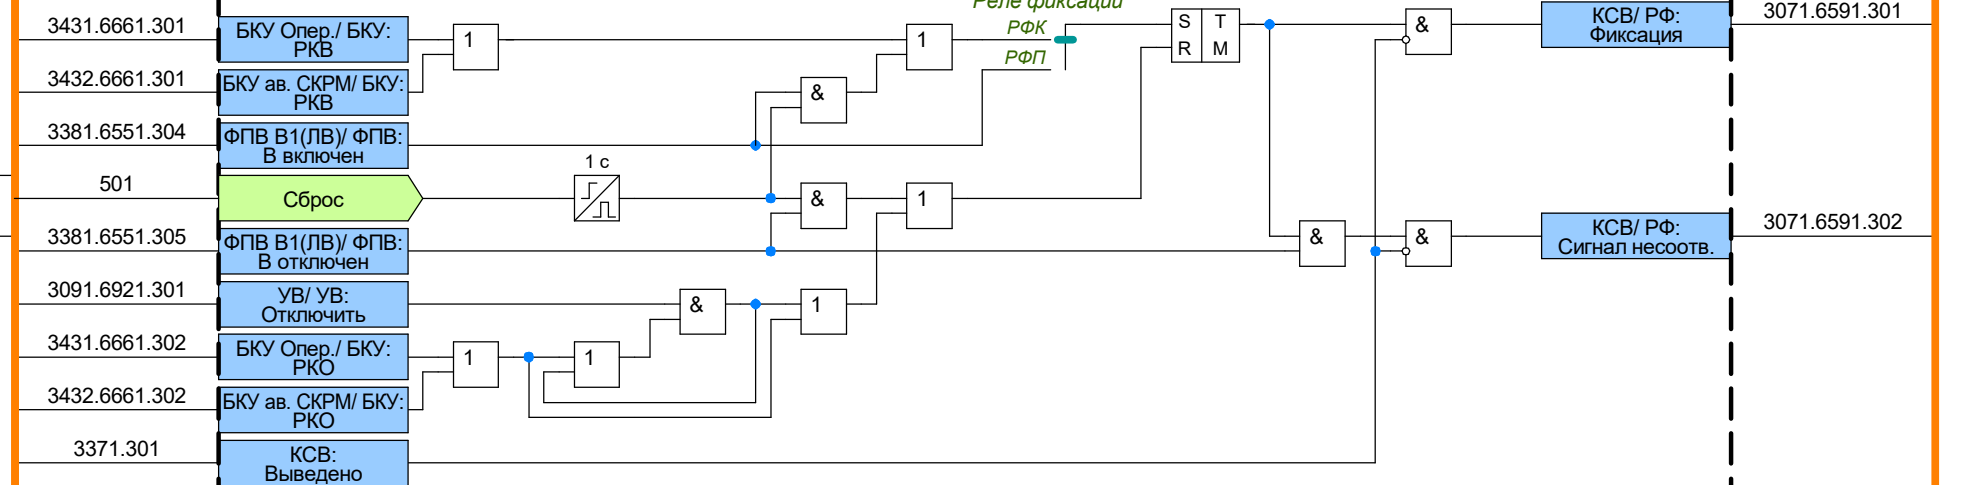


БКУ Опер. (Блок команд управления) 3431

БКУ 6661

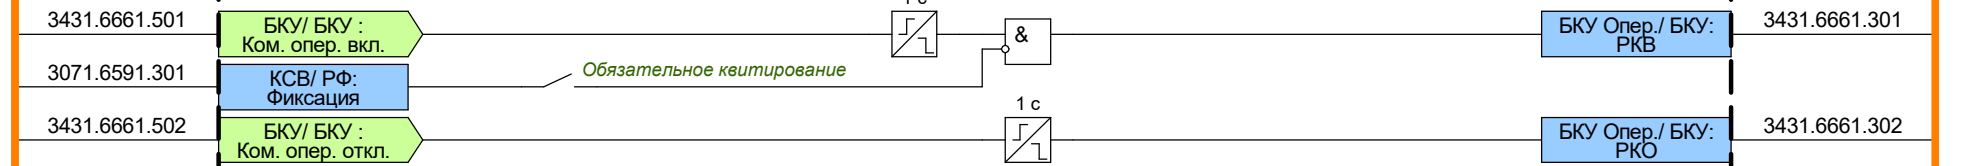



БКУ ав. СКРМ (Блок команд управления от автоматики СКРМ) 3432

БКУ 6661

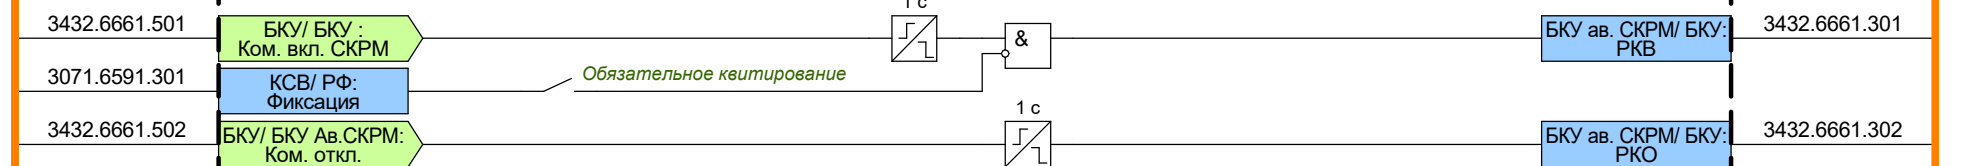


КСВ (Контроль силового выключателя) 3071

Блокировка управления 6901

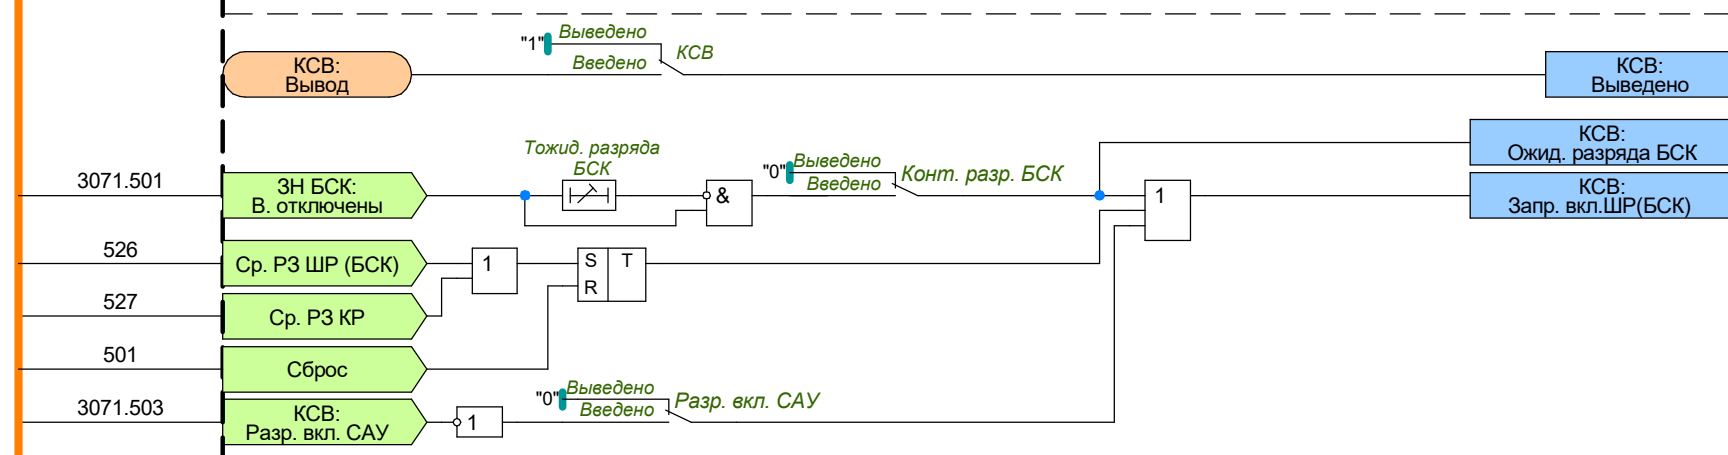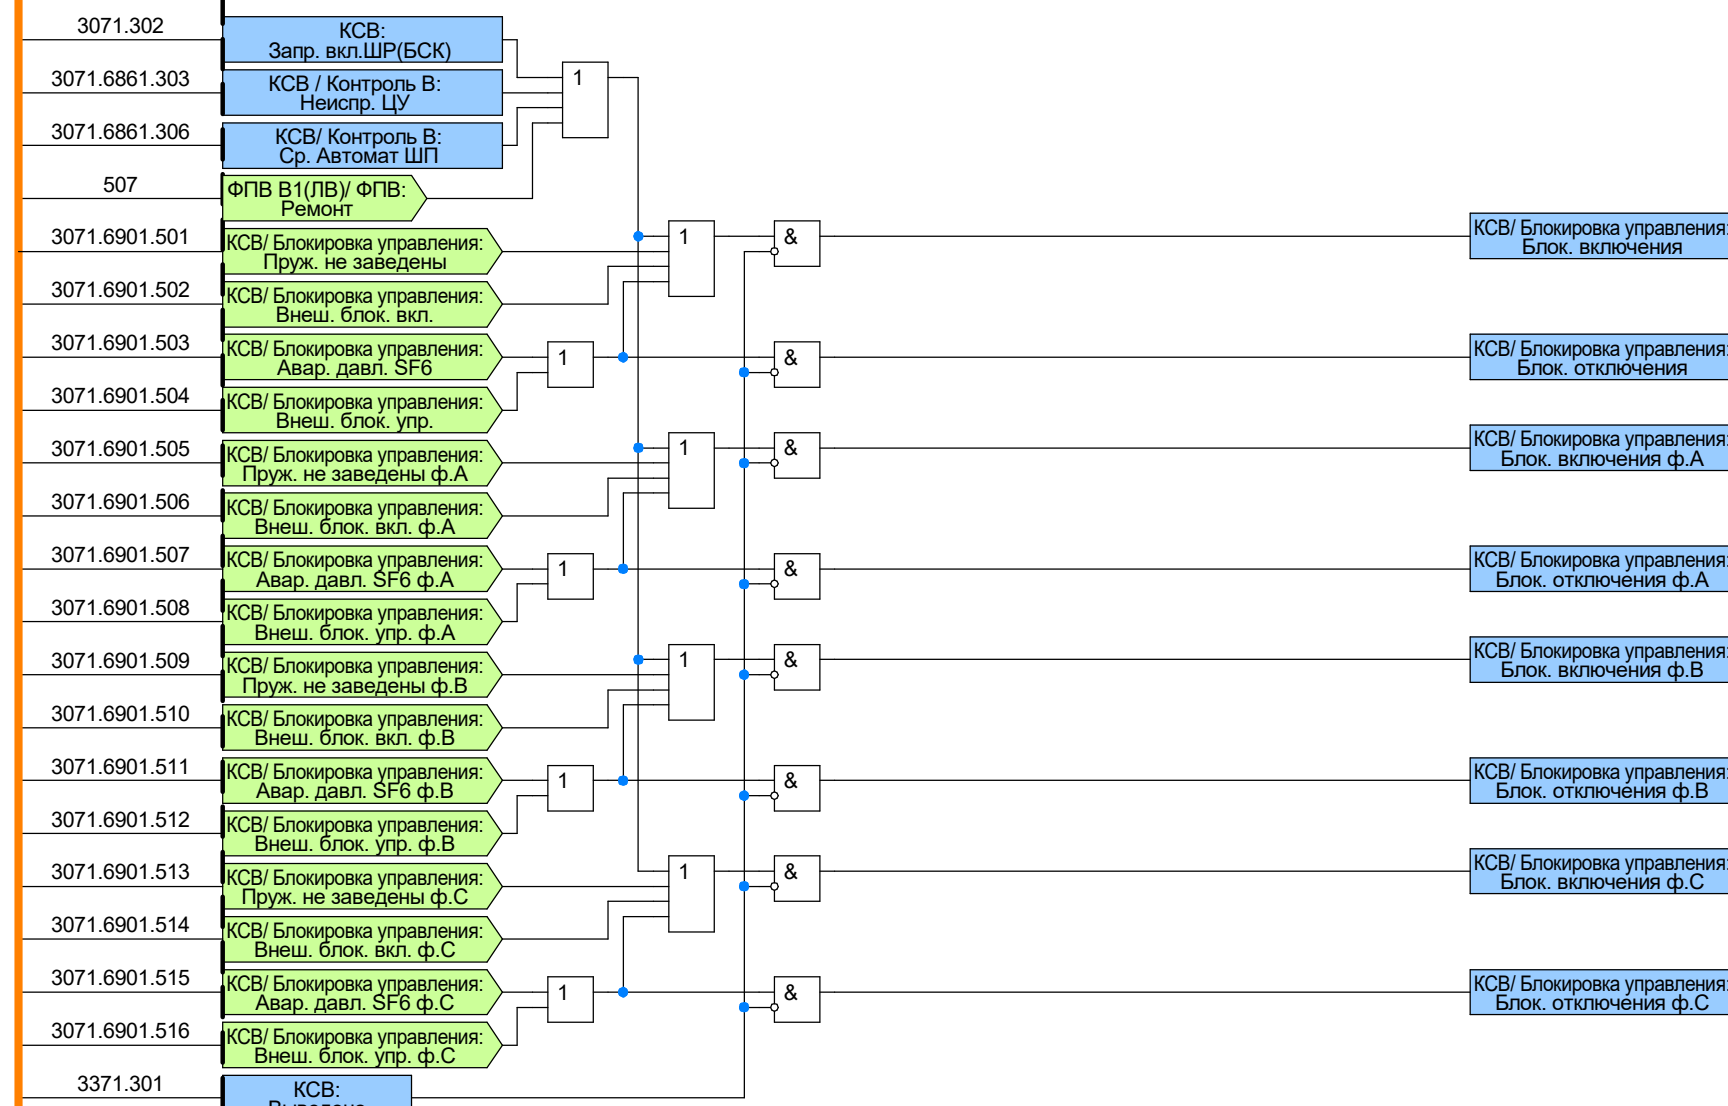

УВ УПНКП (Управление выключателем через синхронизатор) 3081

УВ УПНКП 6911

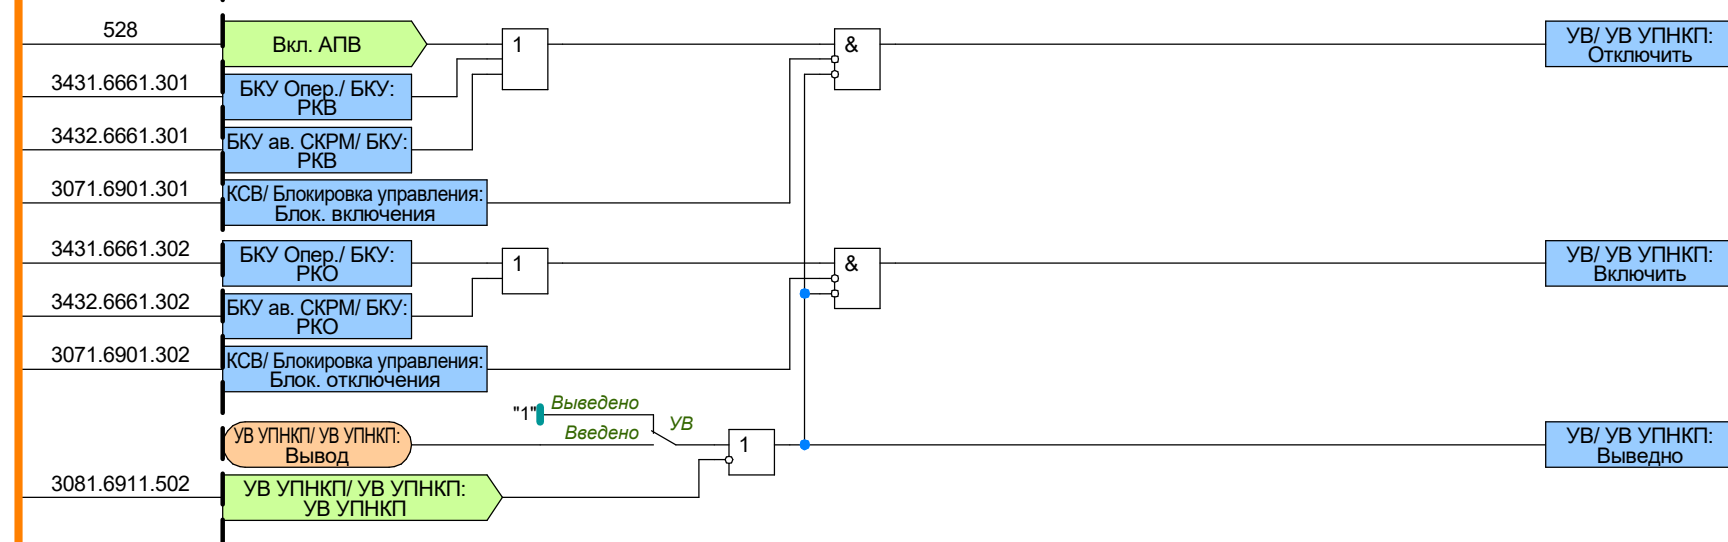

УВ (Управление выключателем) 3091

УВ 6921

