


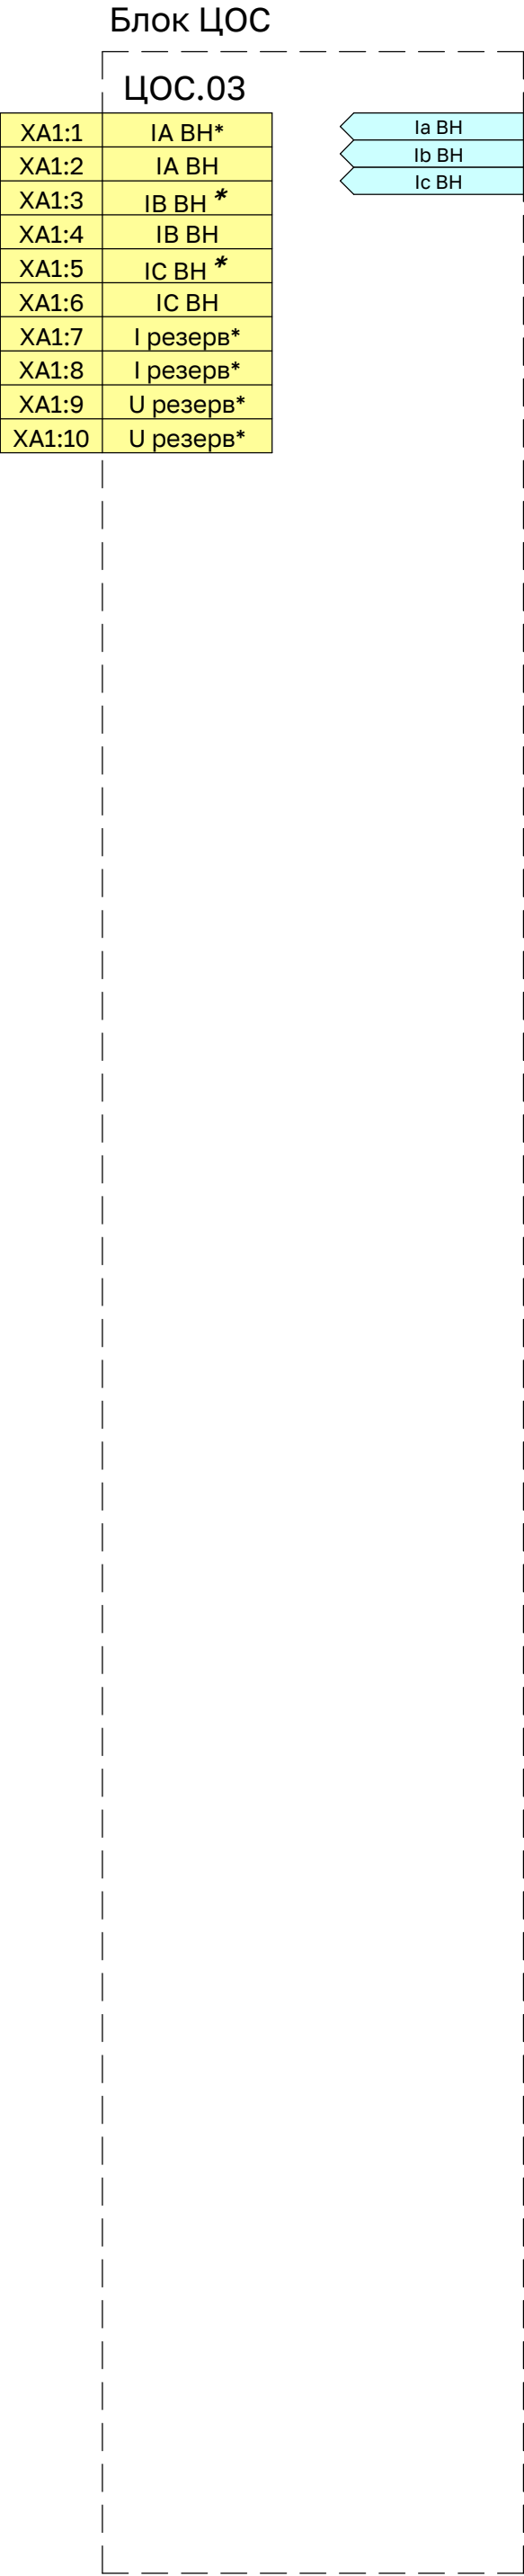

Входы ФСУ		
Общая логика: Контр. ОТ терм	90.501	
Общая логика: БИ ток В	90.502	
Общая логика: SA Упр. В	90.503	
Общая логика: SA Упр. УПНКП	90.504	
Общая логика: SA Откл. УРОВ1	90.505	
Общая логика: SA Откл. УРОВ2	90.506	
Общая логика: SA Упр. КР	90.507	
Общая логика: SA Уск. ОАПВ	90.508	
Общая логика: SA Шунт. КОР	90.509	
Общая логика: Вых. цепи разобраны	90.510	
УРОВ В1(ЛВ) ВН / УРОВ: Пуск УРОВ	3321.6821.501	
ФПВ / ФПВ: Б/К В фА включен	501	
ФПВ / ФПВ: Б/К В фВ включен	502	
ФПВ / ФПВ: Б/К В фС включен	503	
ФПВ / ФПВ: Б/К В фА отключен	504	
ФПВ / ФПВ: Б/К В фВ отключен	505	
ФПВ / ФПВ: Б/К В фС отключен	506	
ЗНФ: Пуск ЗНФ	3541.6701.501	
ЗНФ: Цикл ОАПВ	3541.6701.502	
ФПВ / ФПВ: Б/К В вкл	3461.6551.501	
ФПВ / ФПВ: Б/К В вкл ф.А	3461.6551.502	
ФПВ / ФПВ: Б/К В вкл ф.В	3461.6551.503	
ФПВ / ФПВ: Б/К В вкл ф.С	3461.6551.504	
ФПВ / ФПВ: Б/К В откл ф.А	3461.6551.505	
ФПВ / ФПВ: Б/К В откл ф.В	3461.6551.506	
ФПВ / ФПВ: Б/К В откл ф.С	3461.6551.507	
ФПВ / ФПВ: Б/К В откл	3461.6551.508	
ФПВ / ФПВ: Ремонт	507	
ФПВ / Р1: Б/К Р вкл	3461.6531.501	
ФПВ / Р1: Б/К Р вкл ф.А	3461.6531.502	
ФПВ / Р1: Б/К Р вкл ф.В	3461.6531.503	
ФПВ / Р1: Б/К Р вкл ф.С	3461.6531.504	
ФПВ / Р1: Б/К Р откл	3461.6531.505	
ФПВ / Р1: Б/К Р откл ф.А	3461.6531.506	
ФПВ / Р1: Б/К Р откл ф.В	3461.6531.507	
ФПВ / Р1: Б/К Р откл ф.С	3461.6531.508	
ФПВ / Р2: Б/К Р вкл	3461.6532.501	
ФПВ / Р2: Б/К Р вкл ф.А	3461.6532.502	
ФПВ / Р2: Б/К Р вкл ф.В	3461.6532.503	
ФПВ / Р2: Б/К Р вкл ф.С	3461.6532.504	
ФПВ / Р2: Б/К Р откл	3461.6532.505	
ФПВ / Р2: Б/К Р откл ф.А	3461.6532.506	
ФПВ / Р2: Б/К Р откл ф.В	3461.6532.507	
ФПВ / Р2: Б/К Р откл ф.С	3461.6532.508	
Контр. ЭМО1	508	
Контр. ЭМО1 ф.А	522	
Контр. ЭМО1 ф.В	525	
Контр. ЭМО1 ф.С	528	
Контр. ЭМВ	513	
Контр. ЭМВ ф.А	524	
Контр. ЭМВ ф.В	527	
Контр. ЭМВ ф.С	528	
Контр. ЭМО2	509	
Контр. ЭМО2 ф.А	523	
Контр. ЭМО2 ф.В	526	
Контр. ЭМО2 ф.С	529	
КСВ/ Контроль В: Неиспр. обогр.	3071.6861.513	
КСВ/ Контроль В: Автомат ШП	3071.6861.514	


Входы ФСУ		
КСВ/ Контроль В: Низк. давл. SF6	3071.6861.515	
КСВ/ Контроль В: Низк. давл. SF6 ф.А	3071.6861.516	
КСВ/ Контроль В: Низк. давл. SF6 ф.В	3071.6861.517	
КСВ/ Контроль В: Низк. давл. SF6 ф.С	3071.6861.518	
КСВ/ Контроль В: Авар. давл. SF6	3071.6861.519	
КСВ/ Контроль В: Авар. давл. SF6 ф.А	3071.6861.520	
КСВ/ Контроль В: Авар. давл. SF6 ф.В	3071.6861.521	
КСВ/ Контроль В: Авар. давл. SF6 ф.С	3071.6861.522	
КСВ/ Контроль В: Пруж. не заведены	3071.6861.523	
КСВ/ Контроль В: Пруж. не заведены ф.А	3071.6861.524	
КСВ/ Контроль В: Пруж. не заведены ф.В	3071.6861.525	
КСВ/ Контроль В: Пруж. не заведены ф.С	3071.6861.526	
КСВ/ Контроль В: Контр. ОТ ЭМВ/ЭМО1	3071.6861.527	
КСВ/ Контроль В: Контр. ОТ ЭМО2	3071.6861.528	
КСВ/ Контроль ТТ Низк. давл. SF6 ТТ	3071.6581.501	
КСВ/ Контроль ТТ Низк. давл. SF6 ТТ ф.А	3071.6581.502	
КСВ/ Контроль ТТ Низк. давл. SF6 ТТ ф.В	3071.6581.503	
КСВ/ Контроль ТТ Низк. давл. SF6 ТТ ф.С	3071.6581.504	
КСВ/ Контроль ТТ Авар. давл. SF6 ТТ	3071.6581.505	
КСВ/ Контроль ТТ Авар. давл. SF6 ТТ ф.А	3071.6581.506	
КСВ/ Контроль ТТ Авар. давл. SF6 ТТ ф.В	3071.6581.507	
КСВ/ Контроль ТТ Авар. давл. SF6 ТТ ф.С	3071.6581.508	
КСВ/ Контроль ТТ Неиспр. обогр. ТТ	3071.6581.509	
Работа ЭМВ	510	
Работа ЭМВ ф.А	516	
Работа ЭМВ ф.В	519	
Работа ЭМВ ф.С	522	
Работа ЭМО1	511	
Работа ЭМО1 ф.А	514	
Работа ЭМО1 ф.В	517	
Работа ЭМО1 ф.С	520	
Работа ЭМО2	512	
Работа ЭМО2 ф.А	515	
Работа ЭМО2 ф.В	518	
Работа ЭМО2 ф.С	521	
БКУ / БКУ : Ком. опер. вкл.	3431.6661.501	
БКУ / БКУ : Ком. опер. откл.	3431.6661.502	
БКУ / БКУ : Ком. вкл. СКРМ	3432.6661.501	
БКУ / БКУ Ав.СКРМ: Ком. откл.	3432.6661.502	
ФПВ / ФПВ: Ремонт	507	
КСВ/ Блокировка управления: Пруж. не заведены	3071.6901.502	
КСВ/ Блокировка управления: Внеш. блок. вкл.	3071.6901.503	
КСВ/ Блокировка управления: Авар. давл. SF6	3071.6901.504	
КСВ/ Блокировка управления: Внеш. блок. упр.	3071.6901.505	
КСВ/ Блокировка управления: Пруж. не заведены ф.А	3071.6901.506	
КСВ/ Блокировка управления: Внеш. блок. вкл. ф.А	3071.6901.507	
КСВ/ Блокировка управления: Авар. давл. SF6 ф.А	3071.6901.508	
КСВ/ Блокировка управления: Внеш. блок. упр. ф.А	3071.6901.509	
КСВ/ Блокировка управления: Пруж. не заведены ф.В	3071.6901.510	
КСВ/ Блокировка управления: Внеш. блок. вкл. ф.Б	3071.6901.511	
КСВ/ Блокировка управления: Авар. давл. SF6 ф.В	3071.6901.512	
КСВ/ Блокировка управления: Внеш. блок. упр. ф.В	3071.6901.513	
КСВ/ Блокировка управления: Пруж. не заведены ф.С	3071.6901.514	
КСВ/ Блокировка управления: Внеш. блок. вкл. ф.С	3071.6901.515	
КСВ/ Блокировка управления: Авар. давл. SF6 ф.С	3071.6901.516	
КСВ/ Блокировка управления: Внеш. блок. упр. ф.С	3071.6901.517	
ЗН БСК: В. отключены	3071.501	
КСВ: Ср. РЗ ШР(БСК)	3071.502	

Входы ФСУ		
КСВ: Ср. РЗ КР	3071.503	
КСВ: Сброс	3071.504	
КСВ: Разр. вкл. САУ	3071.505	
УВ УПНКП/ УВ УПНКП: Бкл. АПВ	3081.6911.501	
УВ УПНКП/ УВ УПНКП: УВ УПНКП	3081.6911.502	
УВ/ УВ: Ср. РЗ ШР(БСК)	3091.6921.501	
УВ/ УВ: Ср. РЗ КР	3091.6921.502	
УВ/ УВ: Ср. РЗ ЛЭП	3091.6921.503	
Работа ЭМО1	511	
Контр. ЭМО1	508	
Работа ЭМО2	512	
Контр. ЭМО2	509	
УВ/ УВ: Бкл. АПВ	3091.6921.504	
Работа ЭМВ	510	
Контр. ЭМВ	513	
Работа ЭМО1 ф.А	514	
Контр. ЭМО1 ф.А	522	
Работа ЭМО2 ф.А	515	
Контр. ЭМО2 ф.А	523	
Работа ЭМВ ф.А	516	
Контр. ЭМВ ф.А	524	
Работа ЭМО1 ф.В	517	
Контр. ЭМО1 ф.В	525	
Работа ЭМО2 ф.В	518	
Контр. ЭМО2 ф.В	526	
Работа ЭМВ ф.В	519	
Контр. ЭМВ ф.В	527	
Работа ЭМО1 ф.С	520	
Контр. ЭМО1 ф.С	528	
Работа ЭМО2 ф.С	521	
Контр. ЭМО2 ф.С	529	
Работа ЭМВ ф.С	522	
Контр. ЭМВ ф.С	528	
УВ/ УВ: УВ УПНКП	3091.6921.505	




КСВ (Контроль силового выключателя) 3071

Контроль В 6861

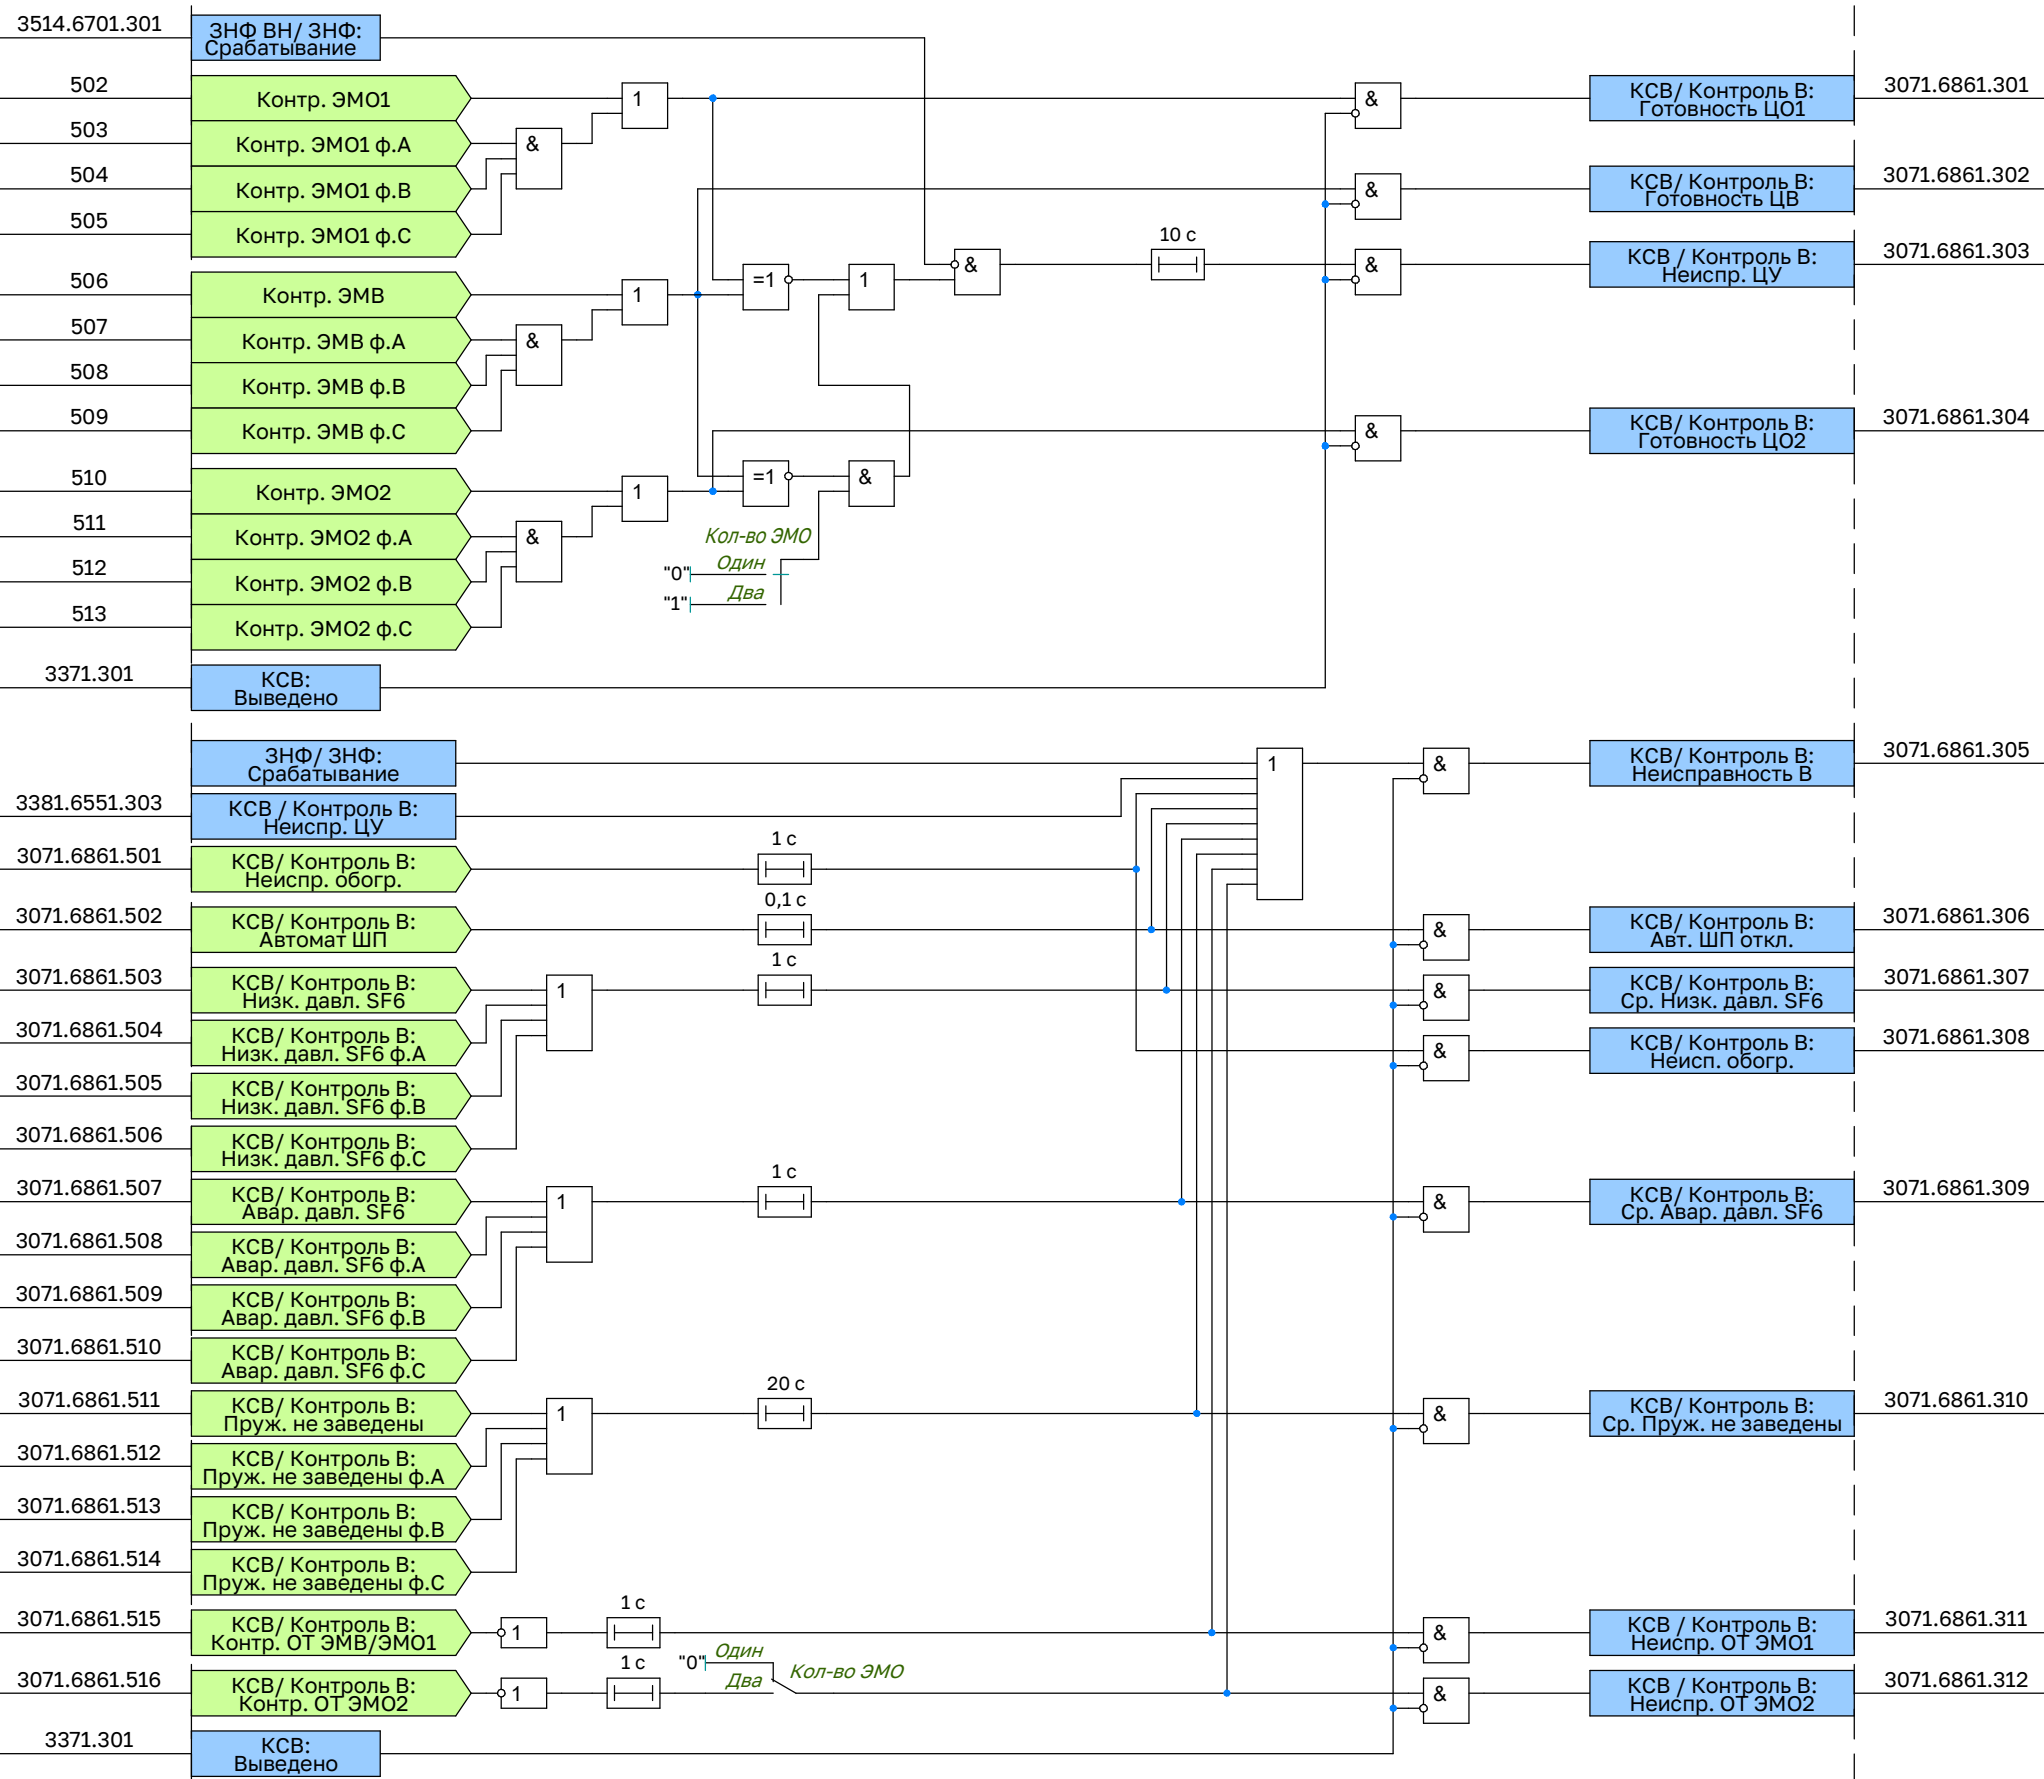


КСВ (Контроль силового выключателя) 3071


Контроль ТТ 6581

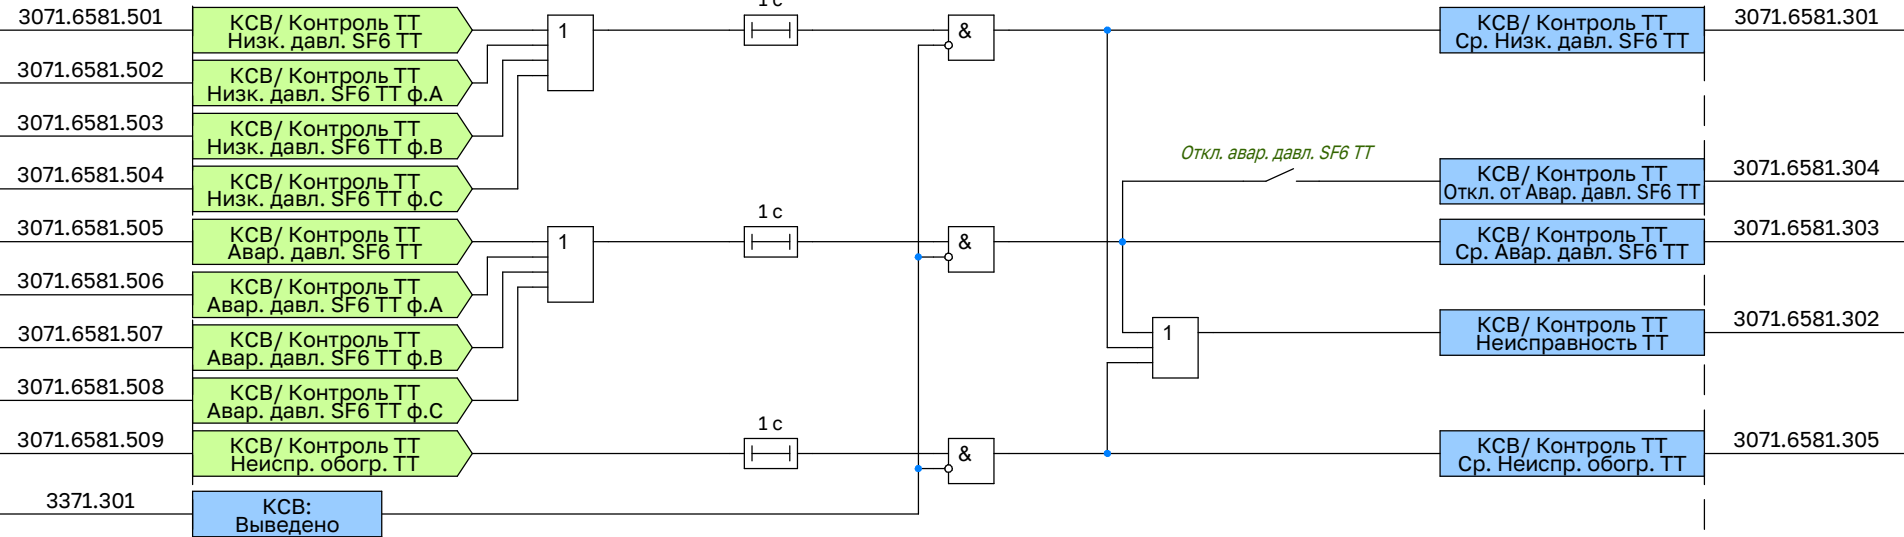

Защита ЭМУ 6601

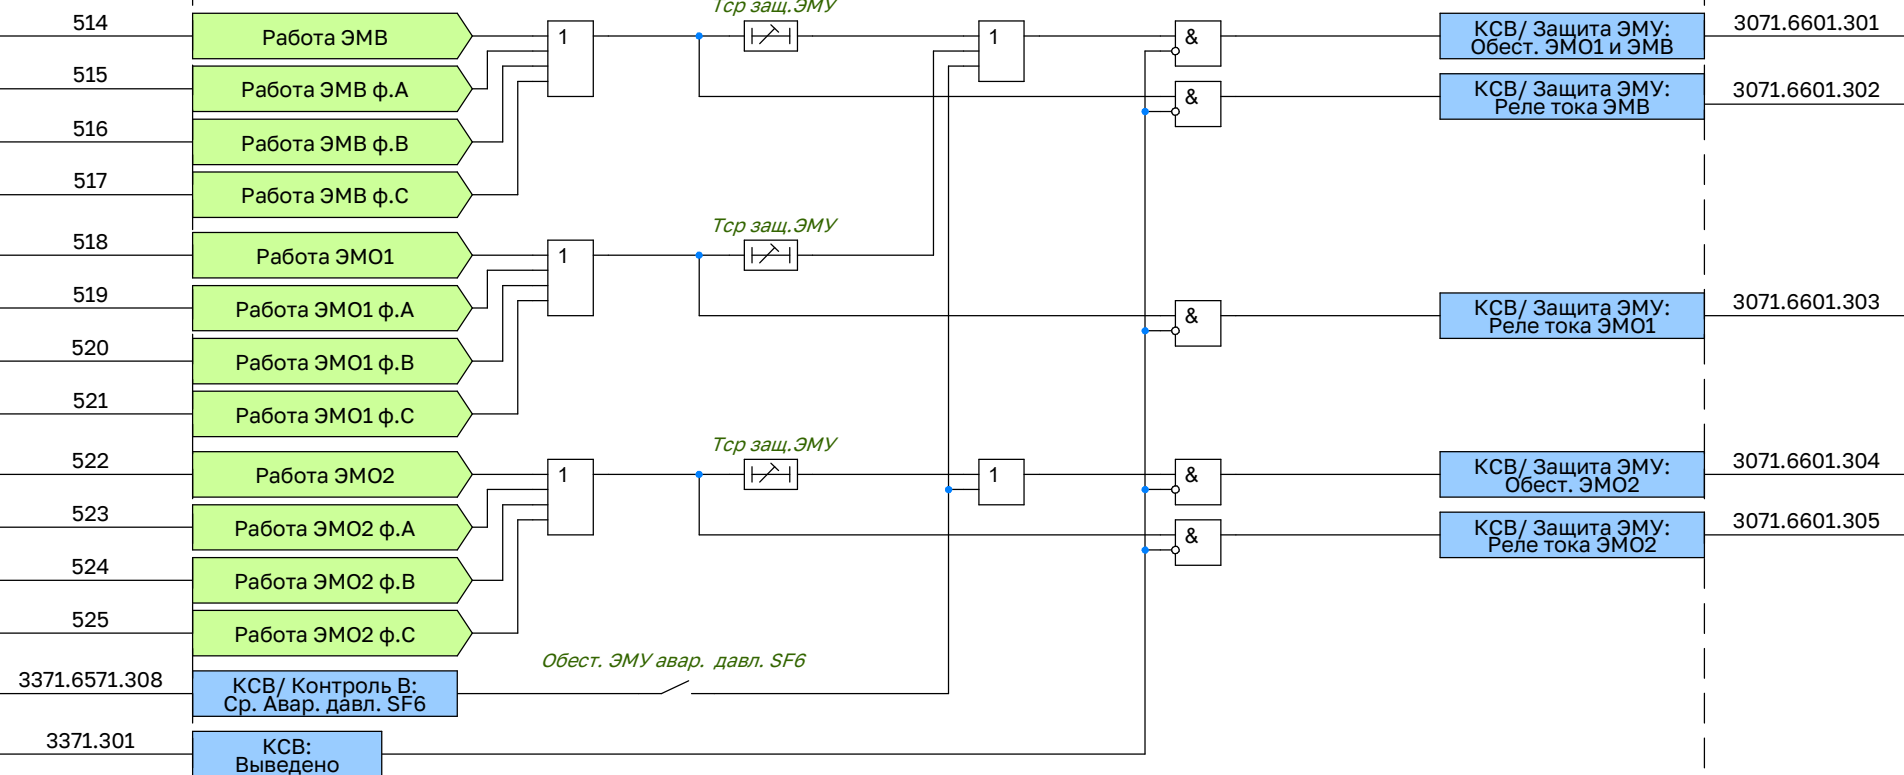


РФ (Реле фиксации) 6591

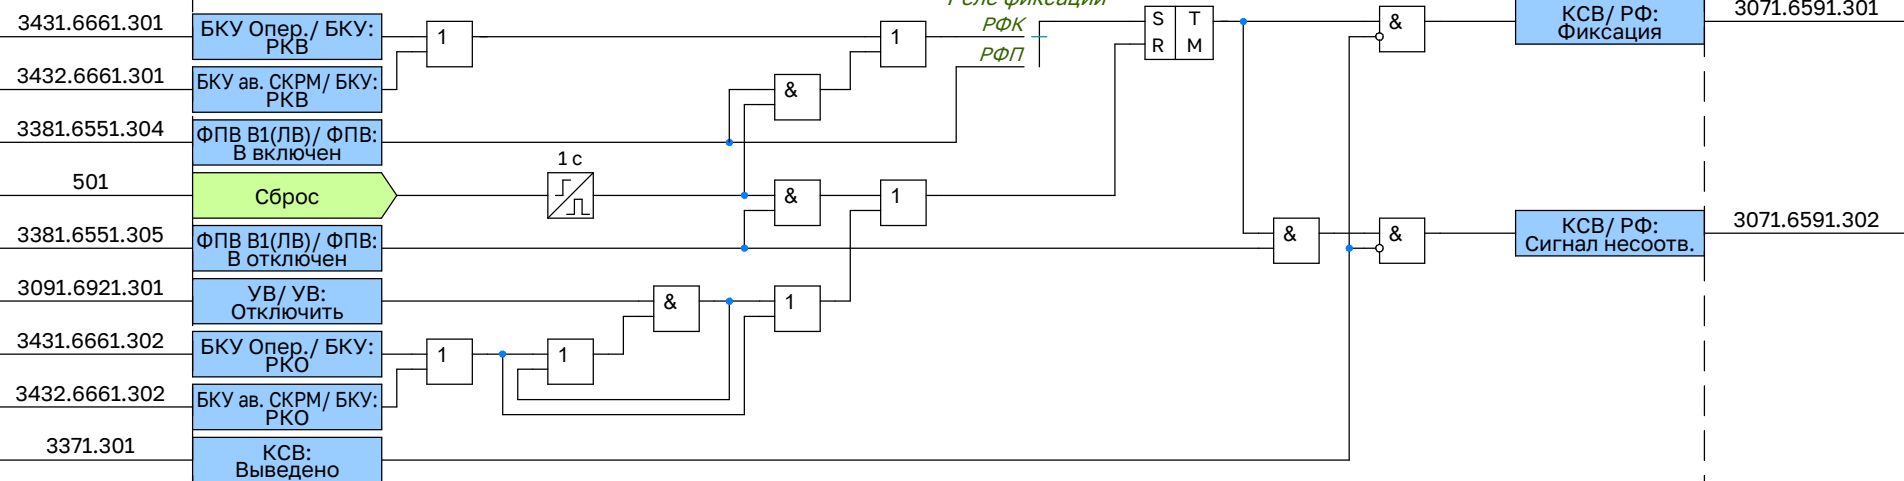


БКУ Опер. (Блок команд управления) 3431

БКУ 6661

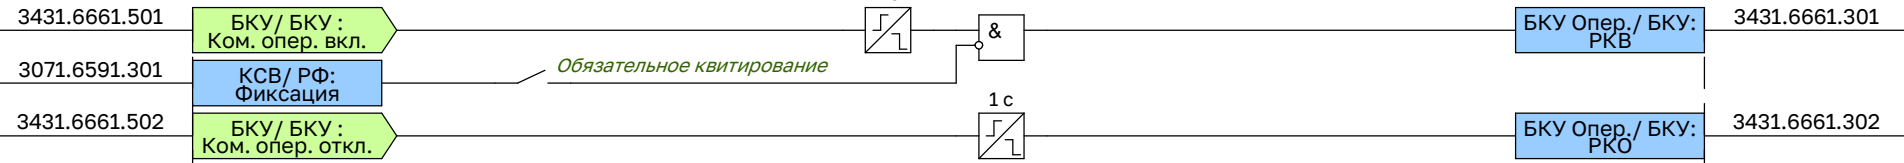


БКУ ав. СКРМ (Блок команд управления от автоматики СКРМ) 3432

БКУ 6661

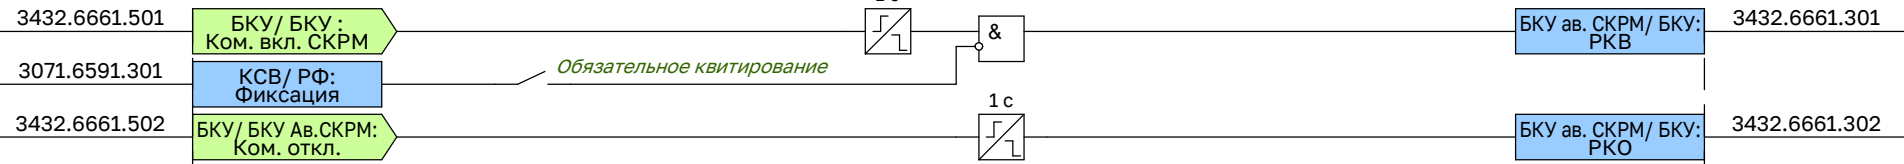


КСВ (Контроль силового выключателя) 3071

Блокировка управления 6901

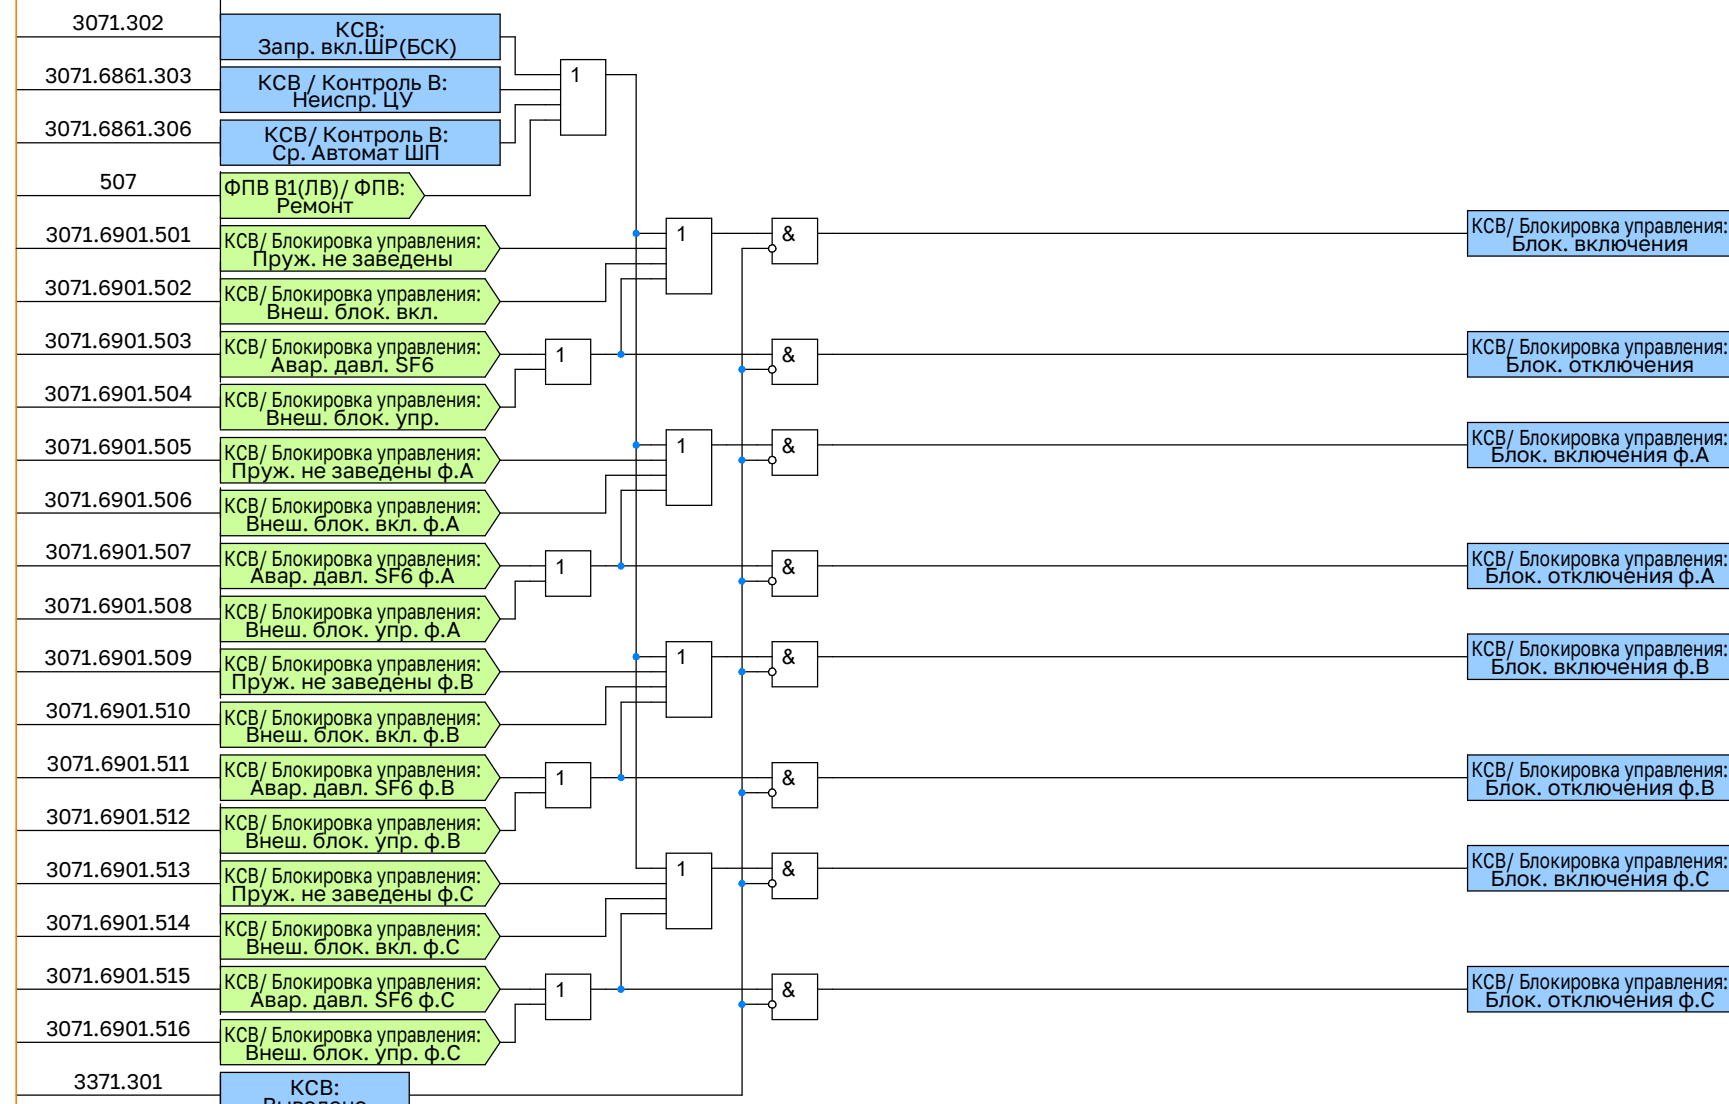


КСВ: Выведено

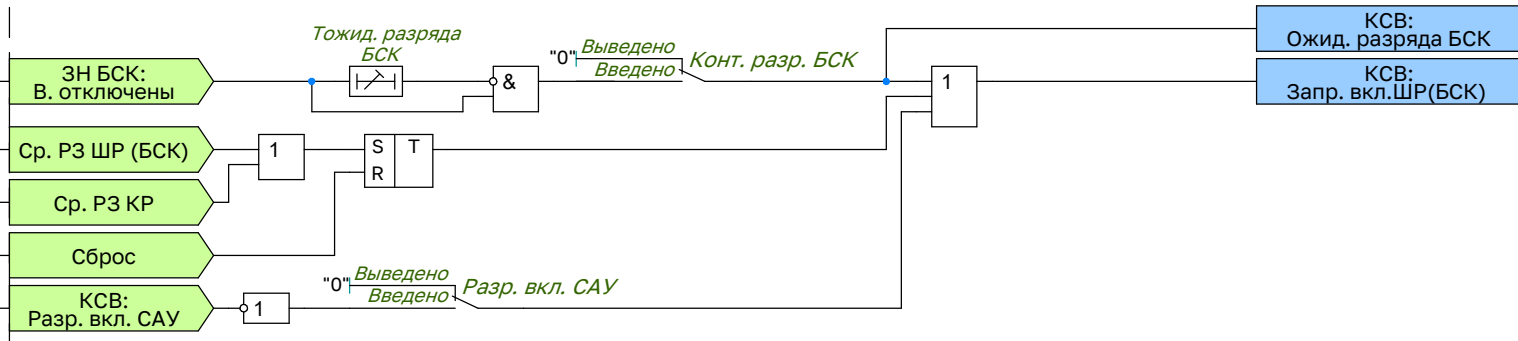

УВ УПНКП (Управление выключателем через синхронизатор) 3081

УВ УПНКП 6911

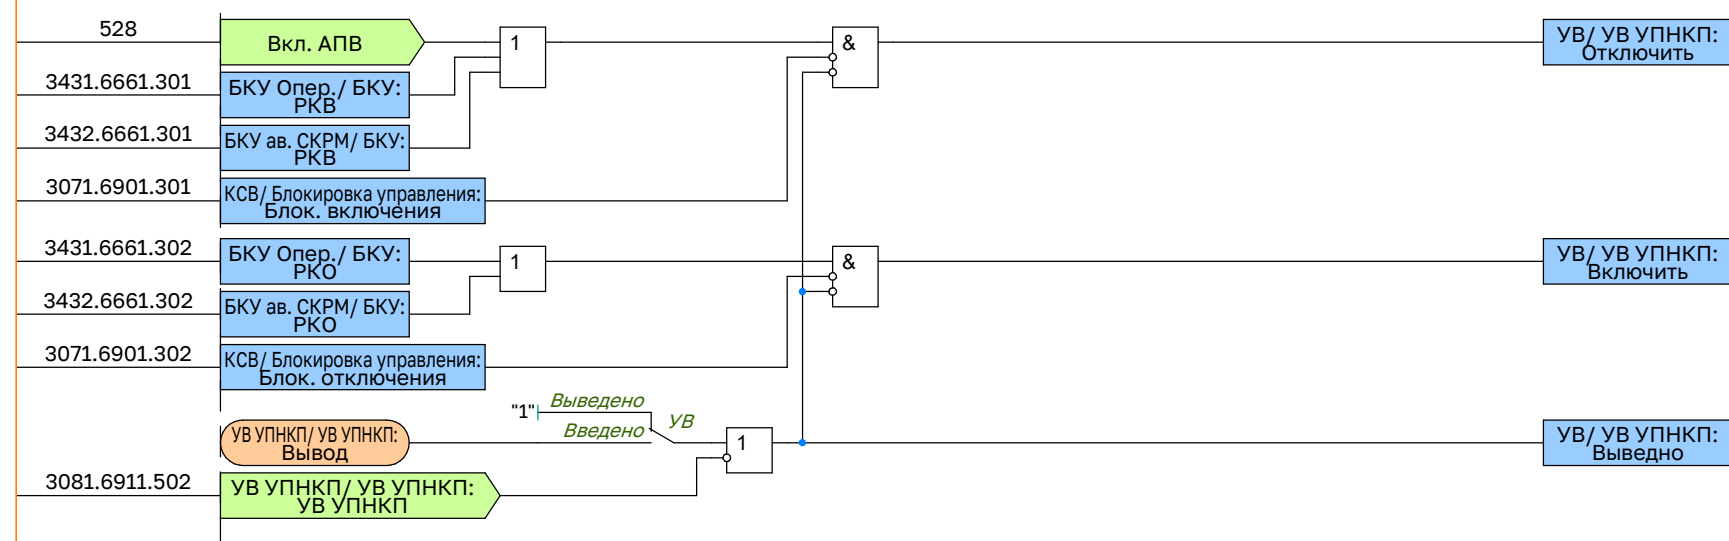

УВ (Управление выключателем) 3091

УВ 6921

