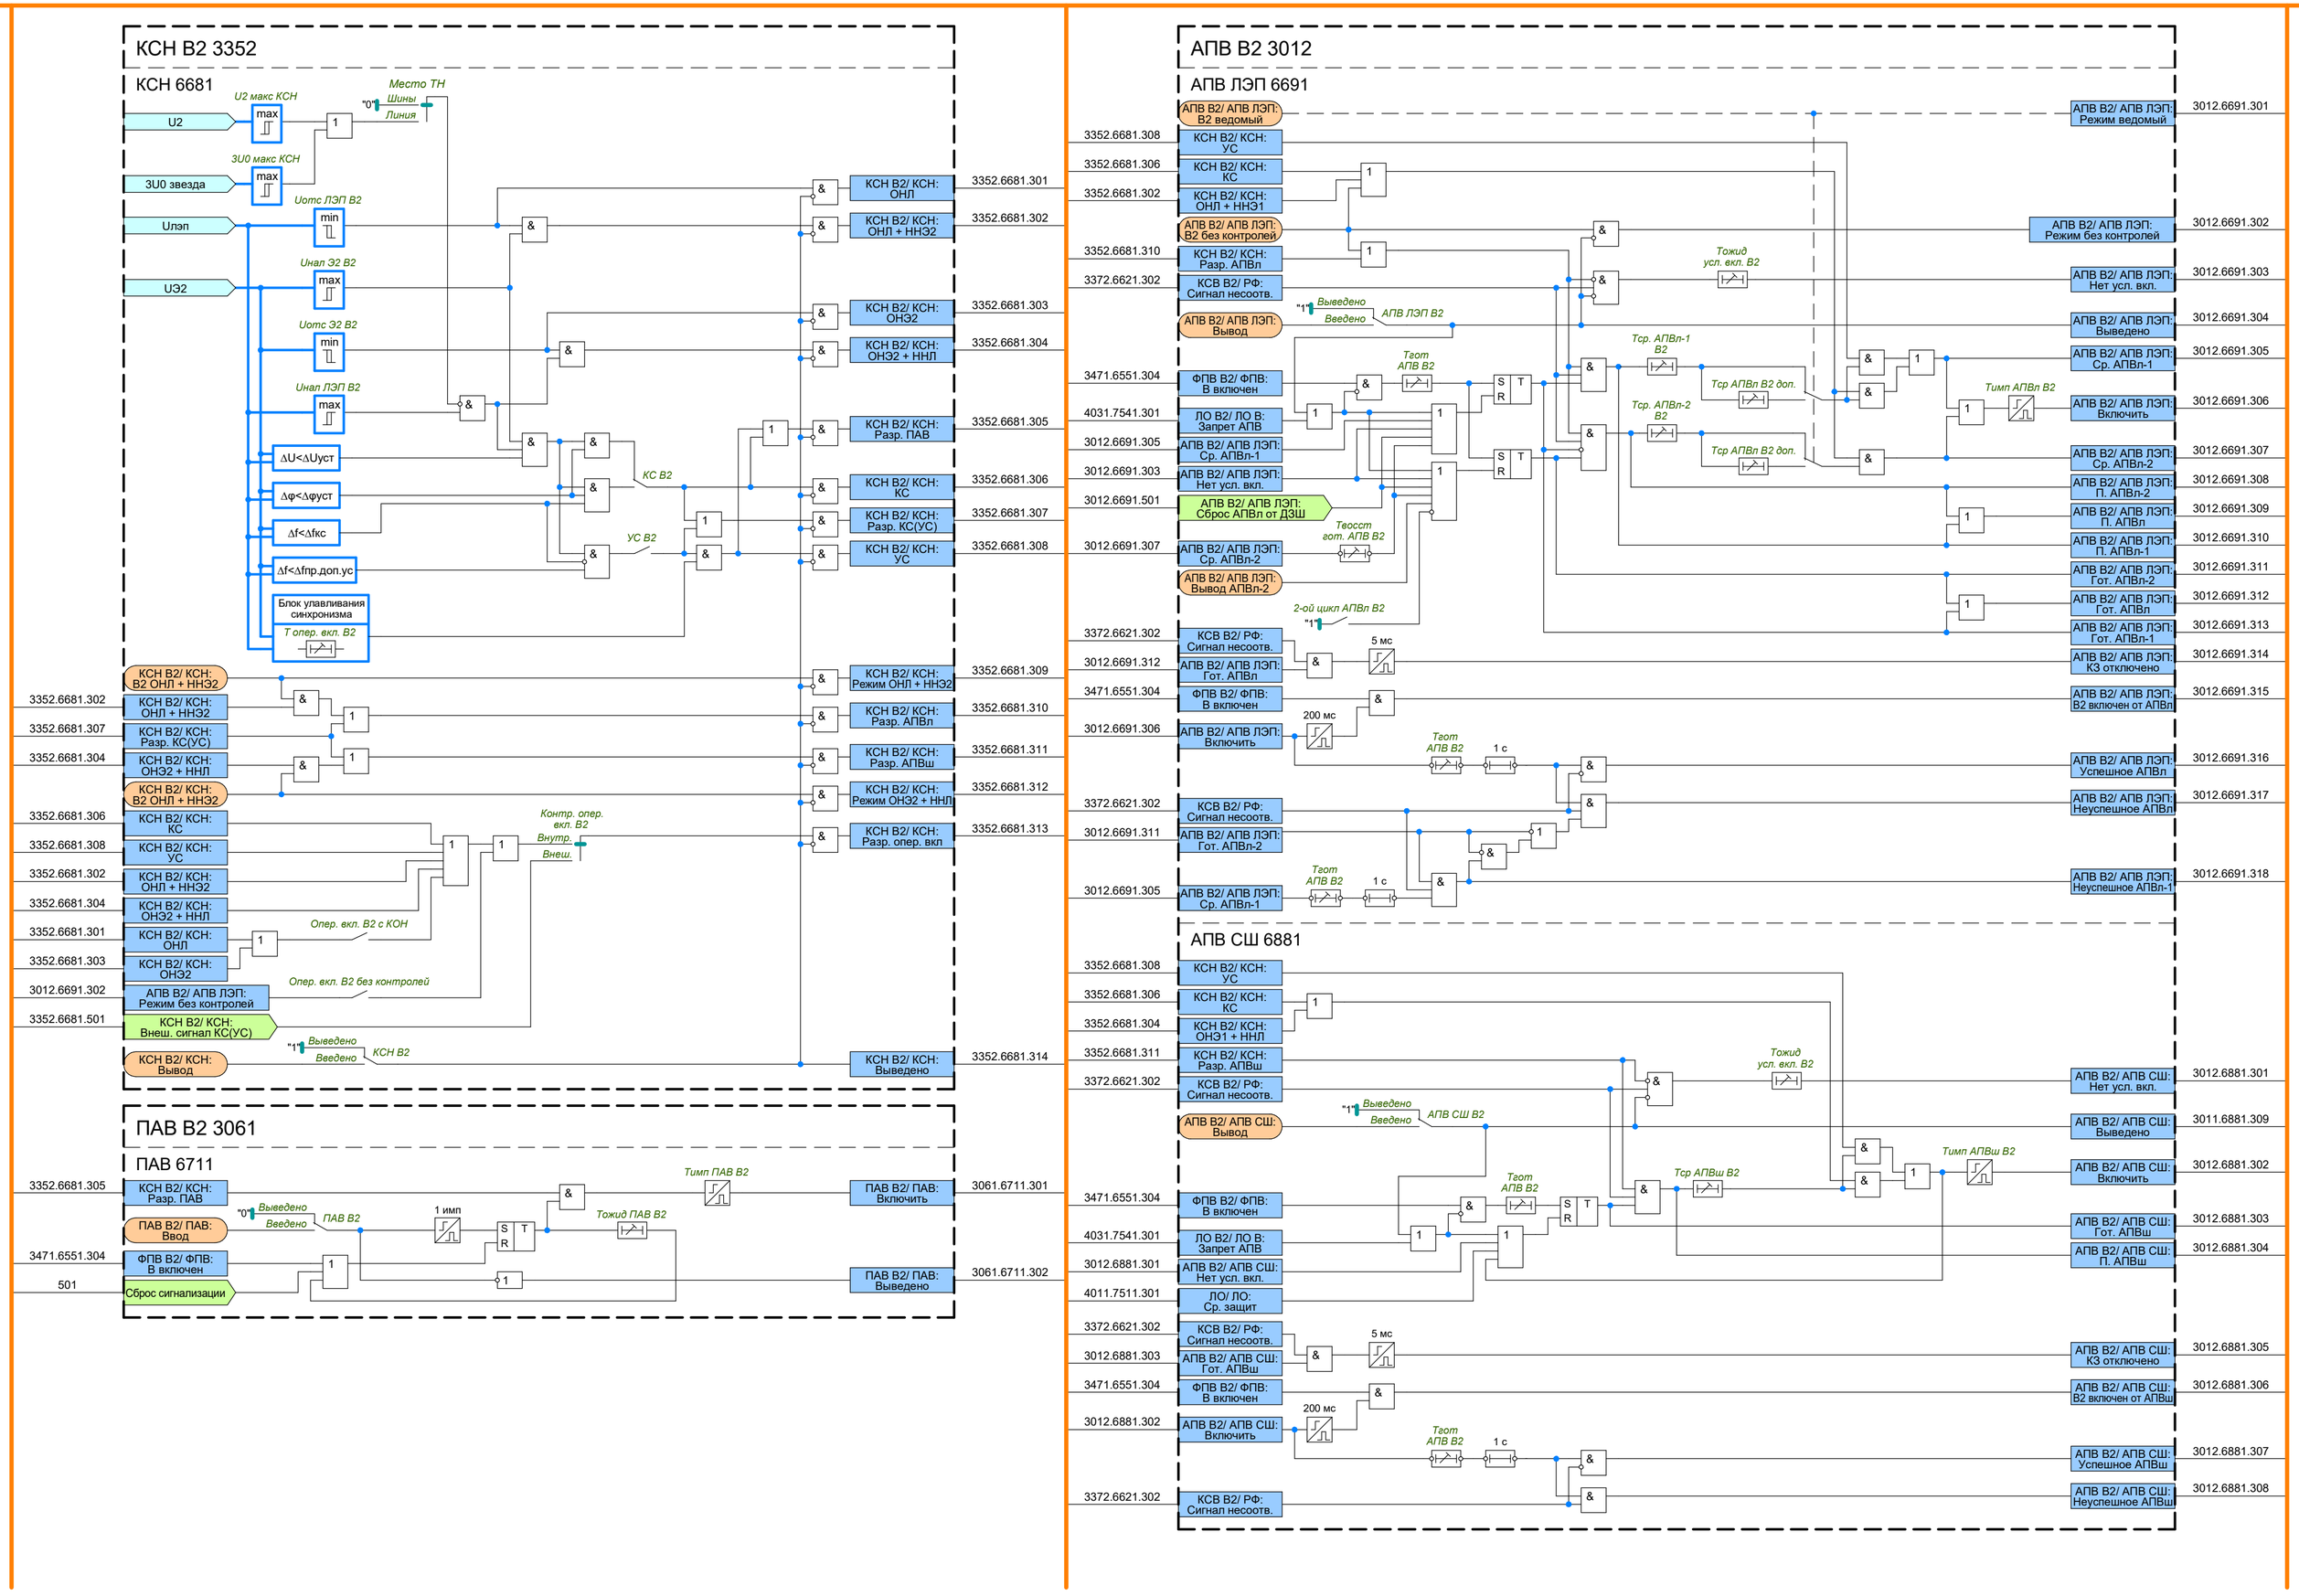
КСН В2 3352
КСН 6681
U2
3U0 звезда
Uлэп
UЭ2
U2 макс КСН
3U0 макс КСН
Uотс ЛЭП В2
Uнал Э2 В2
Uотс Э2 В2
Uнал ЛЭП В2
Место ТН
Шины
Линия
ΔU<ΔUуст
Δφ<Δφуст
Δf<Δfкс
Δf<Δfпр.доп.ус
Блок улавливания синхронизма
Т опер. вкл. В2
КС В2
УС В2
КСН В2/ КСН: ОНЛ
КСН В2/ КСН: ОНЛ + ННЭ2
КСН В2/ КСН: ОНЭ2
КСН В2/ КСН: ОНЭ2 + ННЛ
КСН В2/ КСН: Разр. ПАВ
КСН В2/ КСН: КС
КСН В2/ КСН: Разр. КС(УС)
КСН В2/ КСН: УС
КСН В2/ КСН: В2 ОНЛ + ННЭ2
КСН В2/ КСН: Режим ОНЛ + ННЭ2
КСН В2/ КСН: Разр. АПВл
КСН В2/ КСН: Разр. АПВш
КСН В2/ КСН: Режим ОНЭ2 + ННЛ
КСН В2/ КСН: Разр. опер. вкл
КСН В2/ КСН: Выведено
КСН В2/ КСН: Вывод
Контр. опер. вкл. В2
Внутр.
Внеш.
Опер. вкл. В2 с КОН
Опер. вкл. В2 без контролей
АПВ В2/ АПВ ЛЭП: Режим без контролей
КСН В2/ КСН: Внеш. сигнал КС(УС)
Выведено
Введено
КСН В2
3352.6681.301
3352.6681.302
3352.6681.303
3352.6681.304
3352.6681.305
3352.6681.306
3352.6681.307
3352.6681.308
3352.6681.309
3352.6681.310
3352.6681.311
3352.6681.312
3352.6681.313
3352.6681.314
3352.6681.302
3352.6681.307
3352.6681.304
3352.6681.306
3352.6681.308
3352.6681.302
3352.6681.304
3352.6681.301
3352.6681.303
3012.6691.302
3352.6681.501
ПАВ В2 3061
ПАВ 6711
КСН В2/ КСН: Разр. ПАВ
ПАВ В2/ ПАВ: Ввод
ФПВ В2/ ФПВ: В включен
Сброс сигнализации
Тимп ПАВ В2
Тожид ПАВ В2
ПАВ В2
1 имп
ПАВ В2/ ПАВ: Включить
ПАВ В2/ ПАВ: Выведено
3352.6681.305
3471.6551.304
501
3061.6711.301
3061.6711.302
АПВ В2 3012
АПВ ЛЭП 6691
АПВ В2/ АПВ ЛЭП: В2 ведомый
КСН В2/ КСН: УС
КСН В2/ КСН: КС
КСН В2/ КСН: ОНЛ + ННЭ1
АПВ В2/ АПВ ЛЭП: В2 без контролей
КСН В2/ КСН: Разр. АПВл
КСВ В2/ РФ: Сигнал несоотв.
АПВ В2/ АПВ ЛЭП: Вывод
ФПВ В2/ ФПВ: В включен
ЛО В2/ ЛО В: Запрет АПВ
АПВ В2/ АПВ ЛЭП: Ср. АПВл-1
АПВ В2/ АПВ ЛЭП: Нет усл. вкл.
АПВ В2/ АПВ ЛЭП: Сброс АПВл от ДЗШ
АПВ В2/ АПВ ЛЭП: Ср. АПВл-2
АПВ В2/ АПВ ЛЭП: Вывод АПВл-2
КСВ В2/ РФ: Сигнал несоотв.
АПВ В2/ АПВ ЛЭП: Гот. АПВл
ФПВ В2/ ФПВ: В включен
АПВ В2/ АПВ ЛЭП: Включить
КСВ В2/ РФ: Сигнал несоотв.
АПВ В2/ АПВ ЛЭП: Гот. АПВл-2
АПВ В2/ АПВ ЛЭП: Ср. АПВл-1
Выведено
Введено
АПВ ЛЭП В2
Тгот АПВ В2
Твосст гот. АПВ В2
2-ой цикл АПВл В2
Тожид усл. вкл. В2
Тср. АПВл-1 В2
Тср АПВл В2 доп.
Тср. АПВл-2 В2
Тимп АПВл В2
5 мс
200 мс
1 с
АПВ В2/ АПВ ЛЭП: Режим ведомый
АПВ В2/ АПВ ЛЭП: Режим без контролей
АПВ В2/ АПВ ЛЭП: Нет усл. вкл.
АПВ В2/ АПВ ЛЭП: Выведено
АПВ В2/ АПВ ЛЭП: Ср. АПВл-1
АПВ В2/ АПВ ЛЭП: Включить
АПВ В2/ АПВ ЛЭП: Ср. АПВл-2
АПВ В2/ АПВ ЛЭП: П. АПВл-2
АПВ В2/ АПВ ЛЭП: П. АПВл
АПВ В2/ АПВ ЛЭП: П. АПВл-1
АПВ В2/ АПВ ЛЭП: Гот. АПВл-2
АПВ В2/ АПВ ЛЭП: Гот. АПВл
АПВ В2/ АПВ ЛЭП: Гот. АПВл-1
АПВ В2/ АПВ ЛЭП: КЗ отключено
АПВ В2/ АПВ ЛЭП: В2 включен от АПВл
АПВ В2/ АПВ ЛЭП: Успешное АПВл
АПВ В2/ АПВ ЛЭП: Неуспешное АПВл
АПВ В2/ АПВ ЛЭП: Неуспешное АПВл-1
3352.6681.308
3352.6681.306
3352.6681.302
3352.6681.310
3372.6621.302
3471.6551.304
4031.7541.301
3012.6691.305
3012.6691.303
3012.6691.501
3012.6691.307
3372.6621.302
3012.6691.312
3471.6551.304
3012.6691.306
3372.6621.302
3012.6691.311
3012.6691.305
3012.6691.301
3012.6691.302
АПВ СШ 6881
КСН В2/ КСН: УС
КСН В2/ КСН: КС
КСН В2/ КСН: ОНЭ1 + ННЛ
КСН В2/ КСН: Разр. АПВш
КСВ В2/ РФ: Сигнал несоотв.
АПВ В2/ АПВ СШ: Вывод
ФПВ В2/ ФПВ: В включен
ЛО В2/ ЛО В: Запрет АПВ
АПВ В2/ АПВ СШ: Нет усл. вкл.
ЛО/ ЛО: Ср. защит
КСВ В2/ РФ: Сигнал несоотв.
АПВ В2/ АПВ СШ: Гот. АПВш
ФПВ В2/ ФПВ: В включен
АПВ В2/ АПВ СШ: Включить
КСВ В2/ РФ: Сигнал несоотв.
Тожид усл. вкл. В2
Тср АПВш В2
Тимп АПВш В2
АПВ В2/ АПВ СШ: Нет усл. вкл.
АПВ В2/ АПВ СШ: Выведено
АПВ В2/ АПВ СШ: Включить
АПВ В2/ АПВ СШ: Гот. АПВш
АПВ В2/ АПВ СШ: П. АПВш
АПВ В2/ АПВ СШ: КЗ отключено
АПВ В2/ АПВ СШ: В2 включен от АПВш
АПВ В2/ АПВ СШ: Успешное АПВш
АПВ В2/ АПВ СШ: Неуспешное АПВш
3352.6681.308
3352.6681.306
3352.6681.304
3352.6681.311
3372.6621.302
3471.6551.304
4031.7541.301
3012.6881.301
4011.7511.301
3372.6621.302
3012.6881.303
3471.6551.304
3012.6881.302
3372.6621.302
3012.6881.301
3011.6881.309
3012.6881.302
3012.6881.303
3012.6881.304
3012.6881.305
3012.6881.306
3012.6881.307
3012.6881.308