



УВ В1 (Управление выключателем В1) 3391

УВ 6651

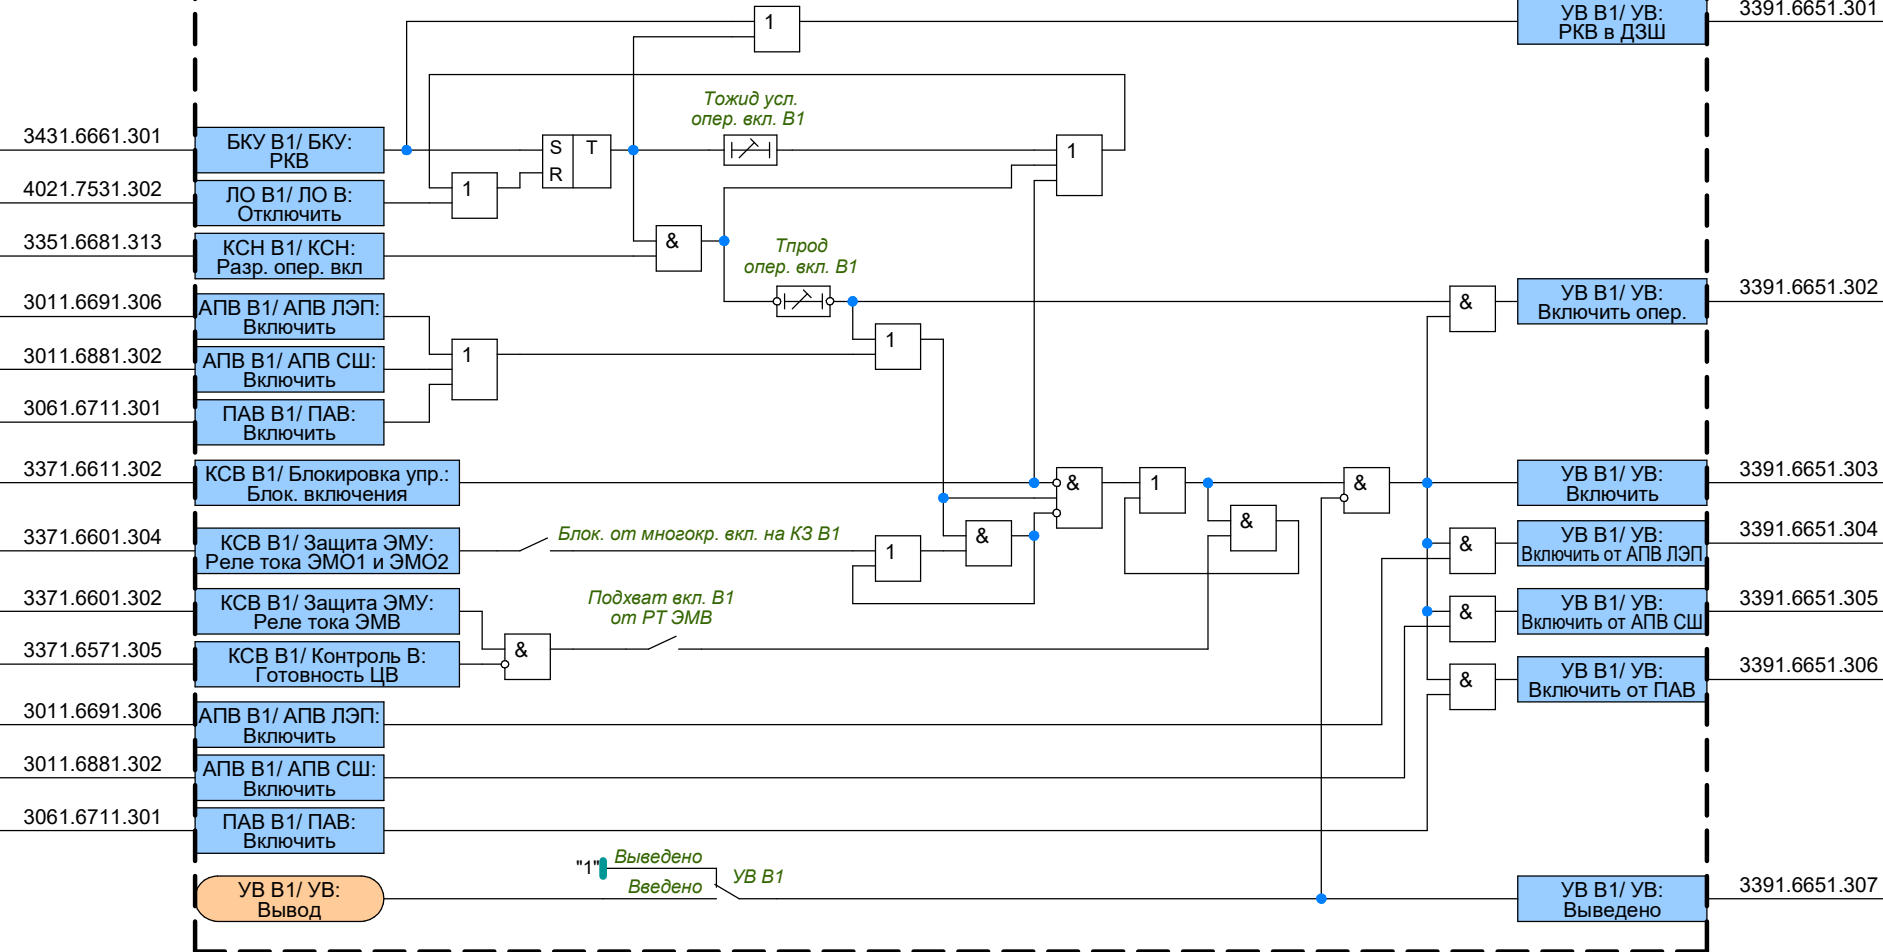


ЛО В1 4021

ЛО В 7531

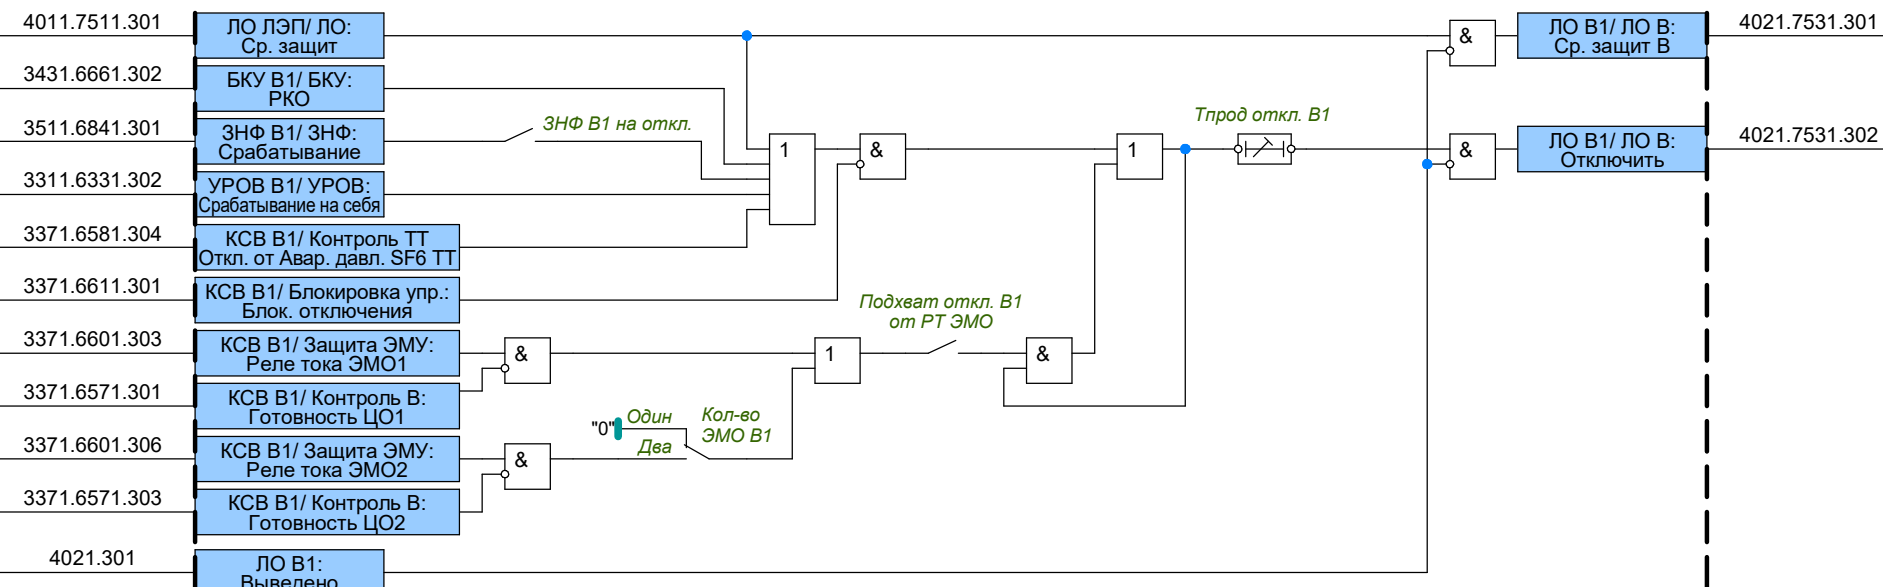


Запрет АПВ В 7541

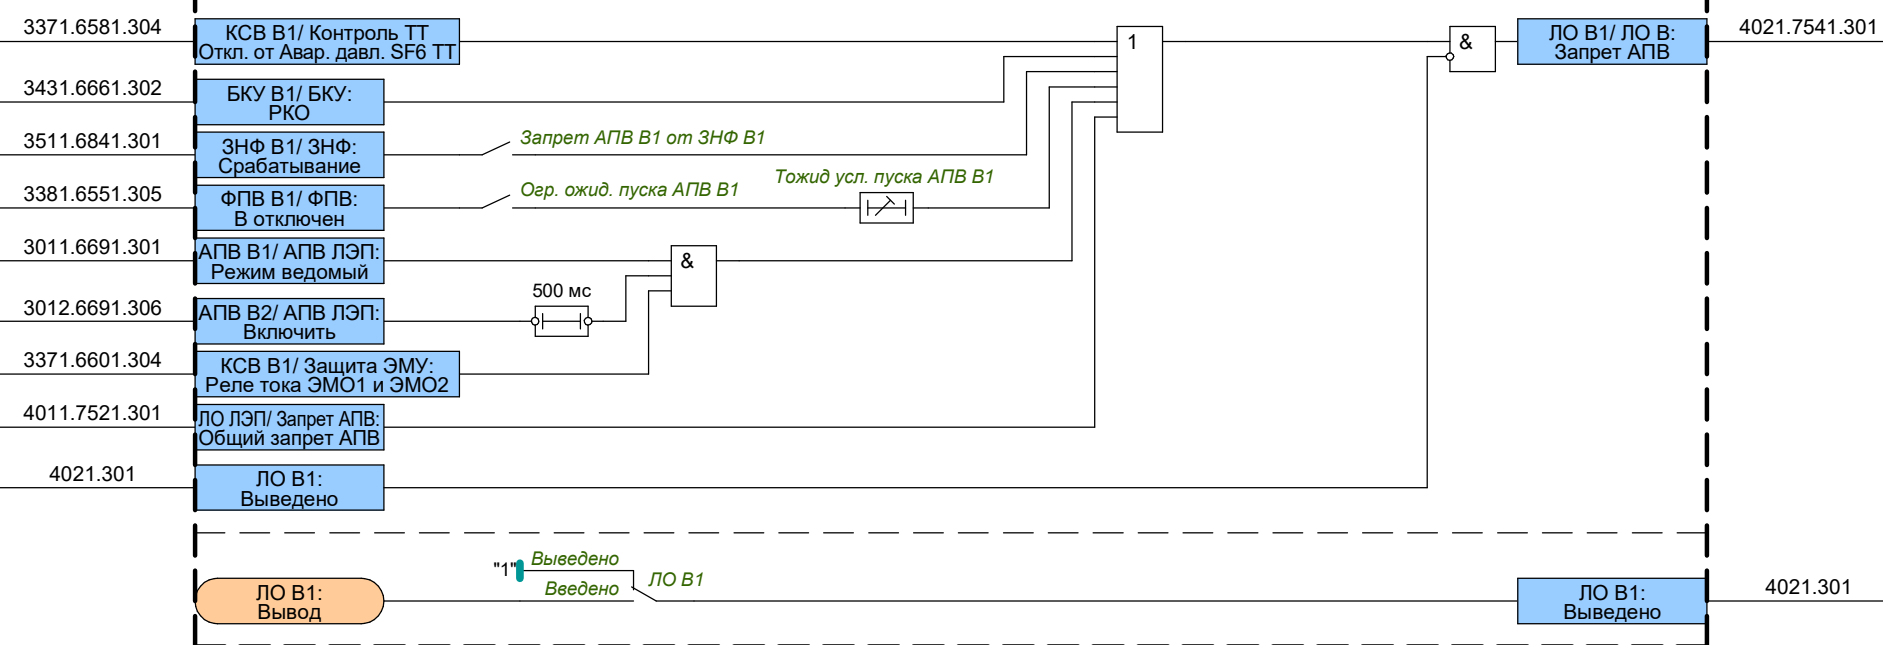


УВ В2 (Управление выключателем В2) 3392

УВ 6651

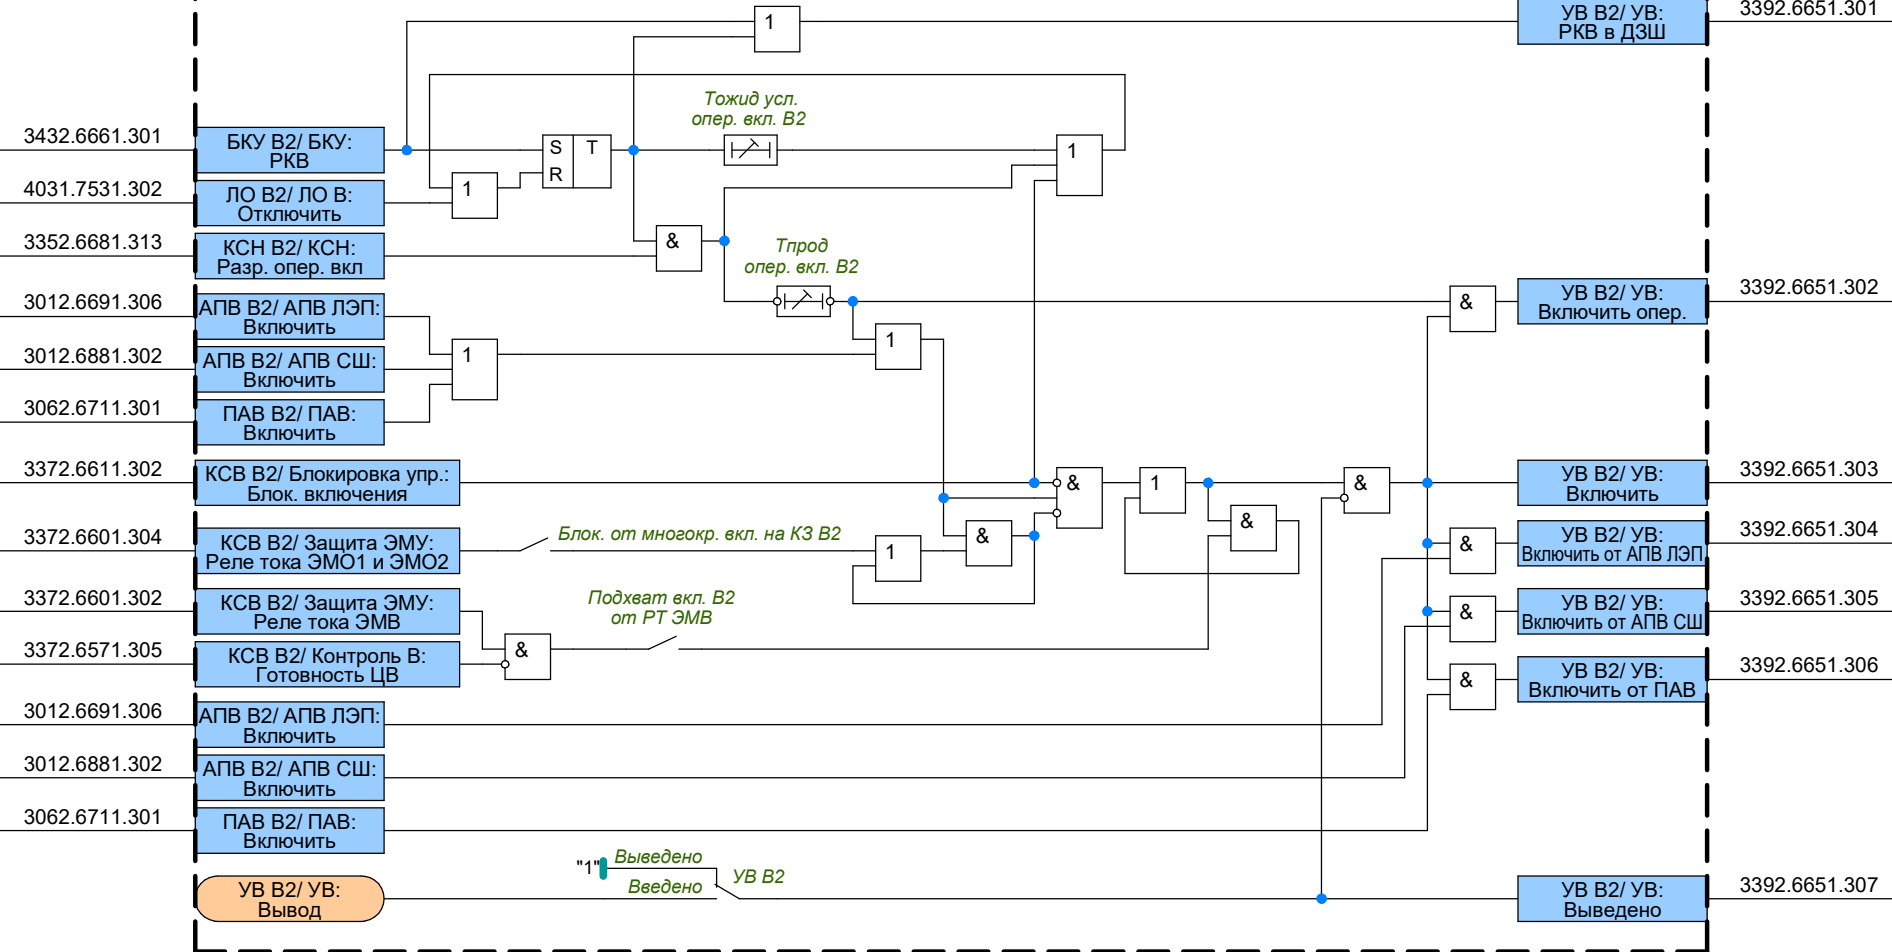

ЛО В2 4031

ЛО В 7531

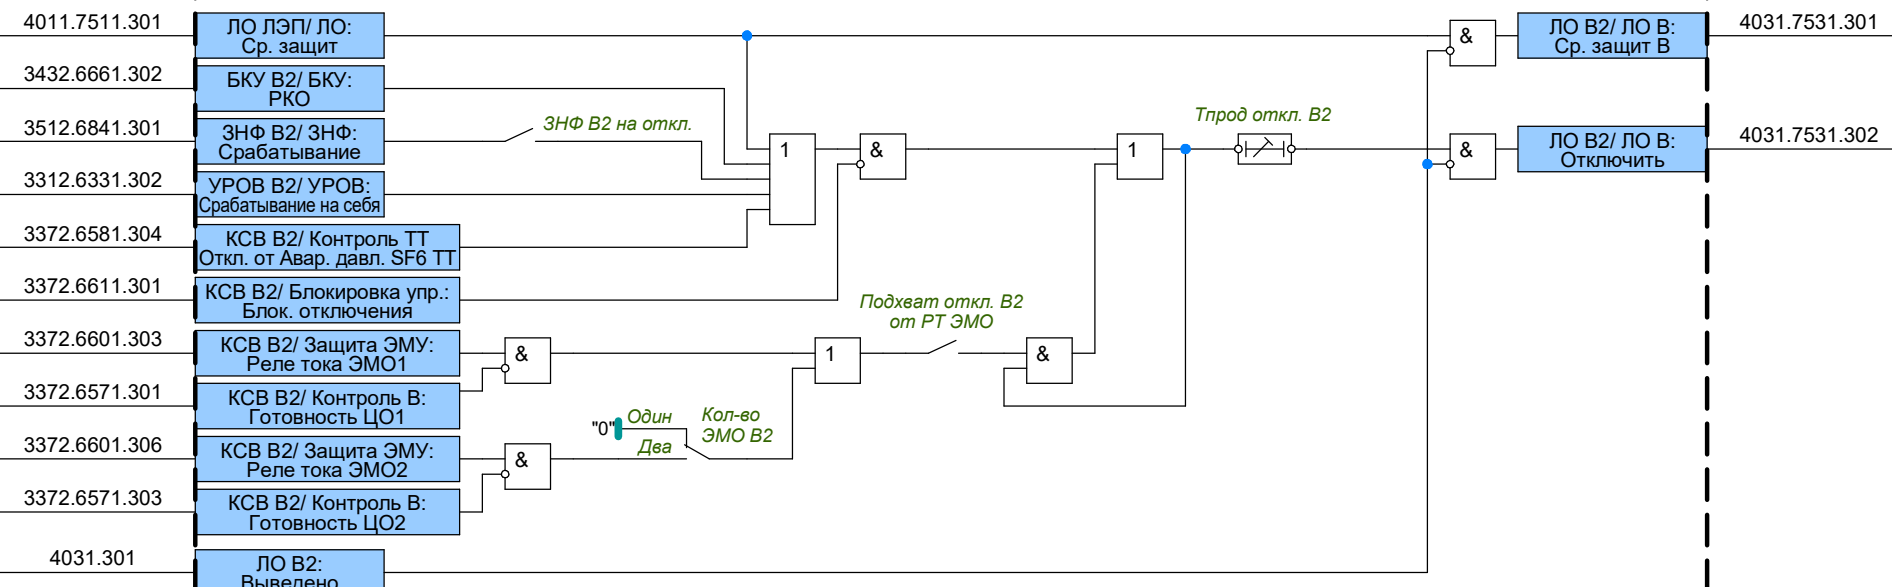

Запрет АПВ В 7541

