

M179 (7I+9U)

ЦОС.02		
XA1:1	Ia B1*	Iад
XA1:2	Ia B1	Iат
XA1:3	Ib B1*	Iiad]
XA1:4	Ib B1	Iад быстр
XA1:5	Ic B1*	Iат быстр
XA1:6	Ic B1	Ibd
XA1:7	Ia B2*	Ibt
XA1:8	Ia B2	Ibd]
XA1:9	Ib B2*	Ibd быстр
XA1:10	Ib B2	Ibt быстр
XA1:11	Ic B2*	Icd
XA1:12	Ic B2	Ict
XA1:13	3I0 пар. ЛЭП*	Icd]
XA1:14	3I0 пар. ЛЭП	Icd быстр
XA1:15	Ua*	Ict быстр
XA1:16	Ua	Ia B1
XA1:17	Ub*	Ib B1
XA1:18	Ub	Ic B1
XA1:19	Uc*	Ia B2
XA1:20	Uc	Ib B2
XA1:21	Уни(Унф)*	Ic B2
XA1:22	Уни(Унф)	Ia
XA1:23	Уик(Уфк)*	Ib
XA1:24	Уик(Уфк)	Ic
XA1:25	Уиф(Унк)*	Iab
XA1:26	Уиф(Унк)	Ibc
XA1:27	Уотб ЛЭП*	Ica
XA1:28	Уотб ЛЭП	I1
XA1:29	Уотб Э1*	I2
XA1:30	Уотб Э1	3I0
XA1:31	Уотб Э2*	I2/I1
XA1:32	Уотб Э2	3I0_2r / 3I0_1r
		dI1
		dI2
		Ua
		Ub
		Uc
		U1
		U2
		3U0 звезда
		3U0 треуг.
		Uлэл
		Uз1
		Uз2
		Уни
		Уиф
		Уфк
		Увнн
		Увнн ф.А
		Увнн ф.В
		Увнн ф.С
		dU1
		Za
		Zb
		Zc
		Zab
		Zbc
		Zca

Входы ФСУ	
Сброс сигнализации	501
Осн. защита выведена	502
Внеш. УРОВ от РЗА Э1	503
Внеш. УРОВ от РЗА Э2	504
Внеш. УРОВ от РЗА ЛЭП	505
Внеш. УРОВ от РЗА ОВ	506
Местное управление	507
Общая логика: Цели тока В1	90.501
Общая логика: Цели тока В2(ОВ)	90.502
Общая логика: Цели напр. звезды ЛВ	90.503
Общая логика: Цели напр. звезды ОВ	90.504
Общая логика: Цели напр. треуг. ЛВ	90.505
Общая логика: Цели напр. треуг. ОВ	90.506
Общая логика: Цели тока 3I0 пар. ЛЭП	90.507
Общая логика: Цели отб. напр. ЛЭП	90.508
Общая логика: Цели отб. напр. Э1	90.509
Общая логика: Цели отб. напр. Э2	90.510
Общая логика: Цели отключения В1	90.511
Общая логика: Цели отключения В2	90.512
Общая логика: Цели пуска УРОВ В1	90.513
Общая логика: Цели пуска УРОВ В2	90.514
Общая логика: Цели выходные	90.515
Общая логика: Цели управления В	90.516
Общая логика: Цели откл. от УРОВ	90.517
Общая логика: Цели ТО и ТУ	90.518
Общая логика: Цели разр. ПУ пар. ЛЭП	90.519
Общая логика: Цели включения в ДЗШ	90.520
Общая логика: Дверь шкафа открыта	90.521
Сигнализация: Внеш. неистр.	91.501
ТЗНП/ ПУ ТЗНП-ШСВ/СВ выведен	0111.0701.501
ТЗНП/ ПУ ТЗНП-ПУ от пар. ЛЭП	0111.0701.502
ТЗО: Б/К ЛР откл	0181.501
ТЗО: Б/К ЛР ф.А откл	0181.502
ТЗО: Б/К ЛР ф.В откл	0181.503
ТЗО: Б/К ЛР ф.С откл	0181.504
ТЗО: Опер. ввод	0181.505
ЗНР/ ЗНР-Ср. ЗНФ В1 в ЗНР	0421.1011.501
ЗНР/ ЗНР-Ср. ЗНФ В2 в ЗНР	0421.1011.502
ЗНР/ ЗНР-ВЗ отключен в ЗНР	0421.1011.503
ЗНФ В1/ ЗНФ: Неперекл. фаз	3511.6841.501
ЗНФ В2/ ЗНФ: Неперекл. фаз	3512.6841.502
БНН/ БНН: Автомат ТН	1461.4511.501
БНН/ БНН: Фикс. неистр. ЦН	1461.4511.502
АМТЗ: Опер. ввод	0471.501
АУ/ АУ: Внеш. Умин ЛЭП	1311.4011.501
ЛС/ Тоткл: Прием Тоткл КС1	1711.5011.501
ЛС/ Тоткл: Прием Тоткл КС2	1711.5011.502
ЛС/ Тоткл: Внеш. пуск Тоткл	1711.5011.503
ЛС/ ТУ ОТФ: Прием ТУ ОТФ КС1	1711.5021.501
ЛС/ ТУ ОТФ: Прием ТУ ОТФ КС2	1711.5021.502
ЛС/ ТУ ДЗ: Прием ТУ ДЗ КС1	1711.5031.501
ЛС/ ТУ ДЗ: Прием ТУ ДЗ КС2	1711.5031.502
ЛС/ ТУ ТЗНП: Прием ТУ ТЗНП КС1	1711.5041.501
ЛС/ ТУ ТЗНП: Прием ТУ ТЗНП КС2	1711.5041.502

Входы ФСУ	
УРОВ В1/ УРОВ: Пуск УРОВ №1	3311.6631.501
УРОВ В1/ УРОВ: Пуск УРОВ №2	3311.6631.502
УРОВ В1/ УРОВ: Пуск УРОВ НН	3311.6631.503
УРОВ В2/ УРОВ: Пуск УРОВ №1	3312.6631.501
УРОВ В2/ УРОВ: Пуск УРОВ №2	3312.6631.502
УРОВ В2/ УРОВ: Пуск УРОВ НН	3312.6631.503
КСН В1/ КСН: Внеш. сигнал КС(УС)	3351.6681.501
АПВ В1/ АПВ ЛЭП: Сброс АПВл от ДЗШ	3011.6691.501
КСН В2/ КСН: Внеш. сигнал КС(УС)	3352.6681.501
АПВ В2/ АПВ ЛЭП: Сброс АПВл от ДЗШ	3012.6691.501
КСВ В1/ Контроль В: Контр. ЭМО1	3371.6571.501
КСВ В1/ Контроль В: Контр. ЭМО1 ф.А	3371.6571.502
КСВ В1/ Контроль В: Контр. ЭМО1 ф.В	3371.6571.503
КСВ В1/ Контроль В: Контр. ЭМО1 ф.С	3371.6571.504
КСВ В1/ Контроль В: Контр. ЭМО2	3371.6571.505
КСВ В1/ Контроль В: Контр. ЭМО2 ф.А	3371.6571.506
КСВ В1/ Контроль В: Контр. ЭМО2 ф.В	3371.6571.507
КСВ В1/ Контроль В: Контр. ЭМО2 ф.С	3371.6571.508
КСВ В1/ Контроль В: Контр. ЭМВ	3371.6571.509
КСВ В1/ Контроль В: Контр. ЭМВ ф.А	3371.6571.510
КСВ В1/ Контроль В: Контр. ЭМВ ф.В	3371.6571.511
КСВ В1/ Контроль В: Контр. ЭМВ ф.С	3371.6571.512
КСВ В1/ Контроль В: Низк. давл. SF6	3371.6571.513
КСВ В1/ Контроль В: Низк. давл. SF6 ф.А	3371.6571.514
КСВ В1/ Контроль В: Низк. давл. SF6 ф.В	3371.6571.515
КСВ В1/ Контроль В: Низк. давл. SF6 ф.С	3371.6571.516
КСВ В1/ Контроль В: Авар. давл. SF6	3371.6571.517
КСВ В1/ Контроль В: Авар. давл. SF6 ф.А	3371.6571.518
КСВ В1/ Контроль В: Авар. давл. SF6 ф.В	3371.6571.519
КСВ В1/ Контроль В: Авар. давл. SF6 ф.С	3371.6571.520
КСВ В1/ Контроль В: Пруж. не заведены	3371.6571.521
КСВ В1/ Контроль В: Пруж. не заведены ф.А	3371.6571.522
КСВ В1/ Контроль В: Пруж. не заведены ф.В	3371.6571.523
КСВ В1/ Контроль В: Пруж. не заведены ф.С	3371.6571.524
КСВ В1/ Контроль В: Неистр. обогр.	3371.6571.525
КСВ В1/ Контроль В: Автомат ШП	3371.6571.526
КСВ В1/ Контроль В: Контр. ОТ ЭМВ/ЭМО1	3371.6571.527
КСВ В1/ Контроль В: Контр. ОТ ЭМО2	3371.6571.528
КСВ В1/ Контроль В: Контр. ОТ сигн.	3371.6571.529
КСВ В1/ Блокировка упр.: Внеш. блок. упр.	3371.6611.501
КСВ В1/ Блокировка упр.: Внеш. блок. вкл.	3371.6611.502
КСВ В1/ Контроль ТТ: Низк. давл. SF6 ТТ	3371.6581.501
КСВ В1/ Контроль ТТ: Низк. давл. SF6 ТТ ф.А	3371.6581.502
КСВ В1/ Контроль ТТ: Низк. давл. SF6 ТТ ф.В	3371.6581.503
КСВ В1/ Контроль ТТ: Низк. давл. SF6 ТТ ф.С	3371.6581.504
КСВ В1/ Контроль ТТ: Авар. давл. SF6 ТТ	3371.6581.505
КСВ В1/ Контроль ТТ: Авар. давл. SF6 ТТ ф.А	3371.6581.506
КСВ В1/ Контроль ТТ: Авар. давл. SF6 ТТ ф.В	3371.6581.507
КСВ В1/ Контроль ТТ: Авар. давл. SF6 ТТ ф.С	3371.6581.508
КСВ В1/ Контроль ТТ: Неистр. обогр. ТТ	3371.6581.509
КСВ В1/ Защита ЭМУ: Работа ЭМВ	3371.6601.501
КСВ В1/ Защита ЭМУ: Работа ЭМВ ф.А	3371.6601.502
КСВ В1/ Защита ЭМУ: Работа ЭМВ ф.В	3371.6601.503
КСВ В1/ Защита ЭМУ: Работа ЭМВ ф.С	3371.6601.504
КСВ В1/ Защита ЭМУ: Работа ЭМО1	3371.6601.505
КСВ В1/ Защита ЭМУ: Работа ЭМО1 ф.А	3371.6601.506
КСВ В1/ Защита ЭМУ: Работа ЭМО1 ф.В	3371.6601.507
КСВ В1/ Защита ЭМУ: Работа ЭМО1 ф.С	3371.6601.508

Входы ФСУ	
КСВ В1/ Контроль В: Работа ЭМО2	3371.6601.509
КСВ В1/ Контроль В: Работа ЭМО2 ф.А	3371.6601.510
КСВ В1/ Контроль В: Работа ЭМО2 ф.В	3371.6601.511
КСВ В1/ Контроль В: Работа ЭМО2 ф.С	3371.6601.512
БКУ В1/ БКУ: Опер. вкл.	3431.6661.501
БКУ В1/ БКУ: Опер. откл.	3431.6661.502
КСВ В2/ Контроль В: Контр. ЭМО1	3372.6571.501
КСВ В2/ Контроль В: Контр. ЭМО1 ф.А	3372.6571.502
КСВ В2/ Контроль В: Контр. ЭМО1 ф.В	3372.6571.503
КСВ В2/ Контроль В: Контр. ЭМО1 ф.С	3372.6571.504
КСВ В2/ Контроль В: Контр. ЭМО2	3372.6571.505
КСВ В2/ Контроль В: Контр. ЭМО2 ф.А	3372.6571.506
КСВ В2/ Контроль В: Контр. ЭМО2 ф.В	3372.6571.507
КСВ В2/ Контроль В: Контр. ЭМО2 ф.С	3372.6571.508
КСВ В2/ Контроль В: Контр. ЭМВ	3372.6571.509
КСВ В2/ Контроль В: Контр. ЭМВ ф.А	3372.6571.510
КСВ В2/ Контроль В: Контр. ЭМВ ф.В	3372.6571.511
КСВ В2/ Контроль В: Контр. ЭМВ ф.С	3372.6571.512
КСВ В2/ Контроль В: Низк. давл. SF6	3372.6571.513
КСВ В2/ Контроль В: Низк. давл. SF6 ф.А	3372.6571.514
КСВ В2/ Контроль В: Низк. давл. SF6 ф.В	3372.6571.515
КСВ В2/ Контроль В: Низк. давл. SF6 ф.С	3372.6571.516
КСВ В2/ Контроль В: Авар. давл. SF6	3372.6571.517
КСВ В2/ Контроль В: Авар. давл. SF6 ф.А	3372.6571.518
КСВ В2/ Контроль В: Авар. давл. SF6 ф.В	3372.6571.519
КСВ В2/ Контроль В: Авар. давл. SF6 ф.С	3372.6571.520
КСВ В2/ Контроль В: Пруж. не заведены	3372.6571.521
КСВ В2/ Контроль В: Пруж. не заведены ф.А	3372.6571.522
КСВ В2/ Контроль В: Пруж. не заведены ф.В	3372.6571.523
КСВ В2/ Контроль В: Пруж. не заведены ф.С	3372.6571.524
КСВ В2/ Контроль В: Неистр. обогр.	3372.6571.525
КСВ В2/ Контроль В: Автомат ШП	3372.6571.526
КСВ В2/ Контроль В: Контр. ОТ ЭМВ/ЭМО1	3372.6571.527
КСВ В2/ Контроль В: Контр. ОТ ЭМО2	3372.6571.528
КСВ В2/ Контроль В: Контр. ОТ сигн.	3372.6571.529
КСВ В2/ Блокировка упр.: Внеш. блок. упр.	3372.6611.501
КСВ В2/ Блокировка упр.: Внеш. блок. вкл.	3372.6611.502
КСВ В2/ Контроль ТТ: Низк. давл. SF6 ТТ	3372.6581.501
КСВ В2/ Контроль ТТ: Низк. давл. SF6 ТТ ф.А	3372.6581.502
КСВ В2/ Контроль ТТ: Низк. давл. SF6 ТТ ф.В	3372.6581.503
КСВ В2/ Контроль ТТ: Низк. давл. SF6 ТТ ф.С	3372.6581.504
КСВ В2/ Контроль ТТ: Авар. давл. SF6 ТТ	3372.6581.505
КСВ В2/ Контроль ТТ: Авар. давл. SF6 ТТ ф.А	3372.6581.506
КСВ В2/ Контроль ТТ: Авар. давл. SF6 ТТ ф.В	3372.6581.507
КСВ В2/ Контроль ТТ: Авар. давл. SF6 ТТ ф.С	3372.6581.508
КСВ В2/ Контроль ТТ: Неистр. обогр. ТТ	3372.6581.509
КСВ В2/ Защита ЭМУ: Работа ЭМВ	3372.6601.501
КСВ В2/ Защита ЭМУ: Работа ЭМВ ф.А	3372.6601.502
КСВ В2/ Защита ЭМУ: Работа ЭМВ ф.В	3372.6601.503
КСВ В2/ Защита ЭМУ: Работа ЭМВ ф.С	3372.6601.504
КСВ В2/ Защита ЭМУ: Работа ЭМО1	3372.6601.505
КСВ В2/ Защита ЭМУ: Работа ЭМО1 ф.А	3372.6601.506
КСВ В2/ Защита ЭМУ: Работа ЭМО1 ф.В	3372.6601.507
КСВ В2/ Защита ЭМУ: Работа ЭМО1 ф.С	3372.6601.508
КСВ В2/ Контроль В: Работа ЭМО2	3372.6601.509
КСВ В2/ Контроль В: Работа ЭМО2 ф.А	3372.6601.510
КСВ В2/ Контроль В: Работа ЭМО2 ф.В	3372.6601.511
КСВ В2/ Контроль В: Работа ЭМО2 ф.С	3372.6601.512


Входы ФСУ	
БКУ В2/ БКУ: Опер. вкл.	3432.6661.501
БКУ В2/ БКУ: Опер. откл.	3432.6661.502
ЛО: Ср. осн. защиты	4011.501
ЛО/ ЛО: Ср. внеш. защит	4011.7511.501
ЛО/ ЛО: П. внеш. защит	4011.7511.502
ЛО/ Запрет АПВ: Внеш. запрет АПВ	4011.7521.501
Коммутация В1/ Коммутация: Коммутация внеш.	1821.5301.501
Коммутация В2/ Коммутация: Коммутация внеш.	1822.5301.501
ФПВ В1/ ФПВ: Б/К В вкл	3381.6551.501
ФПВ В1/ ФПВ: Б/К В вкл ф.А	3381.6551.502
ФПВ В1/ ФПВ: Б/К В вкл ф.В	3381.6551.503
ФПВ В1/ ФПВ: Б/К В вкл ф.С	3381.6551.504
ФПВ В1/ ФПВ: Б/К В вкл ф.С	3381.6551.505
ФПВ В1/ ФПВ: Б/К В откл	3381.6551.506
ФПВ В1/ ФПВ: Б/К В откл ф.А	3381.6551.507
ФПВ В1/ ФПВ: Б/К В откл ф.В	3381.6551.508
ФПВ В1/ ФПВ: Б/К В откл ф.С	3381.6551.509
ФПВ В1/ Р1: Б/К Р вкл	3381.6531.501
ФПВ В1/ Р1: Б/К Р вкл ф.А	3381.6531.502
ФПВ В1/ Р1: Б/К Р вкл ф.В	3381.6531.503
ФПВ В1/ Р1: Б/К Р вкл ф.С	3381.6531.504
ФПВ В1/ Р1: Б/К Р откл	3381.6531.505
ФПВ В1/ Р1: Б/К Р откл ф.А	3381.6531.506
ФПВ В1/ Р1: Б/К Р откл ф.В	3381.6531.507
ФПВ В1/ Р1: Б/К Р откл ф.С	3381.6531.508
ФПВ В1/ Р2: Б/К Р вкл	3381.6532.501
ФПВ В1/ Р2: Б/К Р вкл ф.А	3381.6532.502
ФПВ В1/ Р2: Б/К Р вкл ф.В	3381.6532.503
ФПВ В1/ Р2: Б/К Р вкл ф.С	3381.6532.504
ФПВ В1/ Р2: Б/К Р откл	3381.6532.505
ФПВ В1/ Р2: Б/К Р откл ф.А	3381.6532.506
ФПВ В1/ Р2: Б/К Р откл ф.В	3381.6532.507
ФПВ В1/ Р2: Б/К Р откл ф.С	3381.6532.508
ФПВ В1/ Р3: Б/К Р вкл	3381.6533.501
ФПВ В1/ Р3: Б/К Р вкл ф.А	3381.6533.502
ФПВ В1/ Р3: Б/К Р вкл ф.В	3381.6533.503
ФПВ В1/ Р3: Б/К Р вкл ф.С	3381.6533.504
ФПВ В1/ Р3: Б/К Р откл	3381.6533.505
ФПВ В1/ Р3: Б/К Р откл ф.А	3381.6533.506
ФПВ В1/ Р3: Б/К Р откл ф.В	3381.6533.507
ФПВ В1/ Р3: Б/К Р откл ф.С	3381.6533.508

Входы ФСУ	
ФПВ В2/ ФПВ: Б/К В вкл	3471.6551.501
ФПВ В2/ ФПВ: Б/К В вкл ф.А	3471.6551.502
ФПВ В2/ ФПВ: Б/К В вкл ф.В	3471.6551.503
ФПВ В2/ ФПВ: Б/К В вкл ф.С	3471.6551.504
ФПВ В2/ ФПВ: Б/К В откл	3471.6551.505
ФПВ В2/ ФПВ: Б/К В откл ф.А	3471.6551.506
ФПВ В2/ ФПВ: Б/К В откл ф.В	3471.6551.507
ФПВ В2/ ФПВ: Б/К В откл ф.С	3471.6551.508
ФПВ В2/ ФПВ: Ремонт	3471.6551.509
ФПВ В2/ Р1: Б/К Р вкл	3471.6531.501
ФПВ В2/ Р1: Б/К Р вкл ф.А	3471.6531.502
ФПВ В2/ Р1: Б/К Р вкл ф.В	3471.6531.503
ФПВ В2/ Р1: Б/К Р вкл ф.С	3471.6531.504
ФПВ В2/ Р1: Б/К Р откл	3471.6531.505
ФПВ В2/ Р1: Б/К Р откл ф.А	3471.6531.506
ФПВ В2/ Р1: Б/К Р откл ф.В	3471.6531.507
ФПВ В2/ Р1: Б/К Р откл ф.С	3471.6531.508
ФПВ В2/ Р2: Б/К Р вкл	3471.6532.501
ФПВ В2/ Р2: Б/К Р вкл ф.А	3471.6532.502
ФПВ В2/ Р2: Б/К Р вкл ф.В	3471.6532.503
ФПВ В2/ Р2: Б/К Р вкл ф.С	3471.6532.504
ФПВ В2/ Р2: Б/К Р откл	3471.6532.505
ФПВ В2/ Р2: Б/К Р откл ф.А	3471.6532.506
ФПВ В2/ Р2: Б/К Р откл ф.В	3471.6532.507
ФПВ В2/ Р2: Б/К Р откл ф.С	3471.6532.508
ФПВ В2/ Р3: Б/К Р вкл	3471.6533.501
ФПВ В2/ Р3: Б/К Р вкл ф.А	3471.6533.502
ФПВ В2/ Р3: Б/К Р вкл ф.В	3471.6533.503
ФПВ В2/ Р3: Б/К Р вкл ф.С	3471.6533.504
ФПВ В2/ Р3: Б/К Р откл	3471.6533.505
ФПВ В2/ Р3: Б/К Р откл ф.А	3471.6533.506
ФПВ В2/ Р3: Б/К Р откл ф.В	3471.6533.507
ФПВ В2/ Р3: Б/К Р откл ф.С	3471.6533.508
ФПВ В2/ Р4: Б/К Р вкл	3471.6534.501
ФПВ В2/ Р4: Б/К Р вкл ф.А	3471.6534.502
ФПВ В2/ Р4: Б/К Р вкл ф.В	3471.6534.503
ФПВ В2/ Р4: Б/К Р вкл ф.С	3471.6534.504
ФПВ В2/ Р4: Б/К Р откл	3471.6534.505
ФПВ В2/ Р4: Б/К Р откл ф.А	3471.6534.506
ФПВ В2/ Р4: Б/К Р откл ф.В	3471.6534.507
ФПВ В2/ Р4: Б/К Р откл ф.С	3471.6534.508


Входы ФСУ	
ФПВ В3/ ФПВ: Б/К В вкл	3461.6551.501
ФПВ В3/ ФПВ: Б/К В вкл ф.А	3461.6551.502
ФПВ В3/ ФПВ: Б/К В вкл ф.В	3461.6551.503
ФПВ В3/ ФПВ: Б/К В вкл ф.С	3461.6551.504
ФПВ В3/ ФПВ: Б/К В откл	3461.6551.505
ФПВ В3/ ФПВ: Б/К В откл ф.А	3461.6551.506
ФПВ В3/ ФПВ: Б/К В откл ф.В	3461.6551.507
ФПВ В3/ ФПВ: Б/К В откл ф.С	3461.6551.508
ФПВ В3/ ФПВ: Ремонт	3461.6551.509
ФПВ В3/ Р1: Б/К Р вкл	3461.6531.501
ФПВ В3/ Р1: Б/К Р вкл ф.А	3461.6531.502
ФПВ В3/ Р1: Б/К Р вкл ф.В	3461.6531.503
ФПВ В3/ Р1: Б/К Р вкл ф.С	3461.6531.504
ФПВ В3/ Р1: Б/К Р откл	3461.6531.505
ФПВ В3/ Р1: Б/К Р откл ф.А	3461.6531.506
ФПВ В3/ Р1: Б/К Р откл ф.В	3461.6531.507
ФПВ В3/ Р1: Б/К Р откл ф.С	3461.6531.508
ФПВ В3/ Р2: Б/К Р вкл	3461.6532.501
ФПВ В3/ Р2: Б/К Р вкл ф.А	3461.6532.502
ФПВ В3/ Р2: Б/К Р вкл ф.В	3461.6532.503
ФПВ В3/ Р2: Б/К Р вкл ф.С	3461.6532.504
ФПВ В3/ Р2: Б/К Р откл	3461.6532.505
ФПВ В3/ Р2: Б/К Р откл ф.А	3461.6532.506
ФПВ В3/ Р2: Б/К Р откл ф.В	3461.6532.507
ФПВ В3/ Р2: Б/К Р откл ф.С	3461.6532.508
ФПВ ШСВ/СВ/ ФПВ: Б/К В вкл	3462.6551.501
ФПВ ШСВ/СВ/ ФПВ: Б/К В вкл ф.А	3462.6551.502
ФПВ ШСВ/СВ/ ФПВ: Б/К В вкл ф.В	3462.6551.503
ФПВ ШСВ/СВ/ ФПВ: Б/К В вкл ф.С	3462.6551.504
ФПВ ШСВ/СВ/ ФПВ: Б/К В откл	3462.6551.505
ФПВ ШСВ/СВ/ ФПВ: Б/К В откл ф.А	3462.6551.506
ФПВ ШСВ/СВ/ ФПВ: Б/К В откл ф.В	3462.6551.507
ФПВ ШСВ/СВ/ ФПВ: Б/К В откл ф.С	3462.6551.508
ФПВ ШСВ/СВ/ ФПВ: Ремонт	3462.6551.509
ФПВ ШСВ/СВ/ Р1: Б/К Р вкл	3462.6531.501
ФПВ ШСВ/СВ/ Р1: Б/К Р вкл ф.А	3462.6531.502
ФПВ ШСВ/СВ/ Р1: Б/К Р вкл ф.В	3462.6531.503
ФПВ ШСВ/СВ/ Р1: Б/К Р вкл ф.С	3462.6531.504
ФПВ ШСВ/СВ/ Р1: Б/К Р откл	3462.6531.505
ФПВ ШСВ/СВ/ Р1: Б/К Р откл ф.А	3462.6531.506
ФПВ ШСВ/СВ/ Р1: Б/К Р откл ф.В	3462.6531.507
ФПВ ШСВ/СВ/ Р1: Б/К Р откл ф.С	3462.6531.508
ФПВ ШСВ/СВ/ Р2: Б/К Р вкл	3462.6532.501
ФПВ ШСВ/СВ/ Р2: Б/К Р вкл ф.А	3462.6532.502
ФПВ ШСВ/СВ/ Р2: Б/К Р вкл ф.В	3462.6532.503
ФПВ ШСВ/СВ/ Р2: Б/К Р вкл ф.С	3462.6532.504
ФПВ ШСВ/СВ/ Р2: Б/К Р откл	3462.6532.505
ФПВ ШСВ/СВ/ Р2: Б/К Р откл ф.А	3462.6532.506
ФПВ ШСВ/СВ/ Р2: Б/К Р откл ф.В	3462.6532.507
ФПВ ШСВ/СВ/ Р2: Б/К Р откл ф.С	3462.6532.508



Входы ФСУ	
ДЗЛ/ УКЕТ: Вывод от УТ1	0651.1671.501
ДЗЛ/ УКЕТ: Вывод от УТ2	0651.1671.502
ДЗЛ/ Контроль ЦКС: Блок. ДЗЛ от УТ1	0651.1681.501
ДЗЛ/ Контроль ЦКС: Блок. ДЗЛ от УТ2	0651.1681.502
ДЗЛ/ Контроль ЦКС: Неиспр. ЦКС1	0651.1681.503
ДЗЛ/ Контроль ЦКС: Неиспр. ЦКС2	0651.1681.504
ДЗЛ: ПРМ ДЗЛ ф.А по ЦКС1	0651.501
ДЗЛ: ПРМ ДЗЛ ф.А по ЦКС2	0651.502
ДЗЛ: ПРМ ДЗЛ ф.В по ЦКС1	0651.503
ДЗЛ: ПРМ ДЗЛ ф.В по ЦКС2	0651.504
ДЗЛ: ПРМ ДЗЛ ф.С по ЦКС1	0651.505
ДЗЛ: ПРМ ДЗЛ ф.С по ЦКС2	0651.506
ДЗЛ: Перевод на сигнал	0651.507
ДЗЛ: Режим тест.	0651.508

Общая логика 90

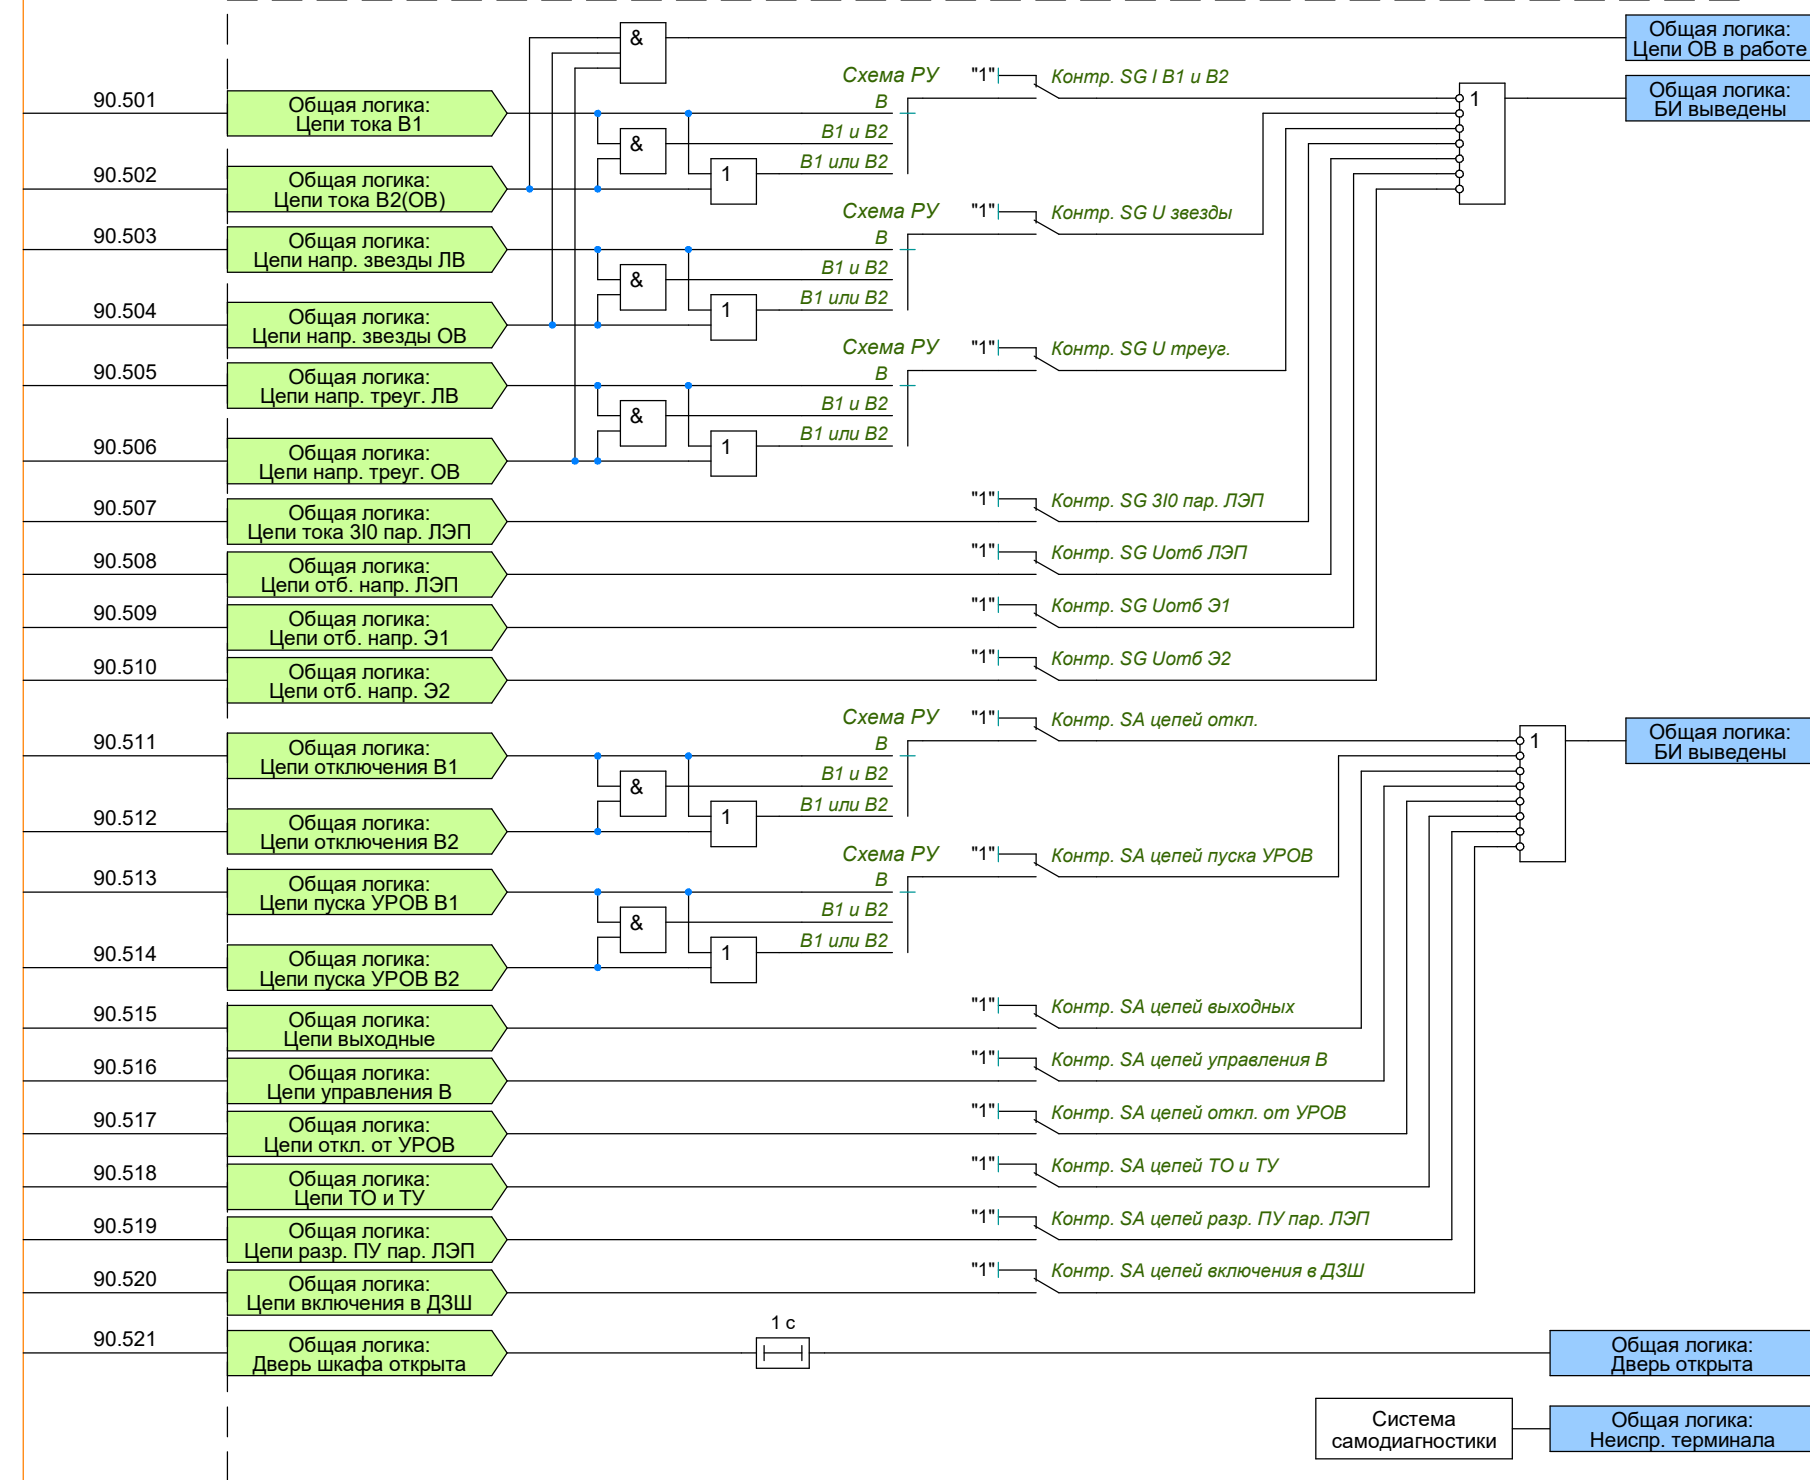


Сигнализация 91

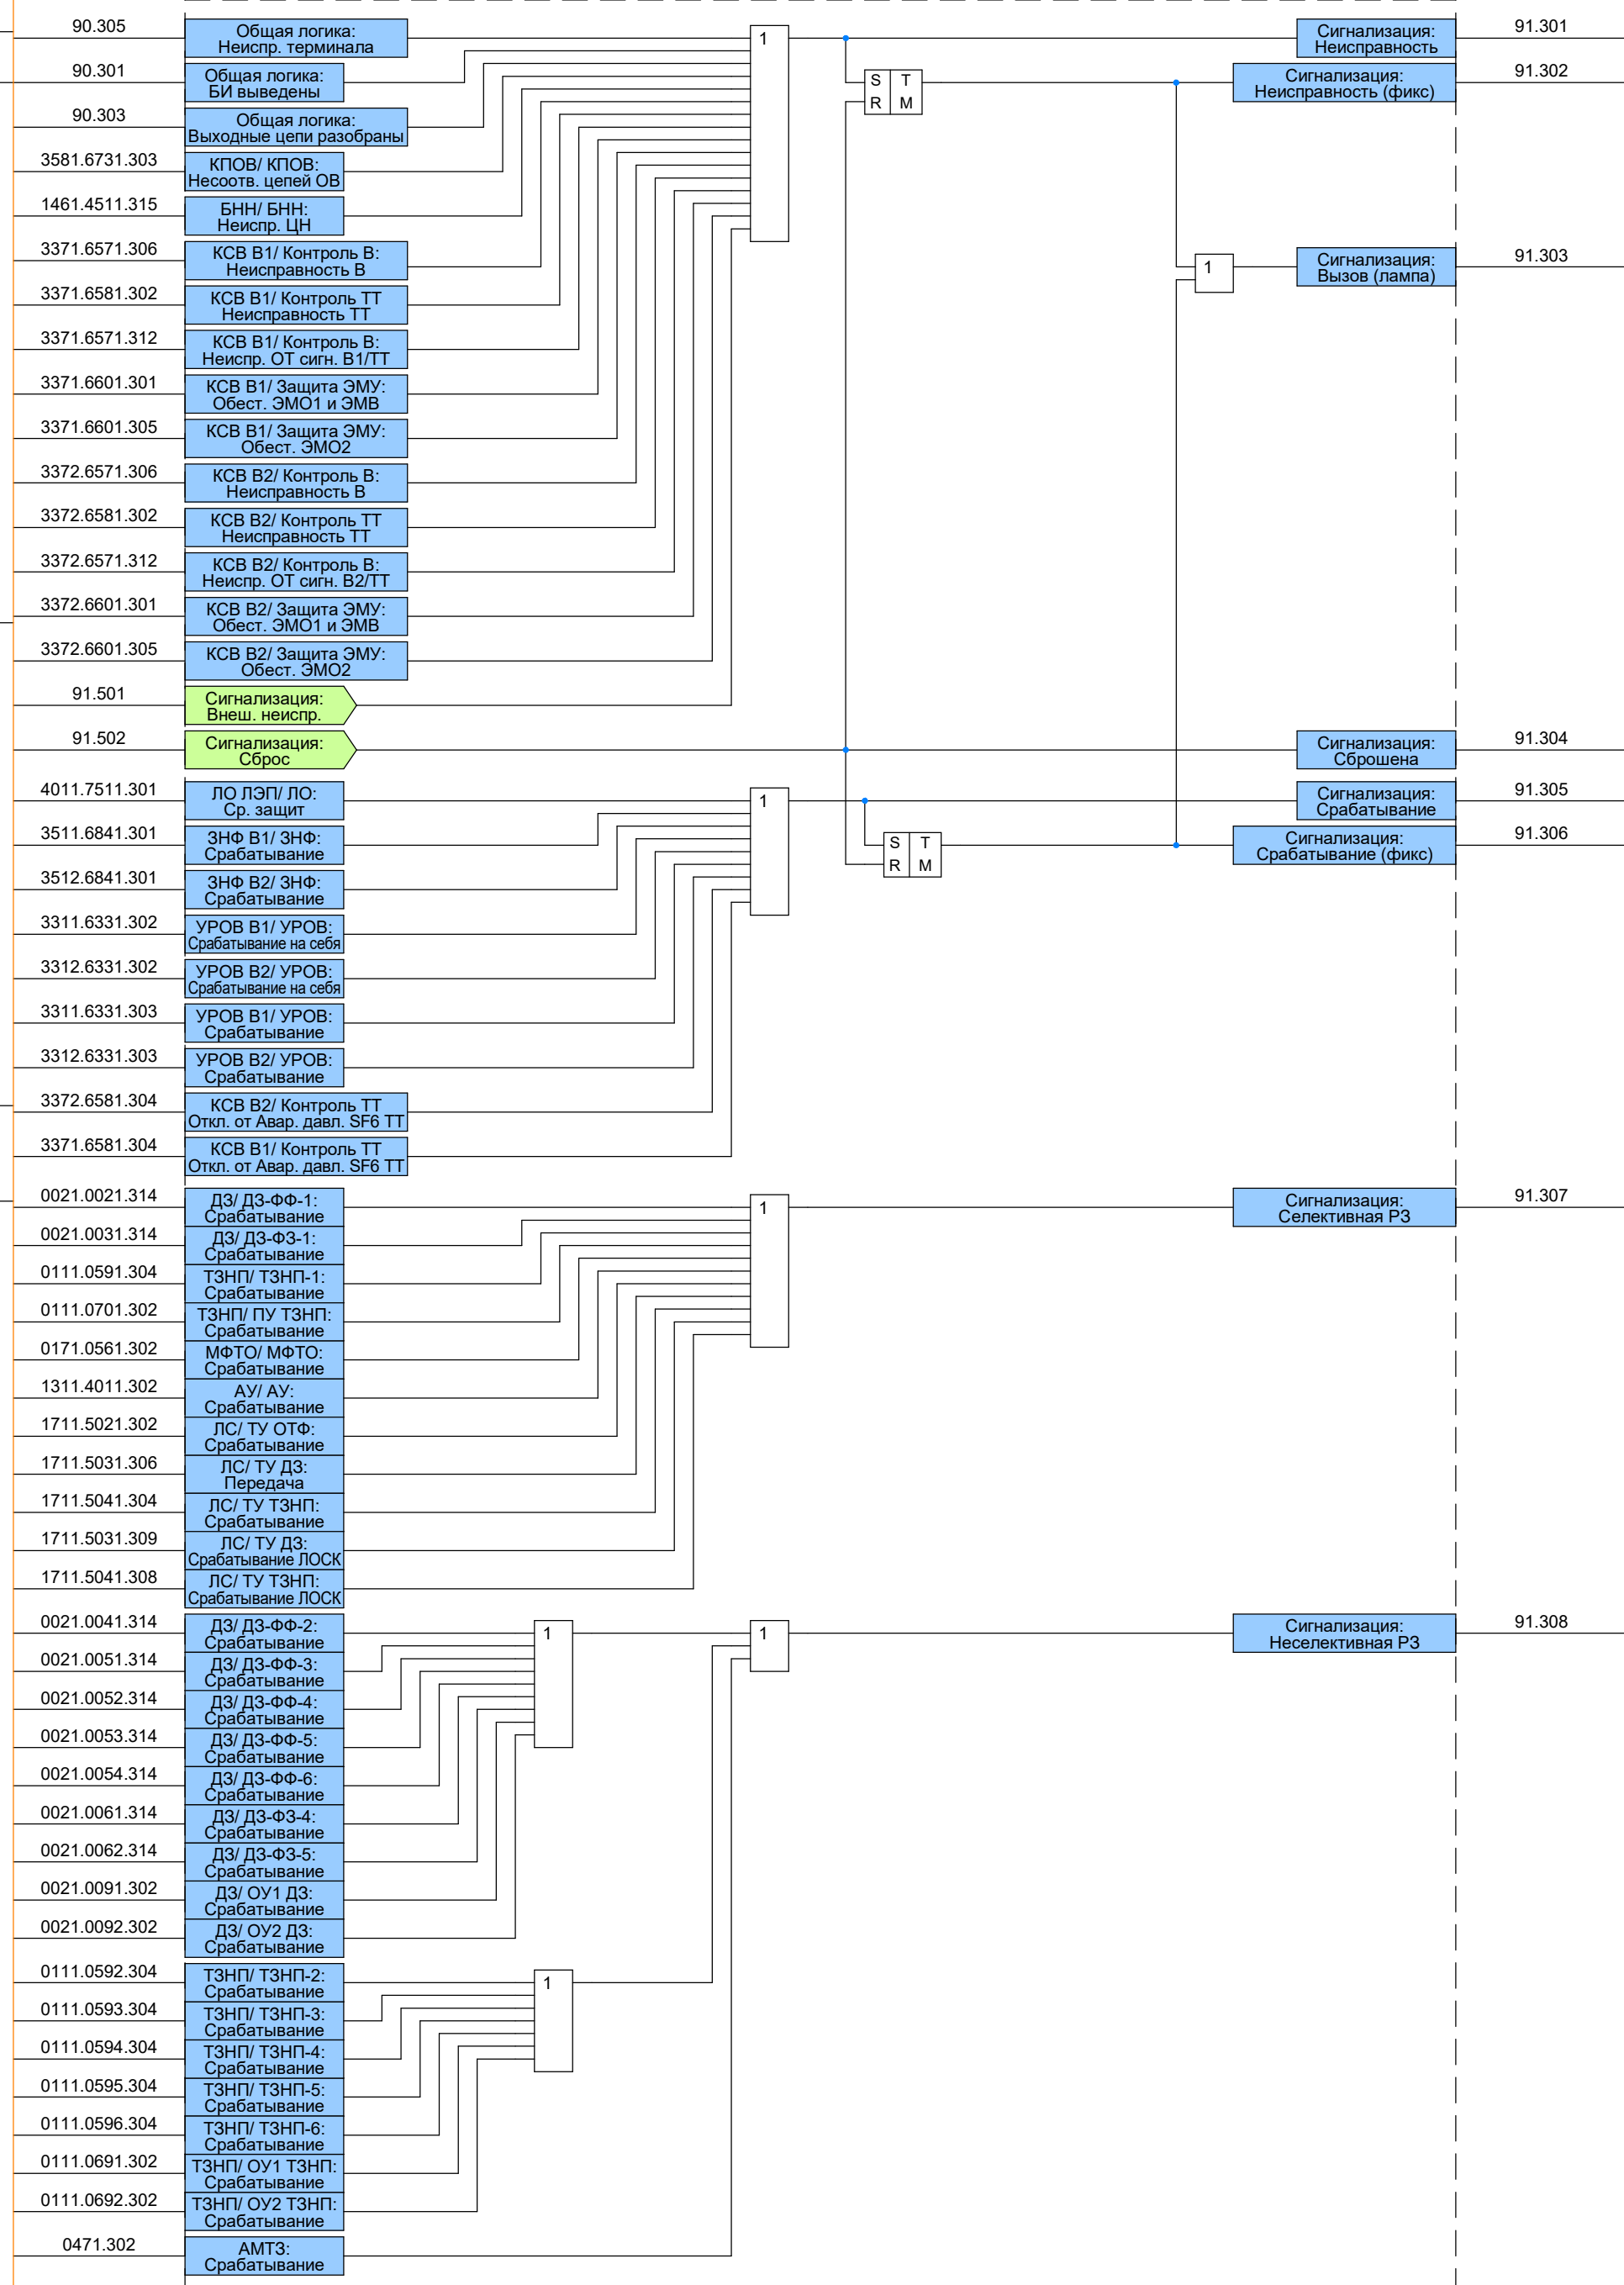

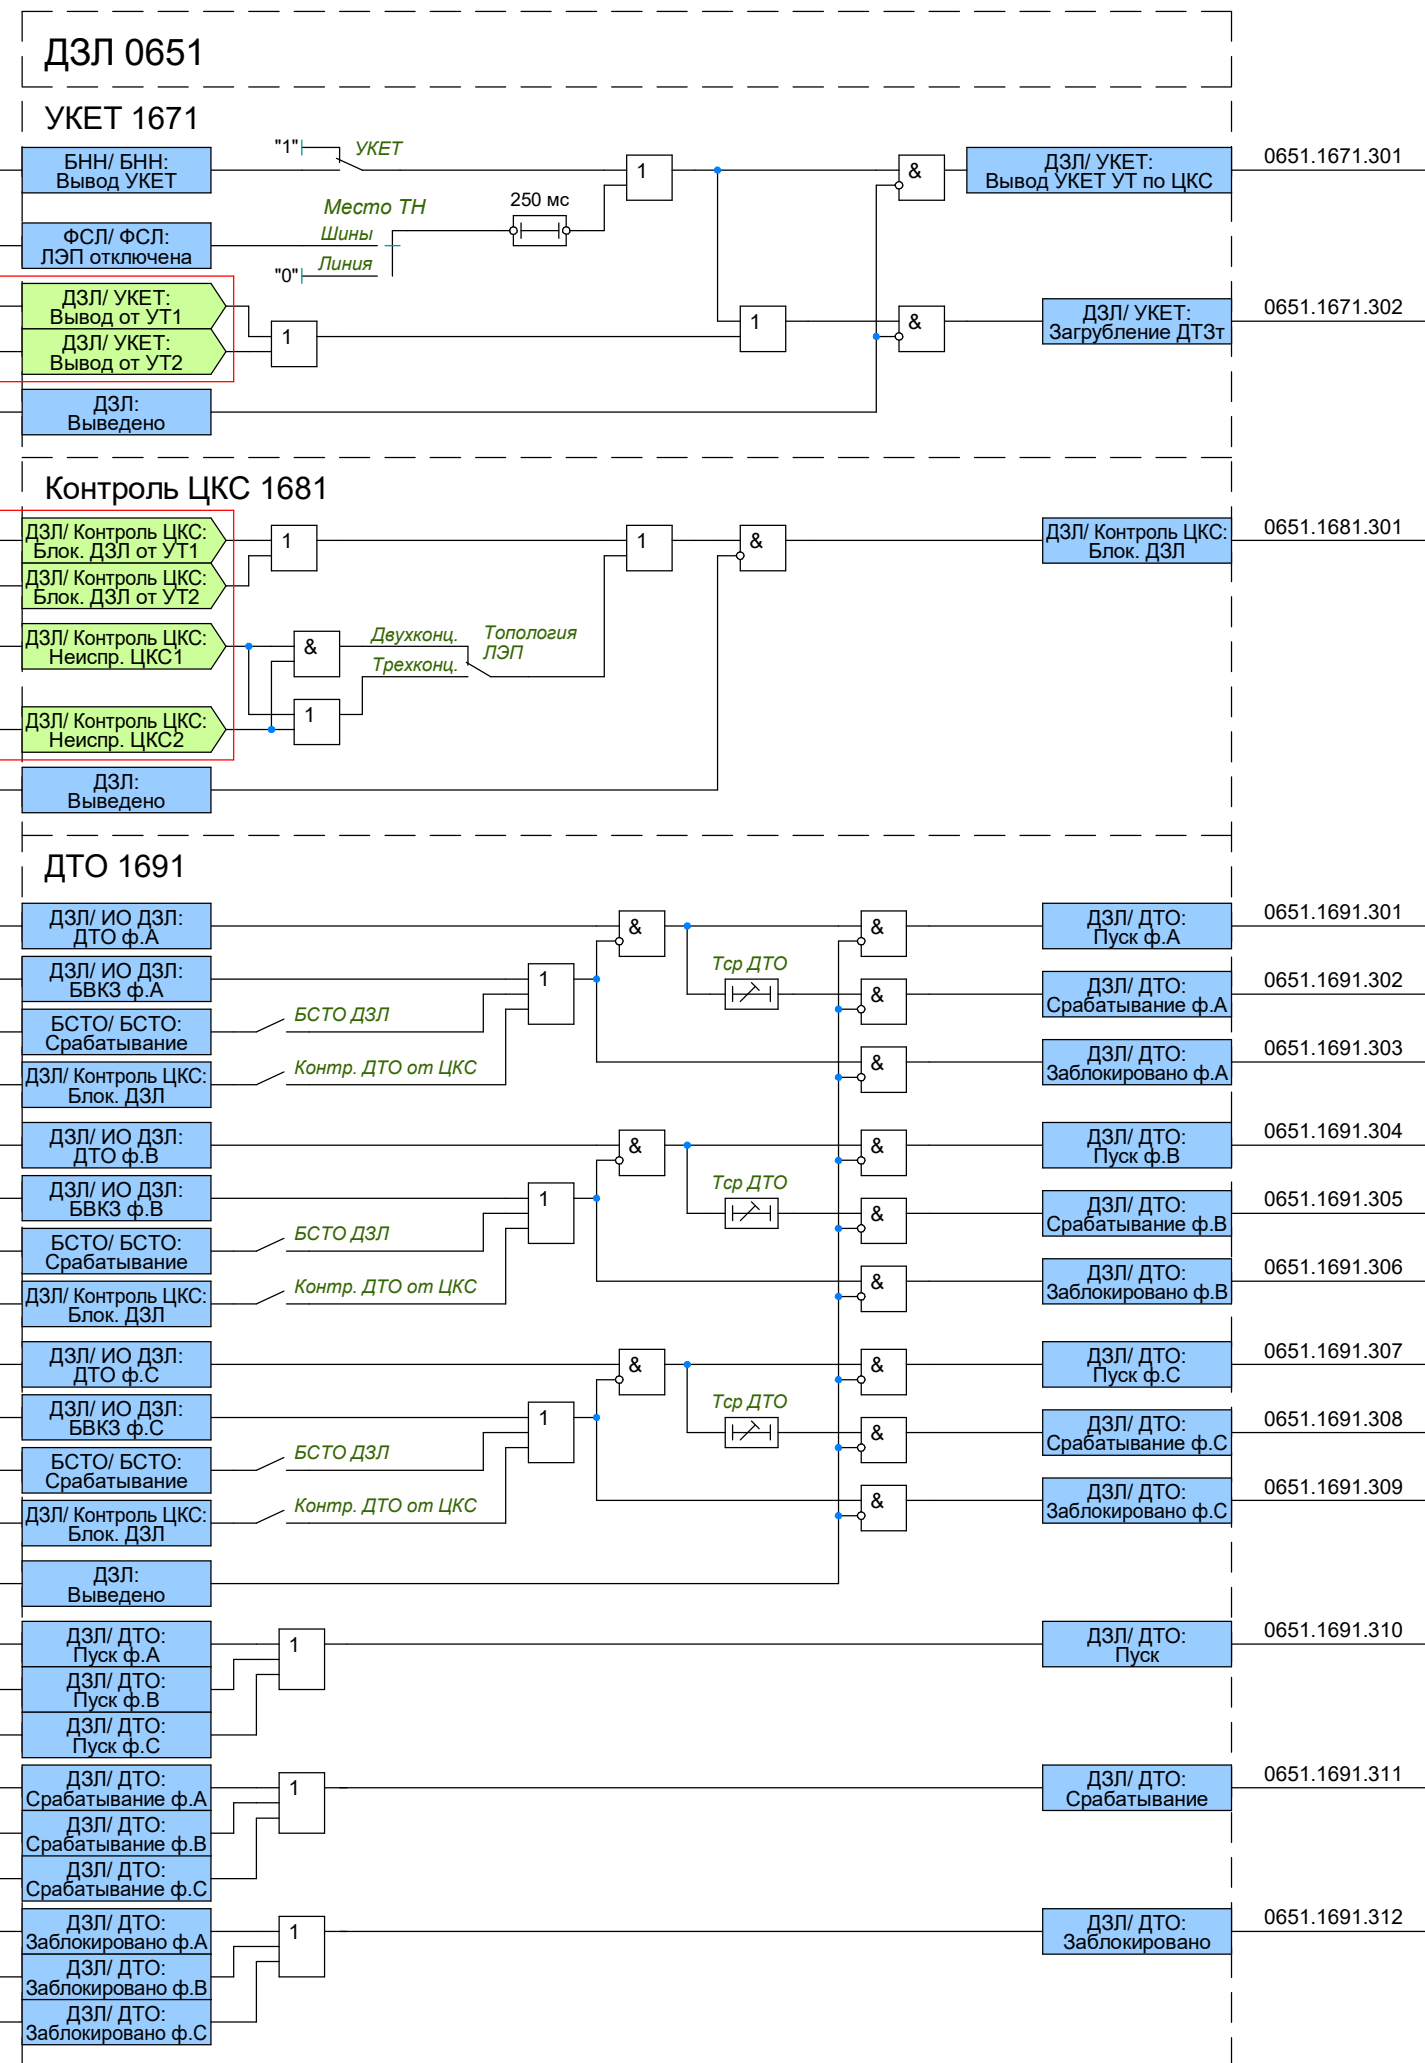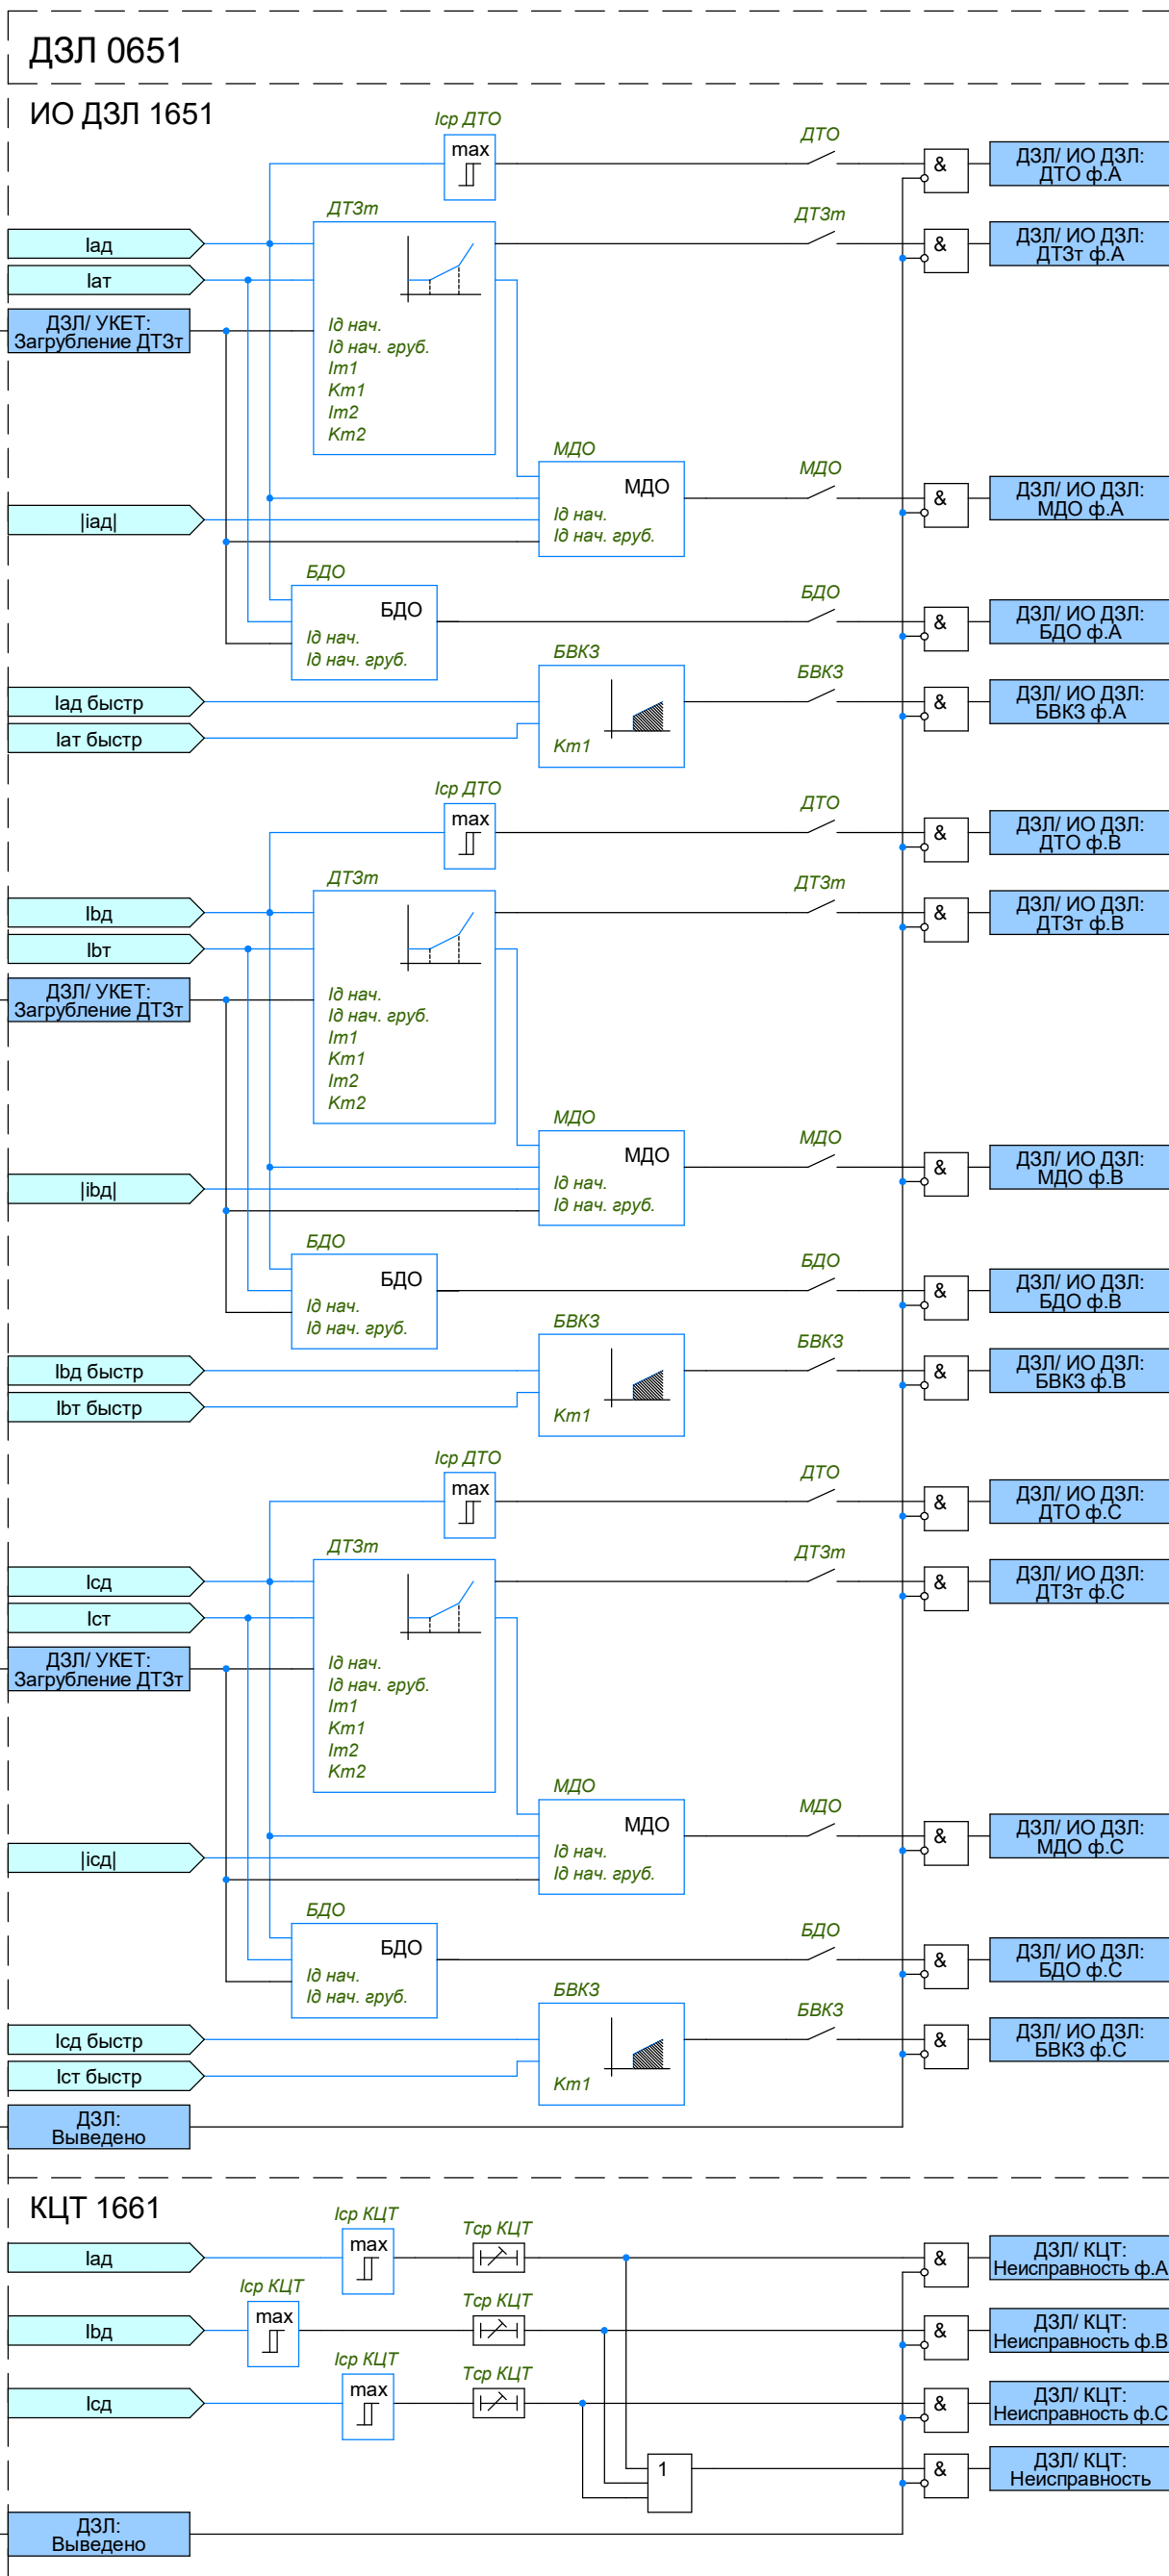


ДЗЛ 0651

ДТЗт 1701

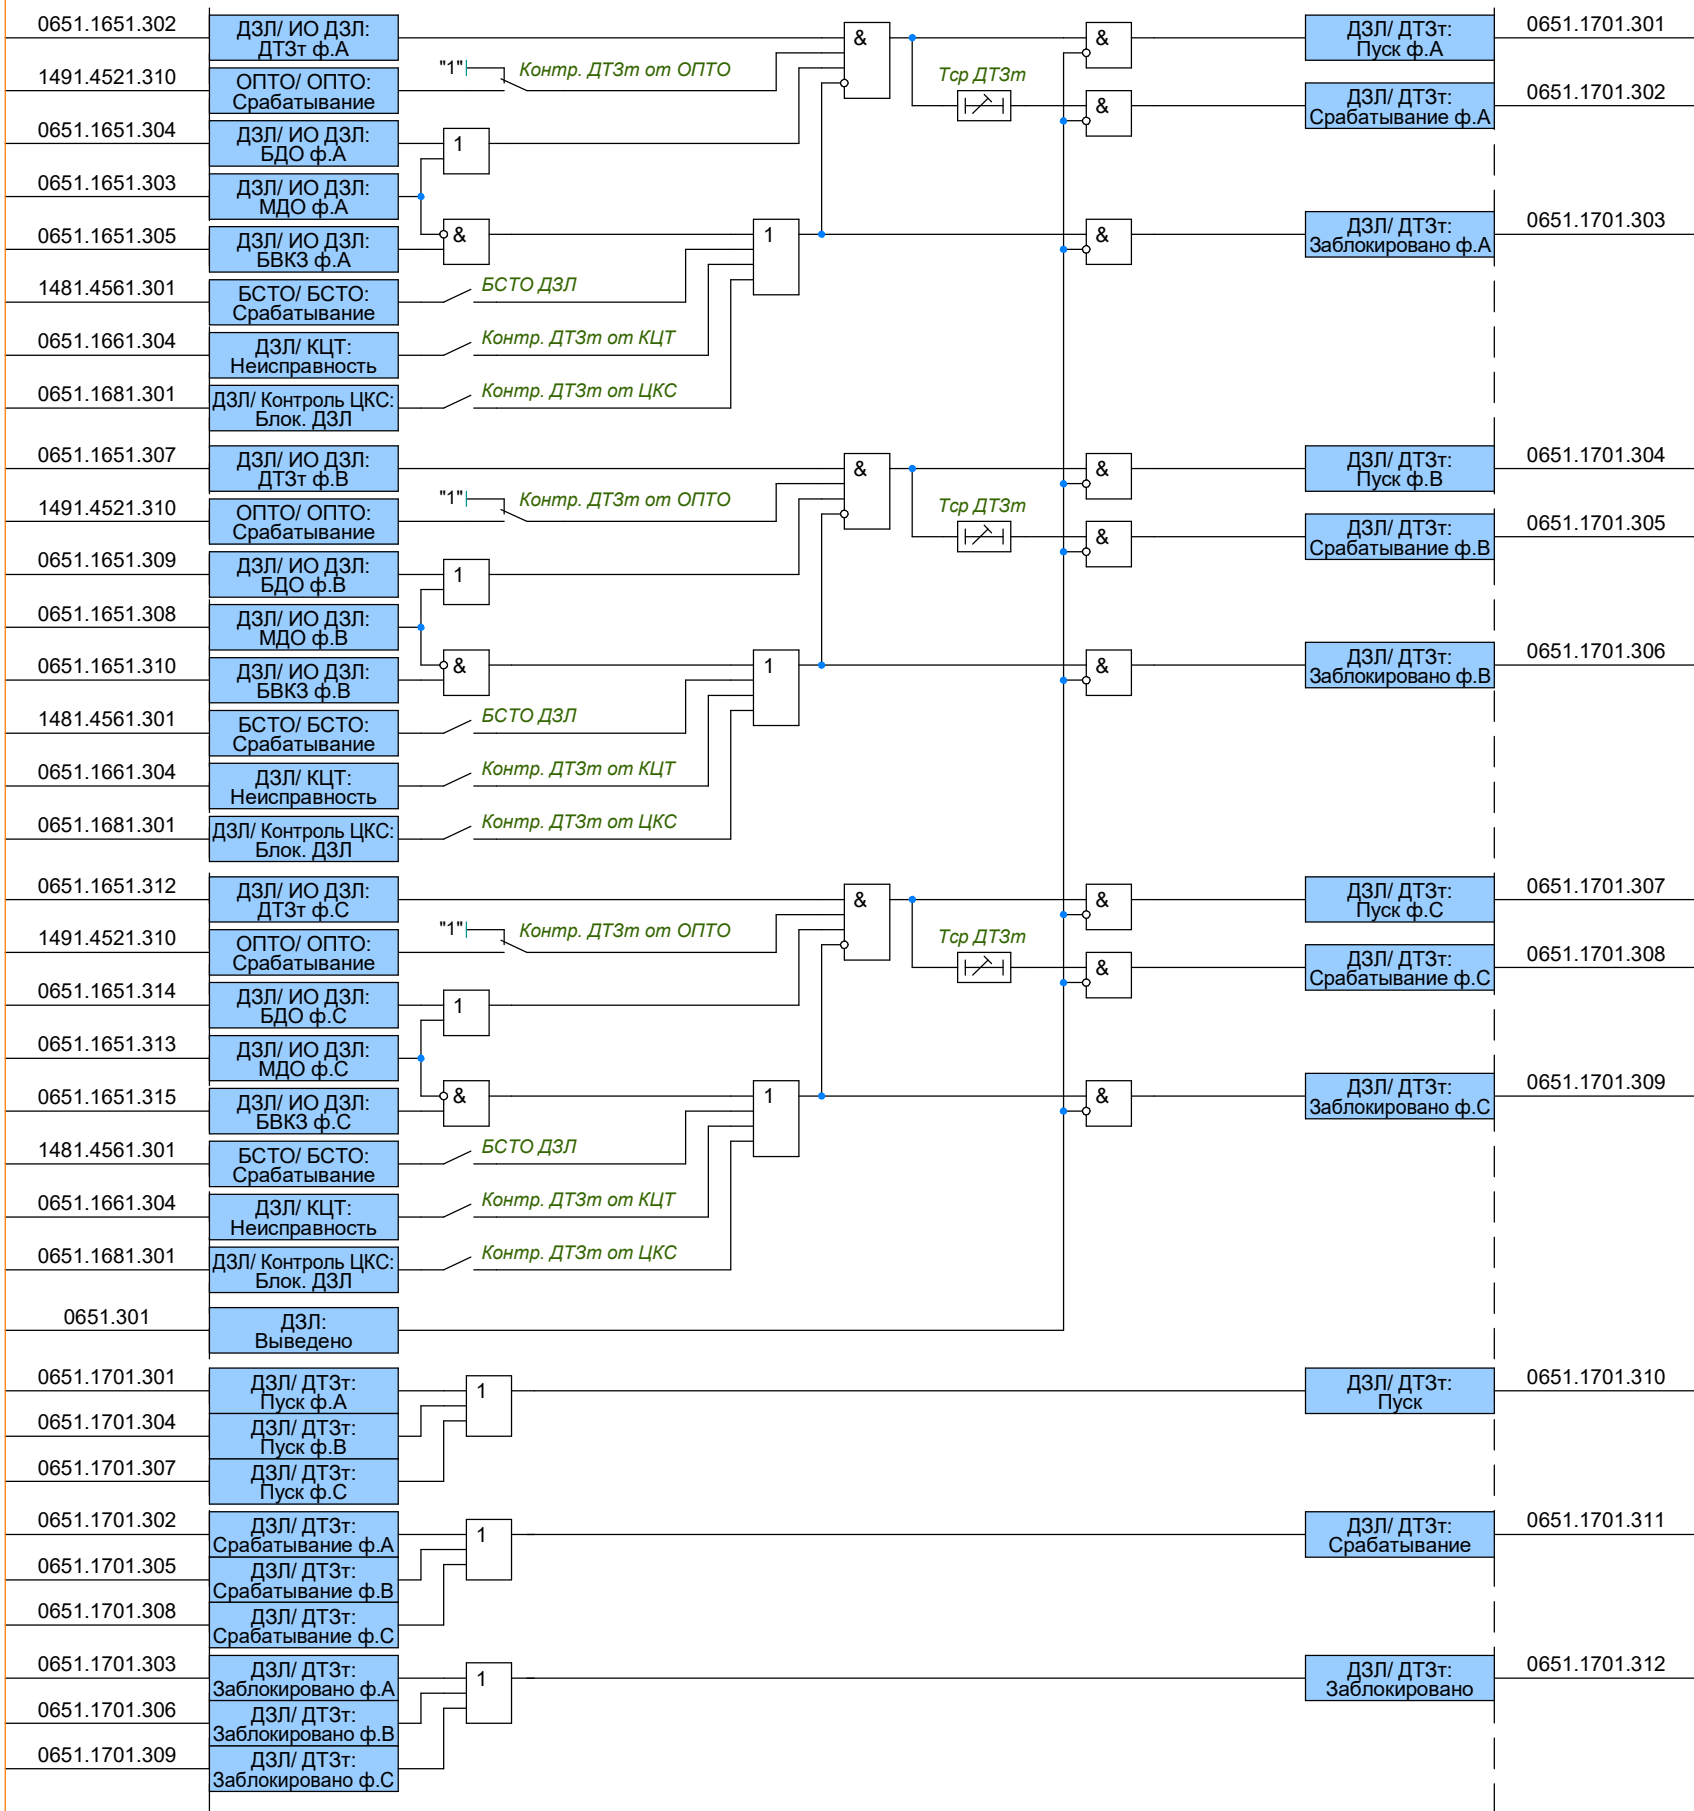


ДЗЛ 0651

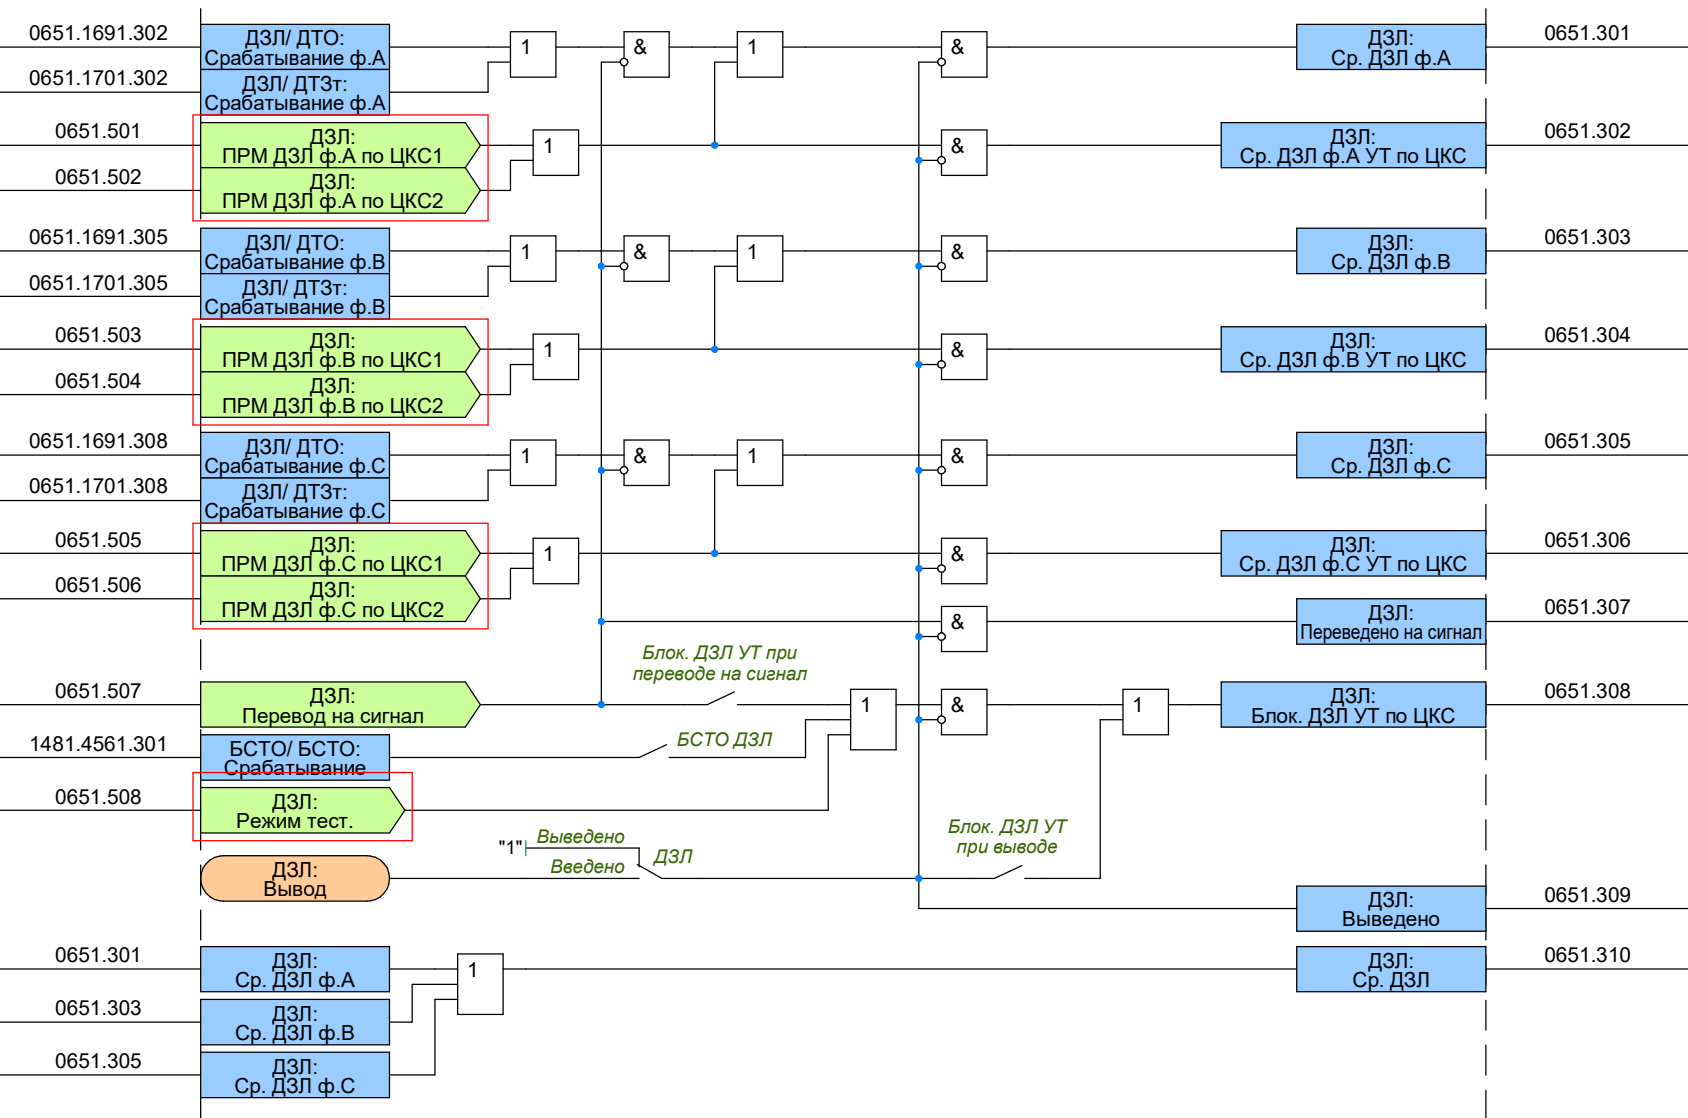


ОПТО 1491

ОПТО 4521

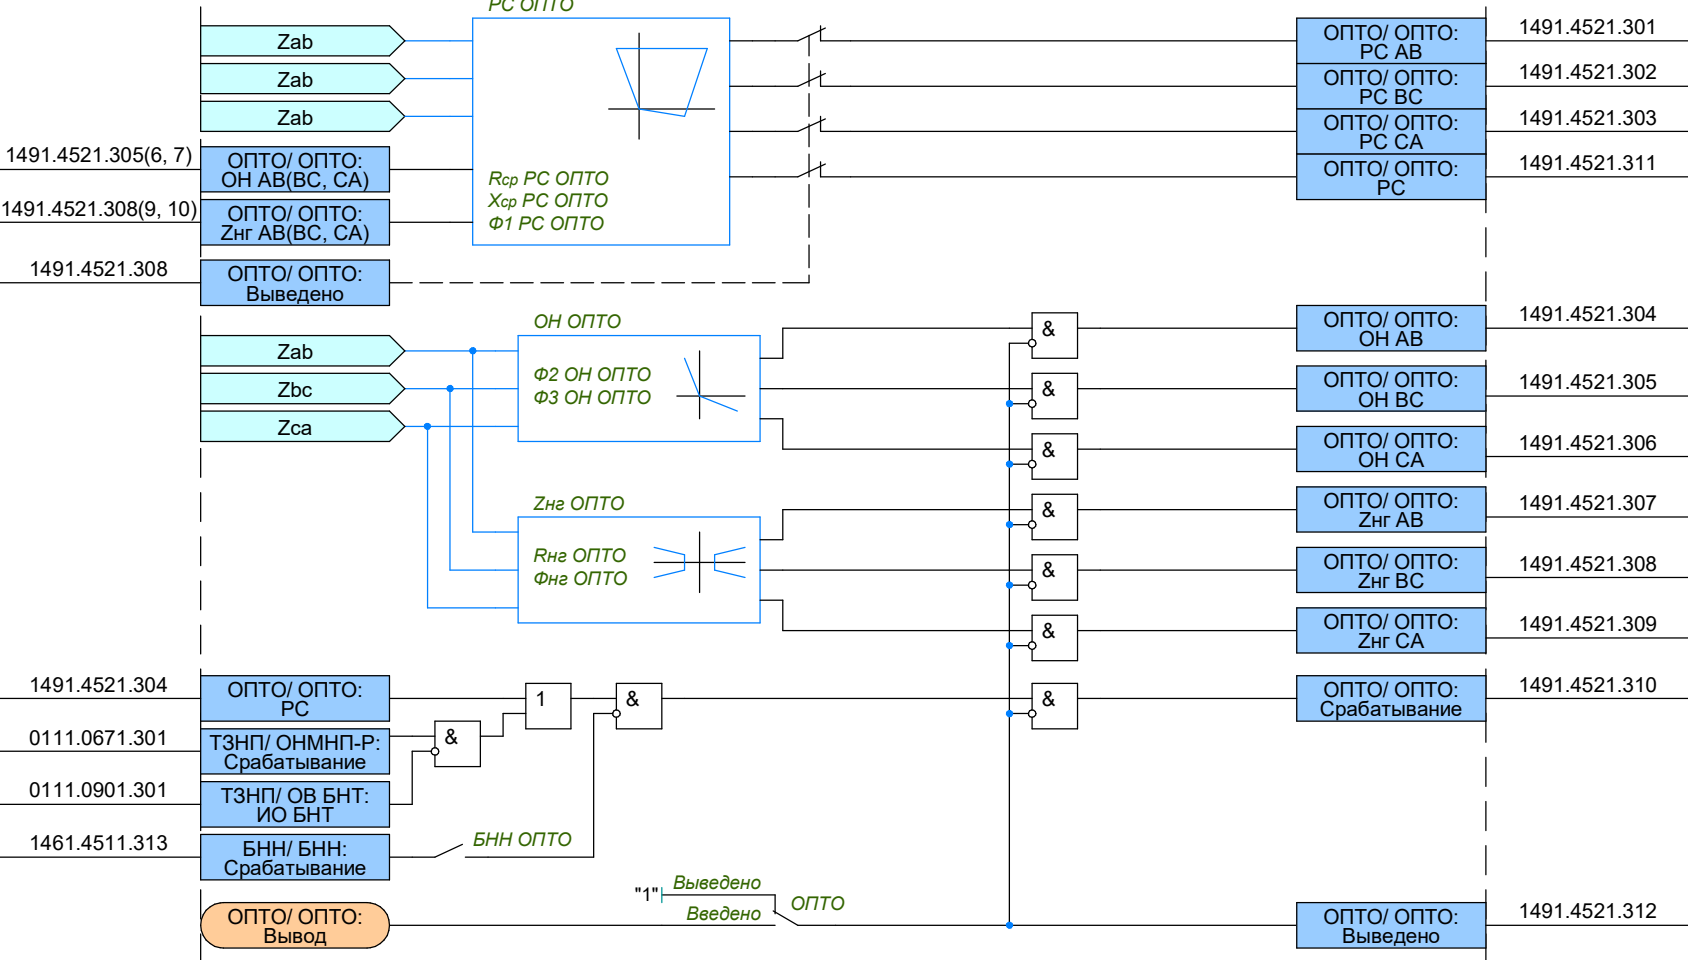


ДЗ 0021



ОУ1 ДЗ 0091

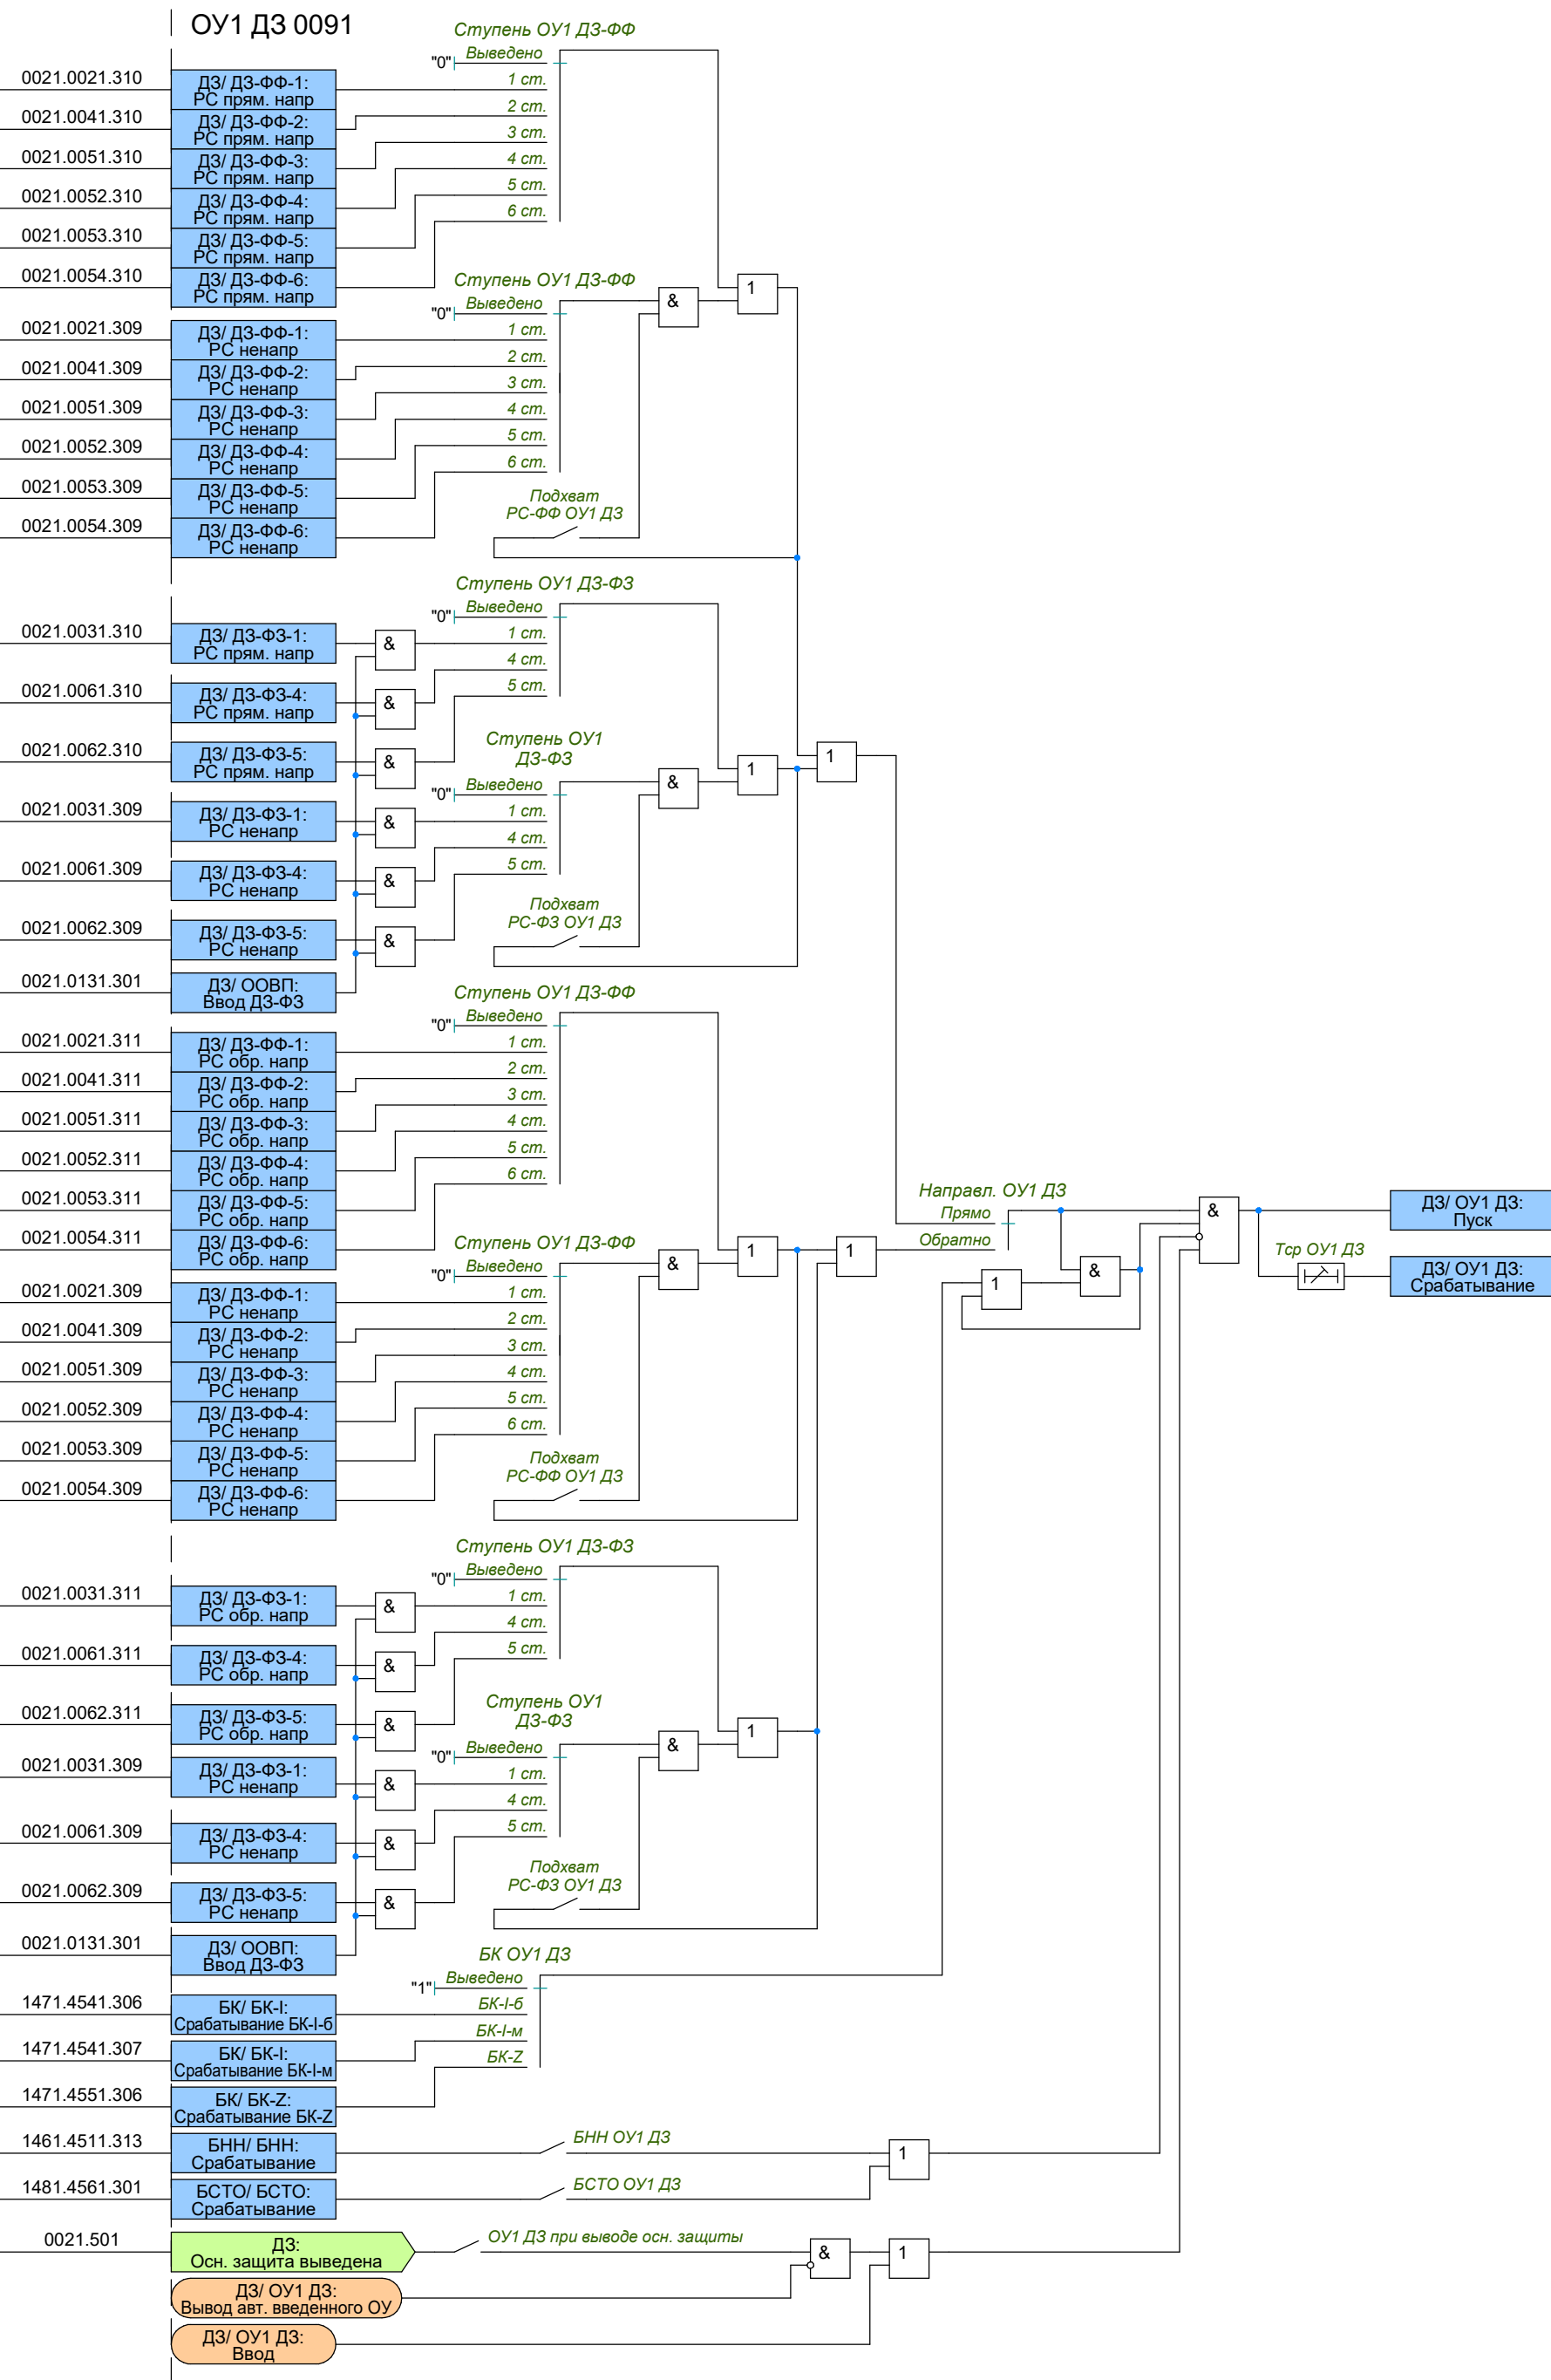

ДЗ 0021


ОУ2 ДЗ 0092

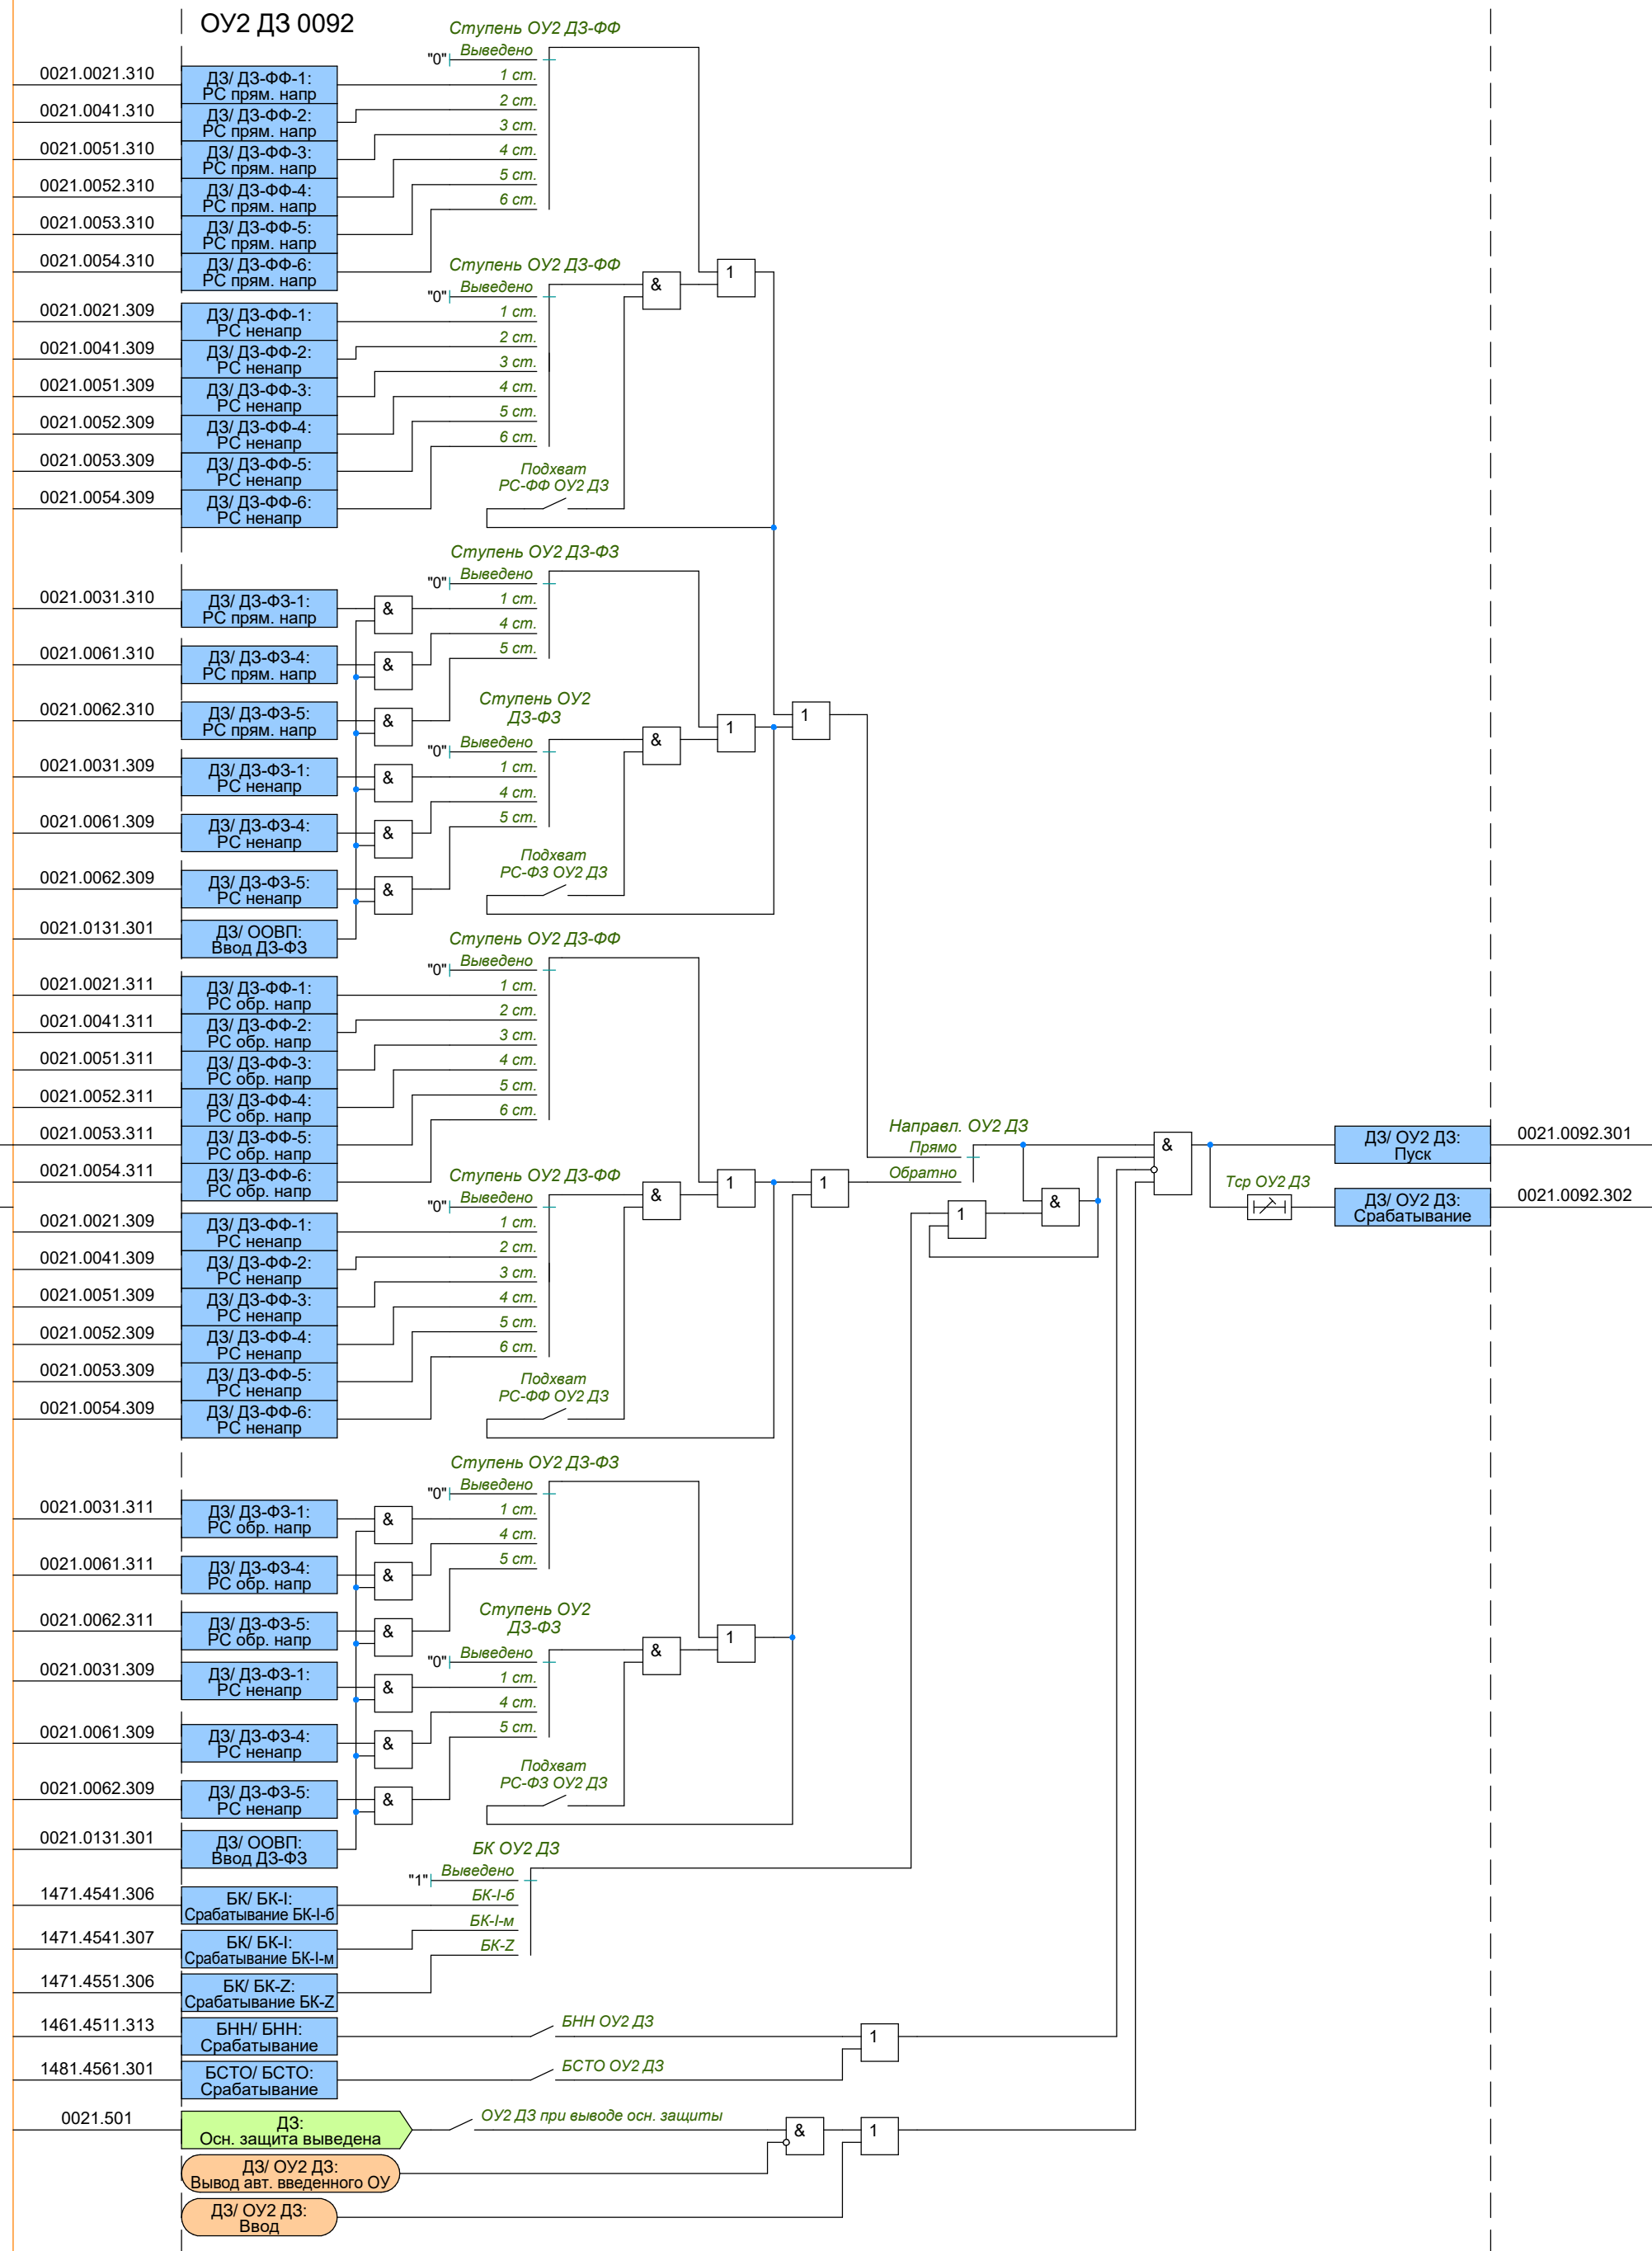

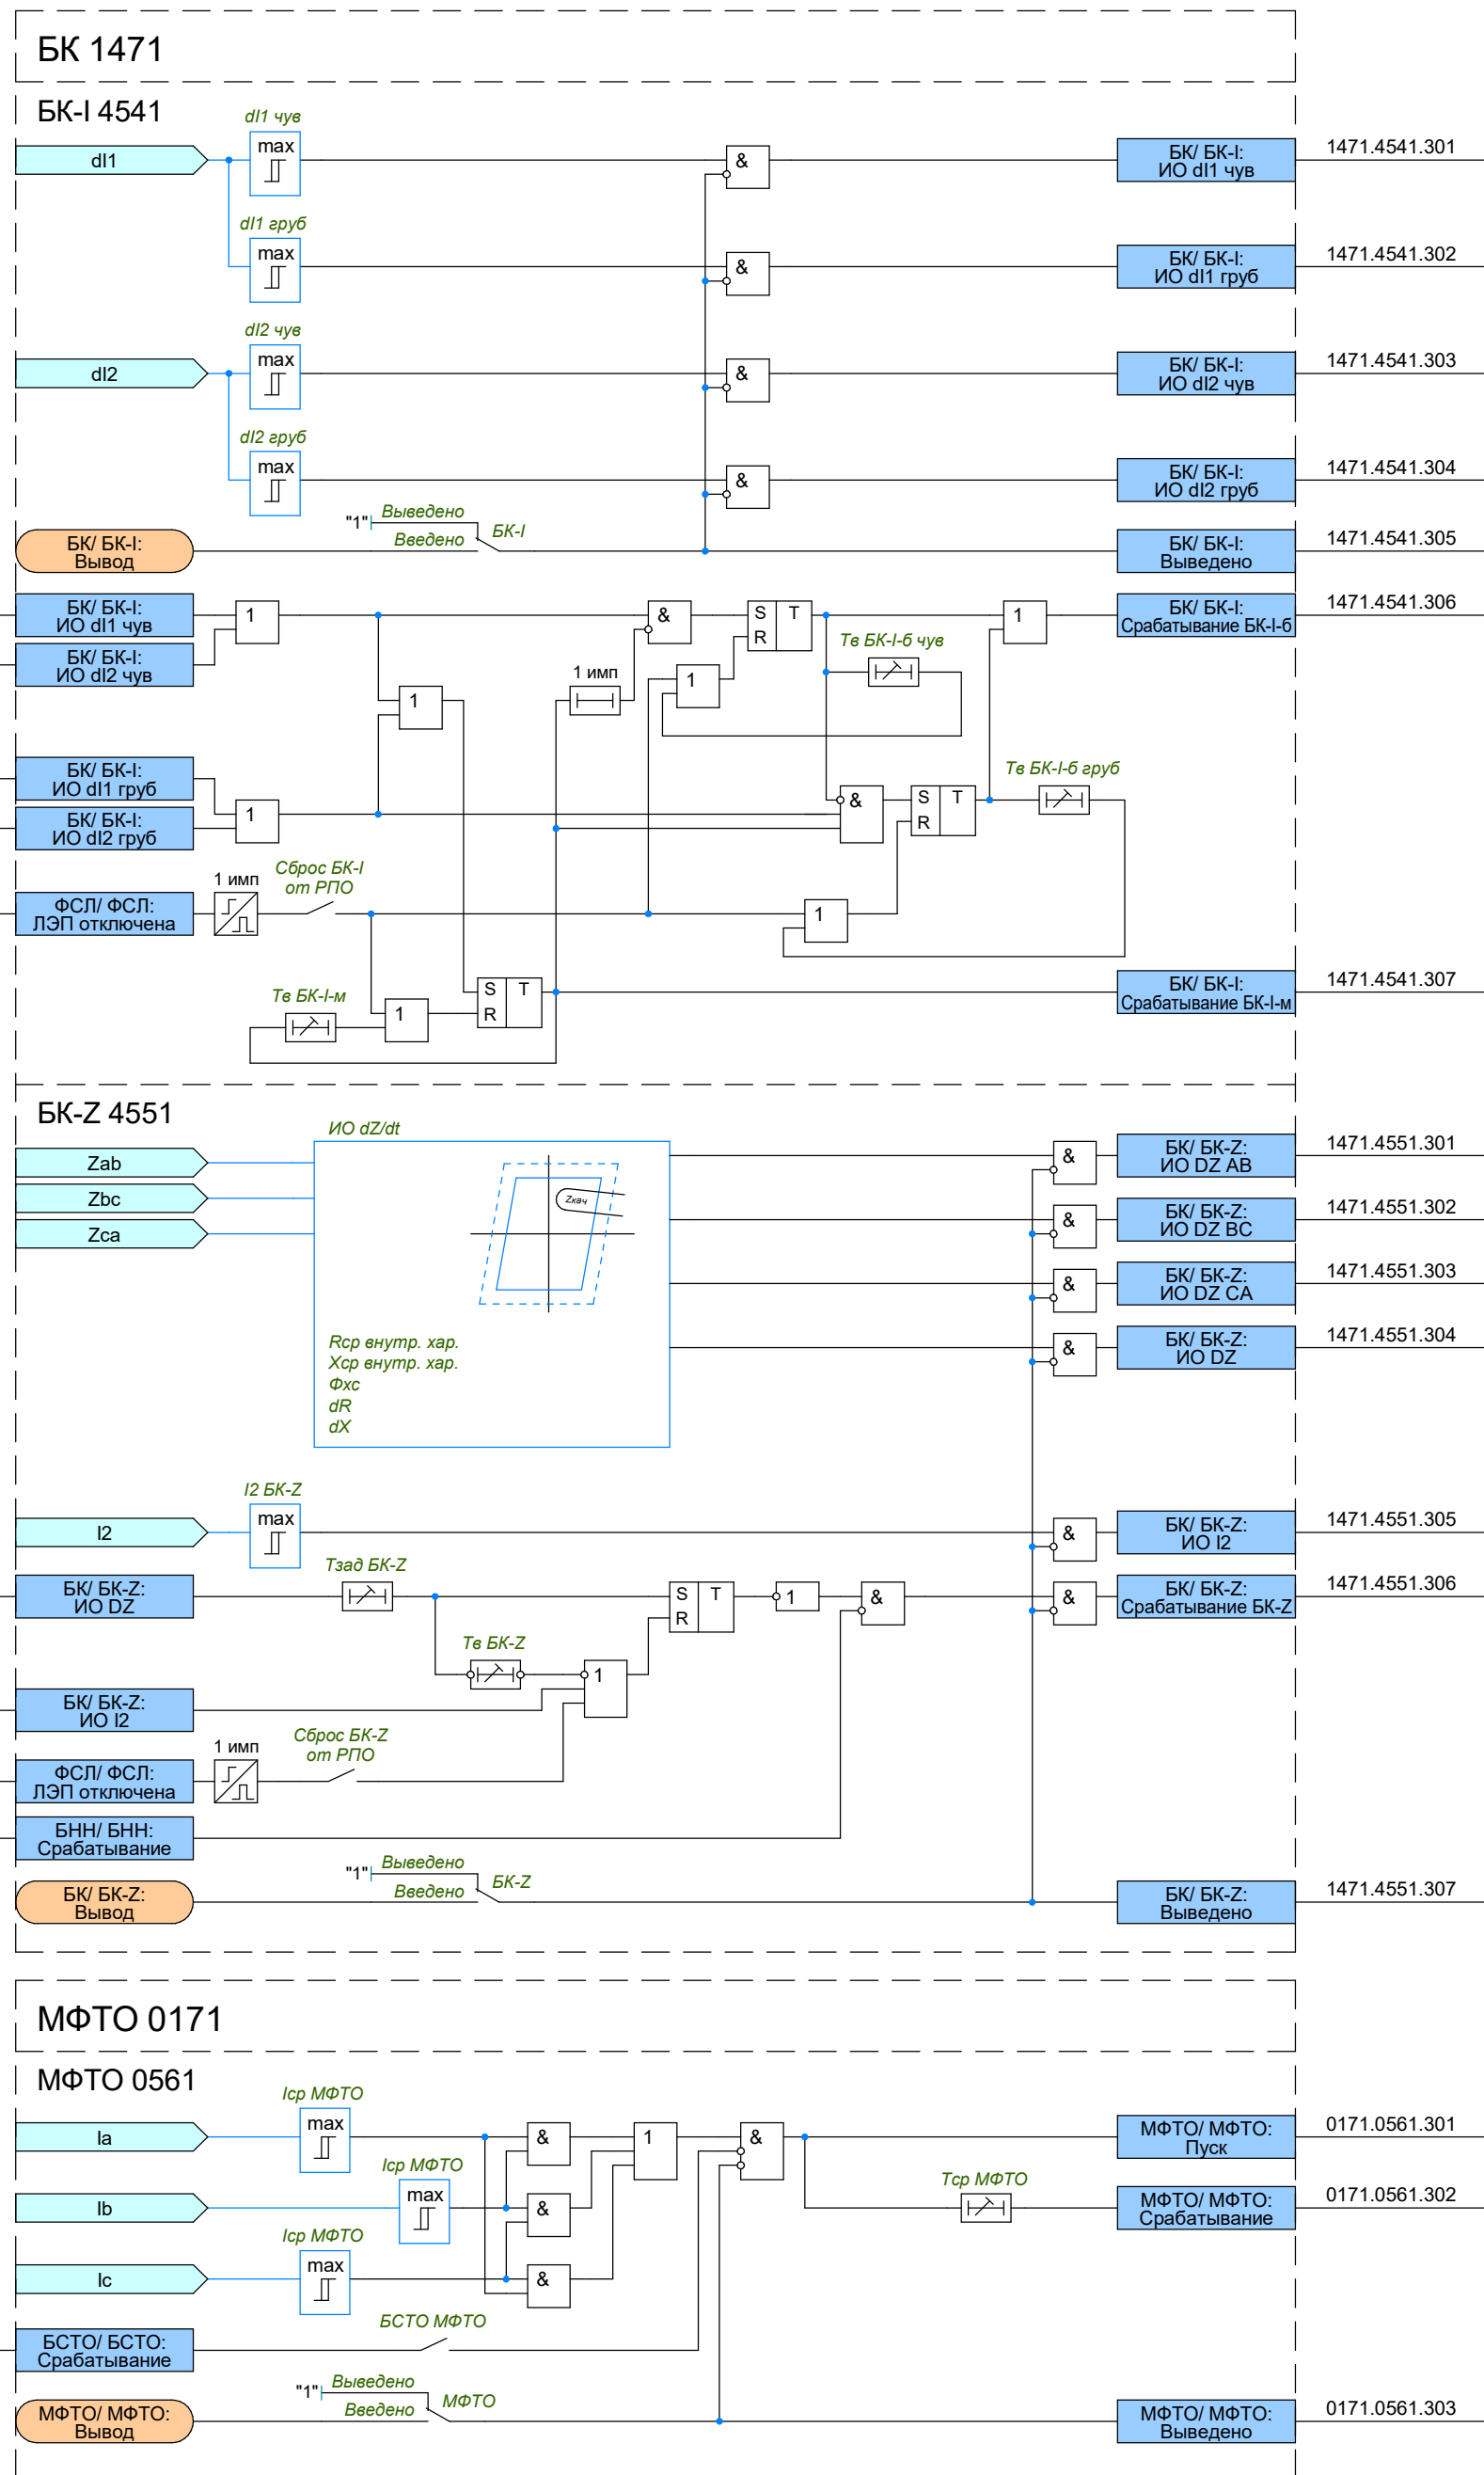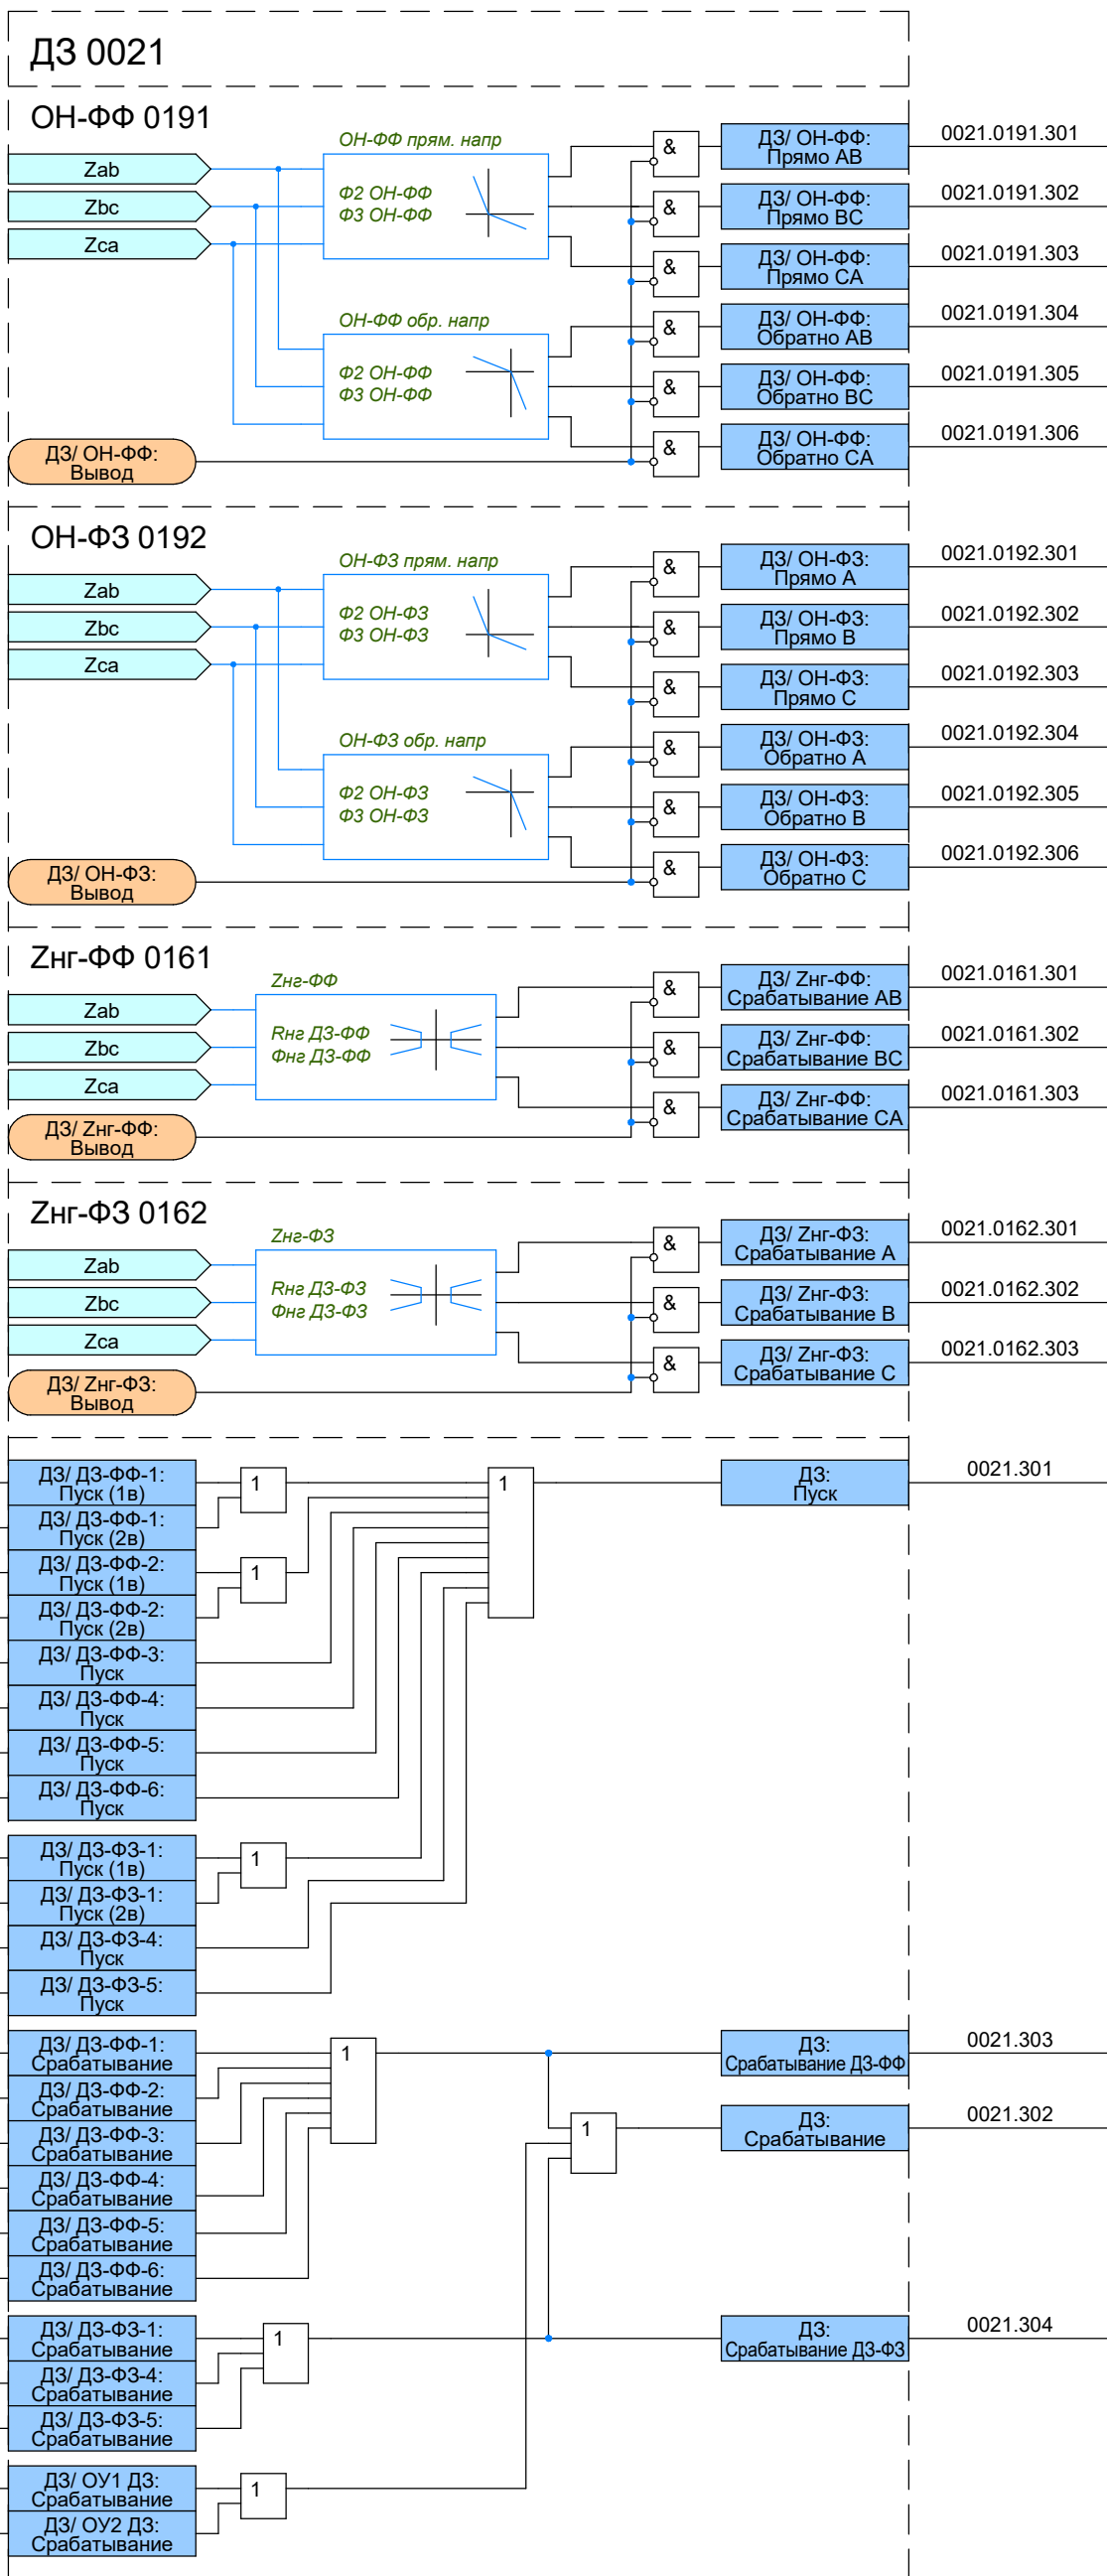


ТЗНП 0111

ТЗНП-1 0591

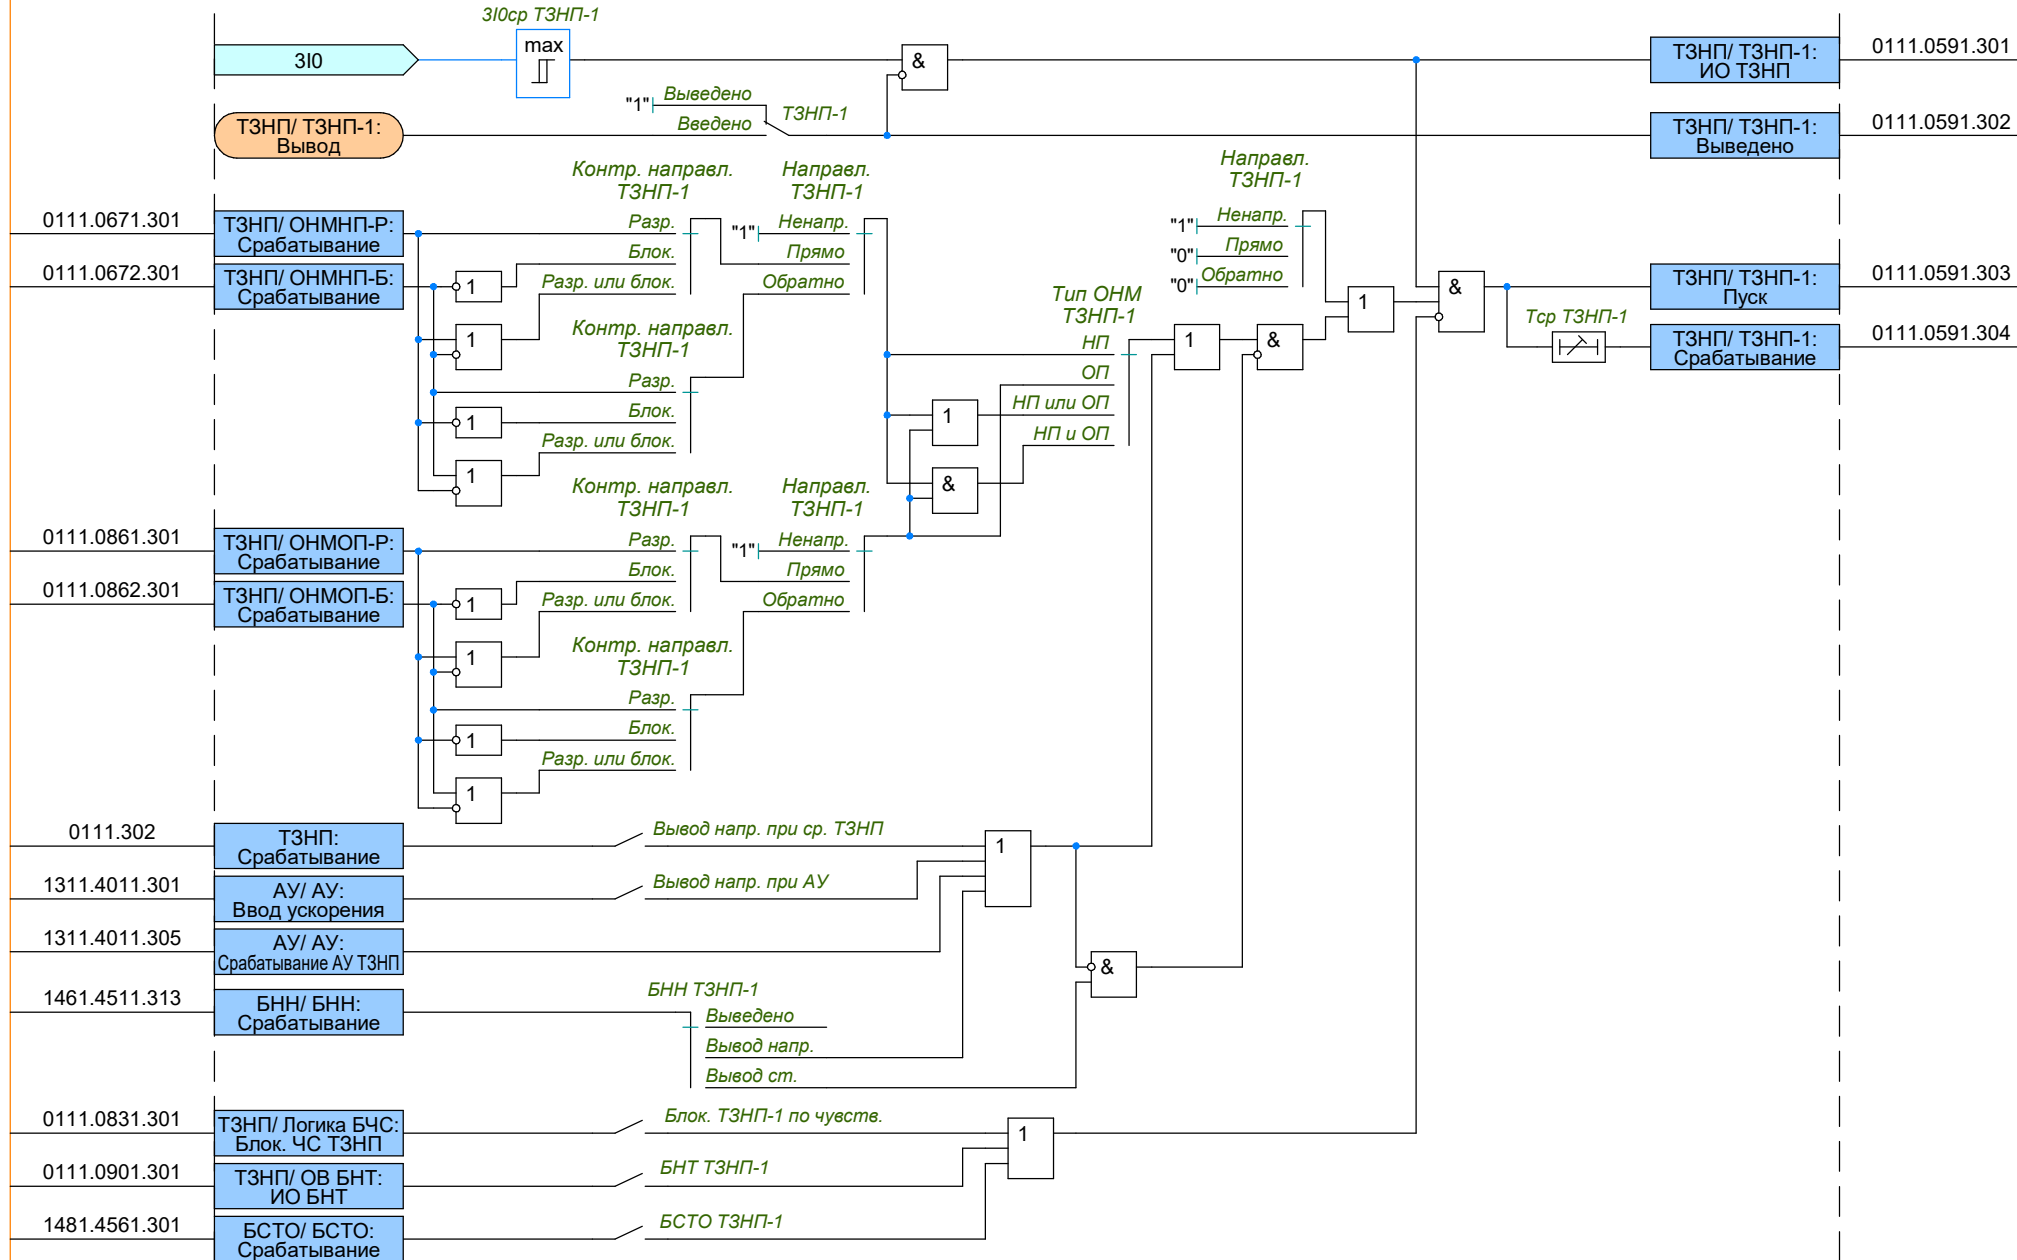


ТЗНП-2 0592

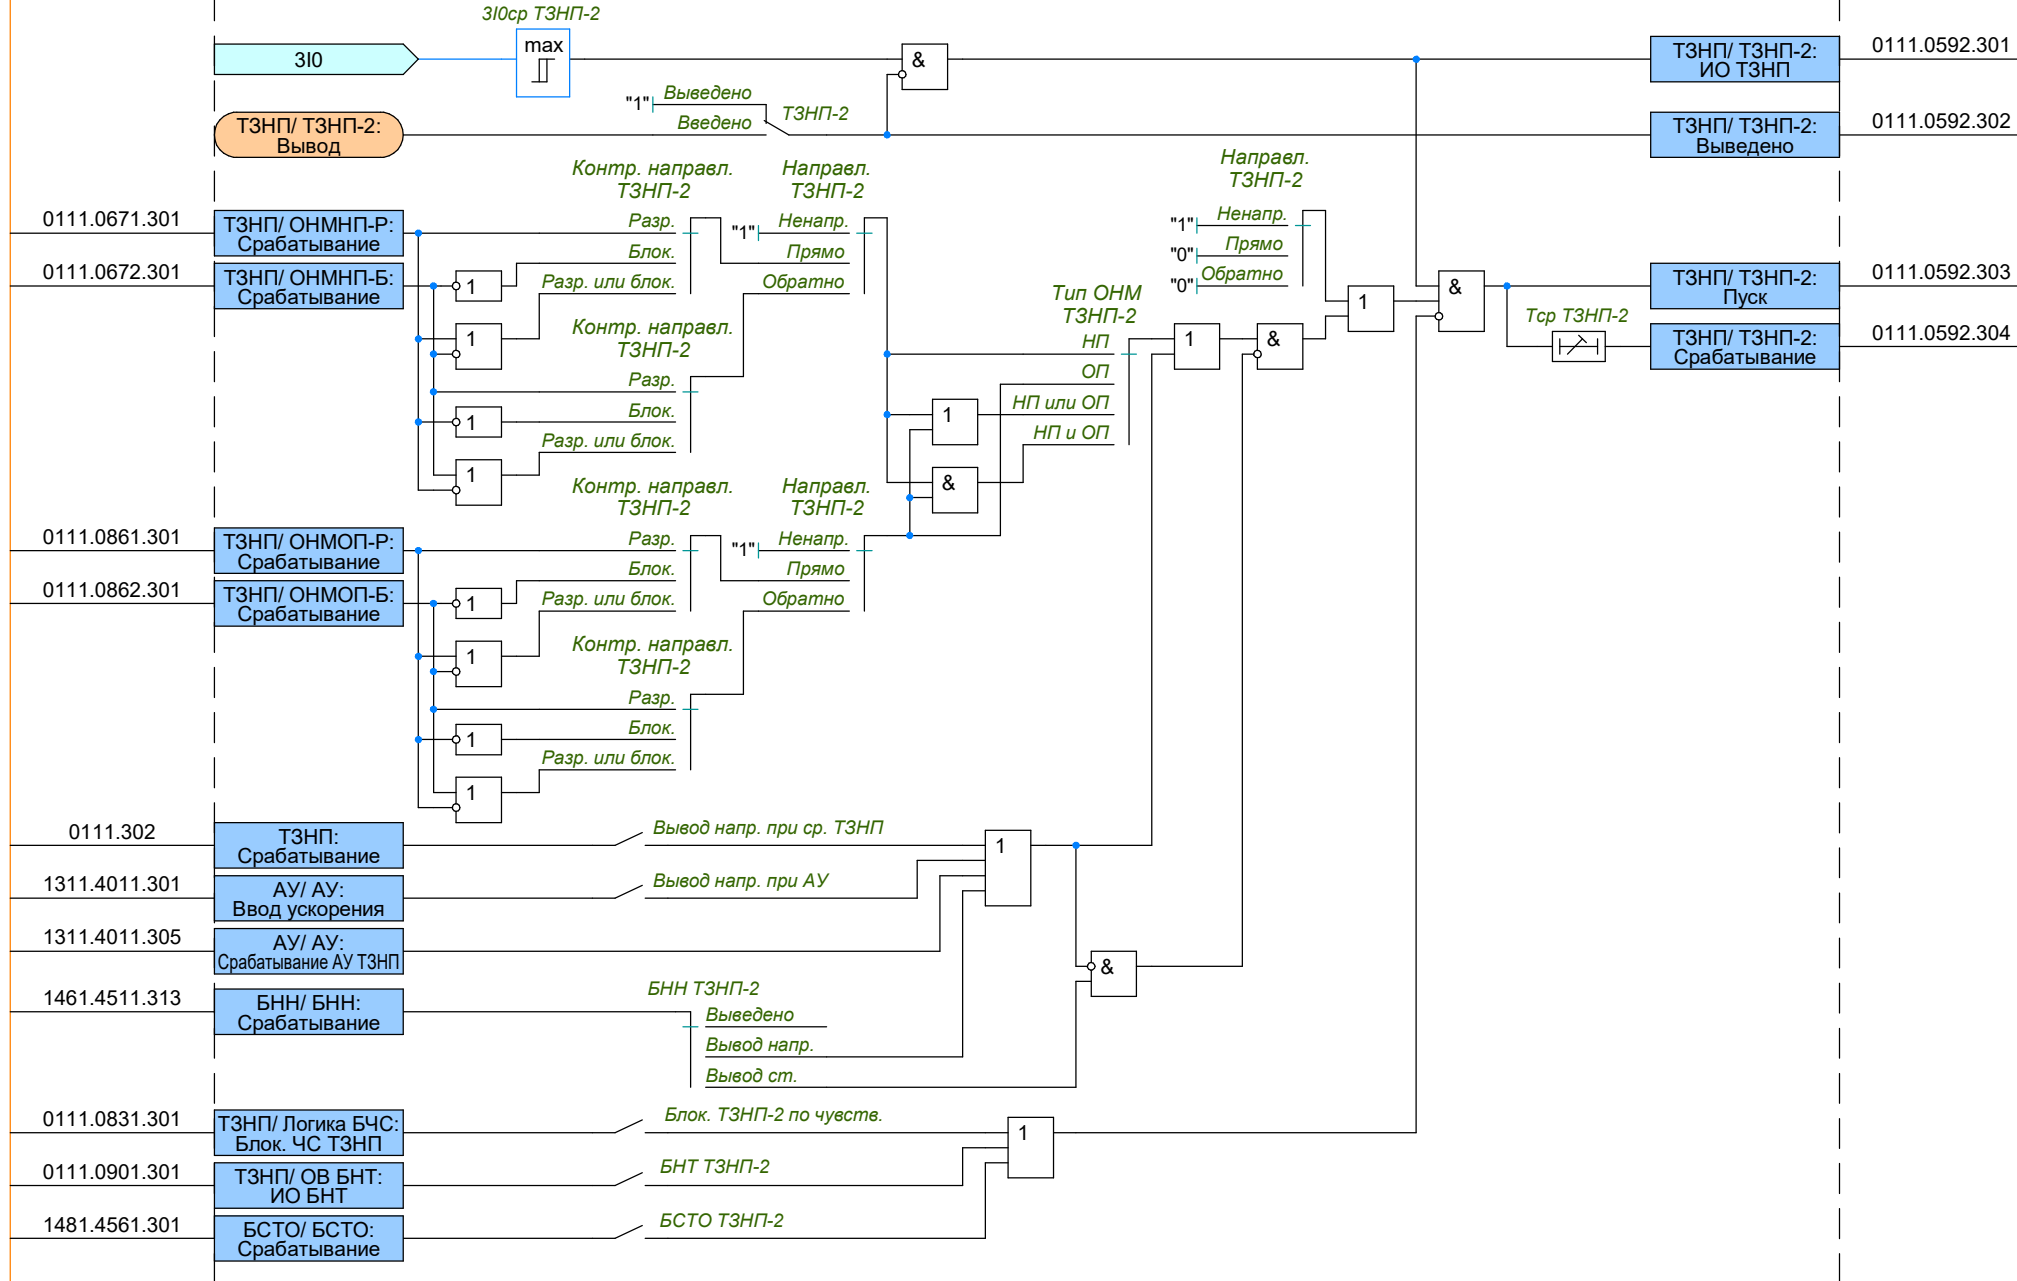


ТЗНП 0111

ТЗНП-3 0593

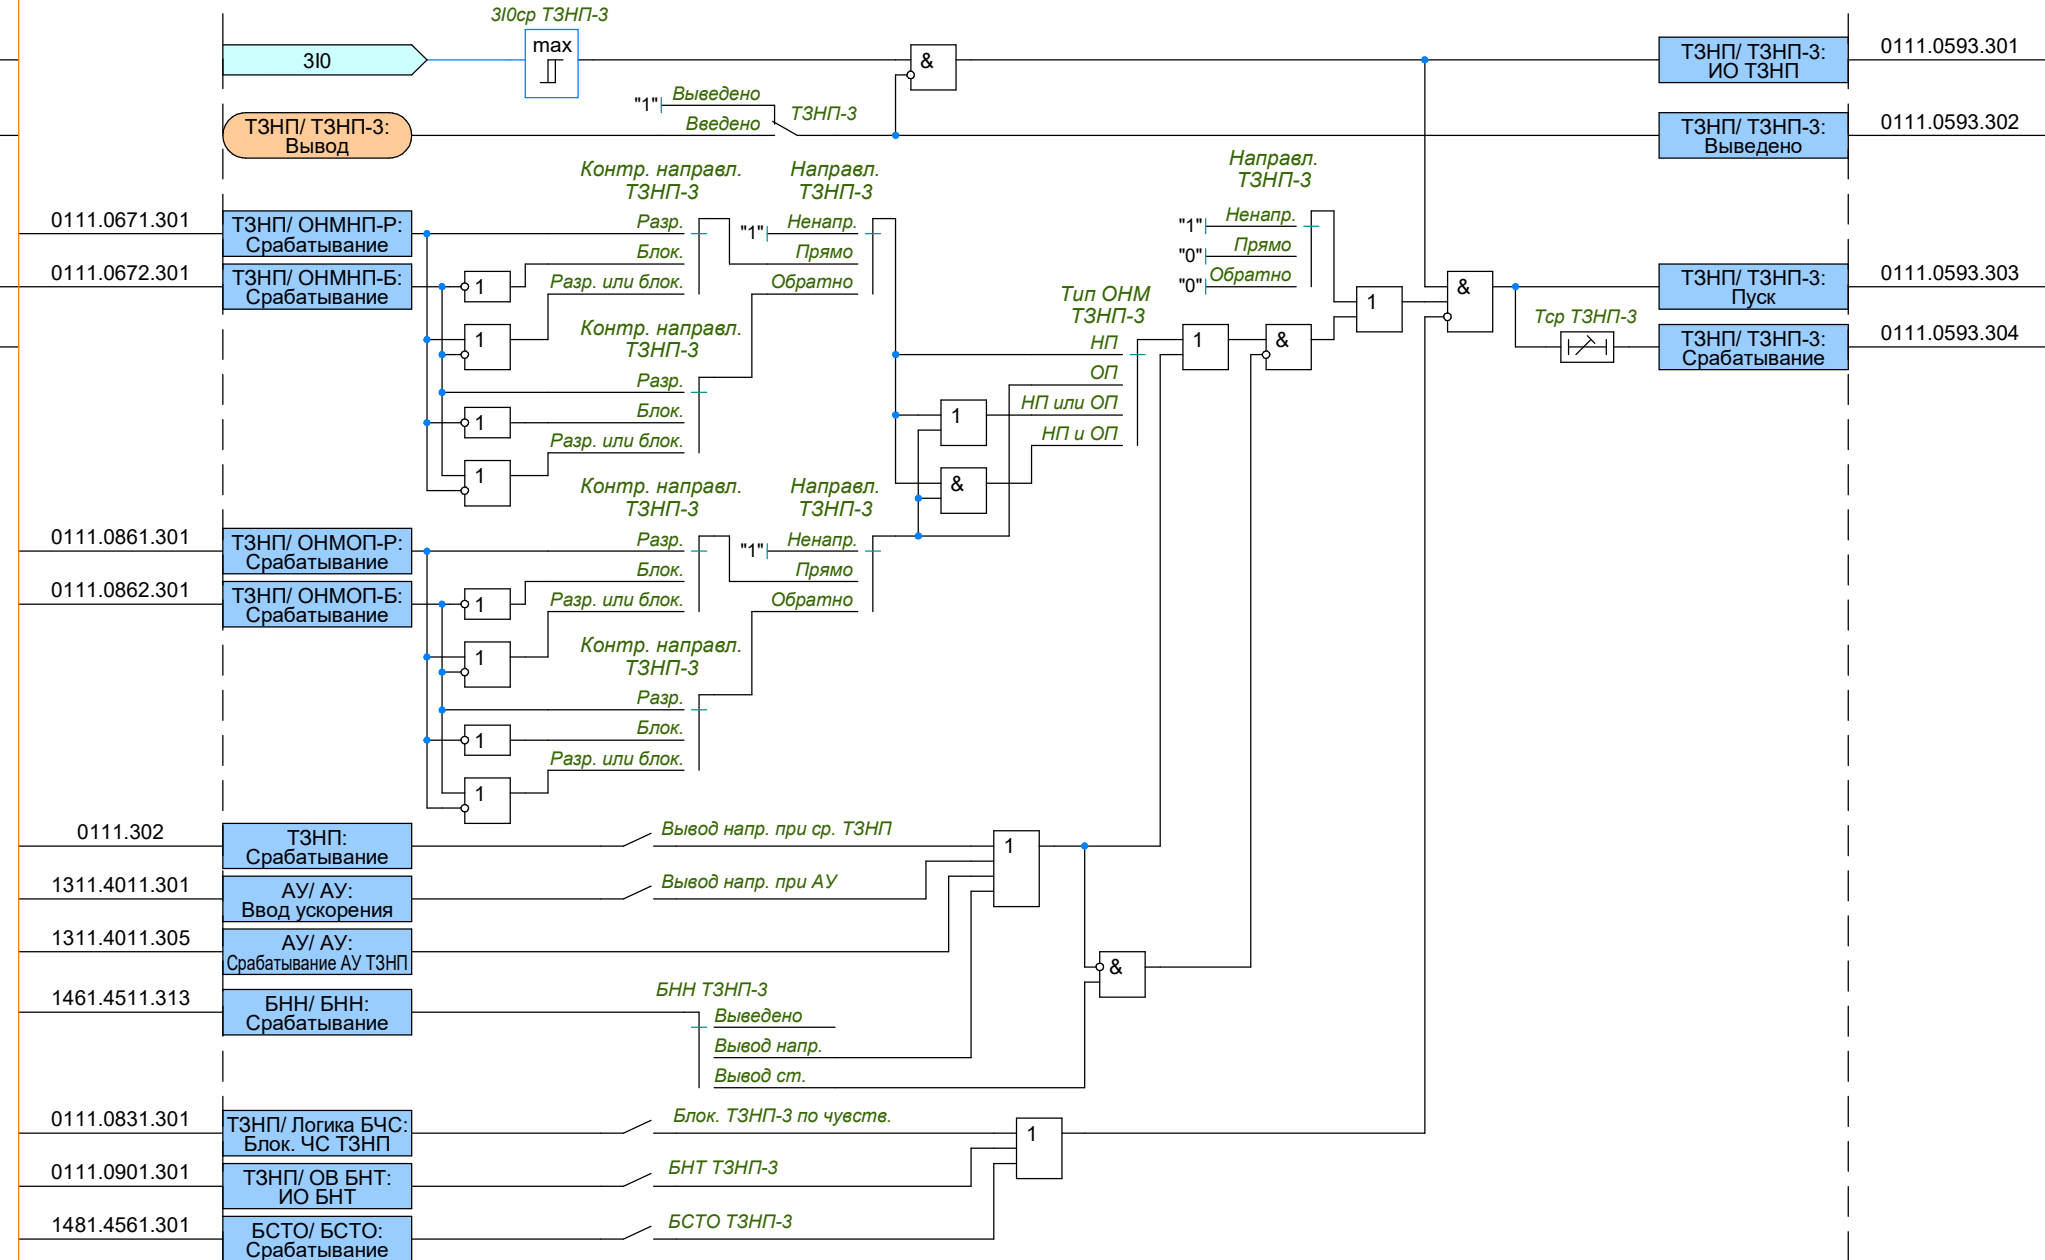


ТЗНП-4 0594

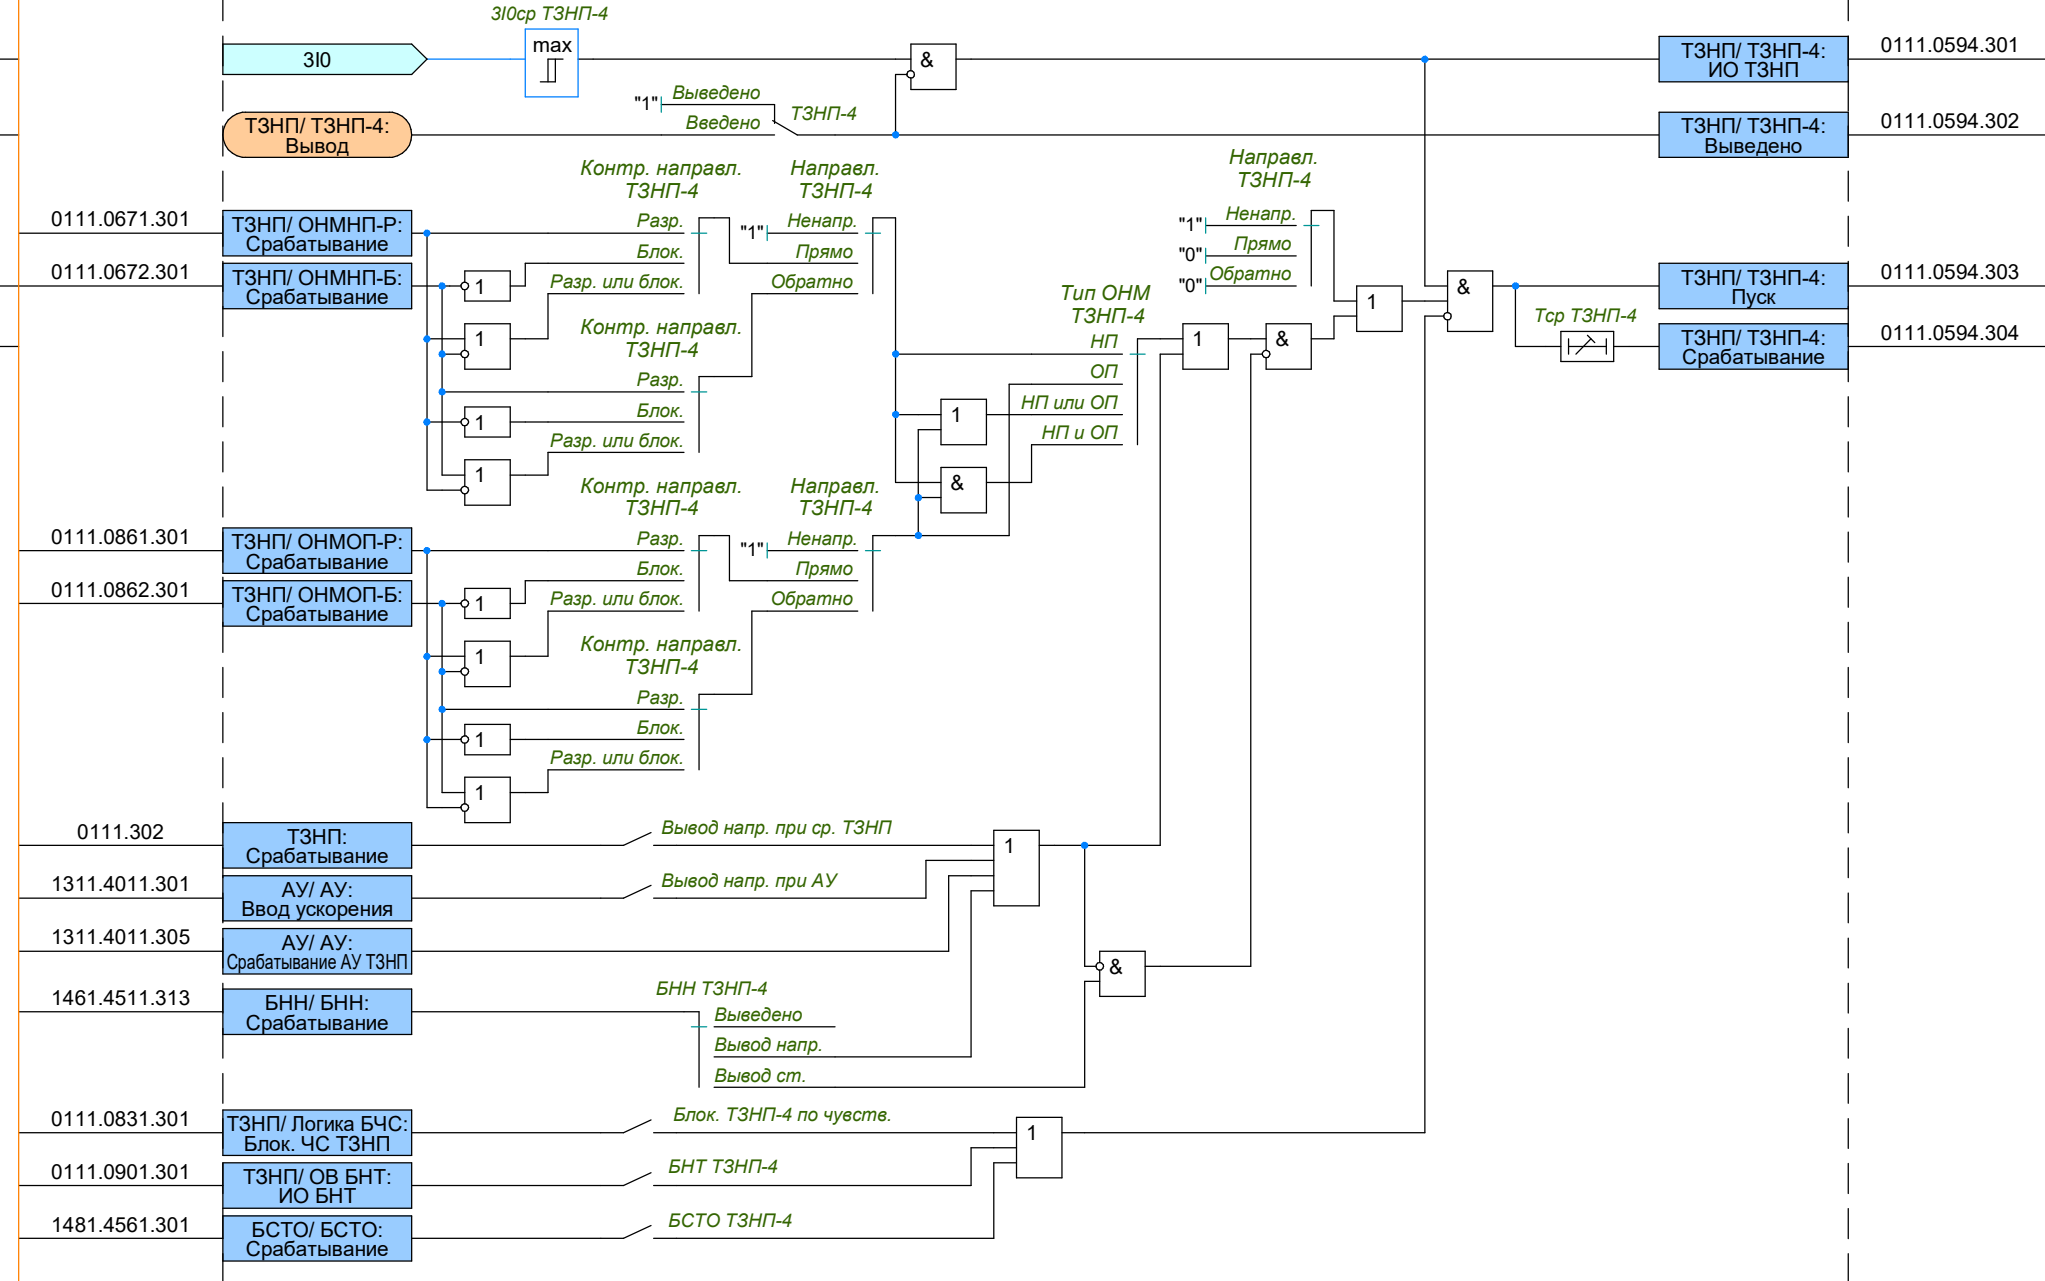


ТЗНП 0111

ТЗНП-5 0595

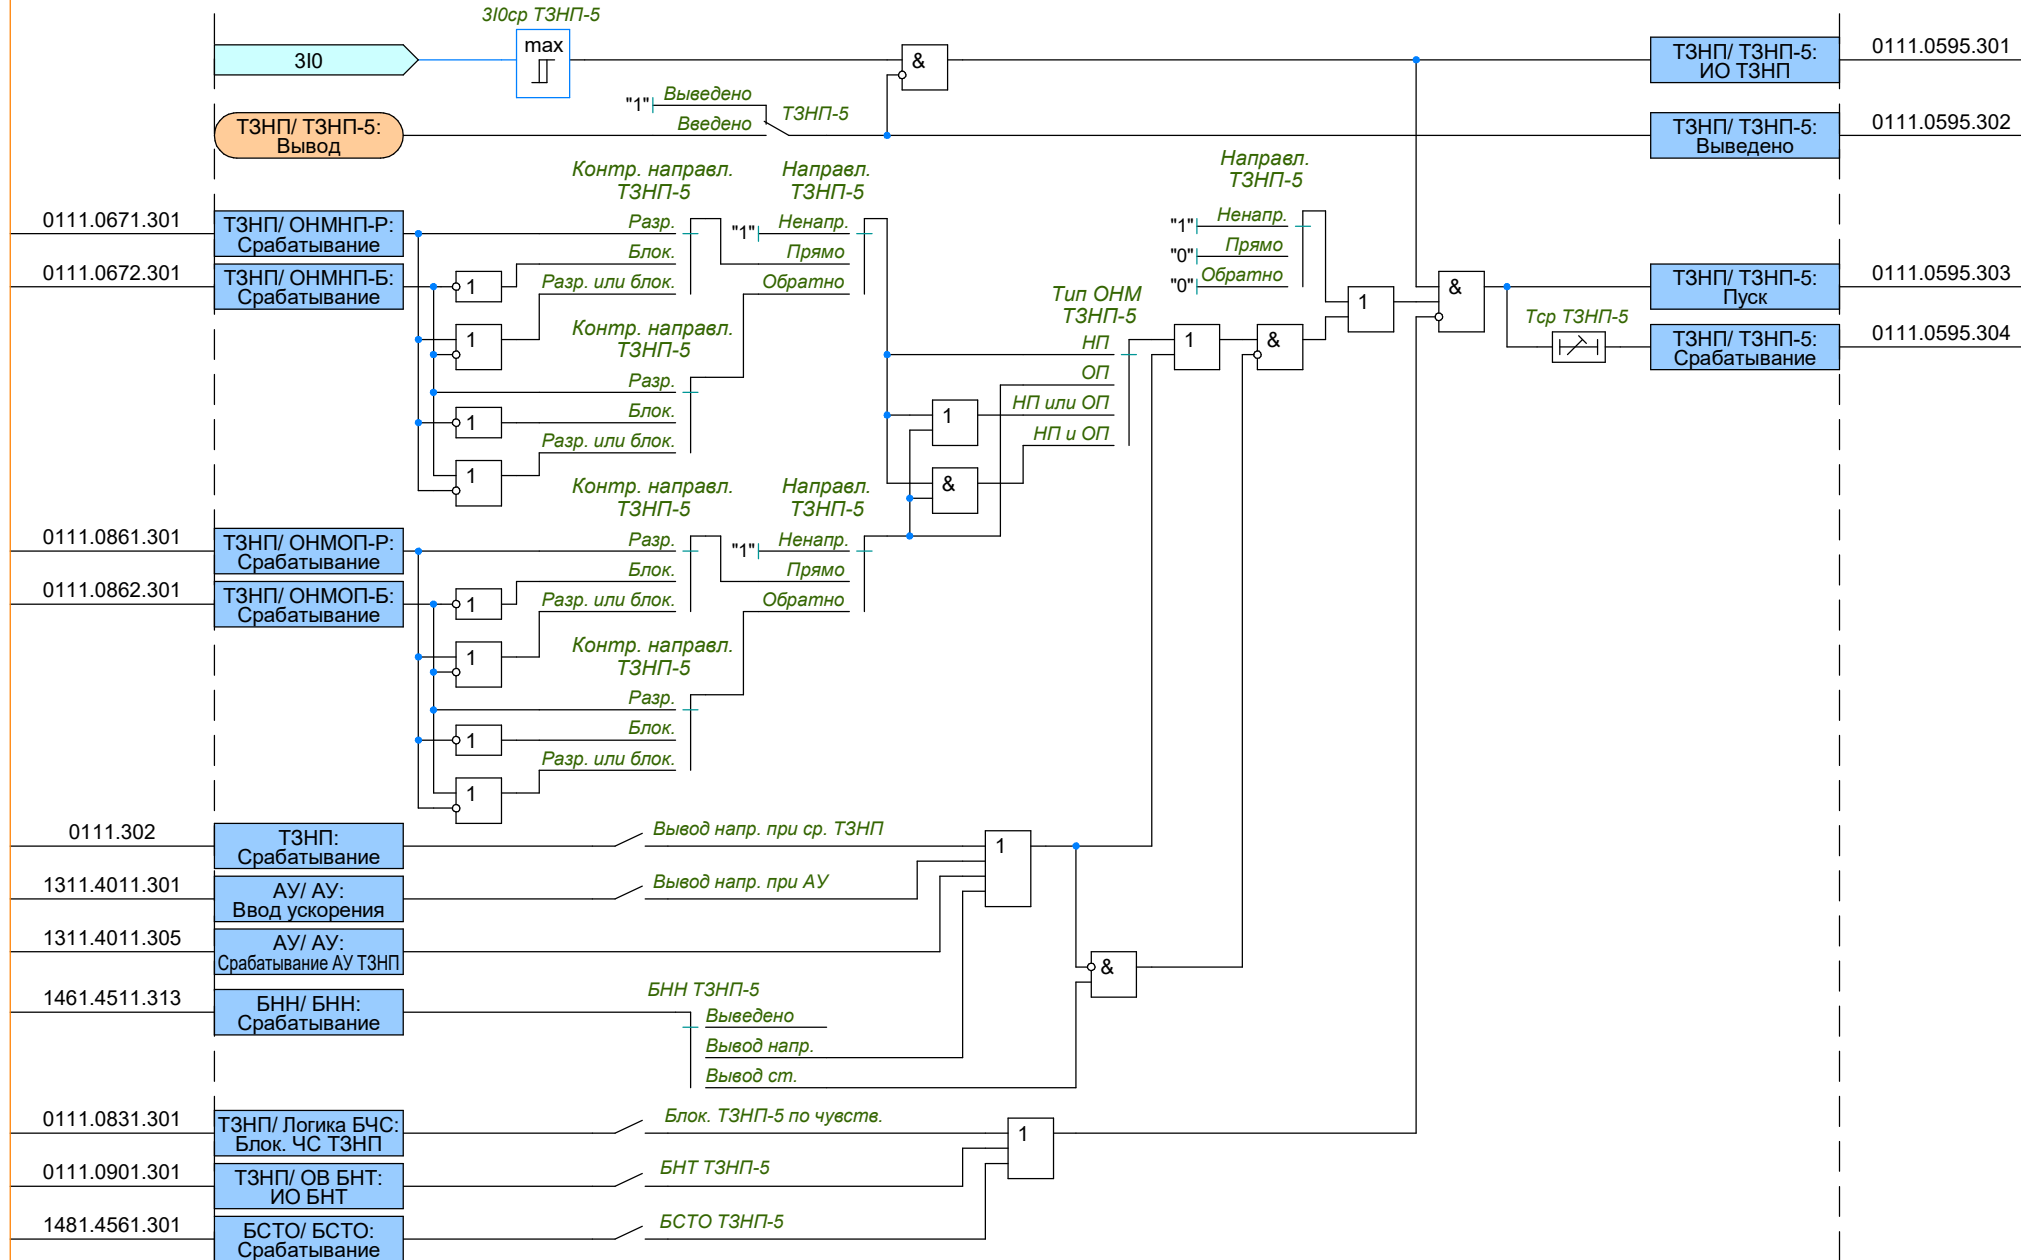


ТЗНП-6 0596

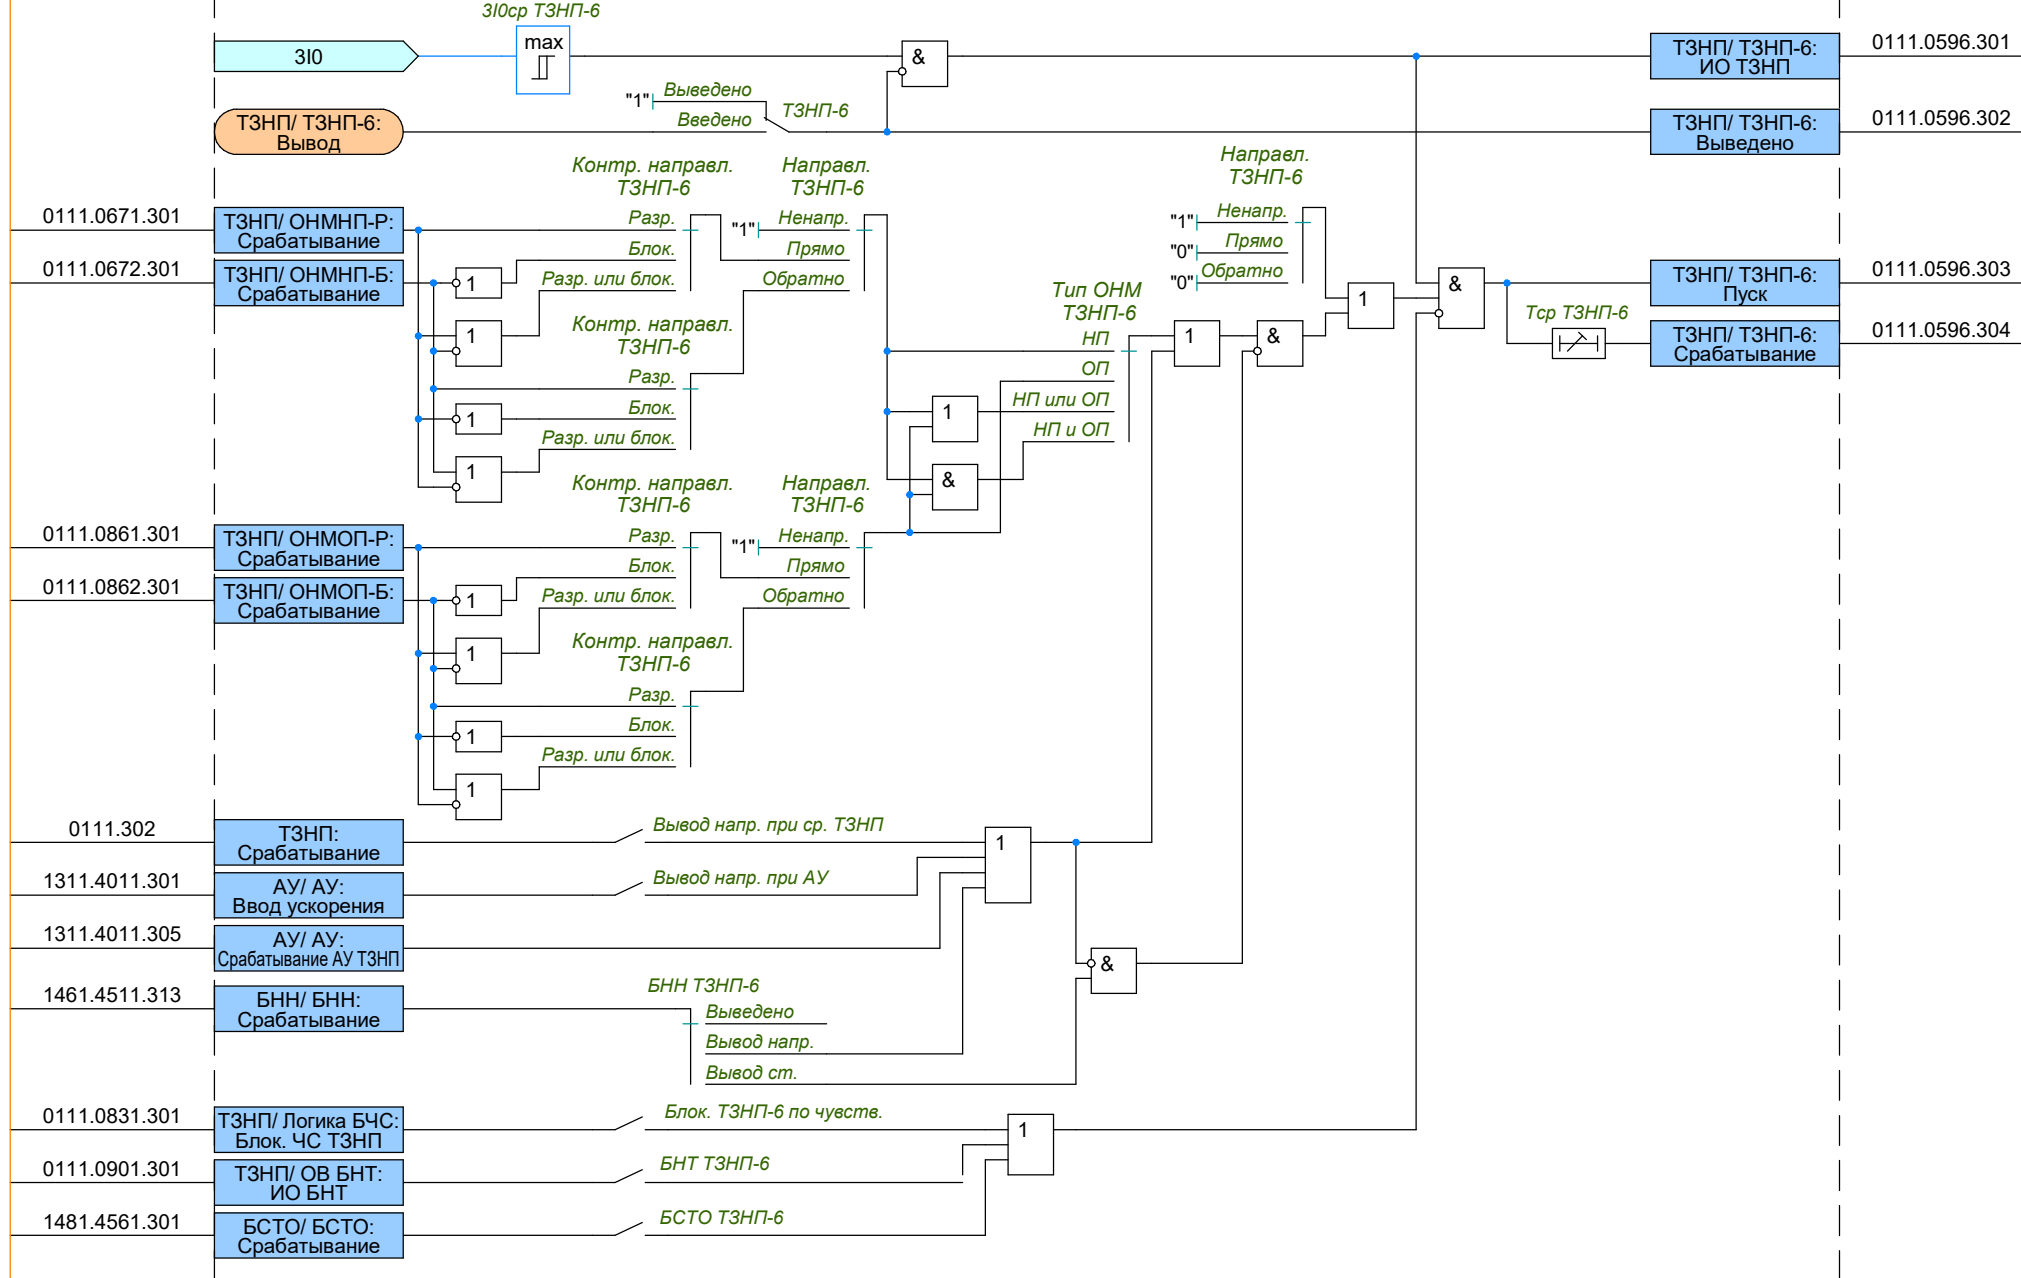


ТЗНП 0111

АУ ТЗНП 0731


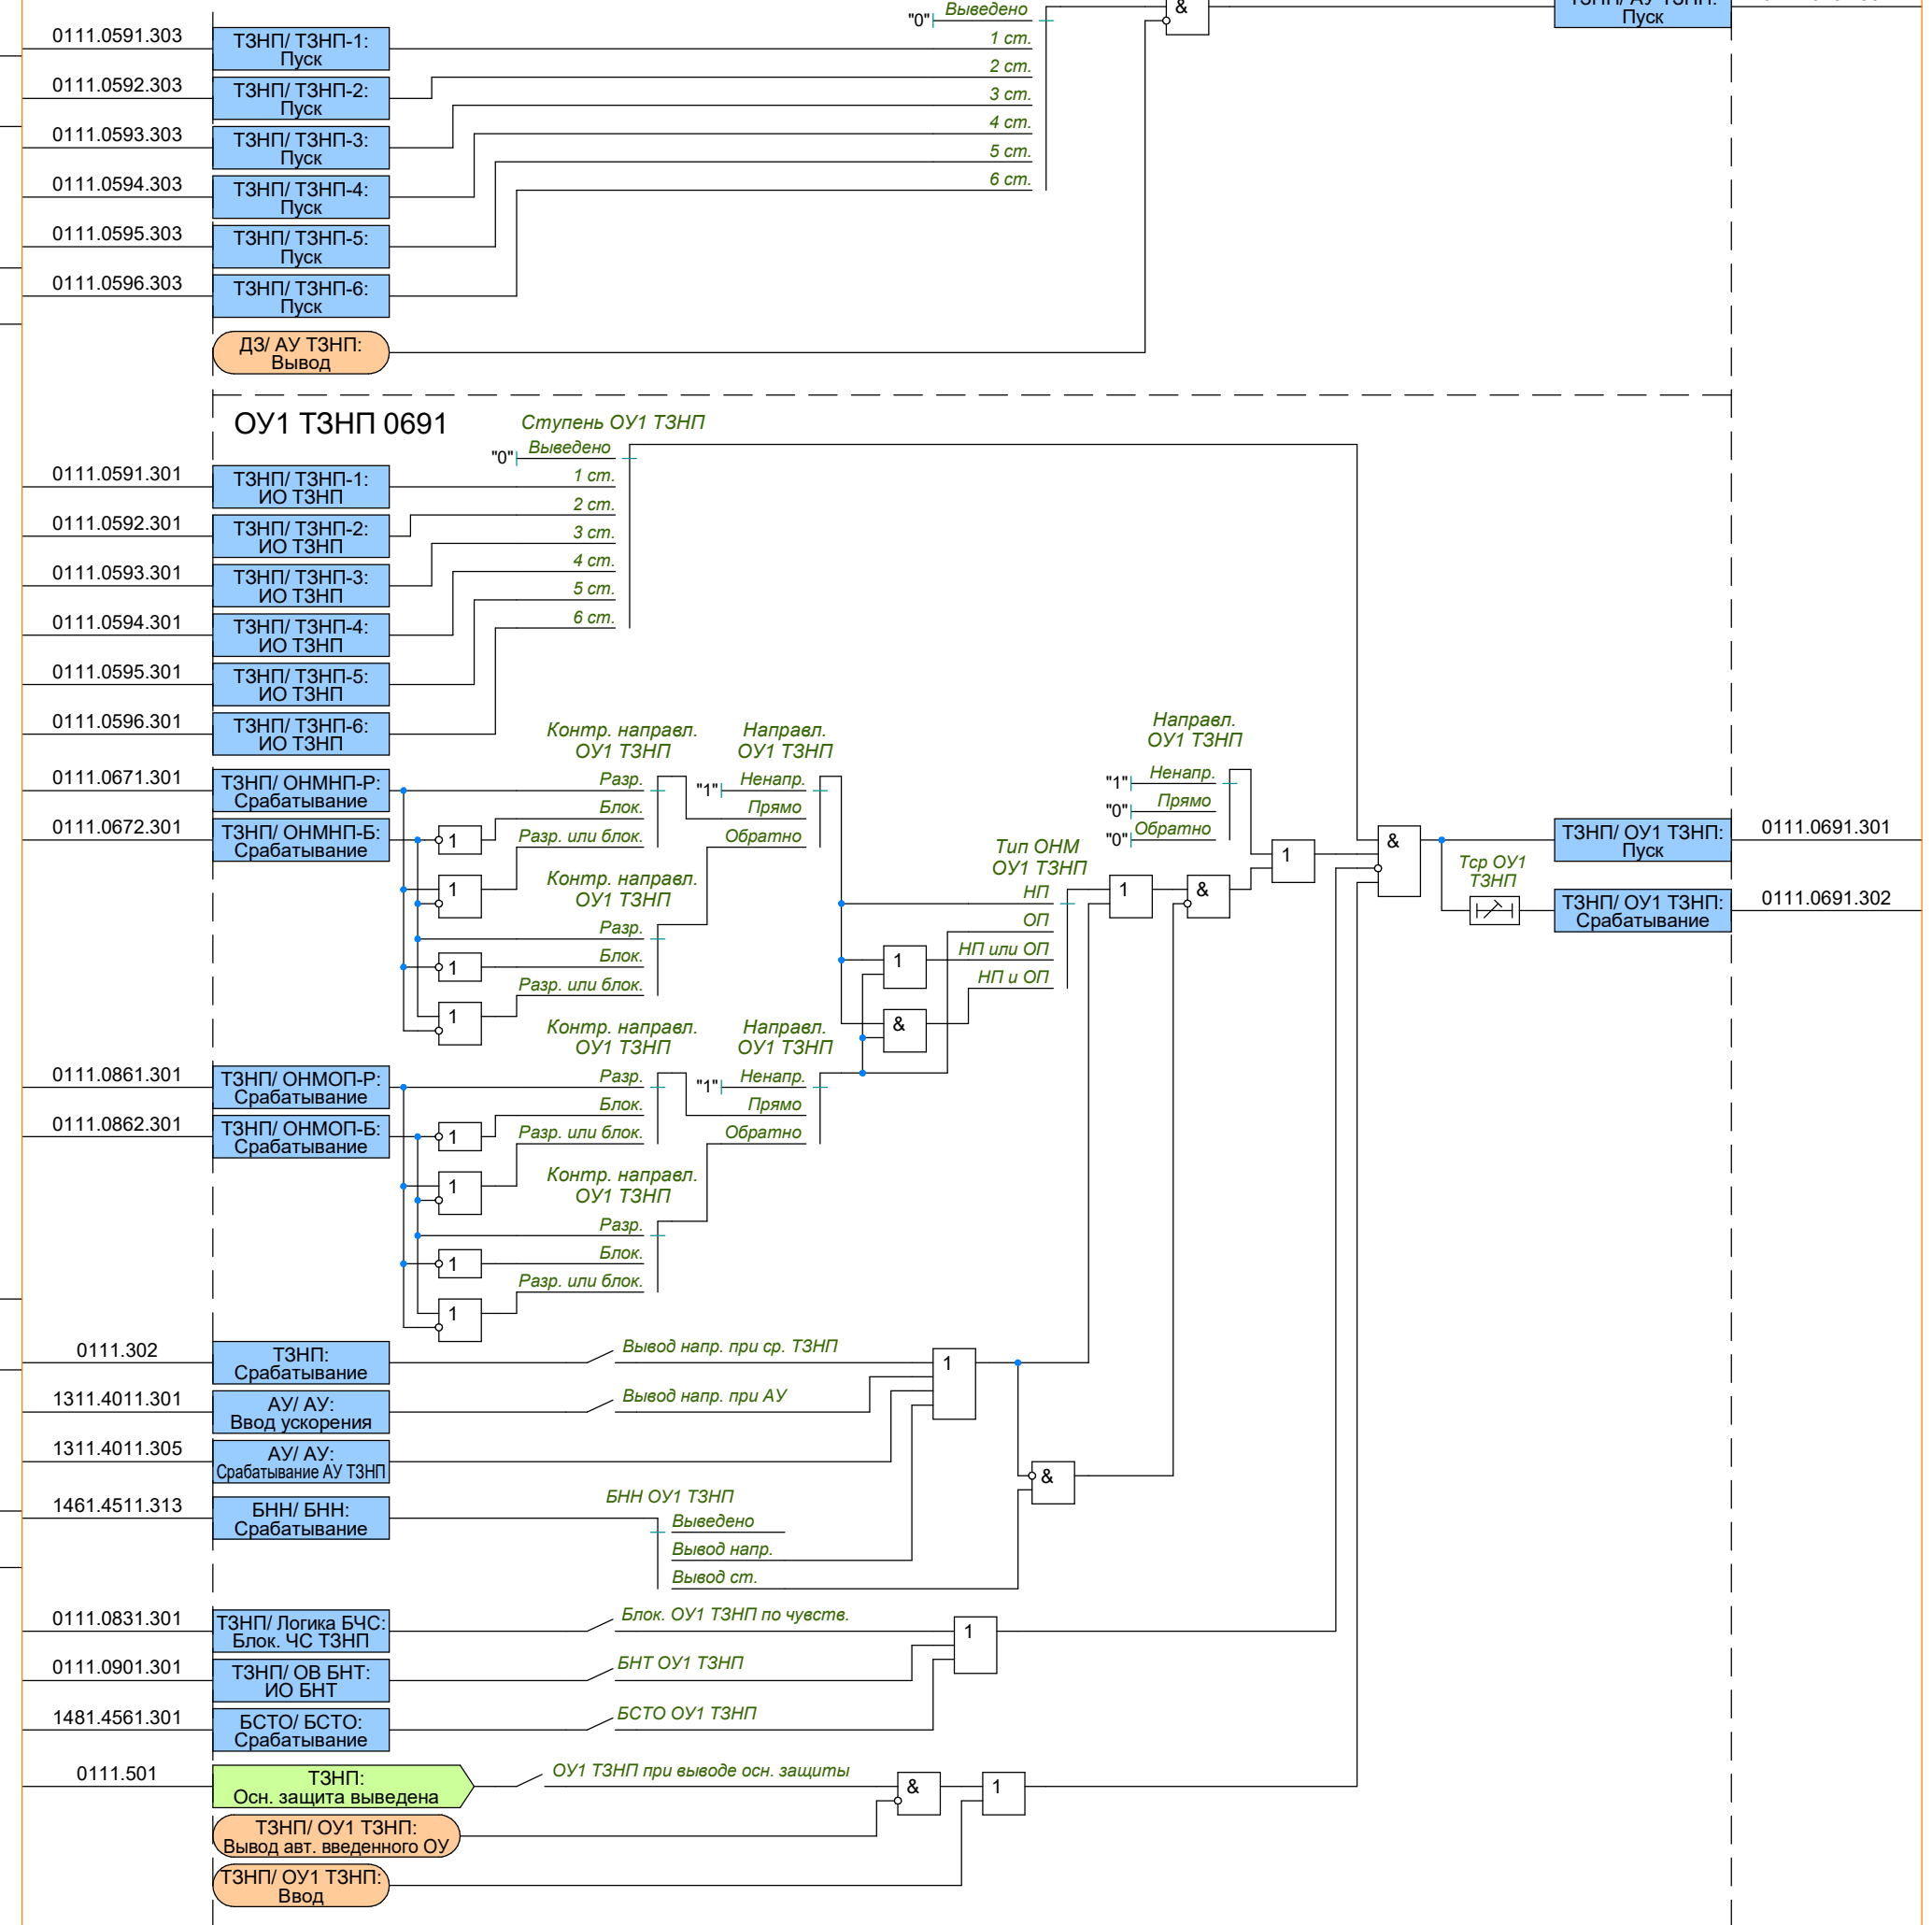


ТЗО 0181

ТЗО-Ф 0841



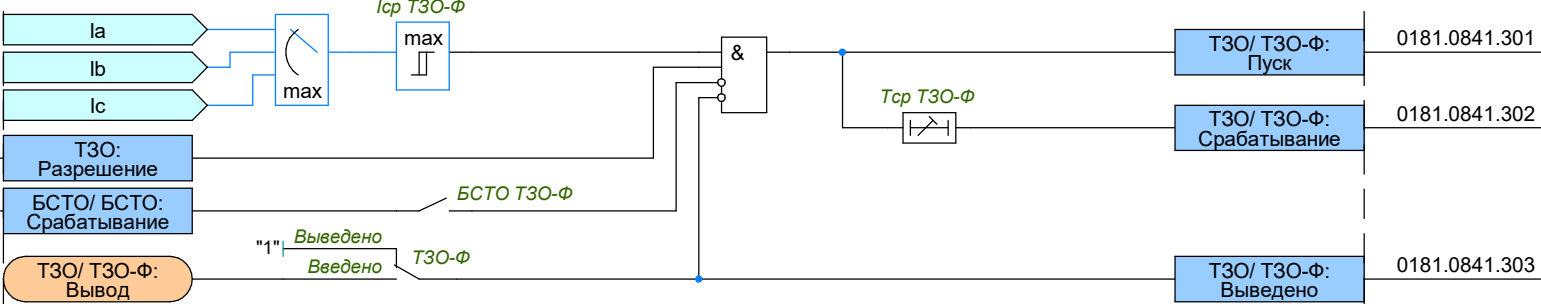


ТЗО-НП 0911

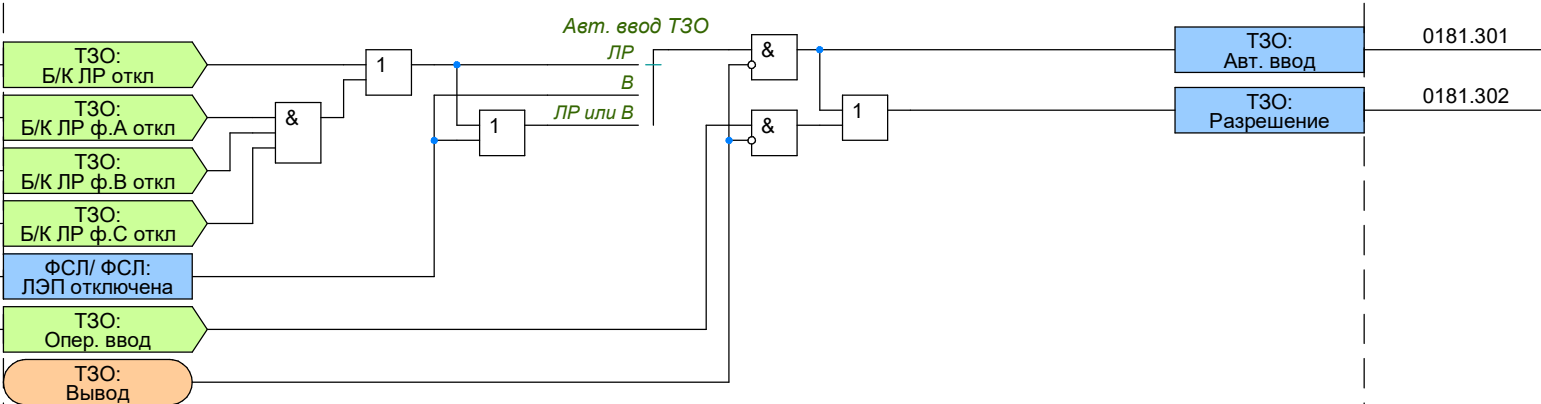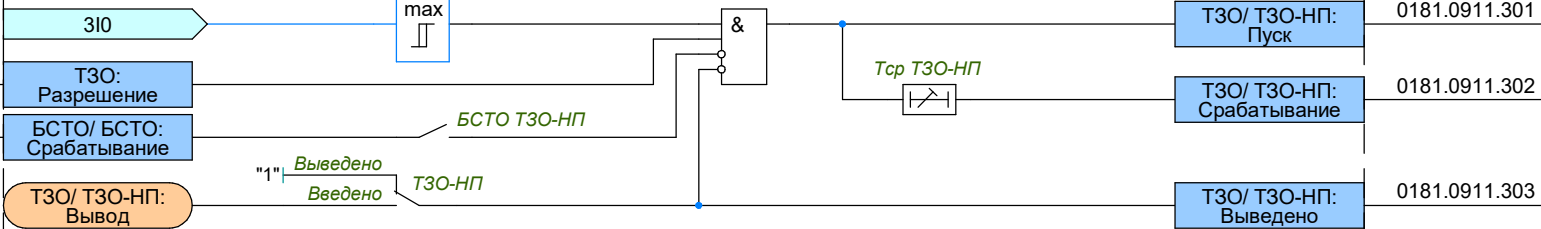


ЗНР 0421

ЗНР 1011

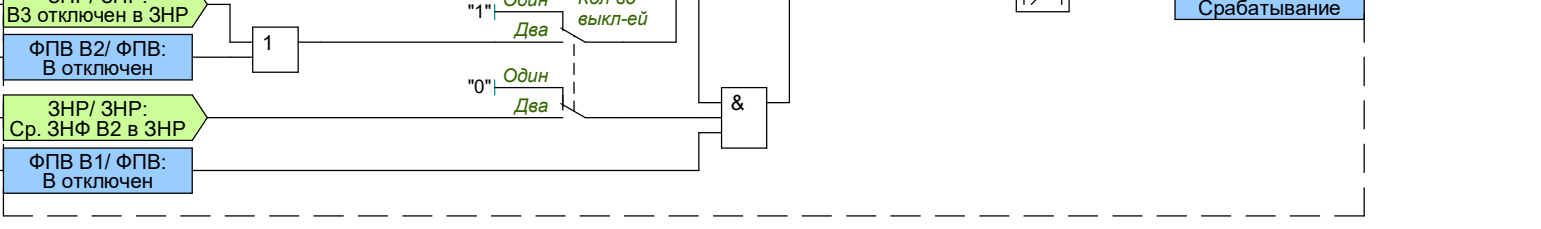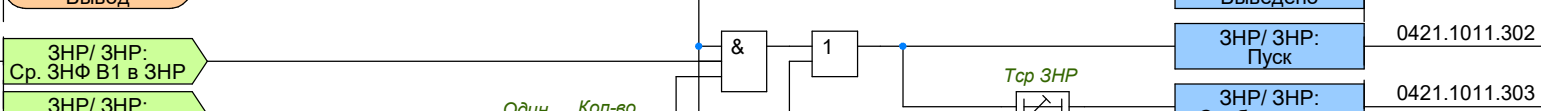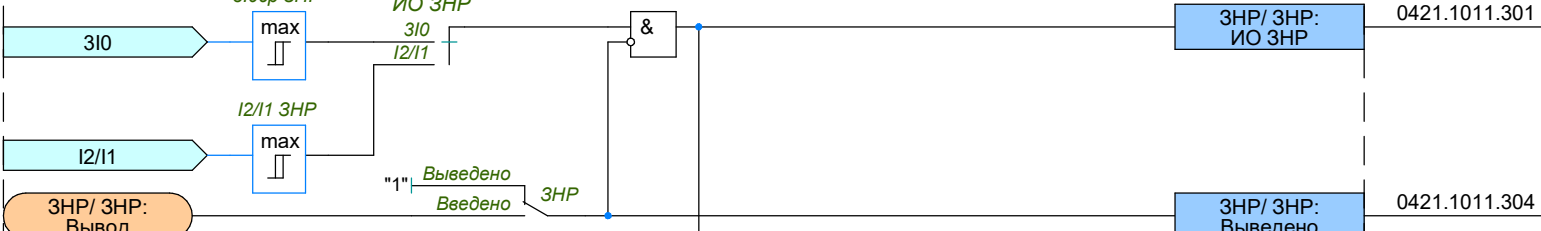


ЗНФ В1 3511

ЗНФ (6841)

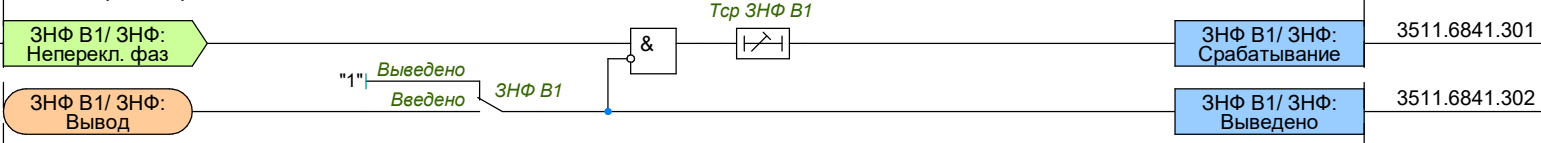







ЗНФ В2 3512

ЗНФ (6841)

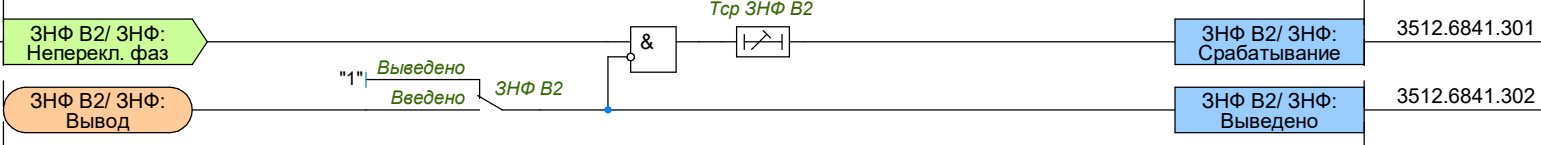


БНН 1461

БНН 4511

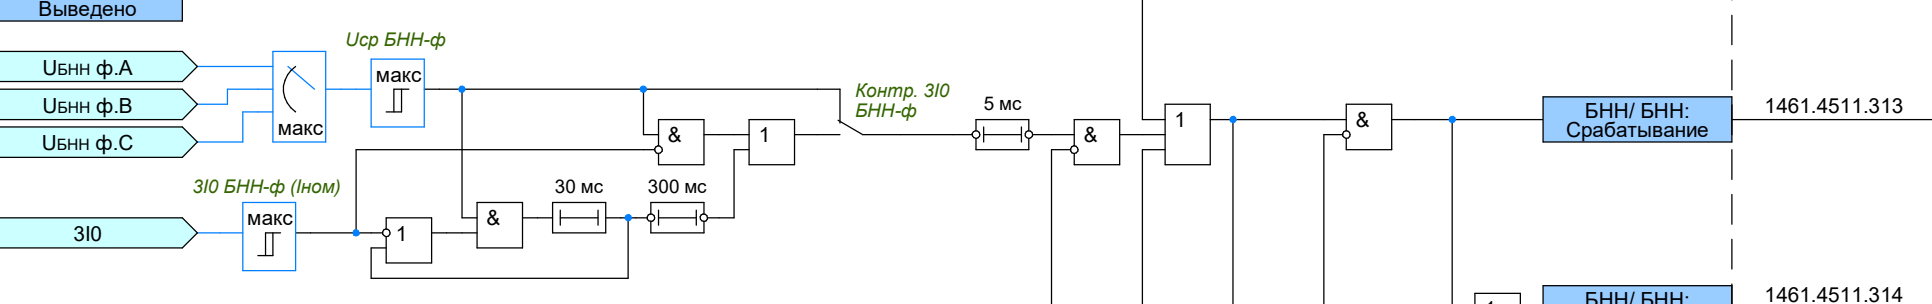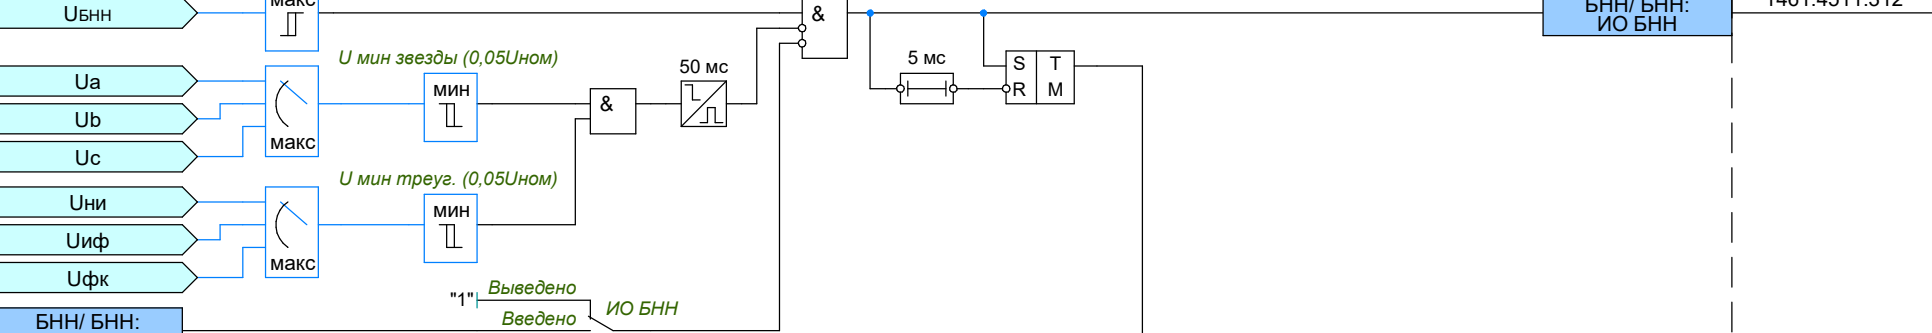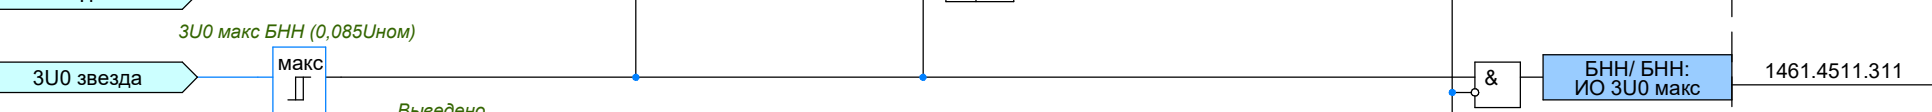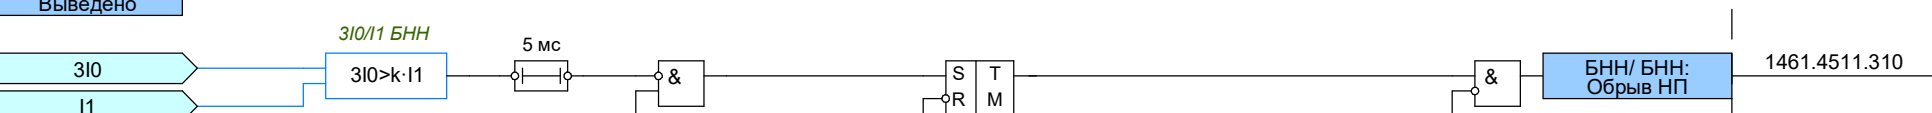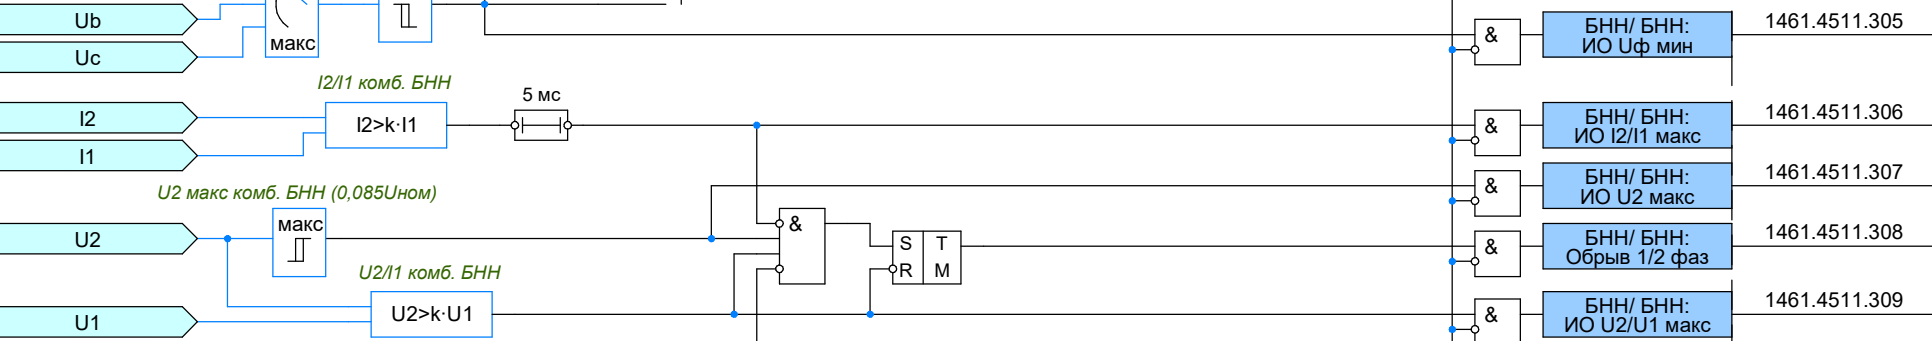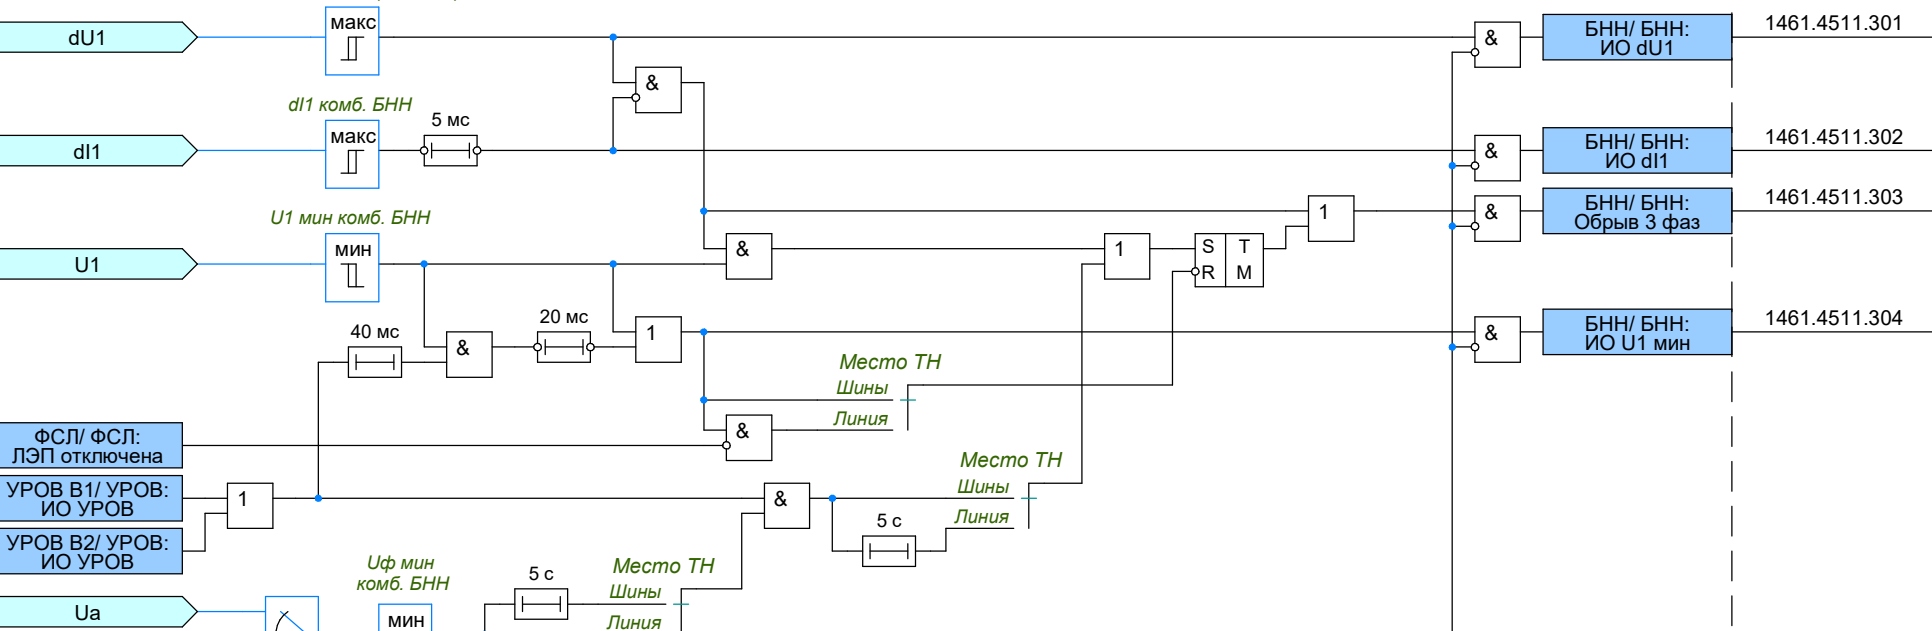


ЛС (Логика связи) 1711

Тоткл (Телеотключение) 5011

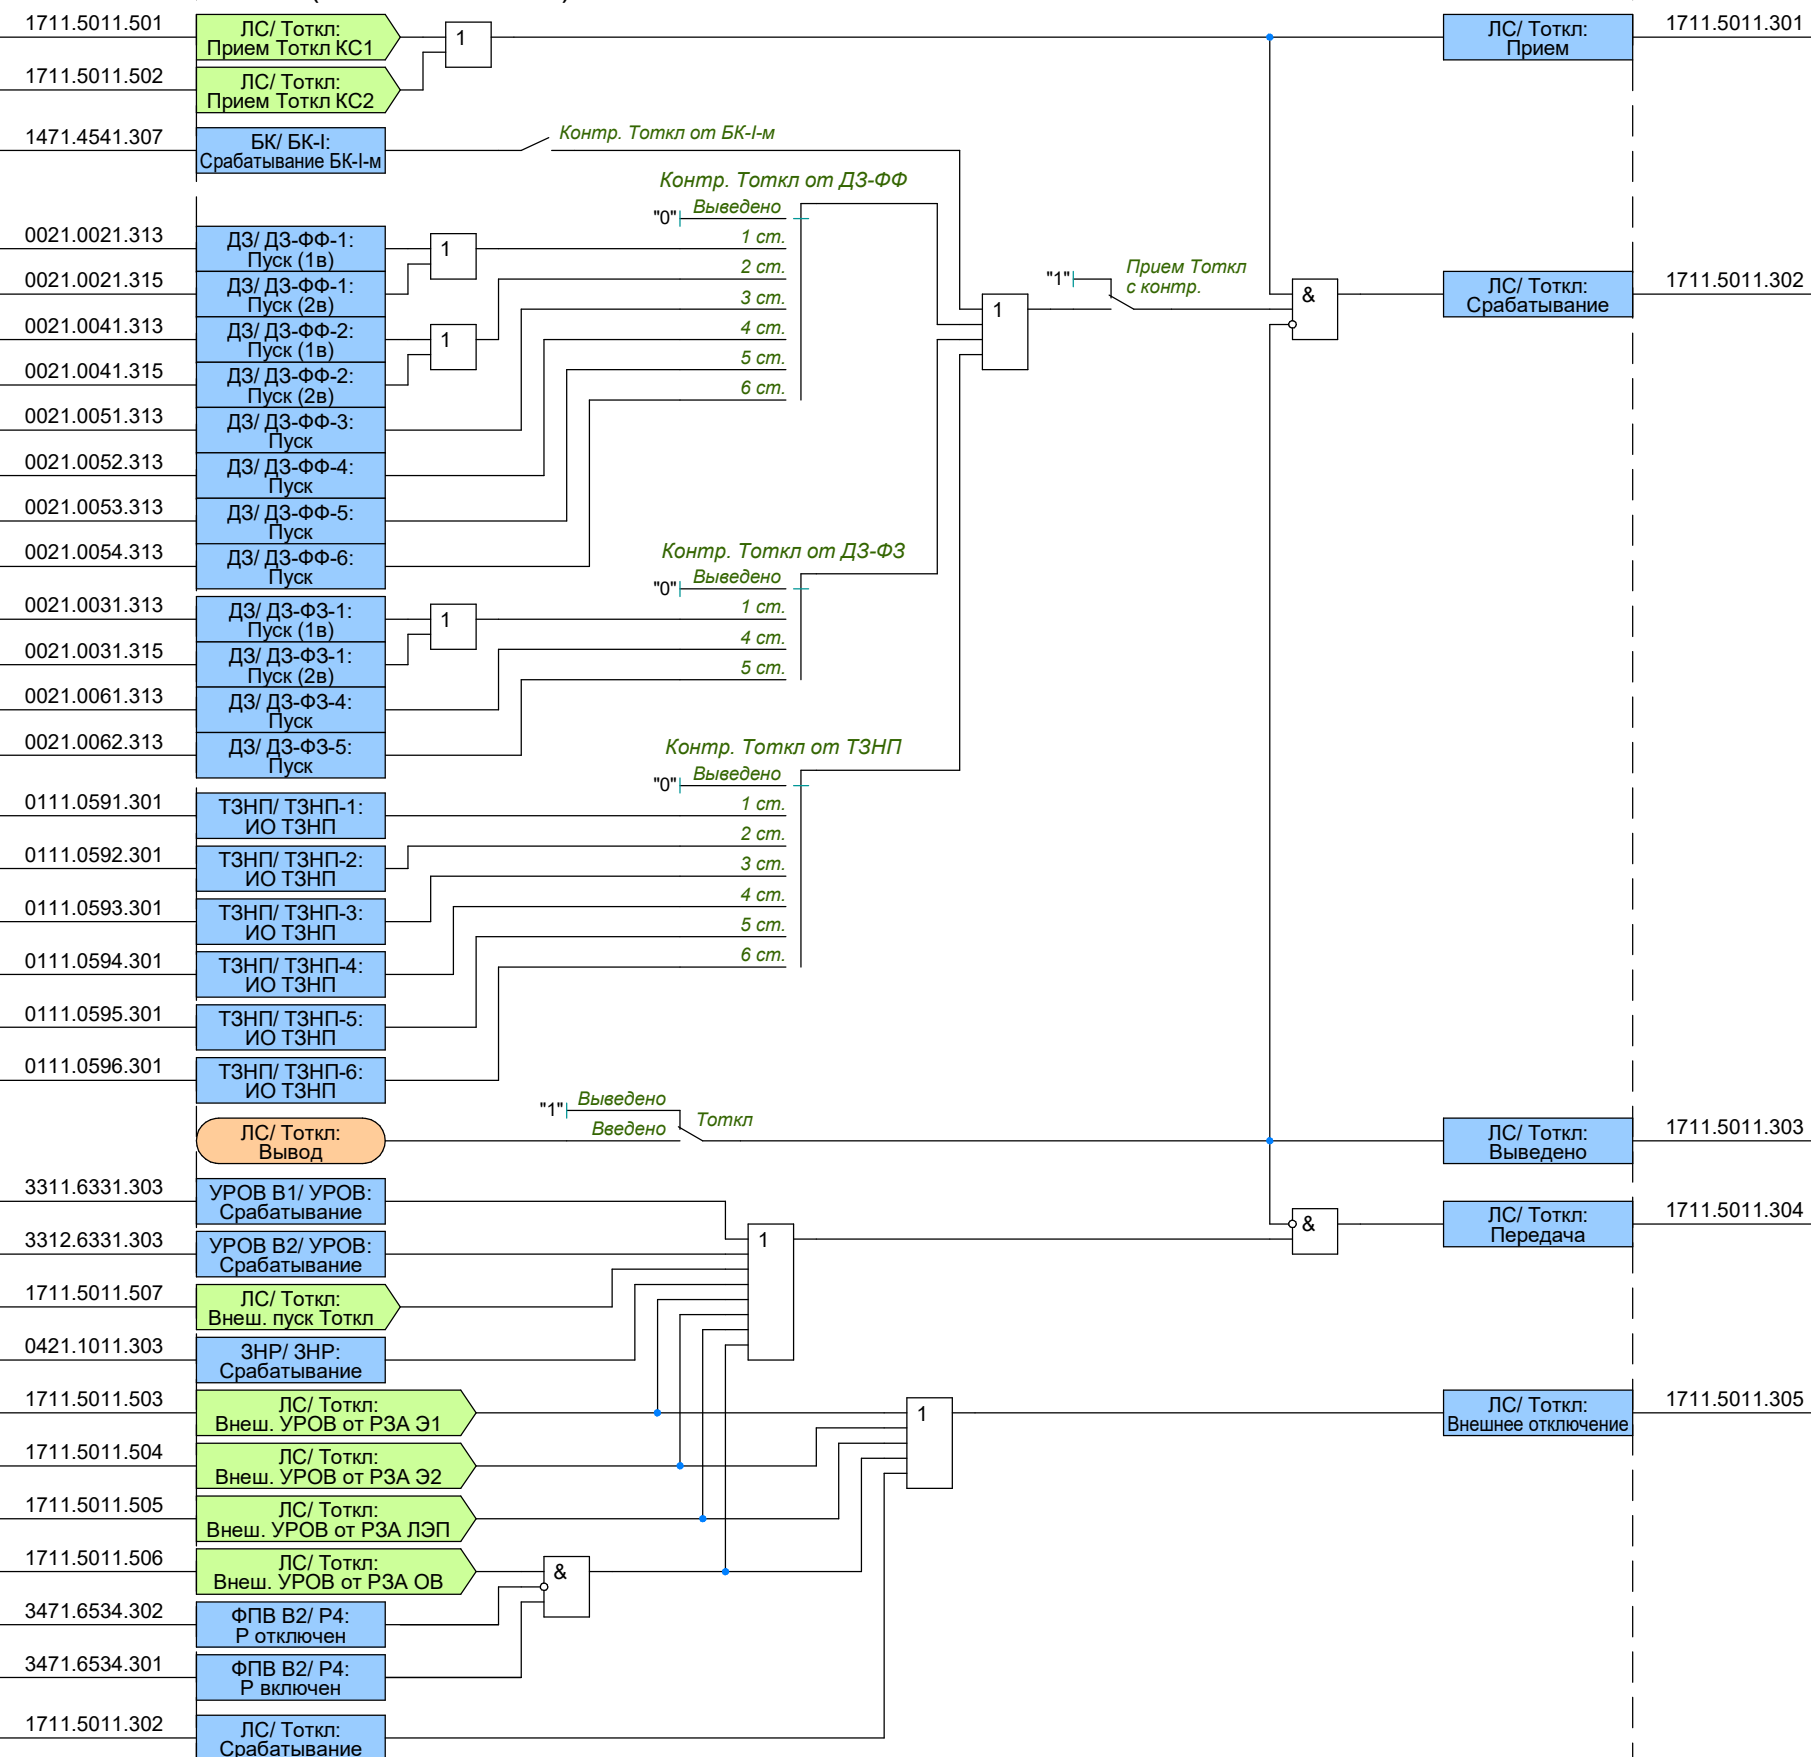


ТУ ОТФ 5021

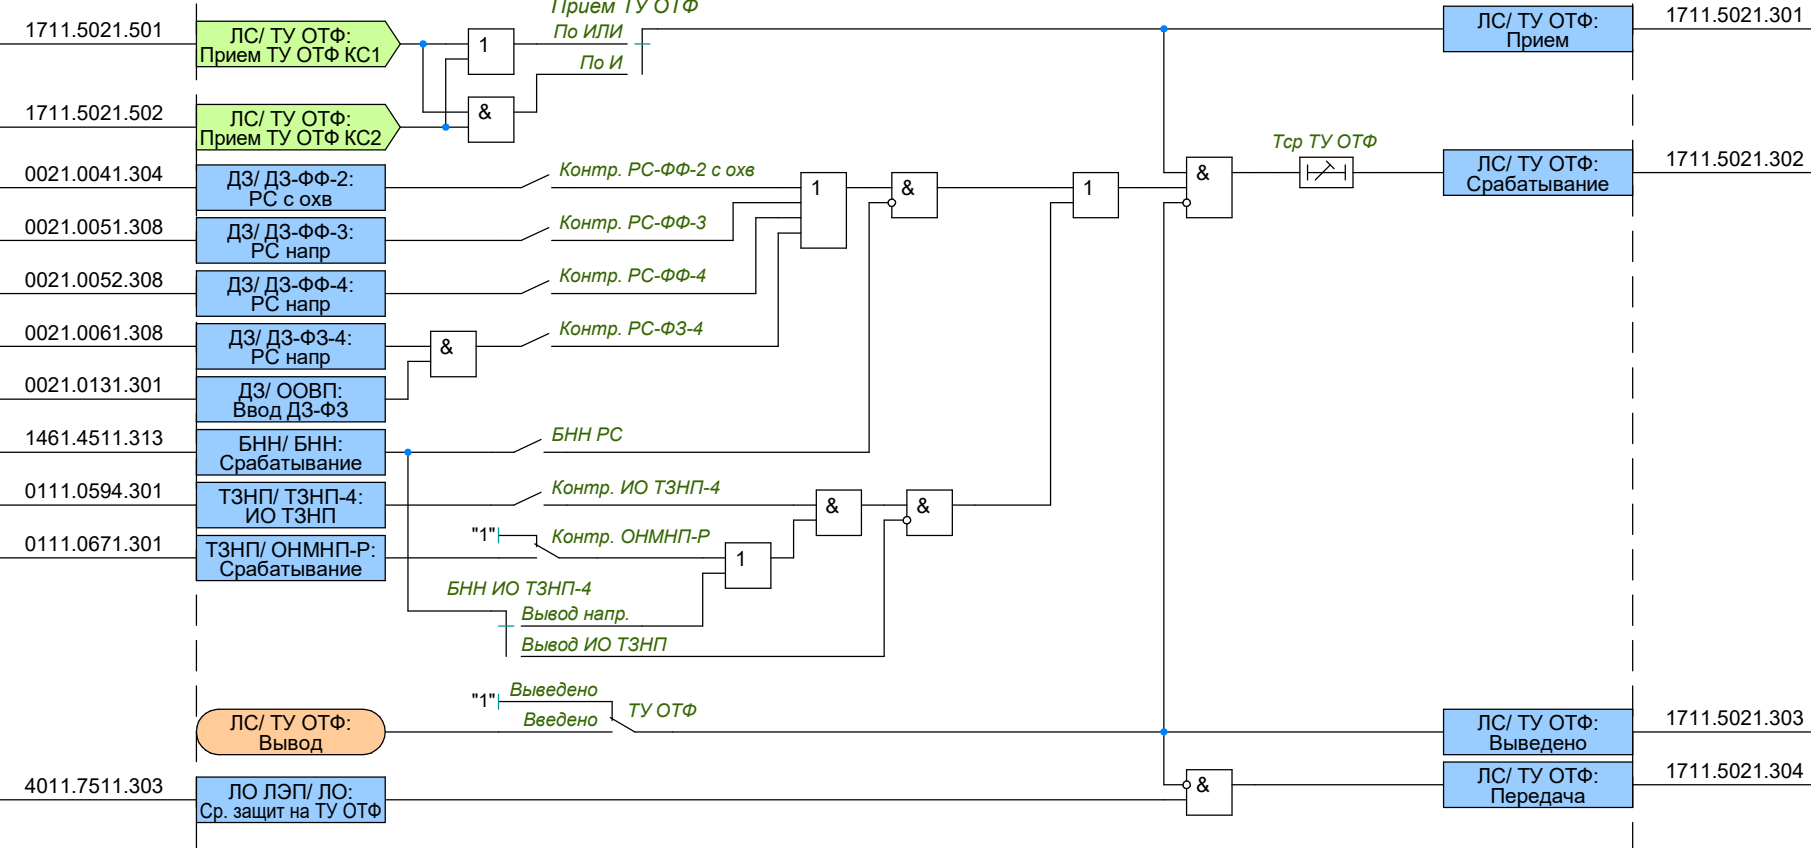


ЛС (Логика связи) 1711

ТУ ДЗ 5031

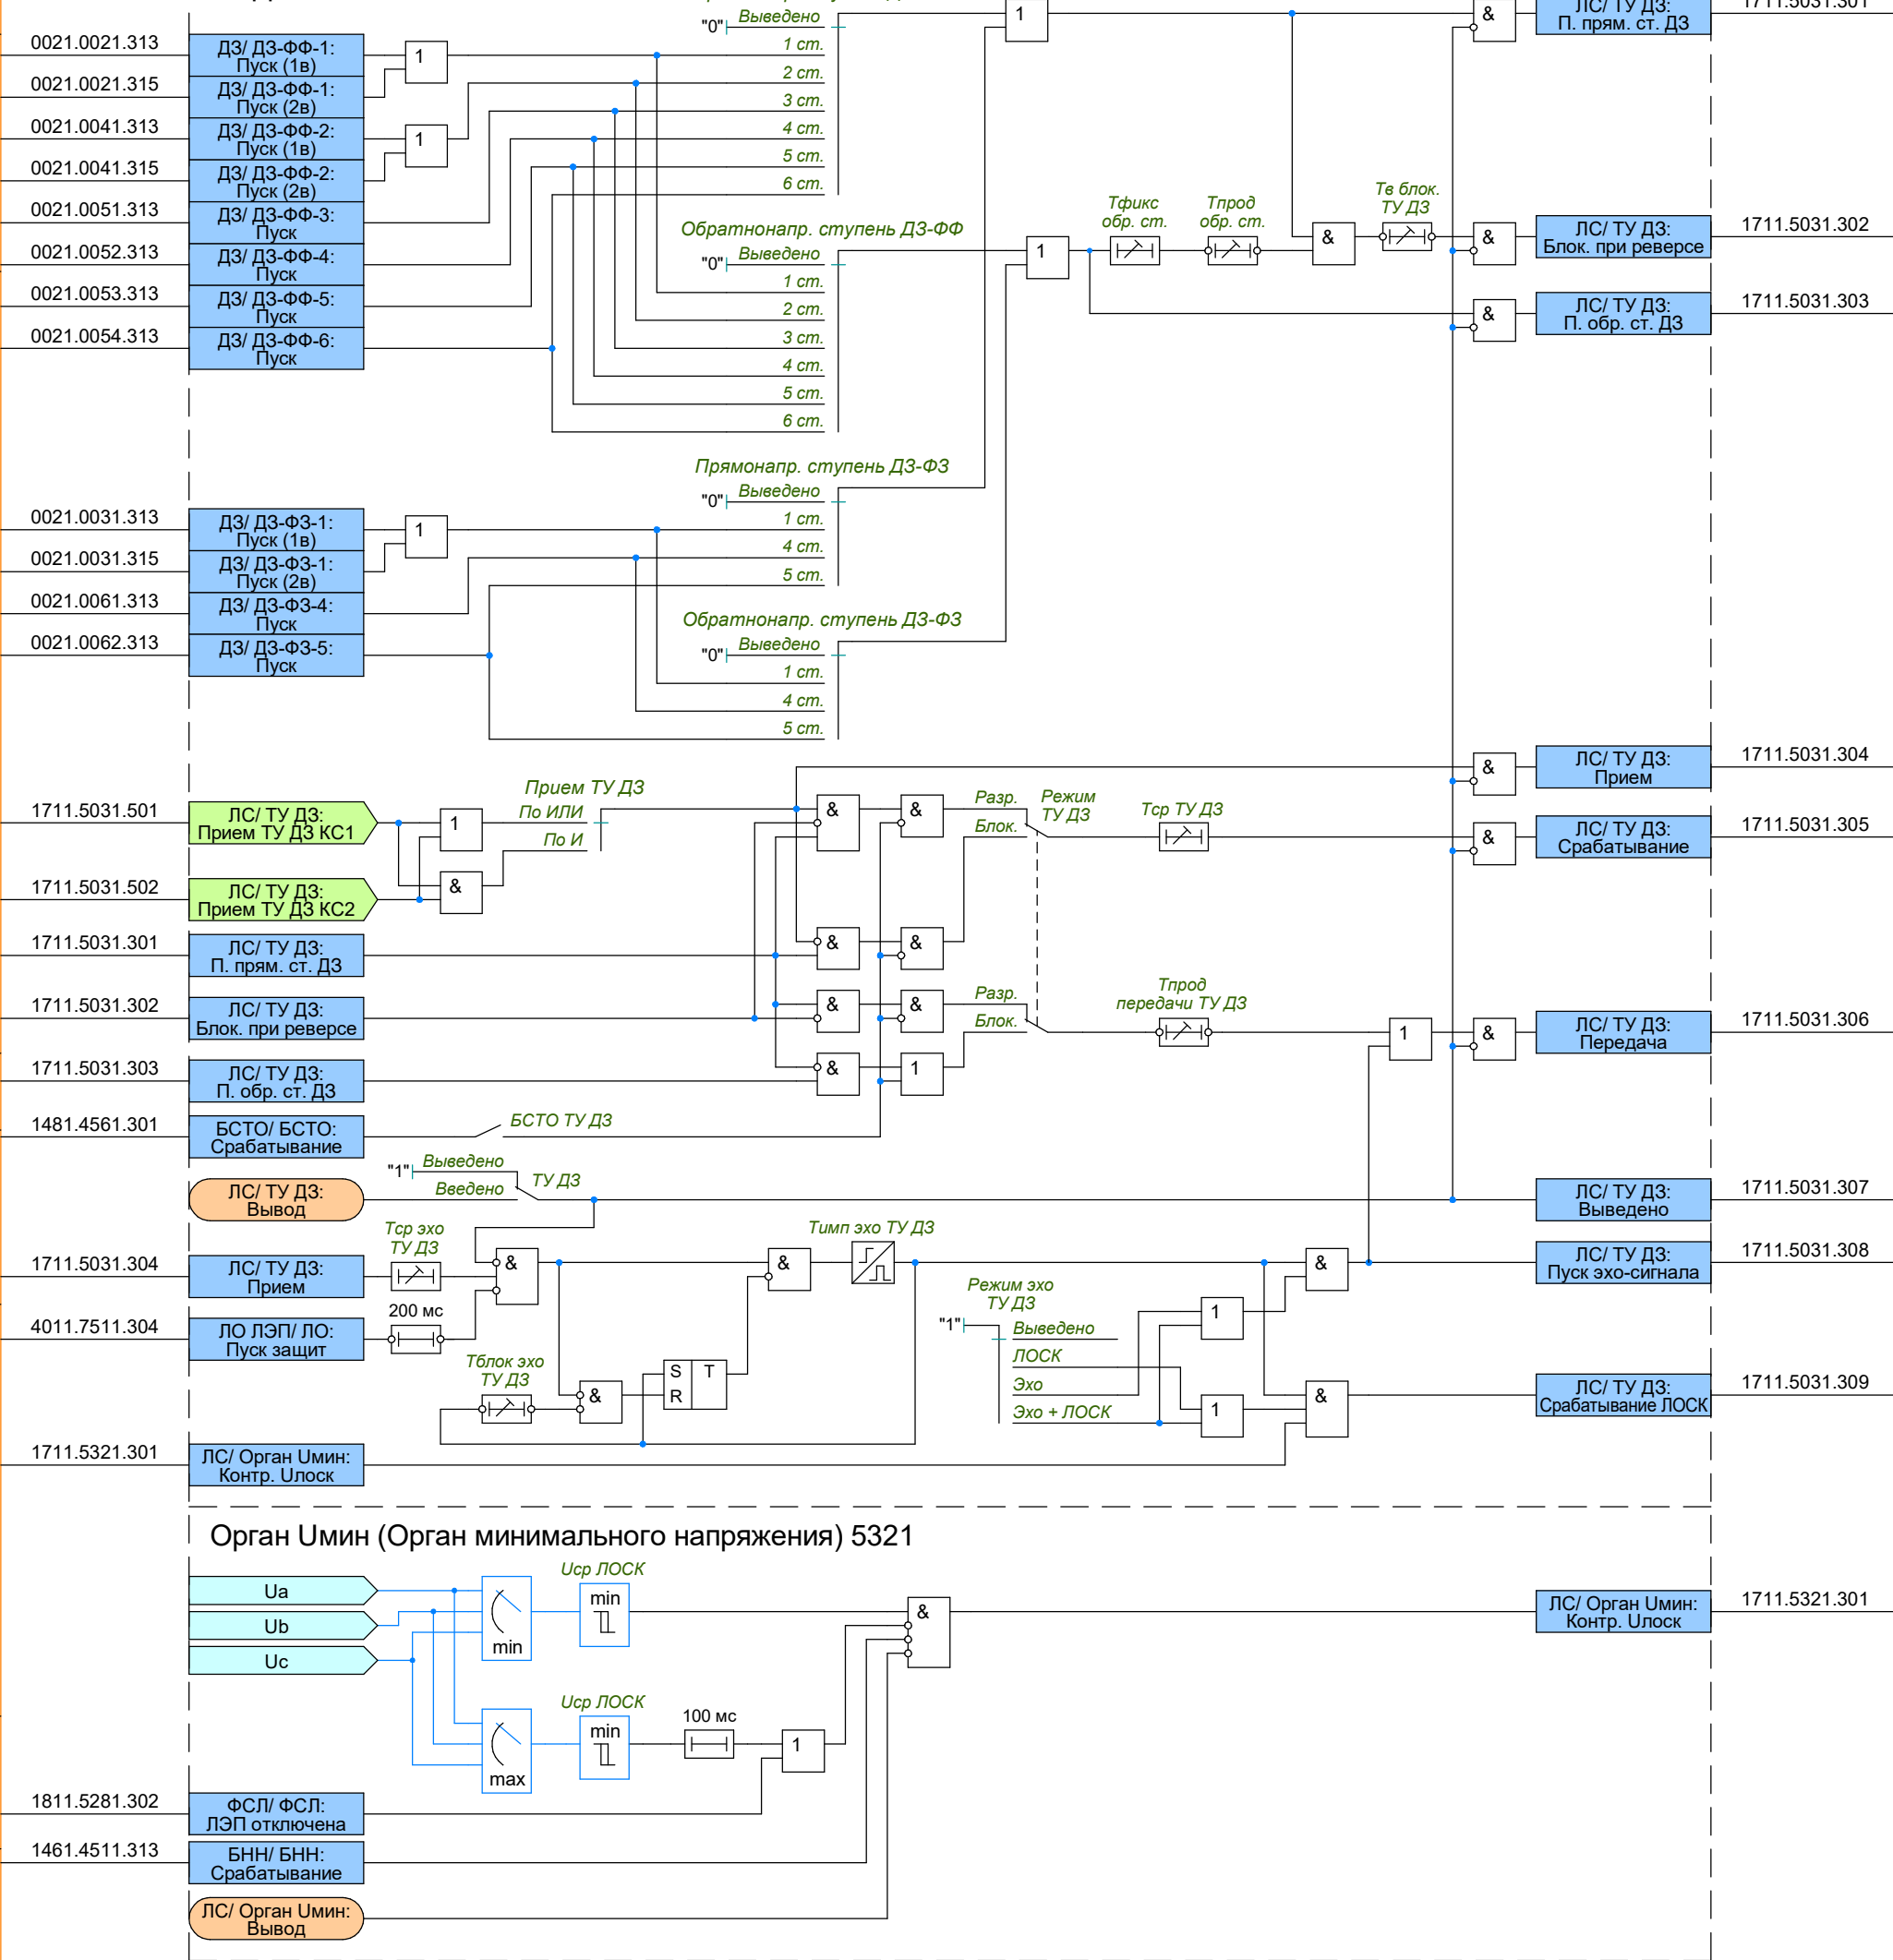


ЛС (Логика связи) 1711

ТУ ТЗНП 5041

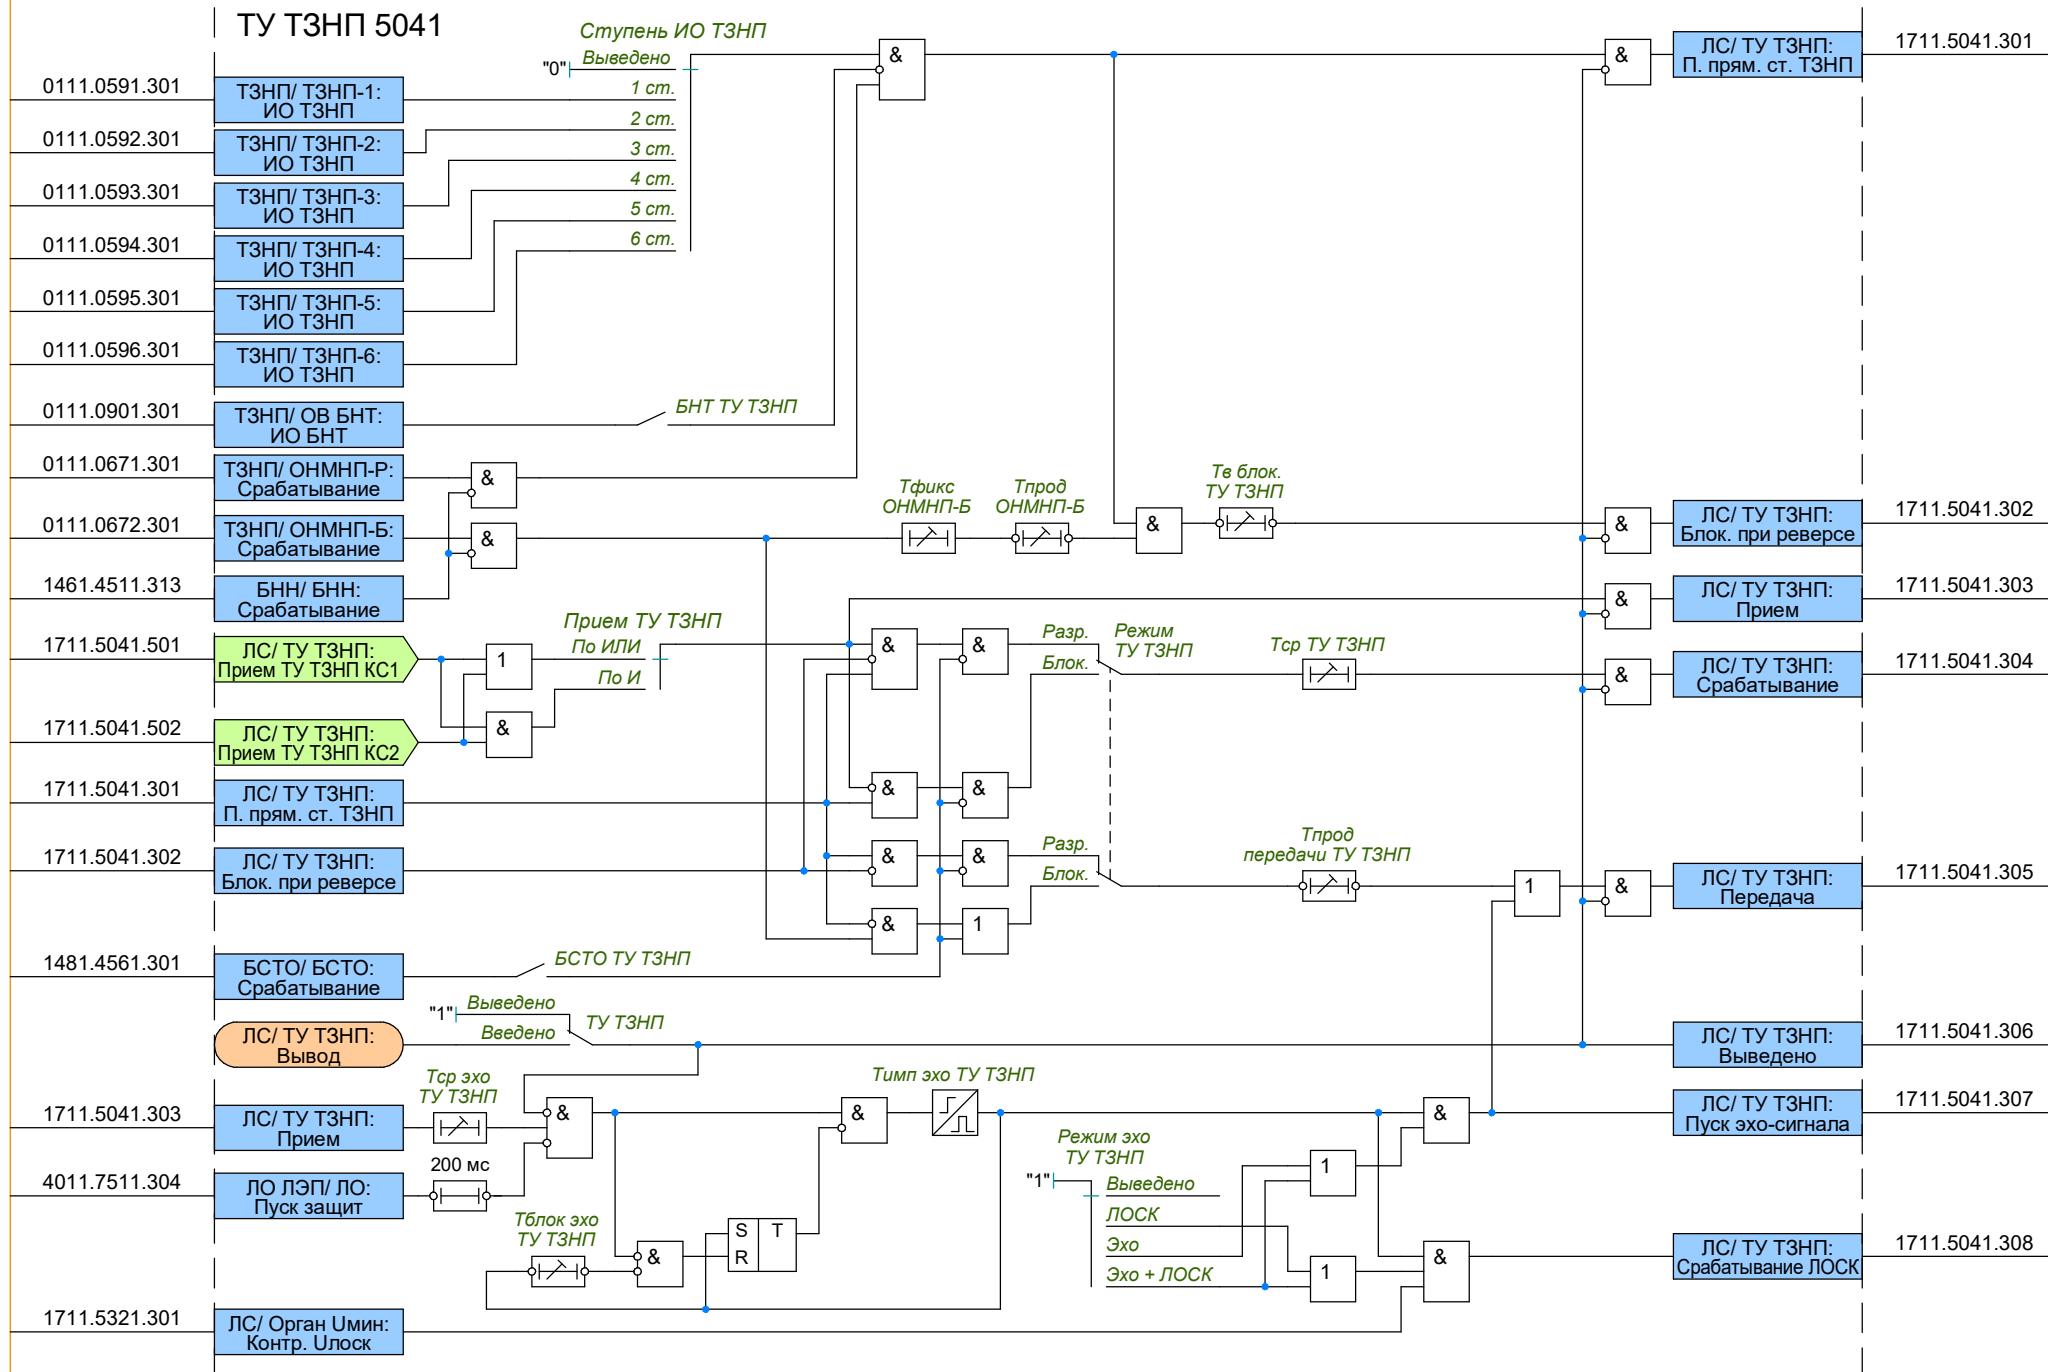


УРОВ В1 3311

УРОВ 6631

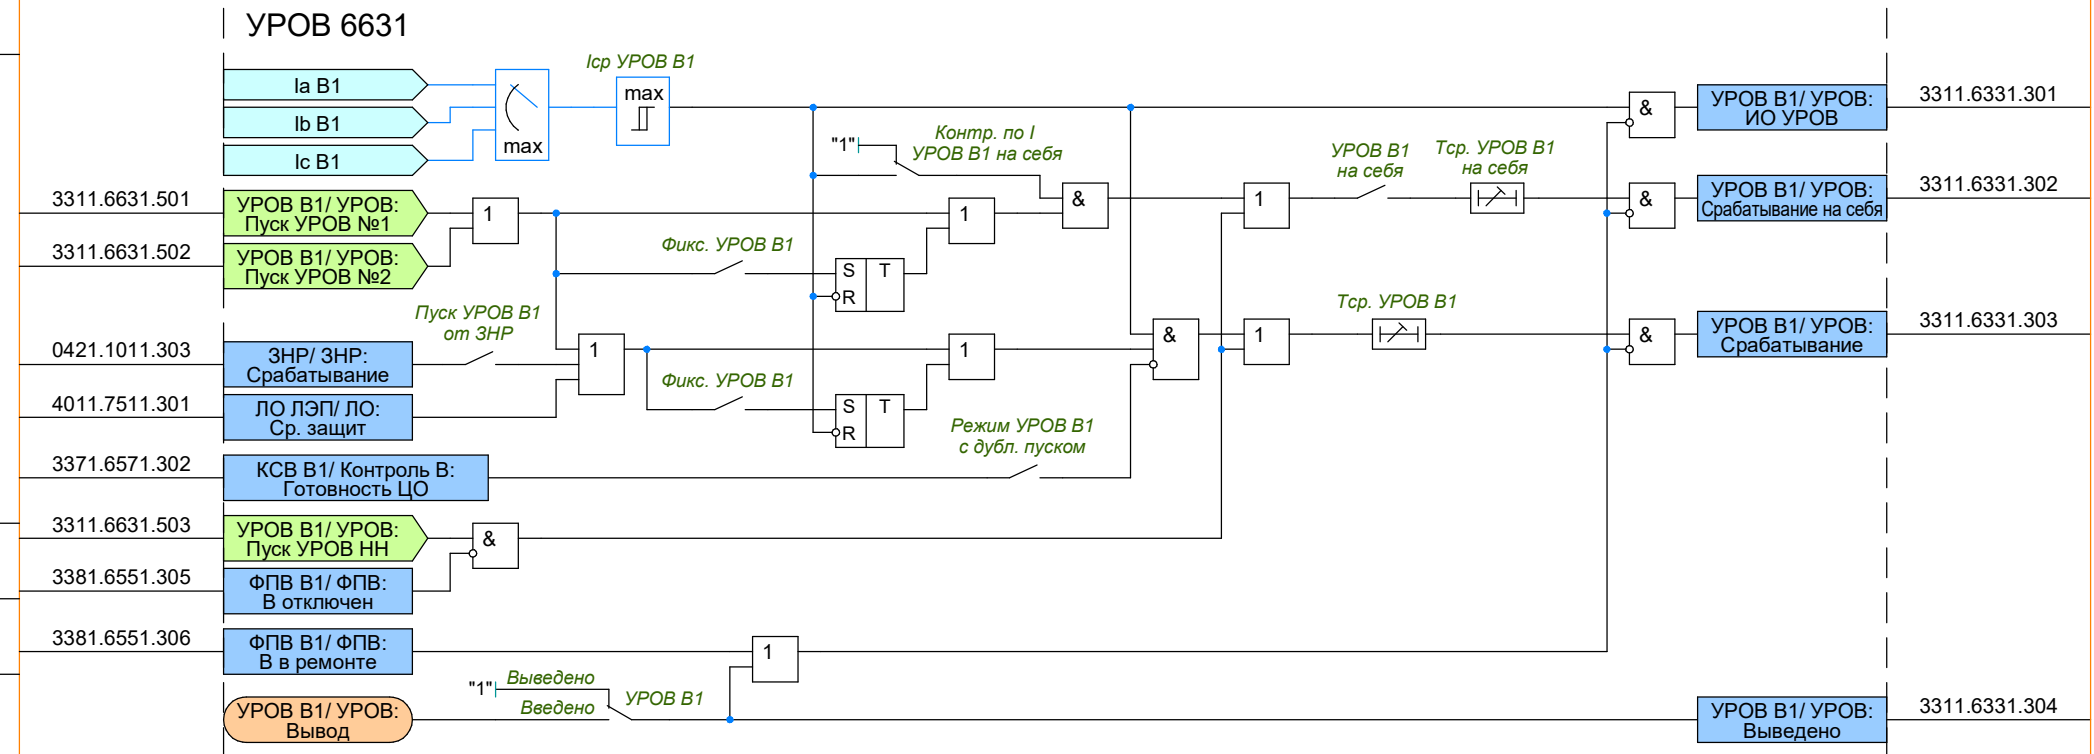


УРОВ В2 3312

УРОВ 6631

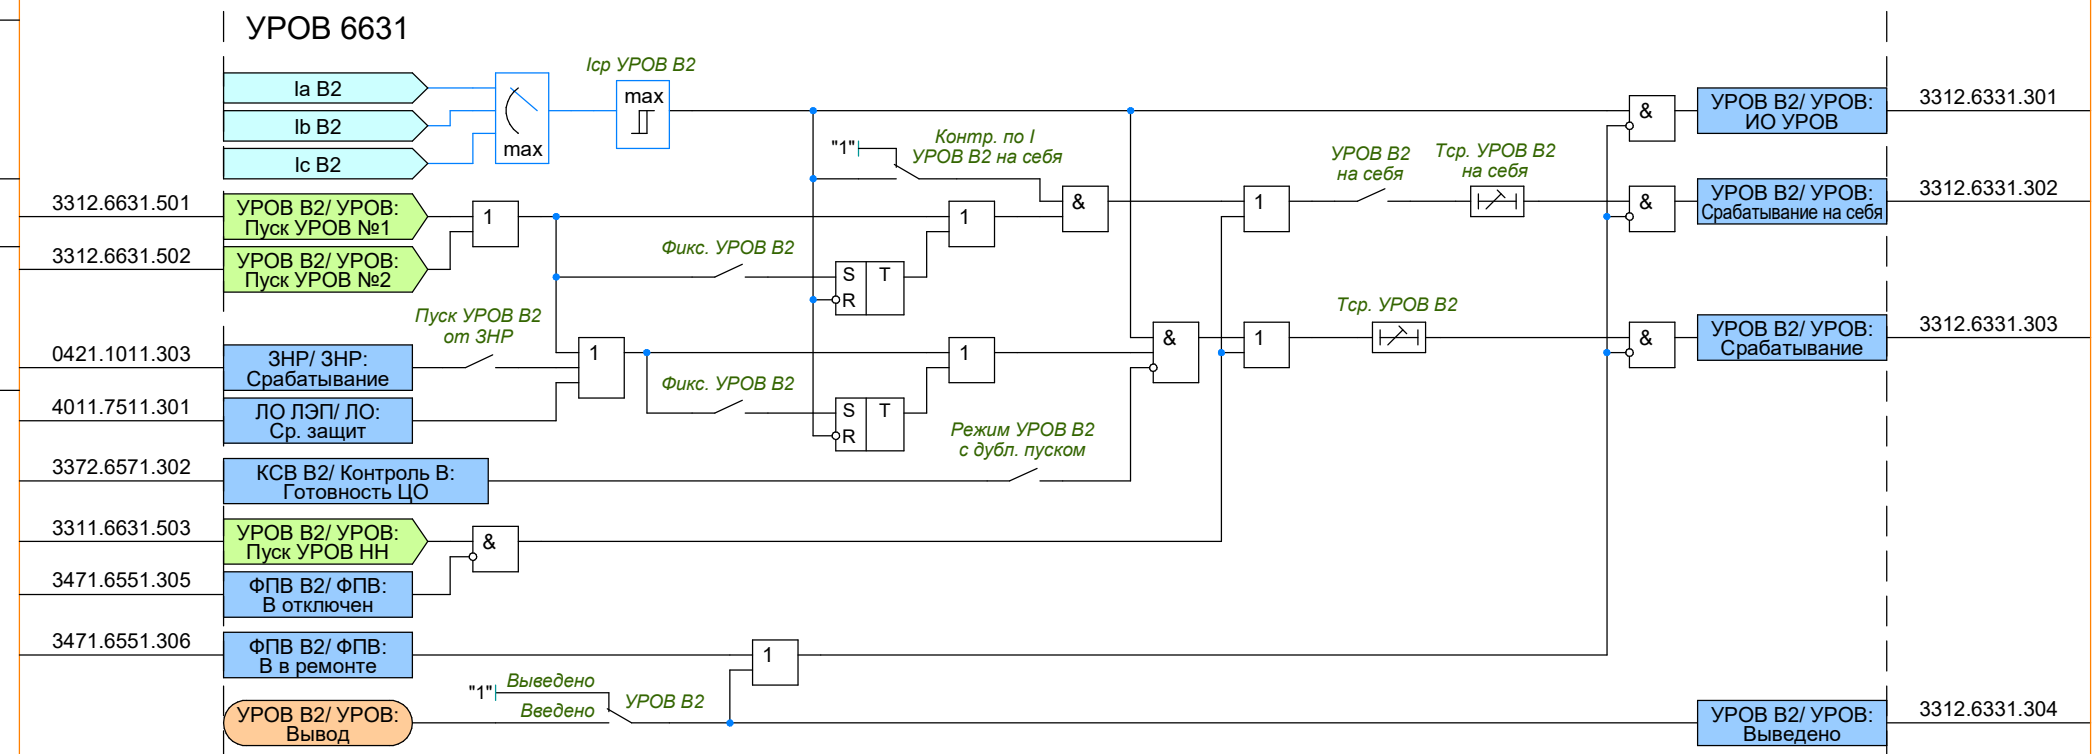


КСВ В1 (Контроль силового выключателя) В1 3371

Контроль В 6571

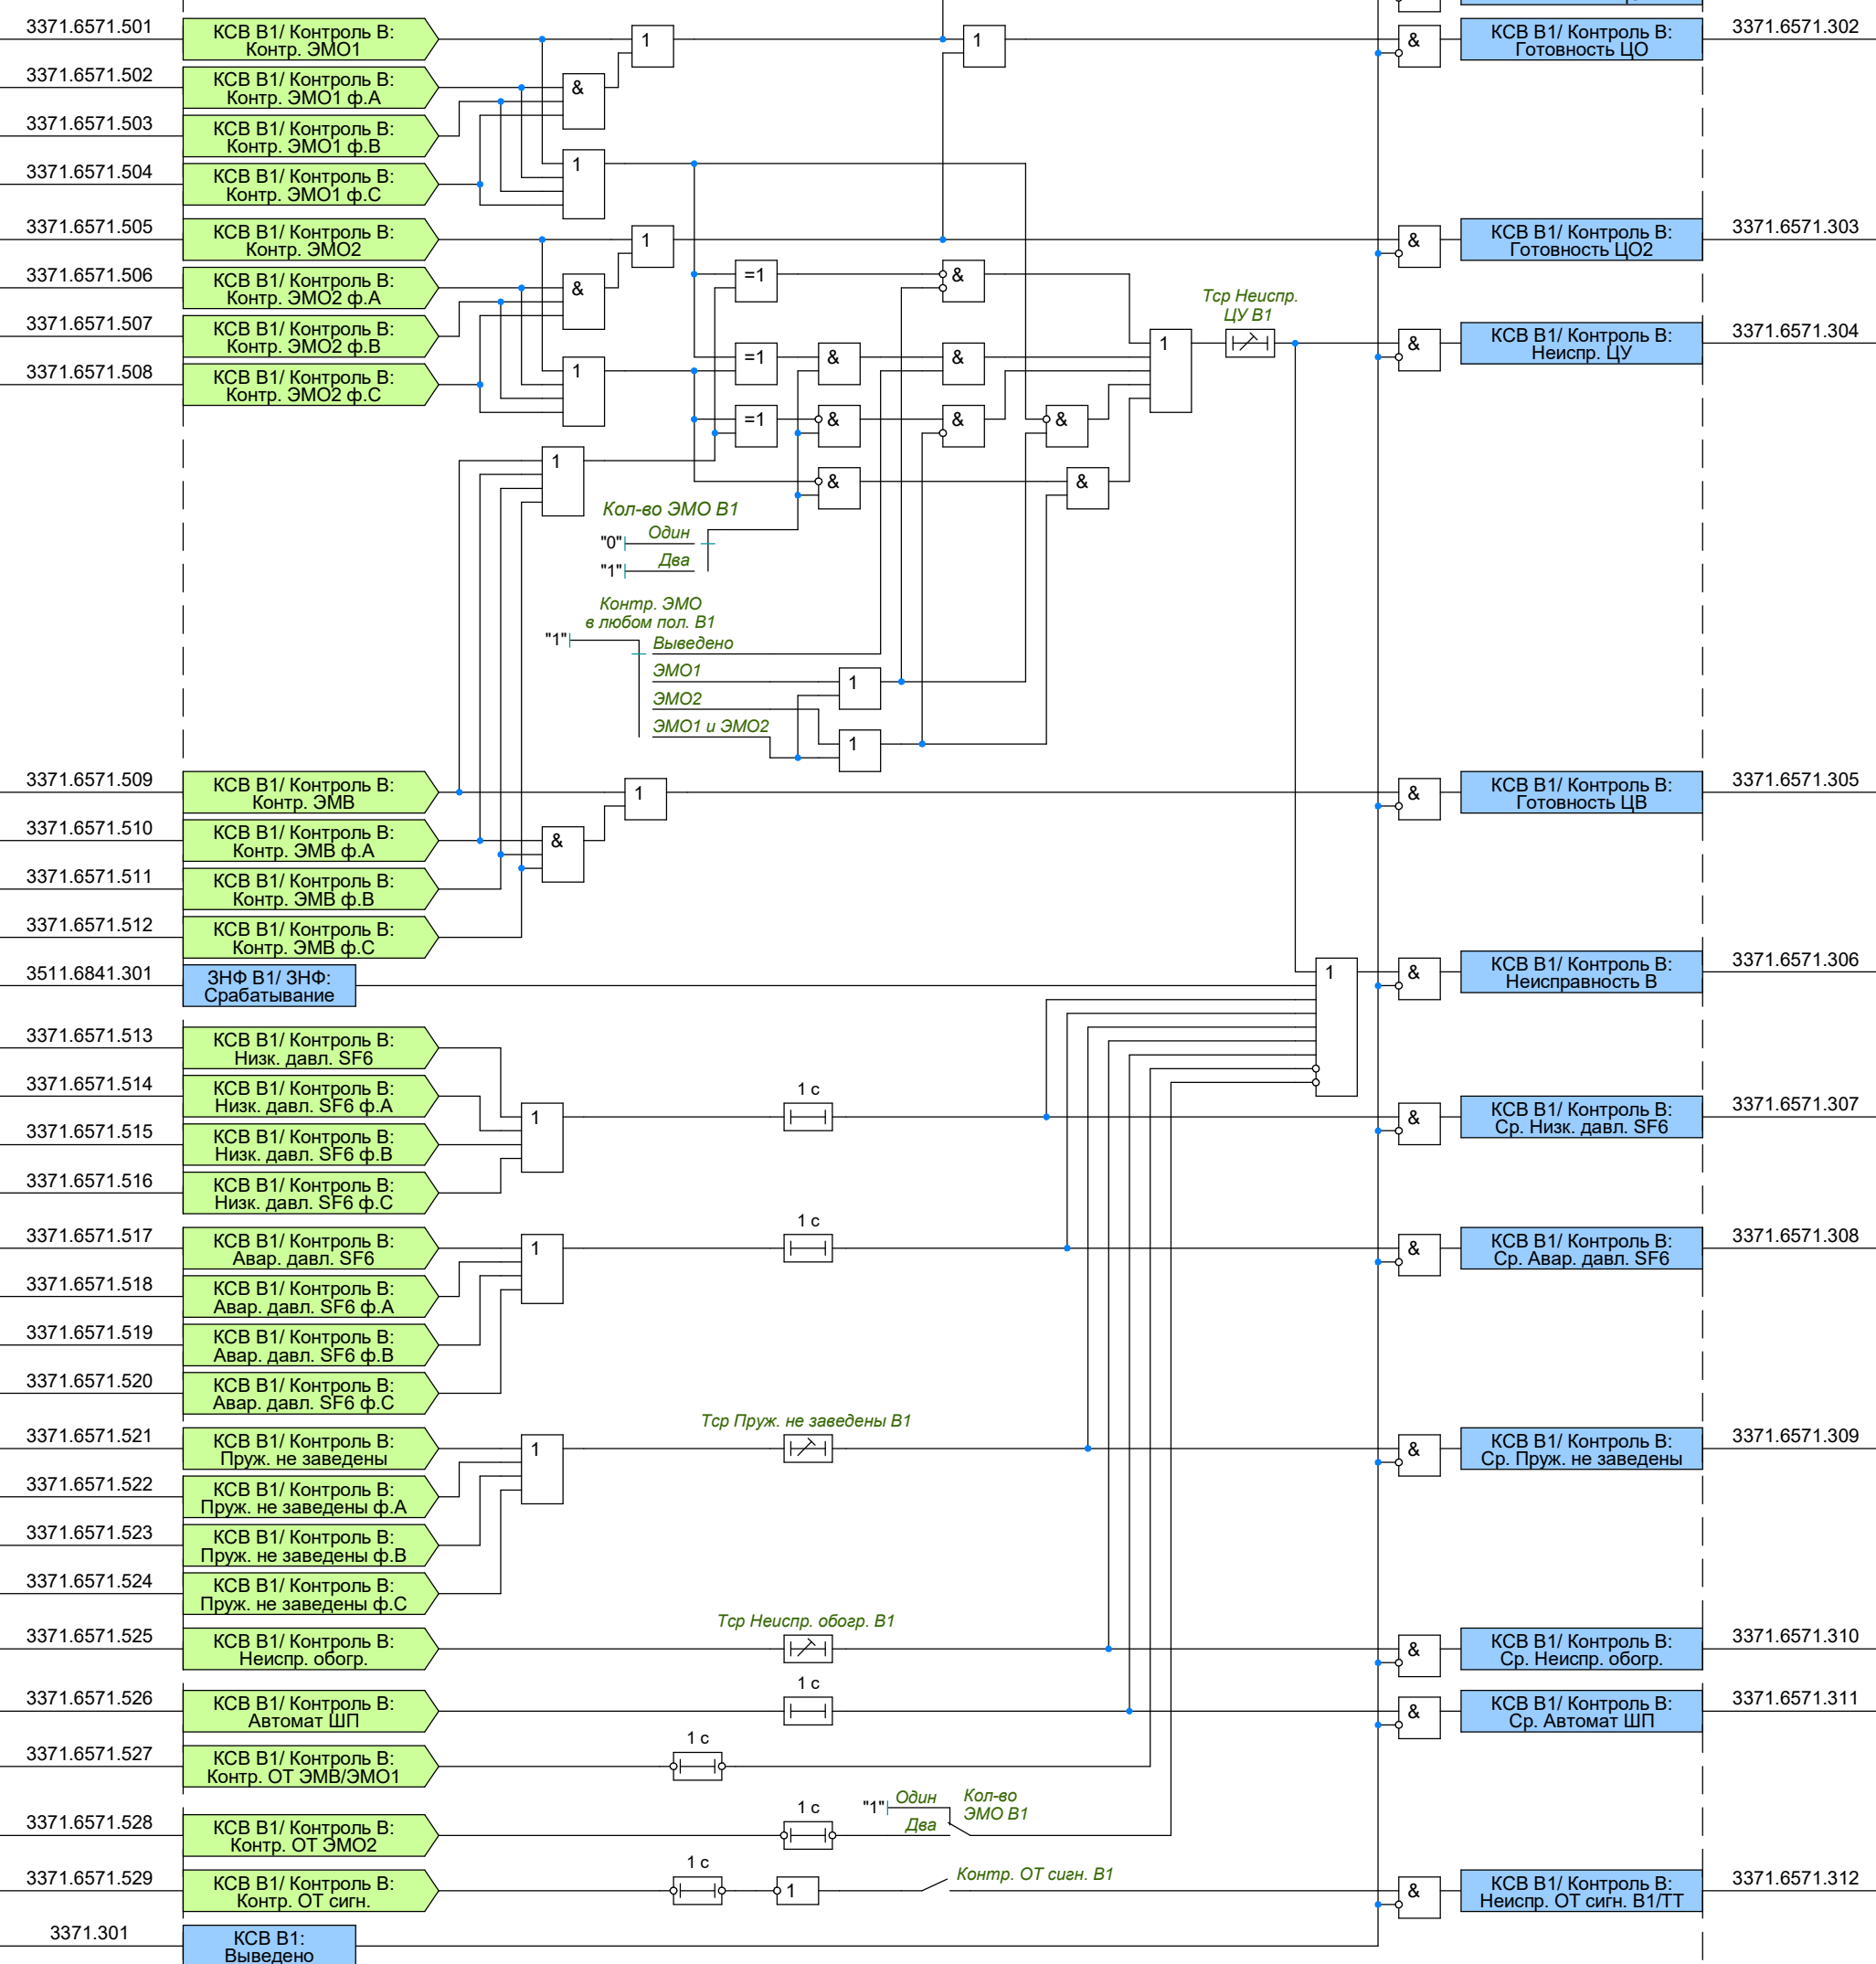


Блокировка управления 6611

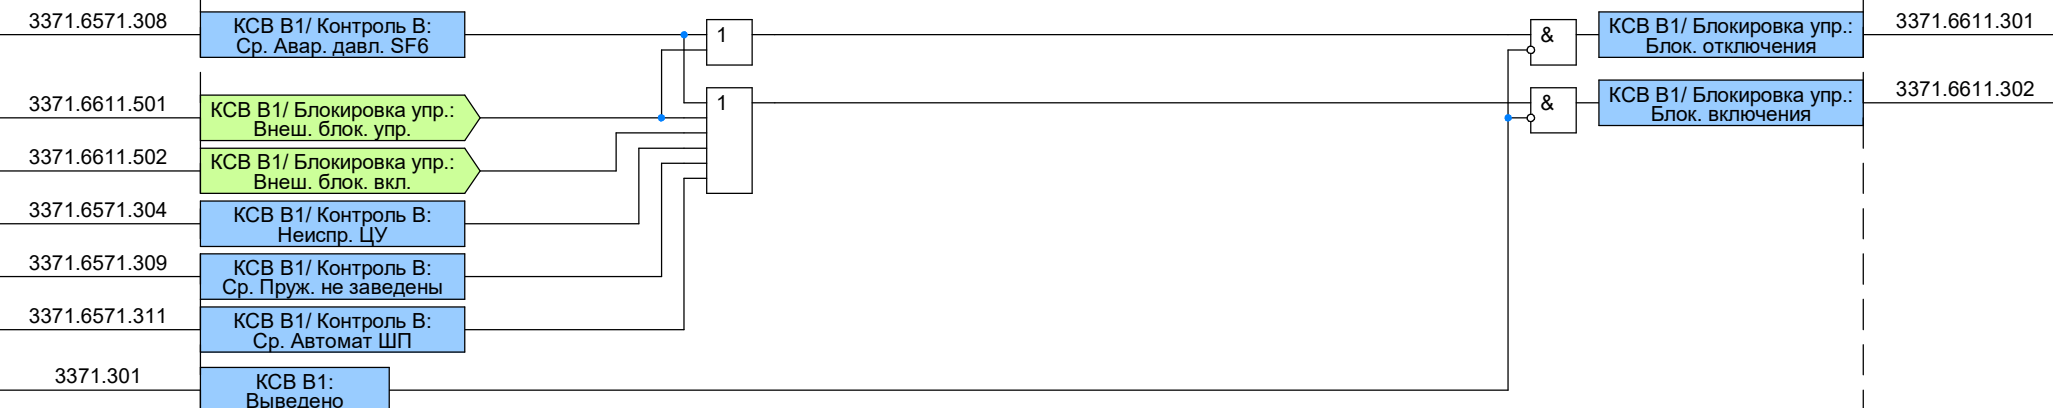


КСВ В1 (Контроль силового выключателя) В1 3371


Контроль ТТ 6581

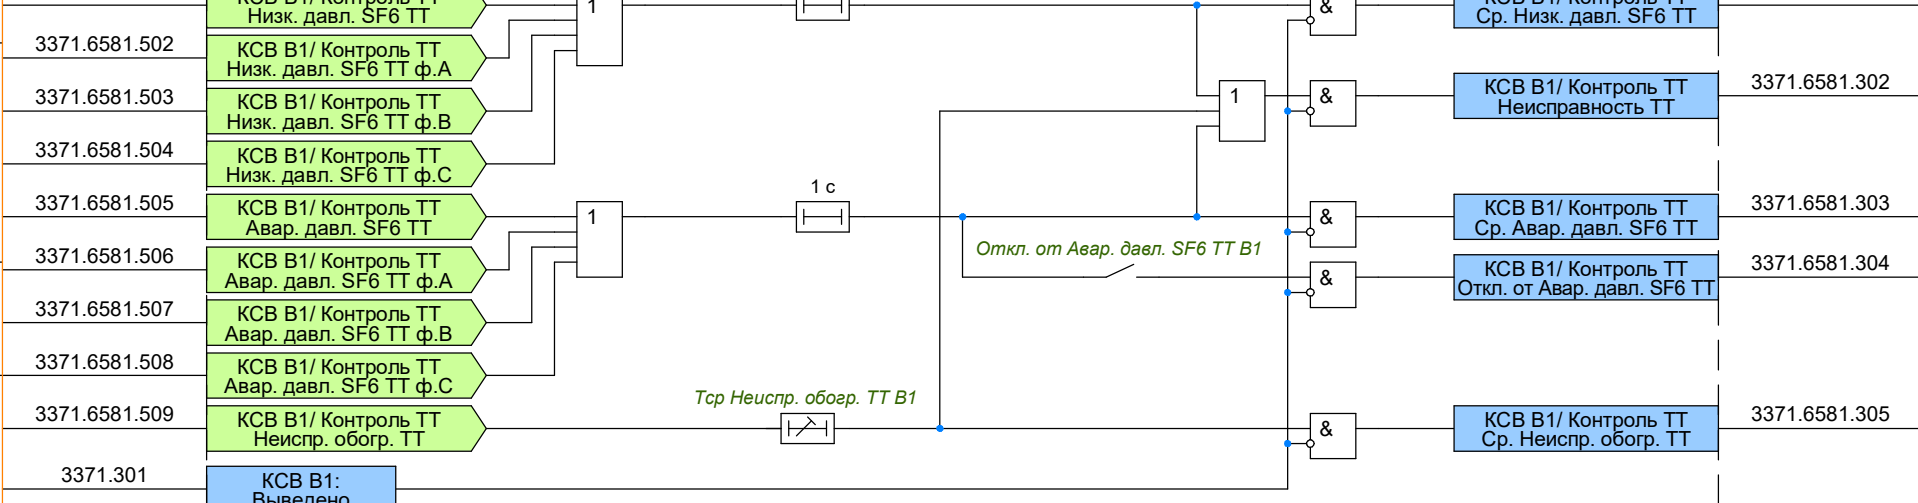

Защита ЭМУ 6601

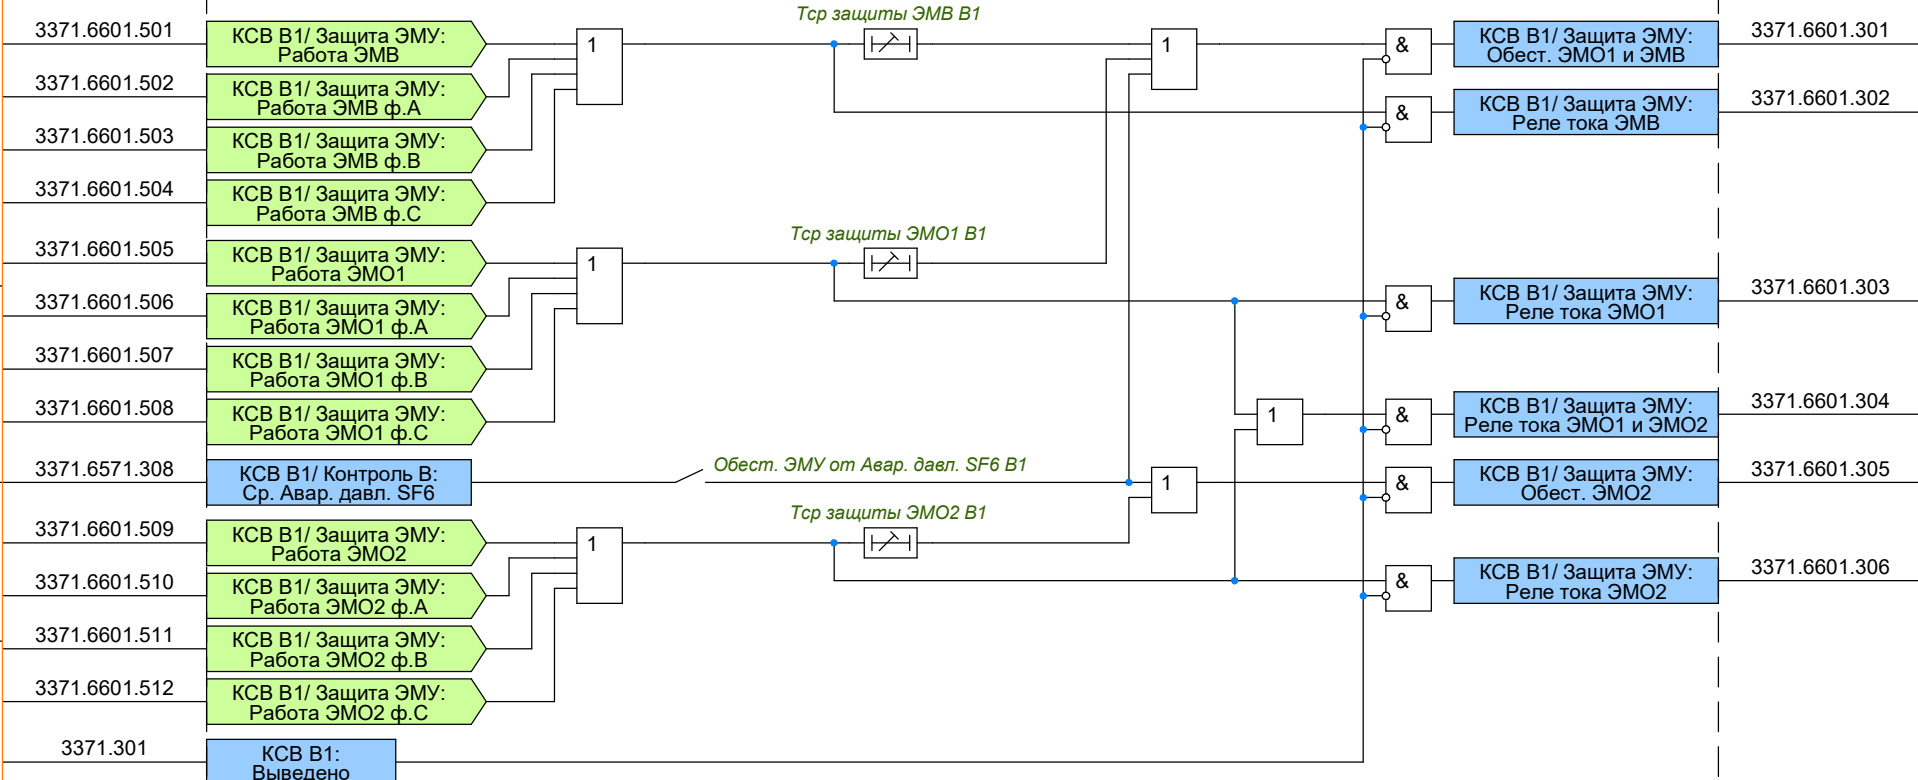


РФ (Реле фиксации) 6621

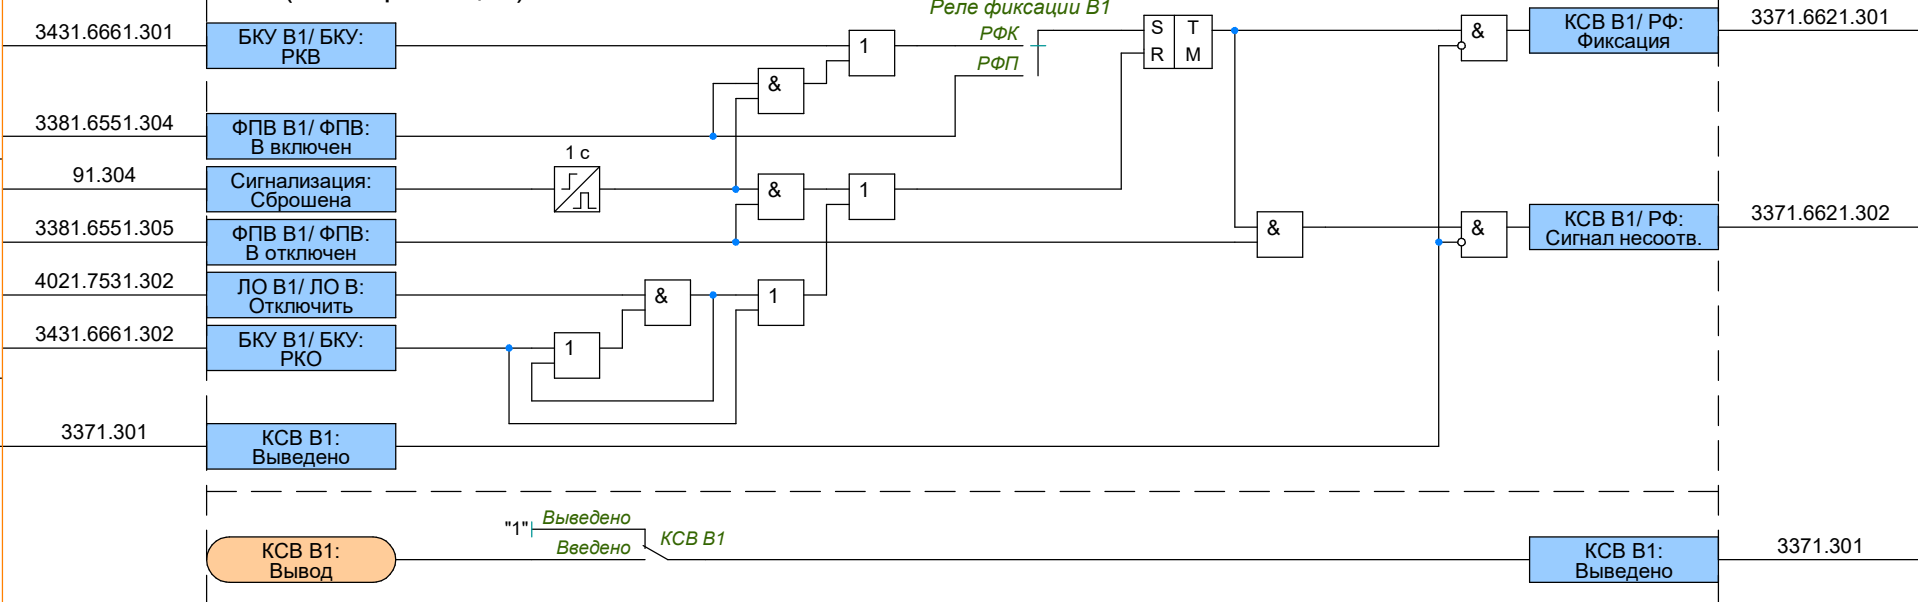


БКУ В1 (Блок команд управления В1) 3431

БКУ 6661

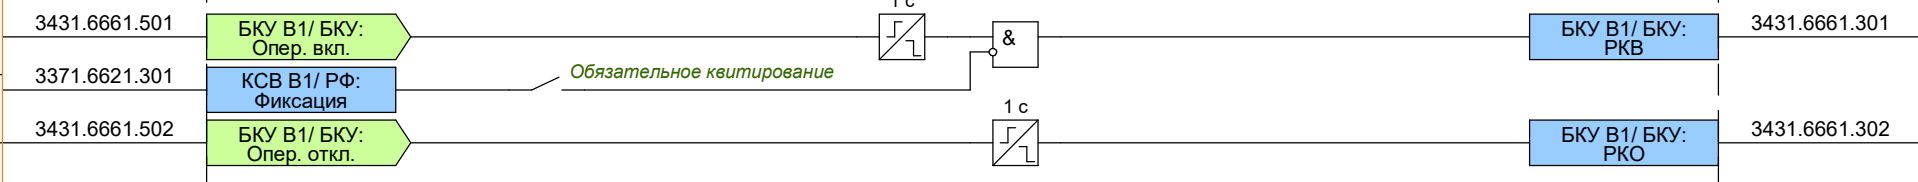


КСВ В2 (Контроль силового выключателя) В2 3372

Контроль В 6571

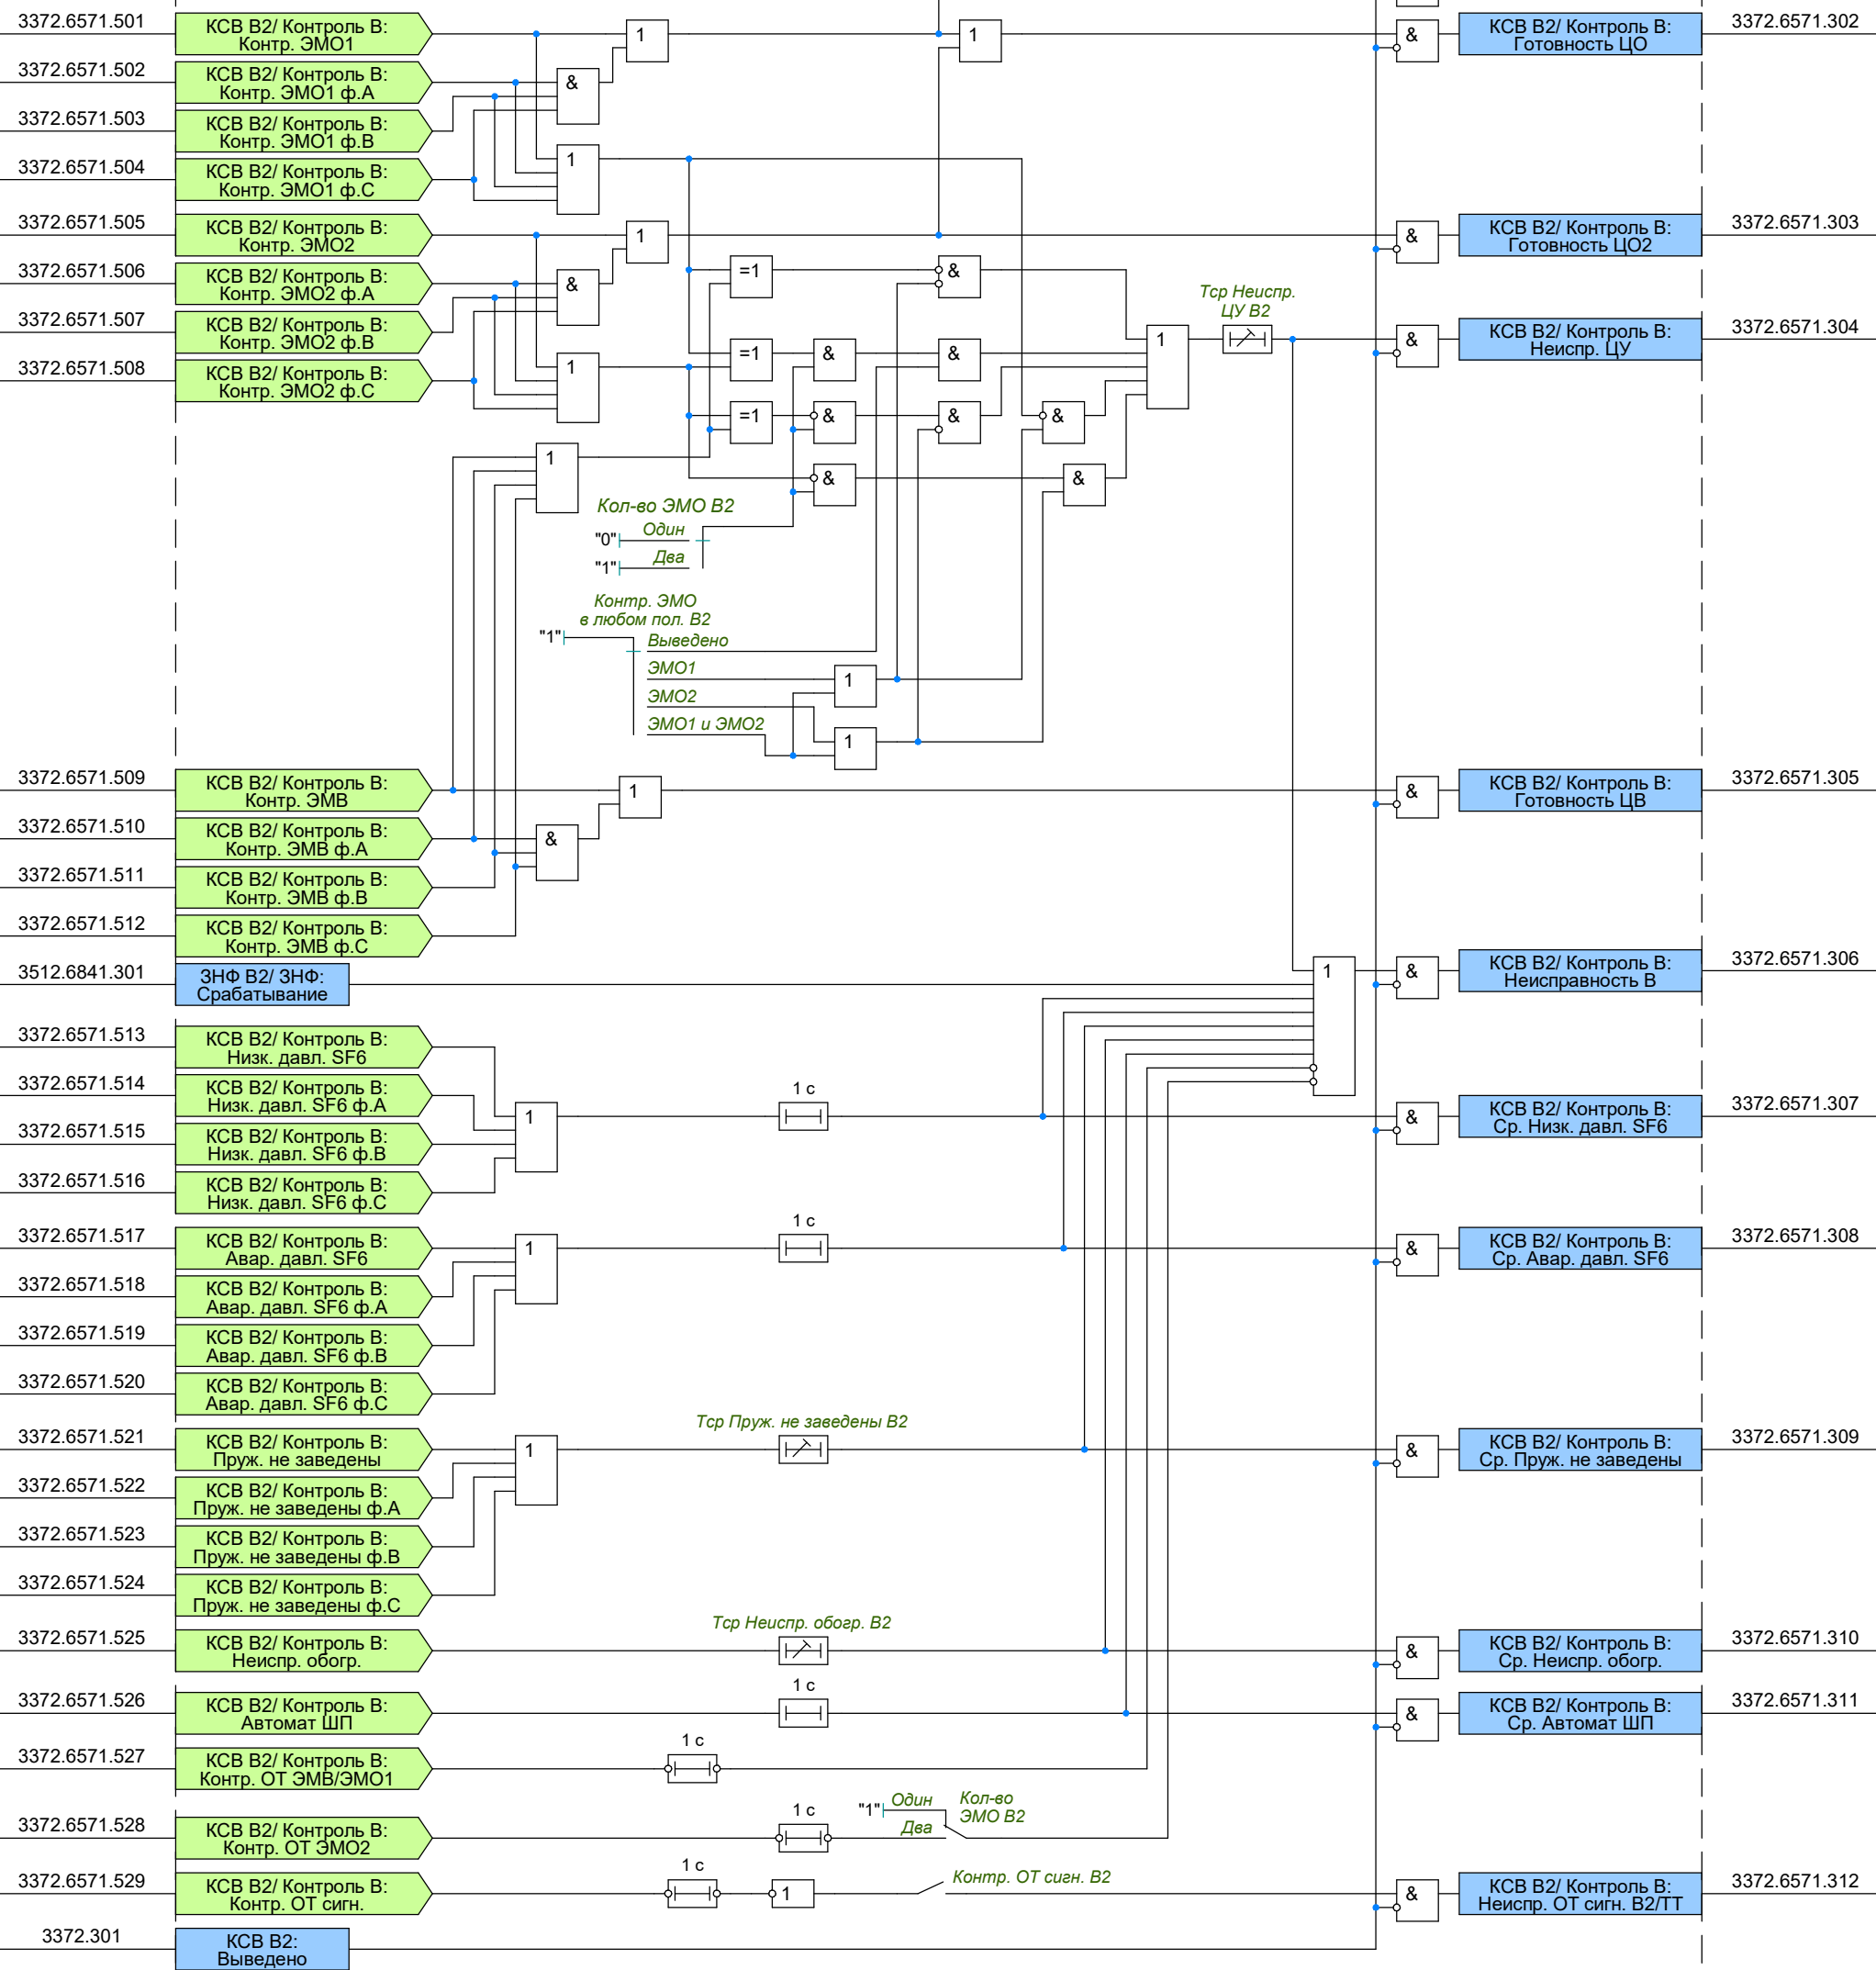


Блокировка управления 6611

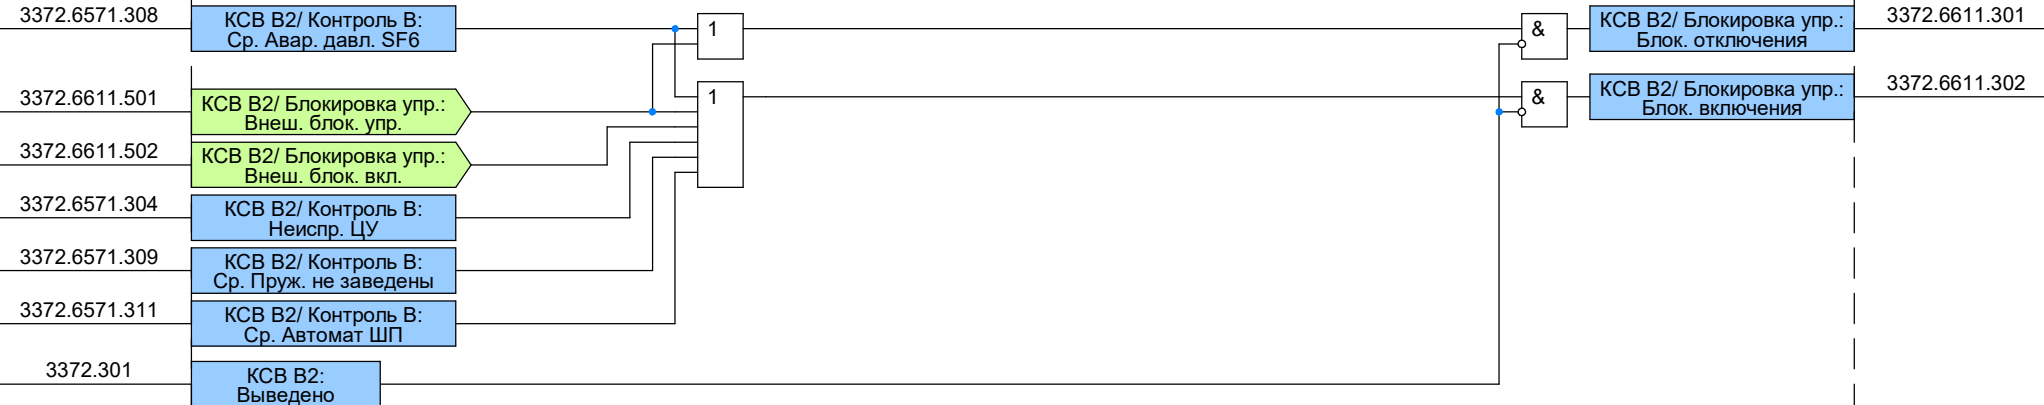


КСВ В2 (Контроль силового выключателя) В2 3372


Контроль ТТ 6581

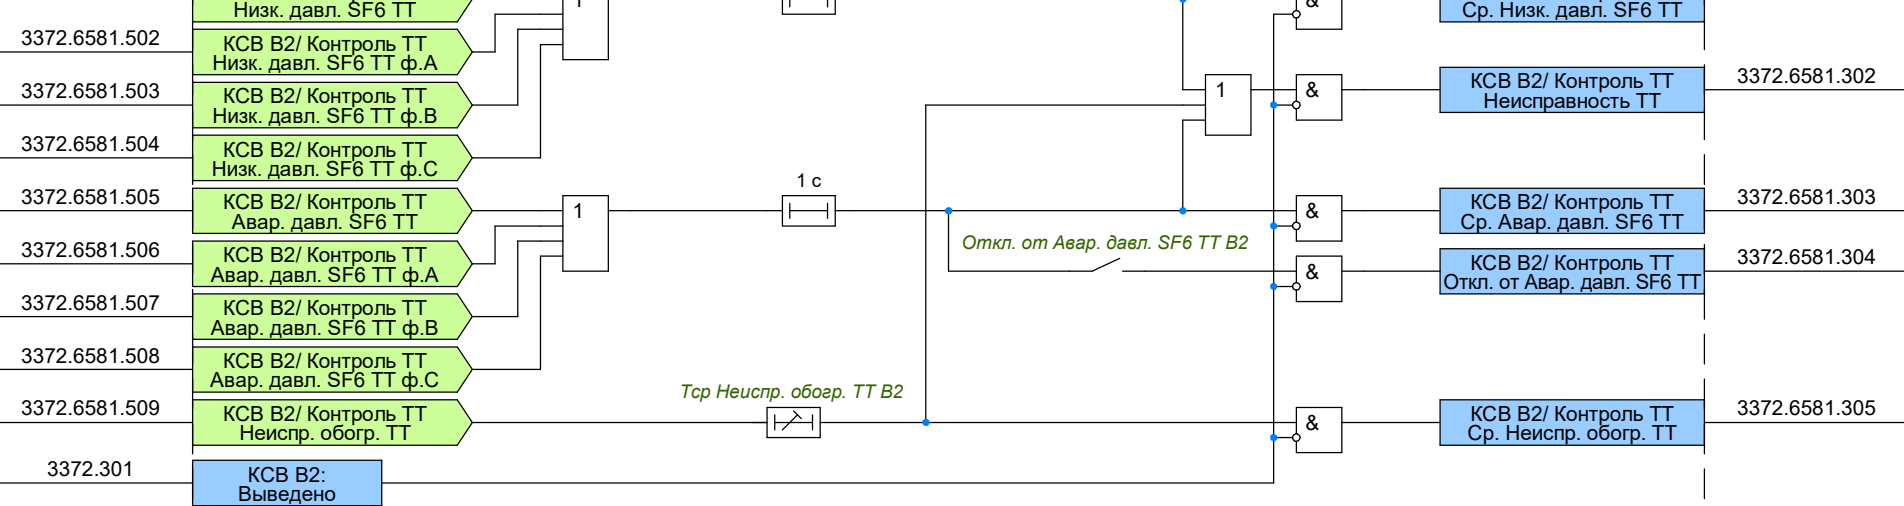

Защита ЭМУ 6601

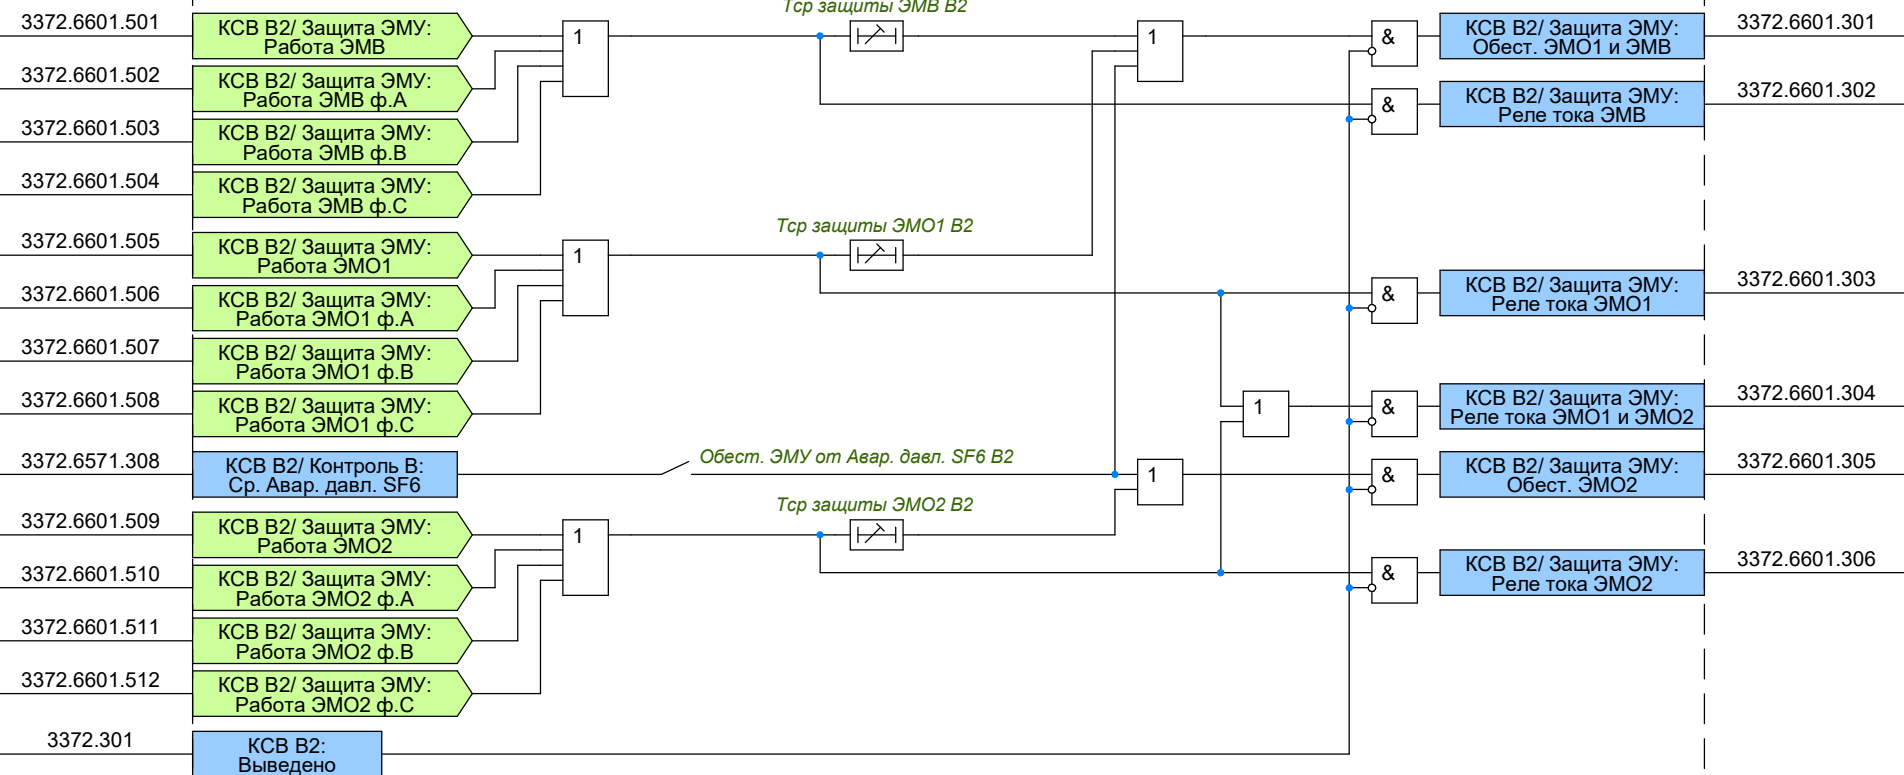


РФ (Реле фиксации) 6621

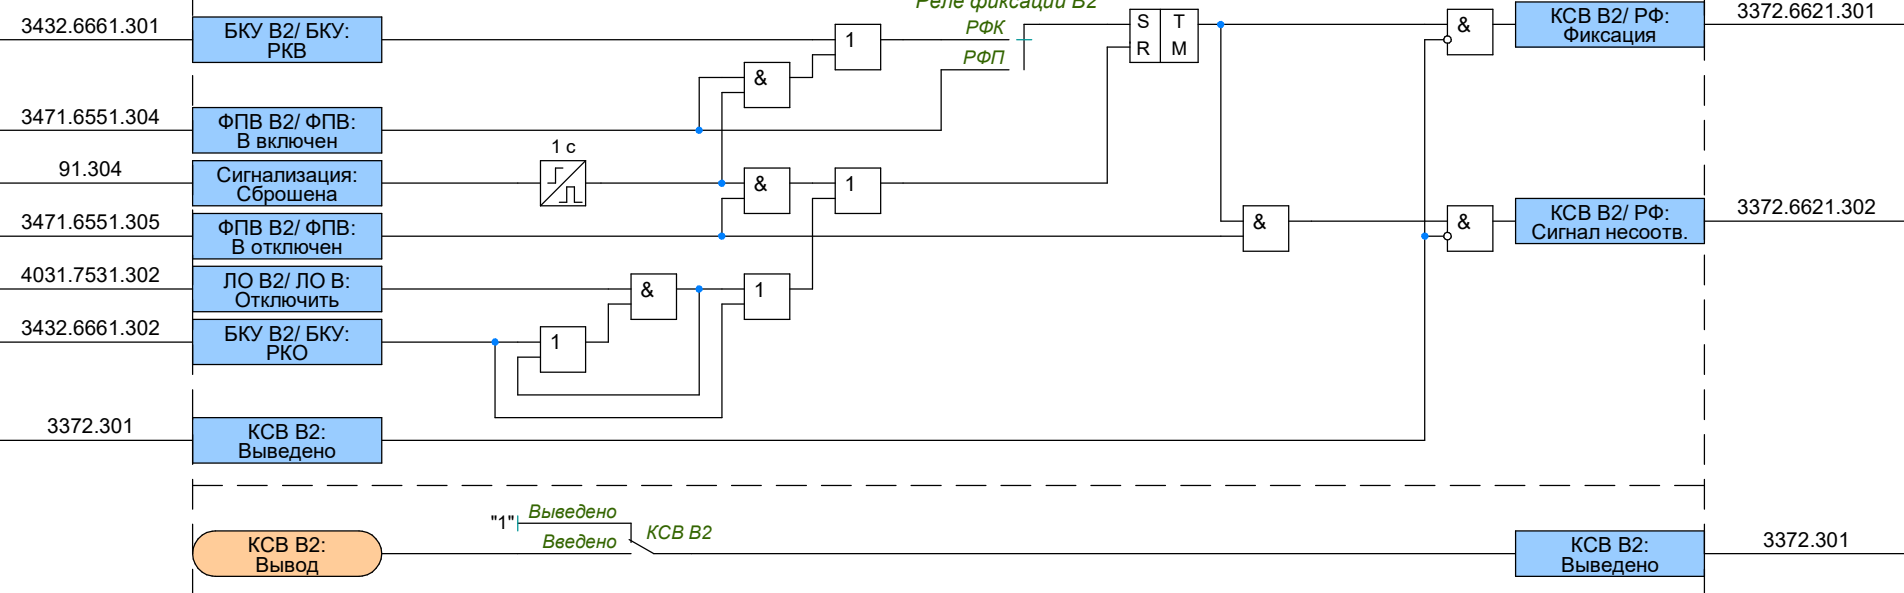


БКУ В2 (Блок команд управления В2) 3432

БКУ 6661

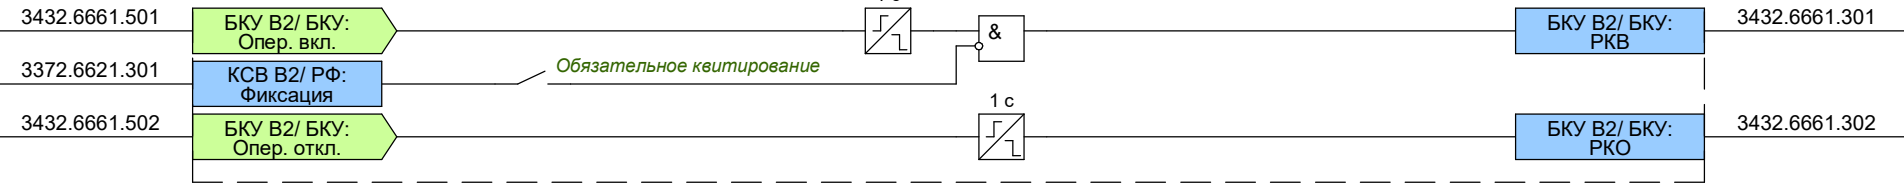


ЛО 4011

ЛО 7511

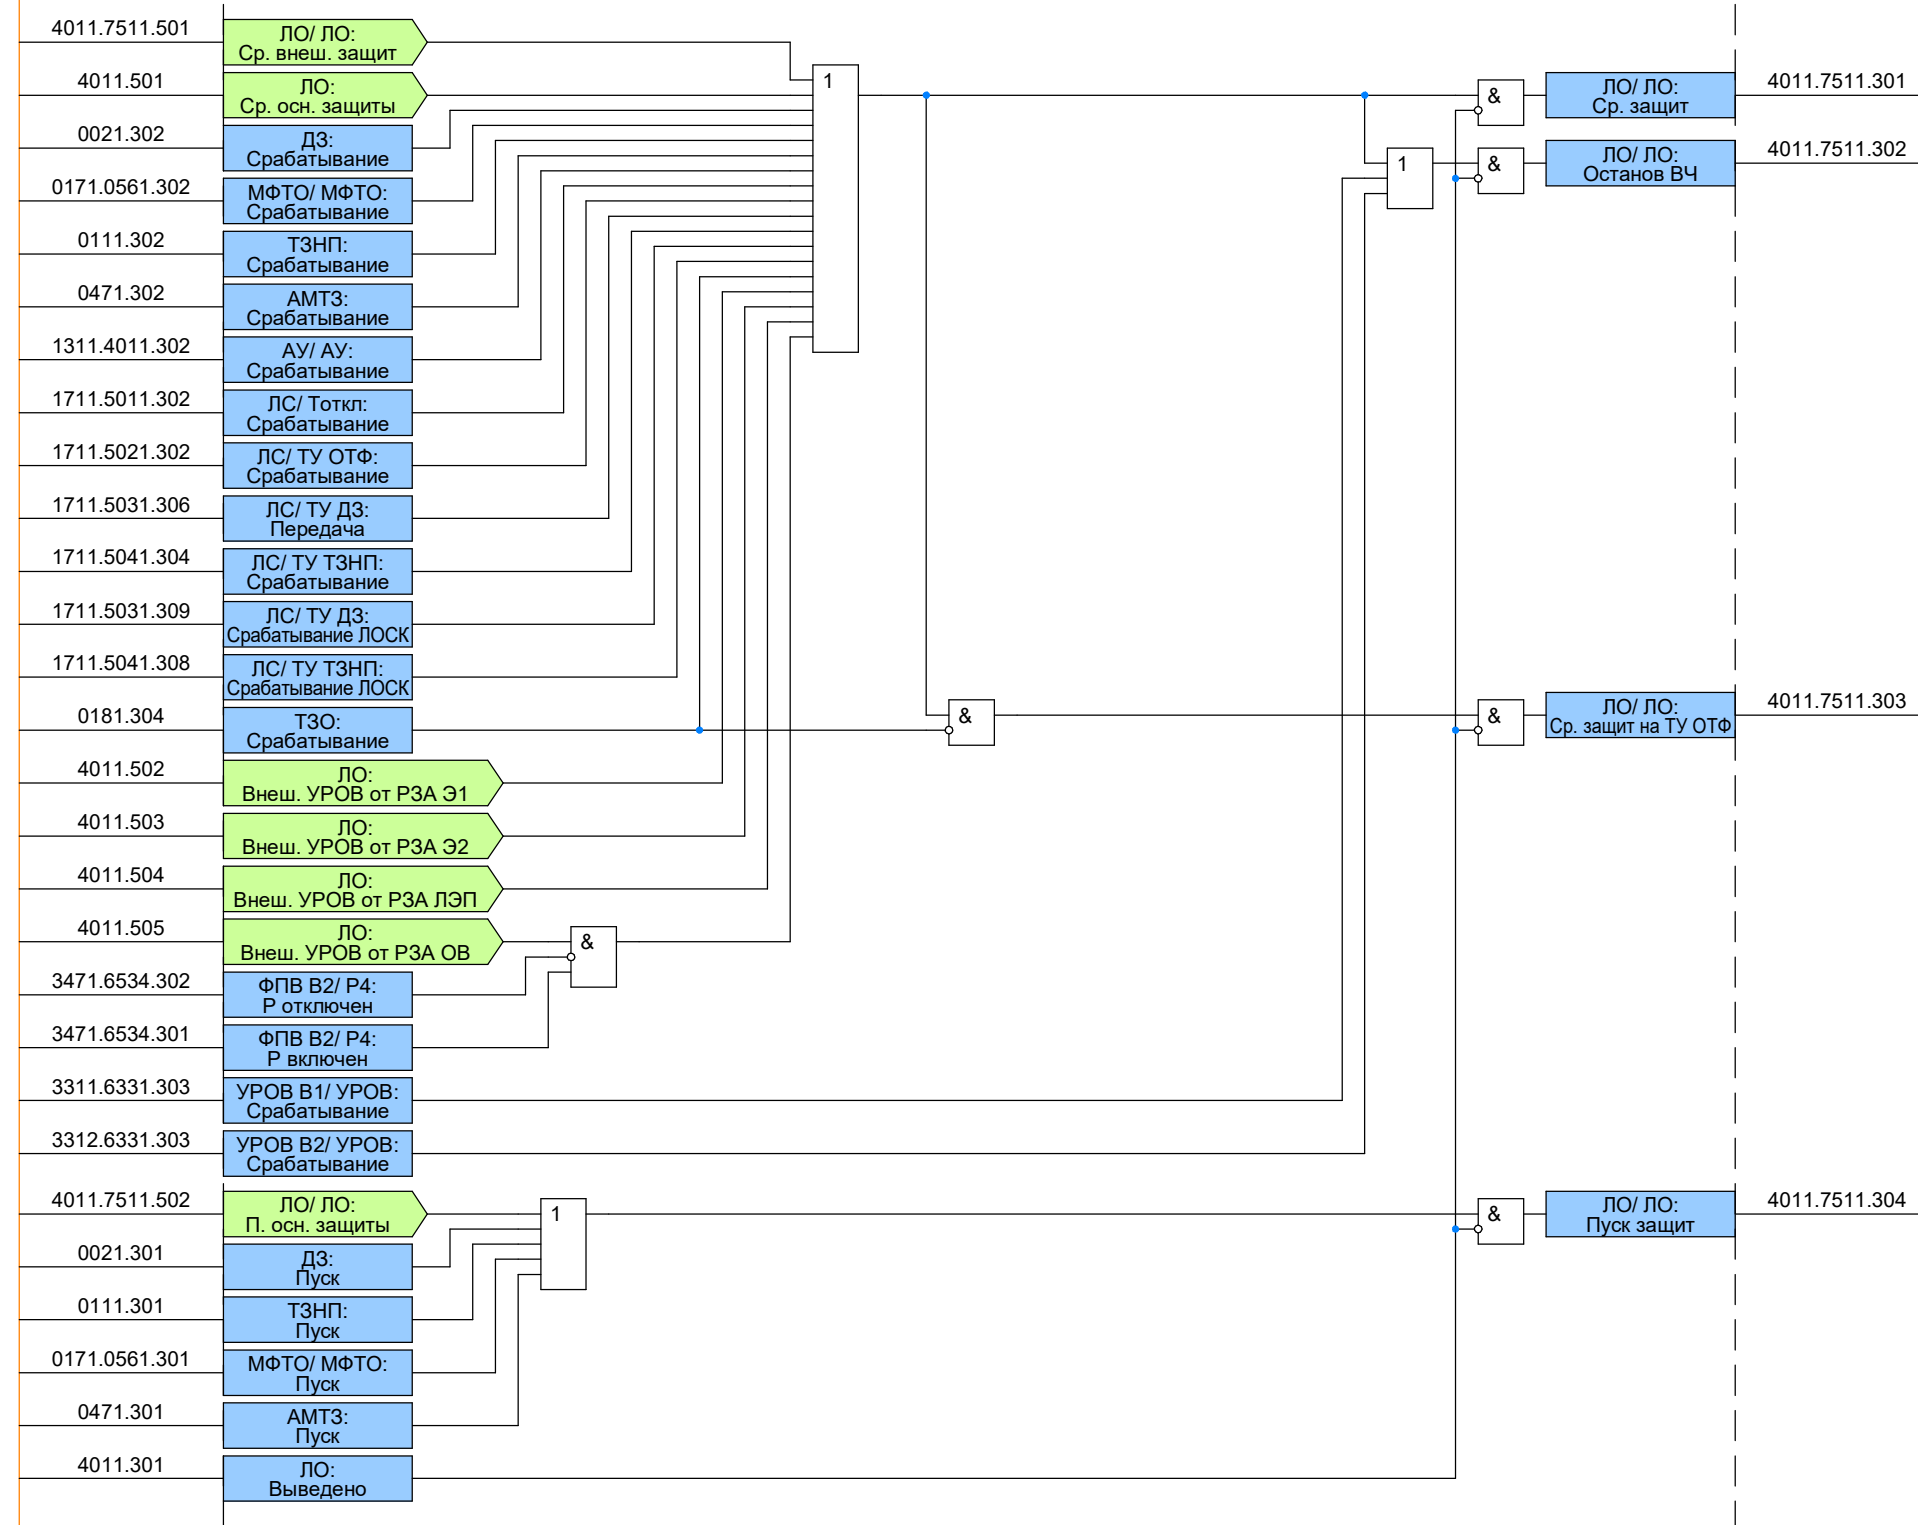


ЛО 4011

Запрет АПВ 7521

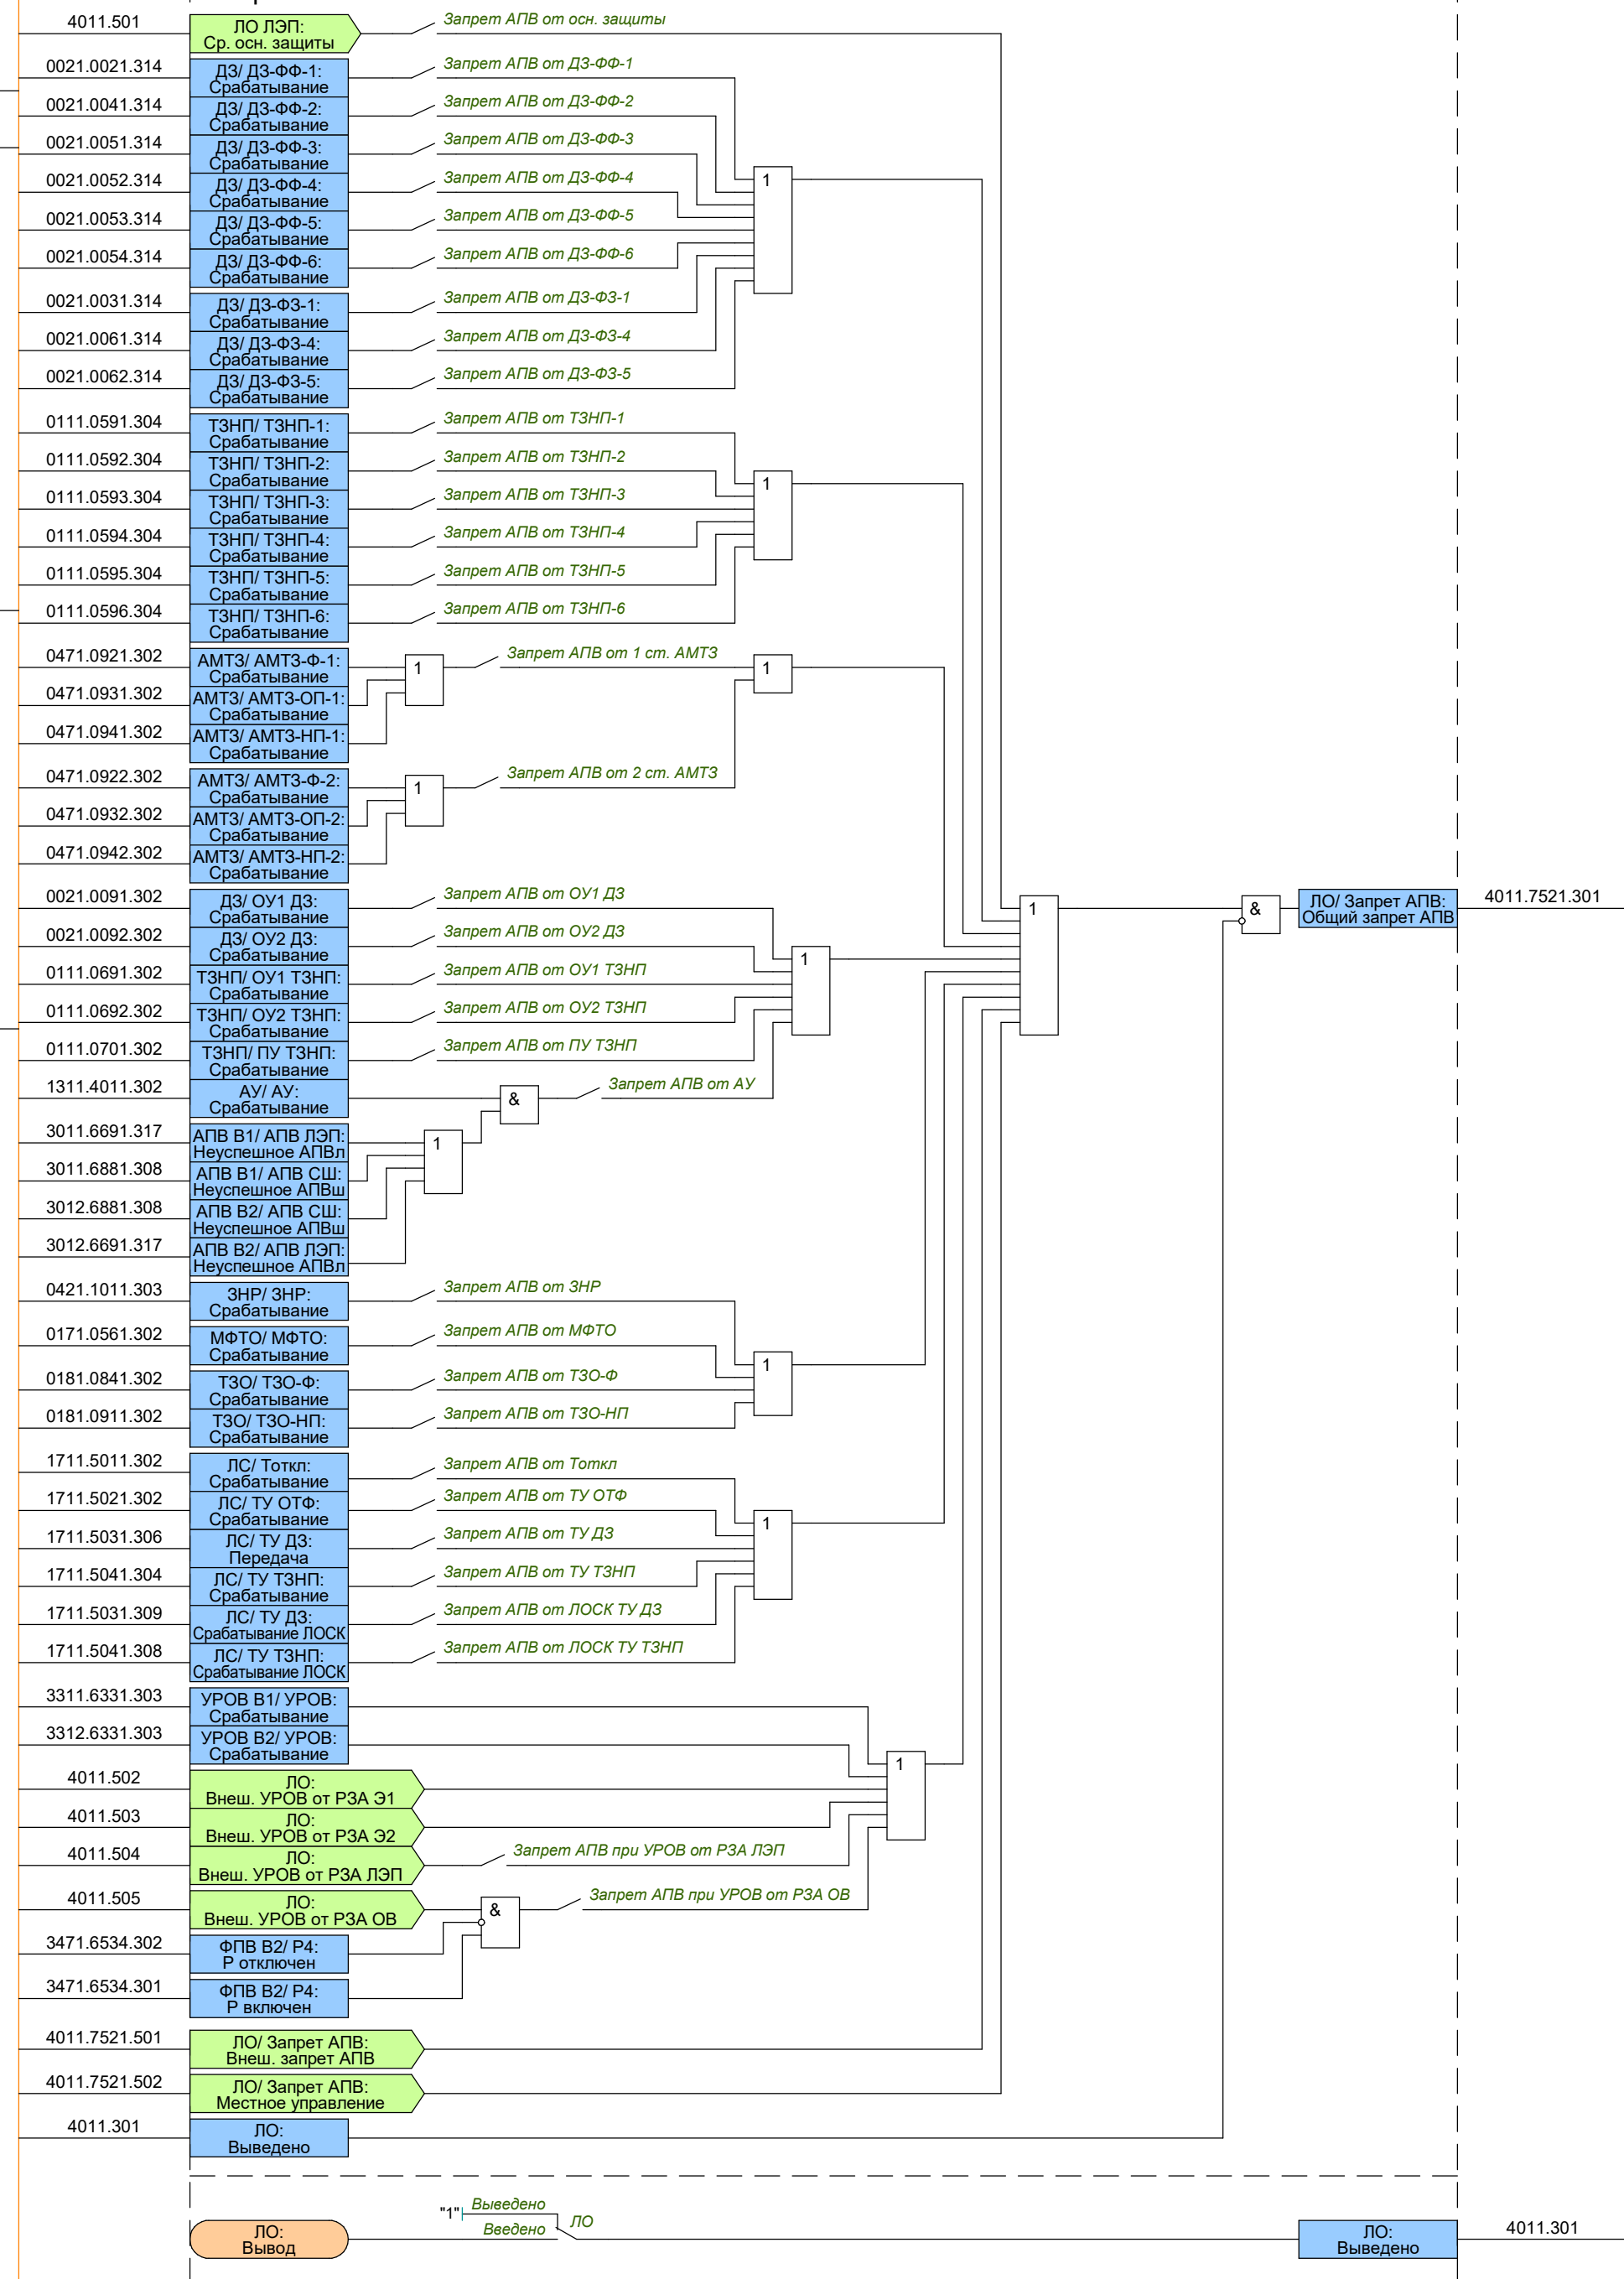


ФПВ ВЗ (Фиксация положения выключателя ВЗ) 3461


ФПВ 6551

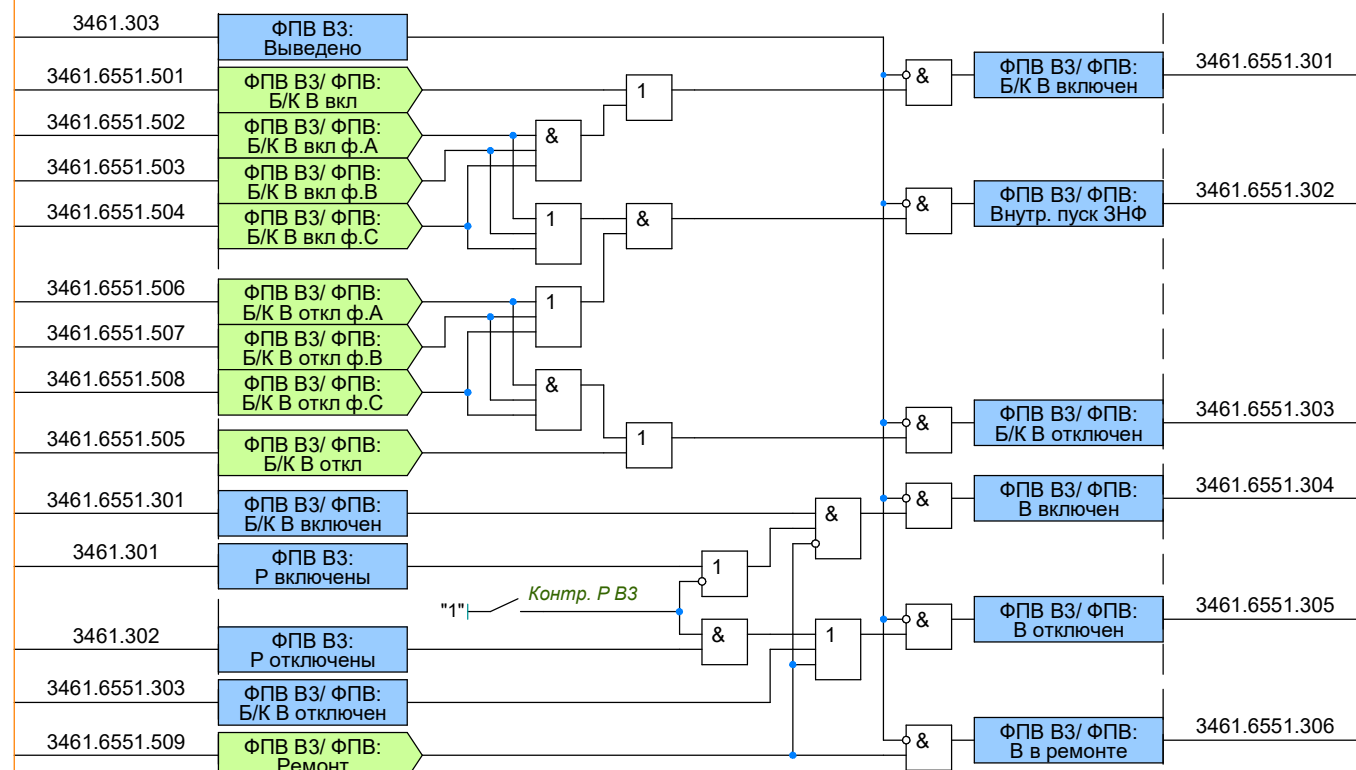

Р1 6531

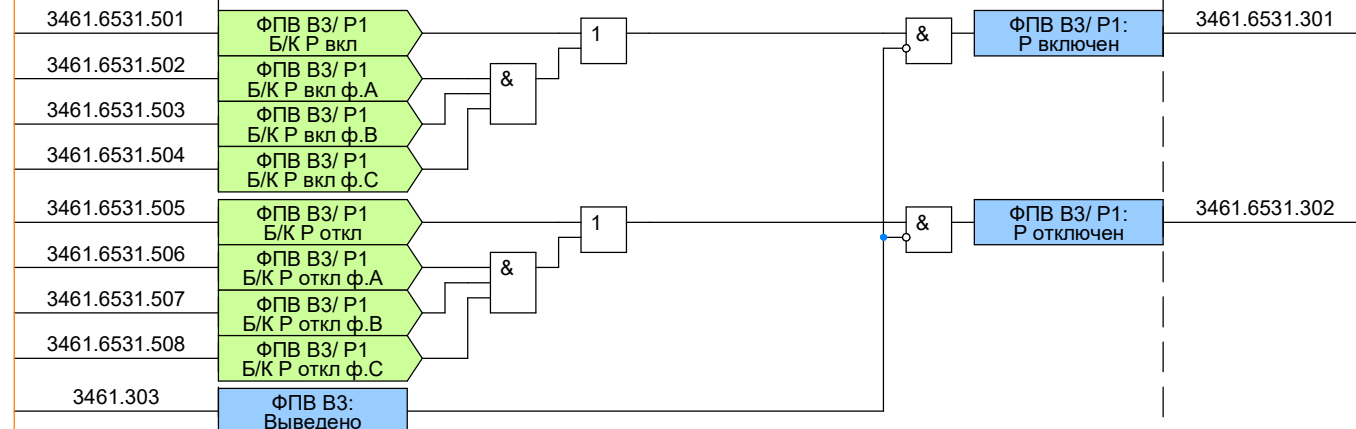

Р2 (6532)

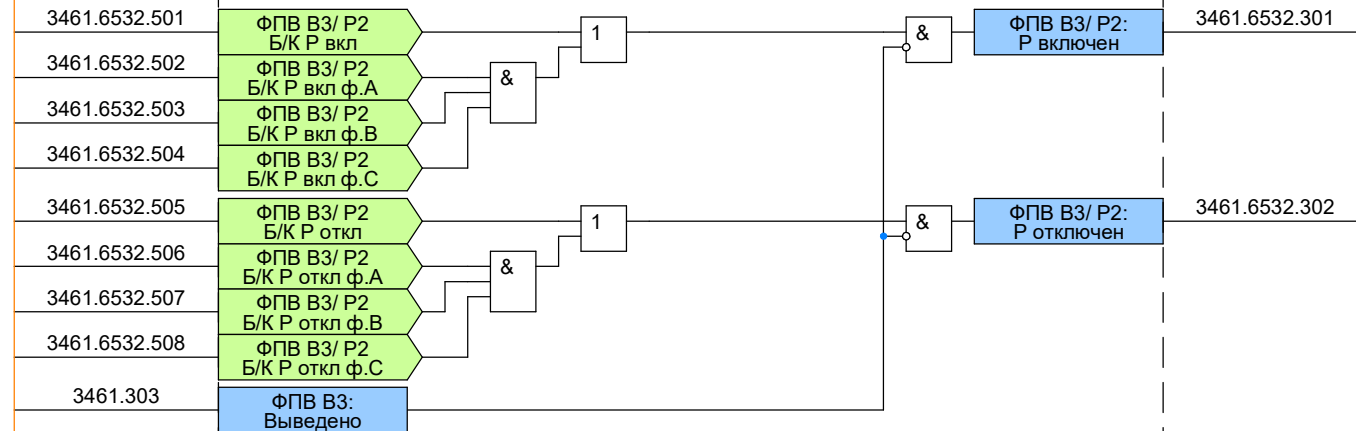

ФПВ ВЗ: Р включены


ФПВ ВЗ: Р отключены

ФПВ ВЗ: Выведено

ФПВ ВЗ: Вывод


Коммутация В1 1821

Коммутация 5301

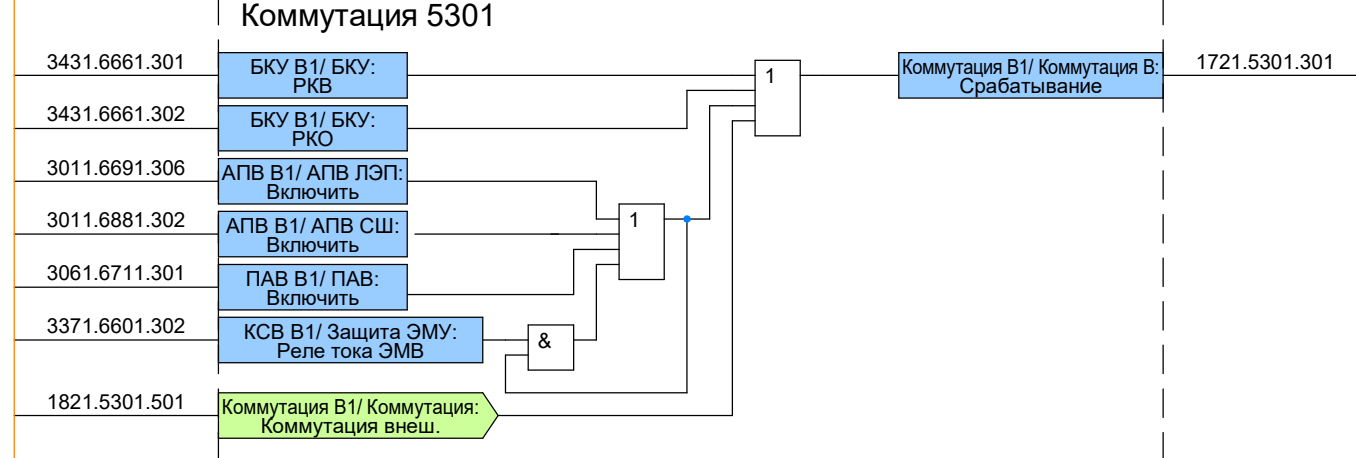


ФПВ ШСВ/СВ (Фиксация положения выключателя ШСВ/СВ) 3462


ФПВ 6551

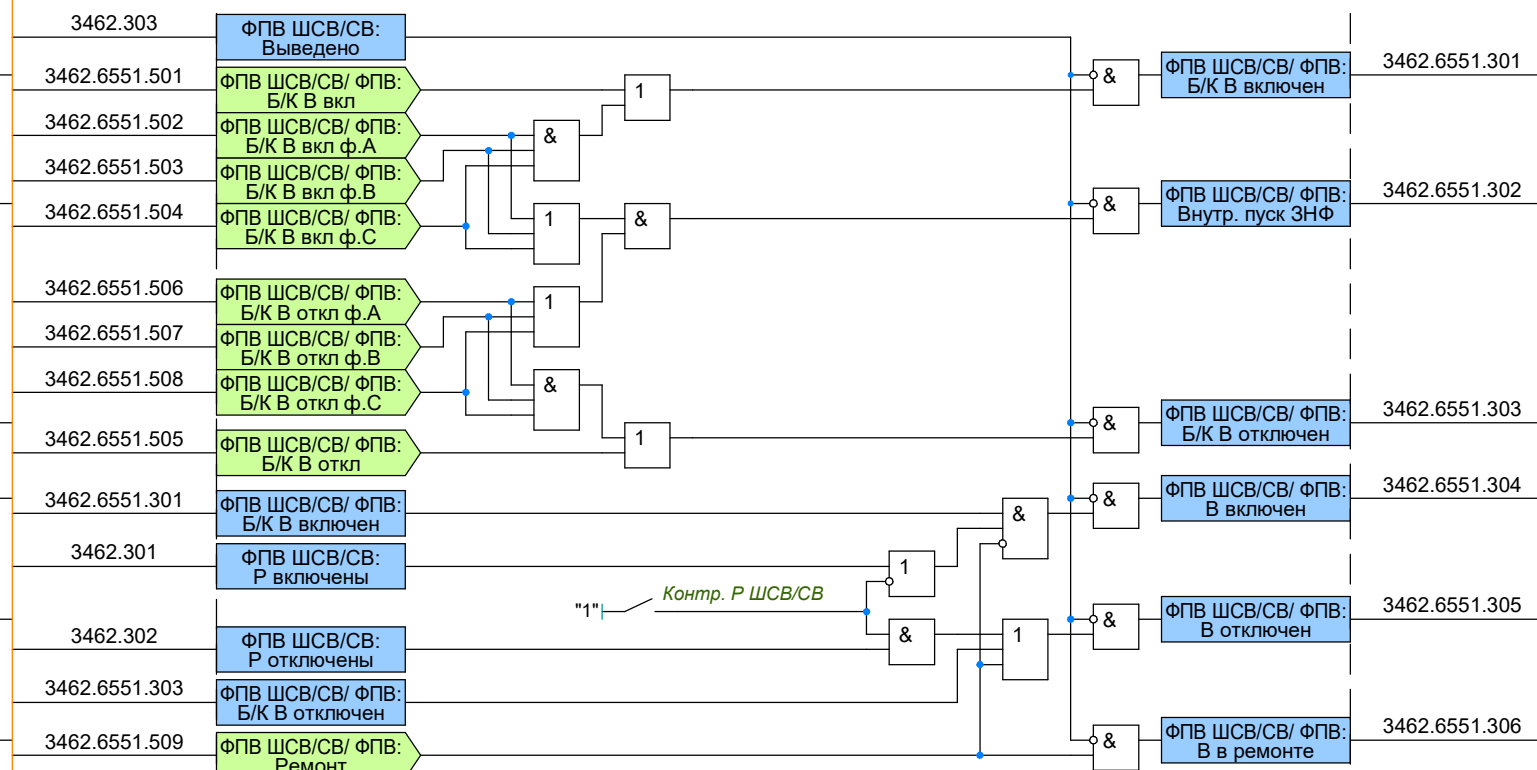

Р1 6531

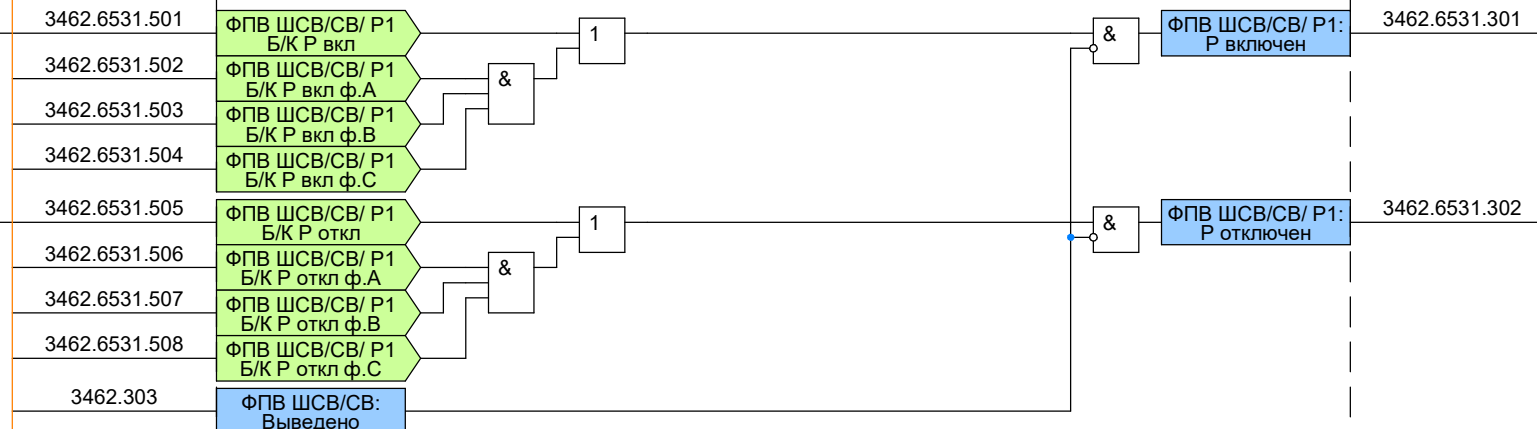

Р2 (6532)

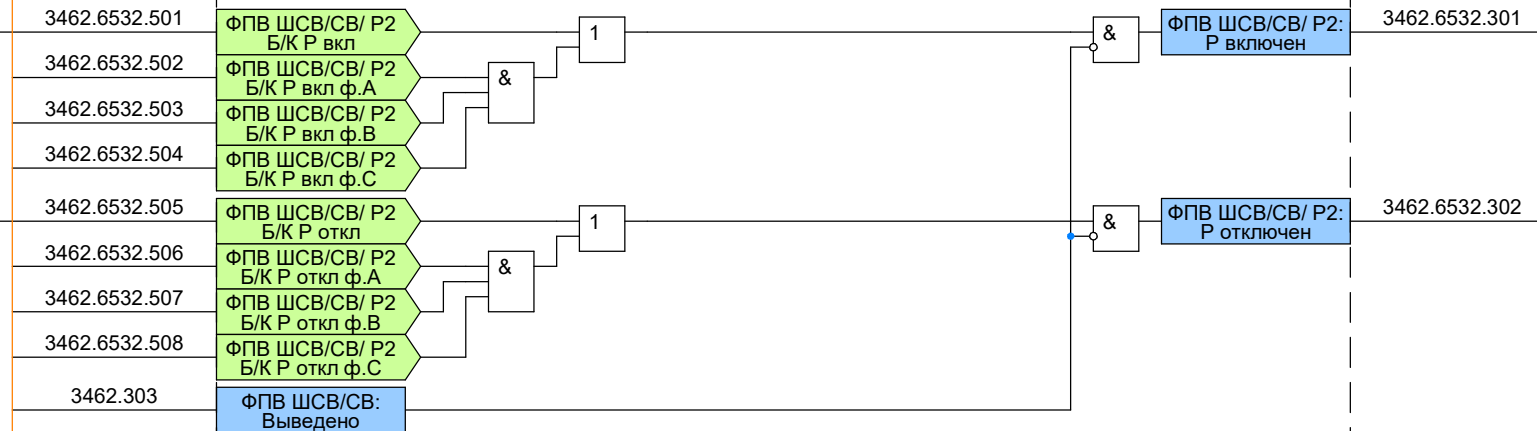

ФПВ ШСВ/СВ/ Р1: Р включены

ФПВ ШСВ/СВ/ Р2: Р включены

ФПВ ШСВ/СВ/ Р1: Р отключены

ФПВ ШСВ/СВ/ Р2: Р отключены

ФПВ ШСВ/СВ: Вывод

Коммутация В2 1822

Коммутация 5301

