




Вид спереди
Дверь условно не показана

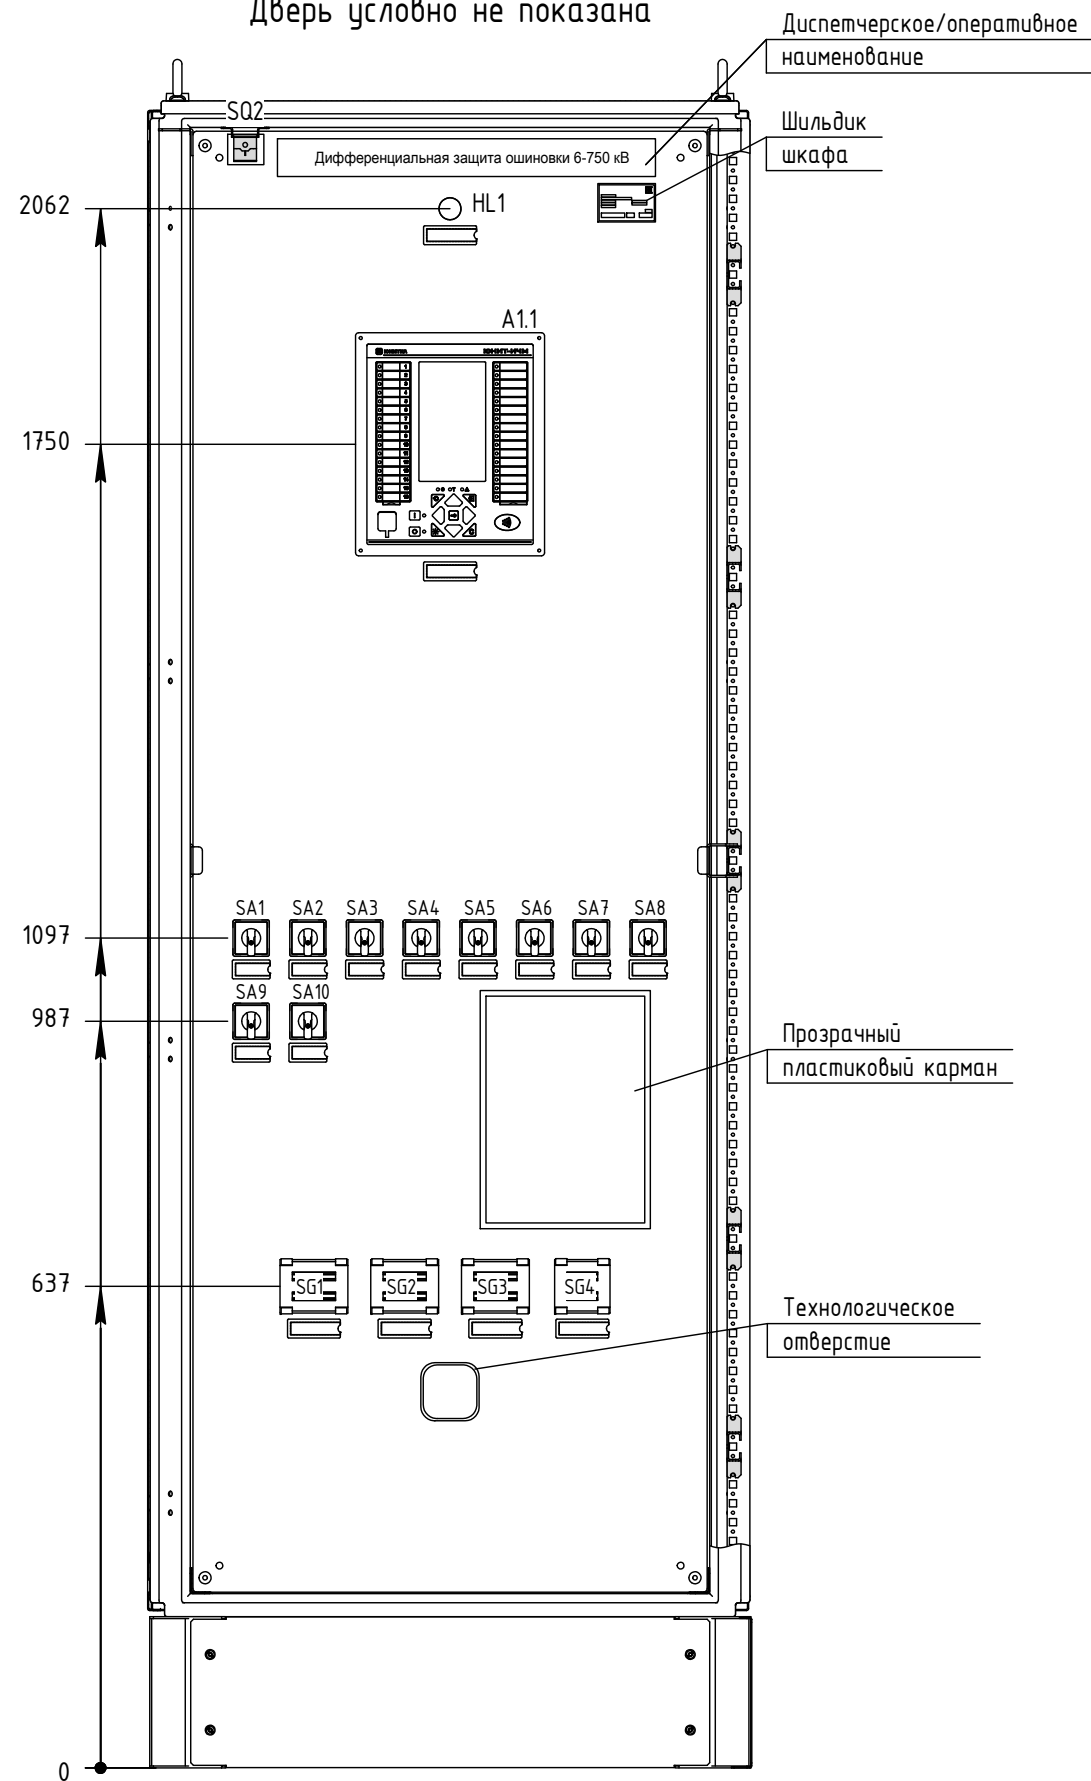

┌ ─ ┐

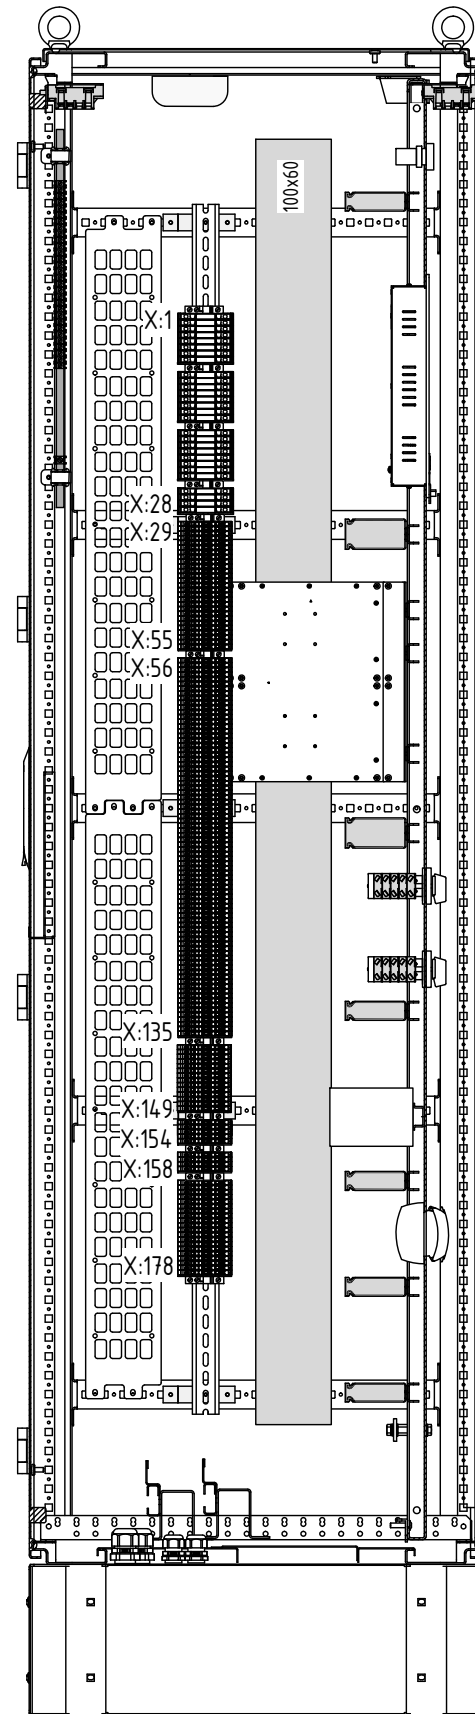

Вид сзади
Дверь, ряды зажимов и вертикальные короба
условно не показаны

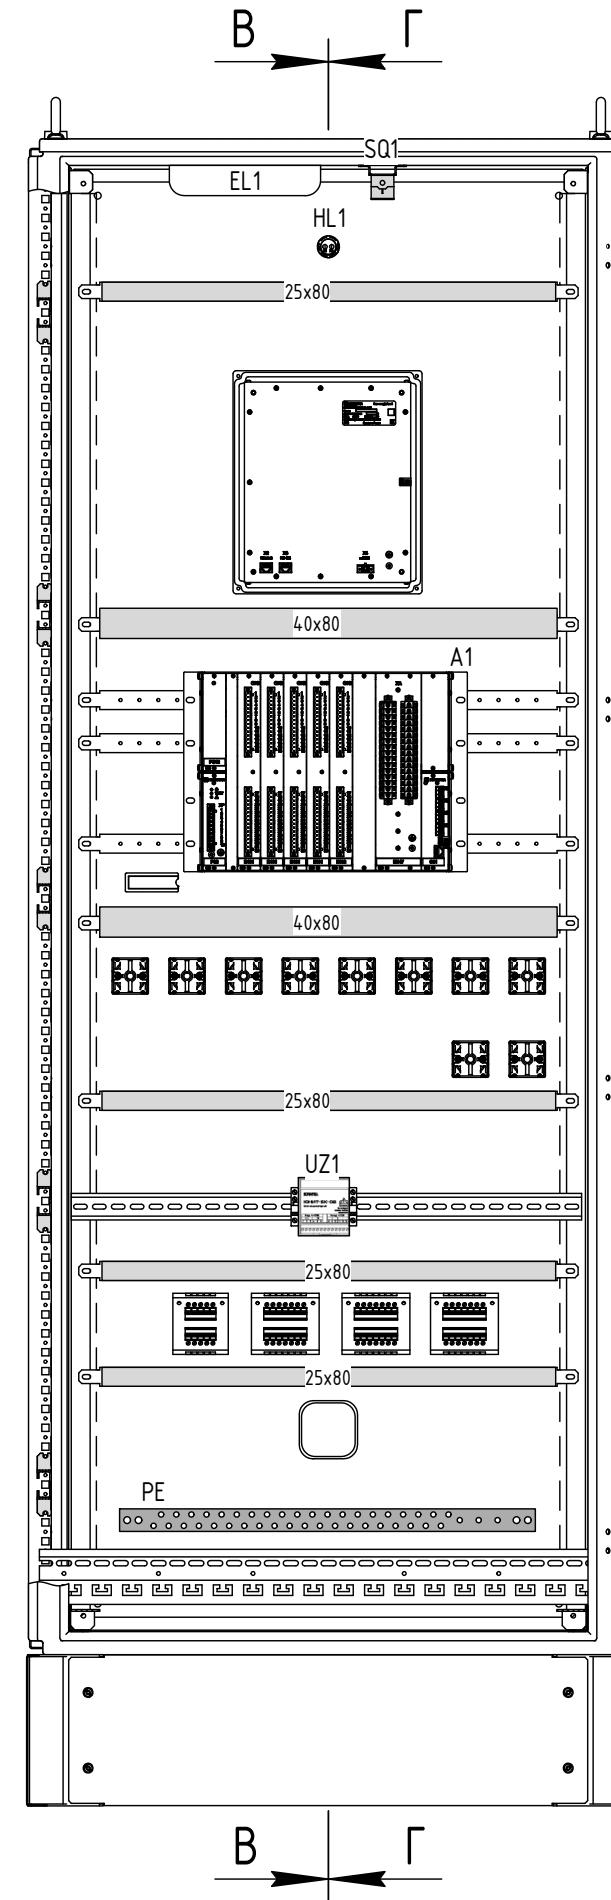

B-B

