


Логика отключения отключающей ступени ГЗ (ЛО ГЗоткл) (TTRGASLGC)


Логика отключения отключающей ступени (ЛО ГЗоткл) (TECHPTRC) PTRC1

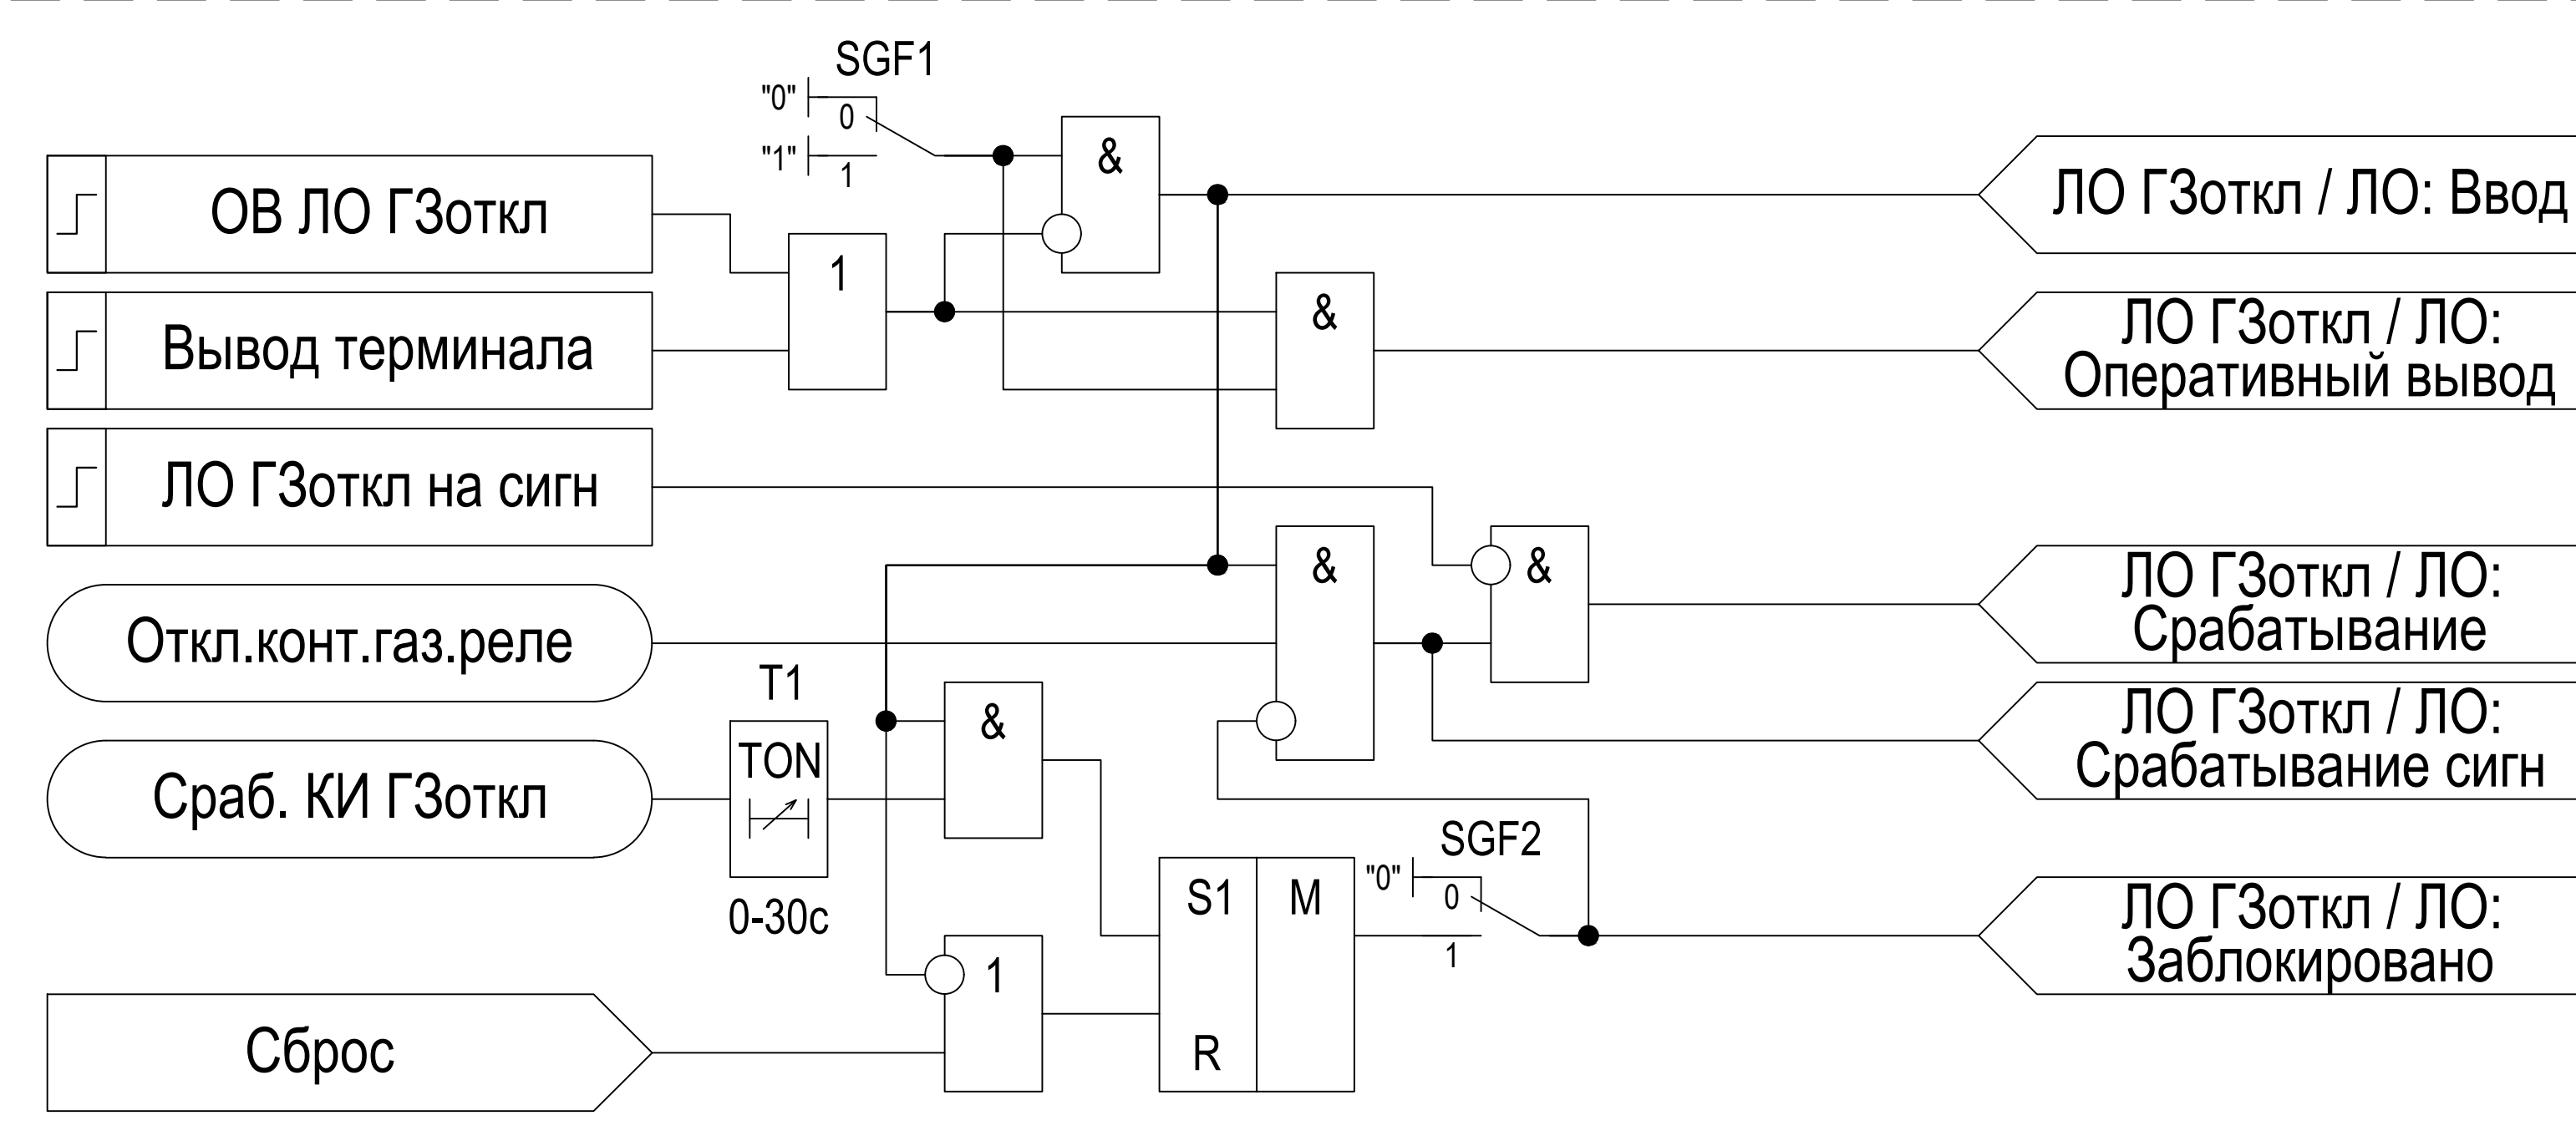

SGF1 - Ввод_функции - Ввод функции в работу (Не предусмотрено/ Предусмотрено)
SGF2 - Блок_от_НИ - Блокировка от низкой изоляции (Не предусмотрено/ Предусмотрено)

Логика отключения сигнальной ступени ГЗ (ЛО ГЗсигн) (TALMGASLGC)

Логика отключения сигнальной ступени (ЛО ГЗсигн) (TECHPTRC) PTRC2

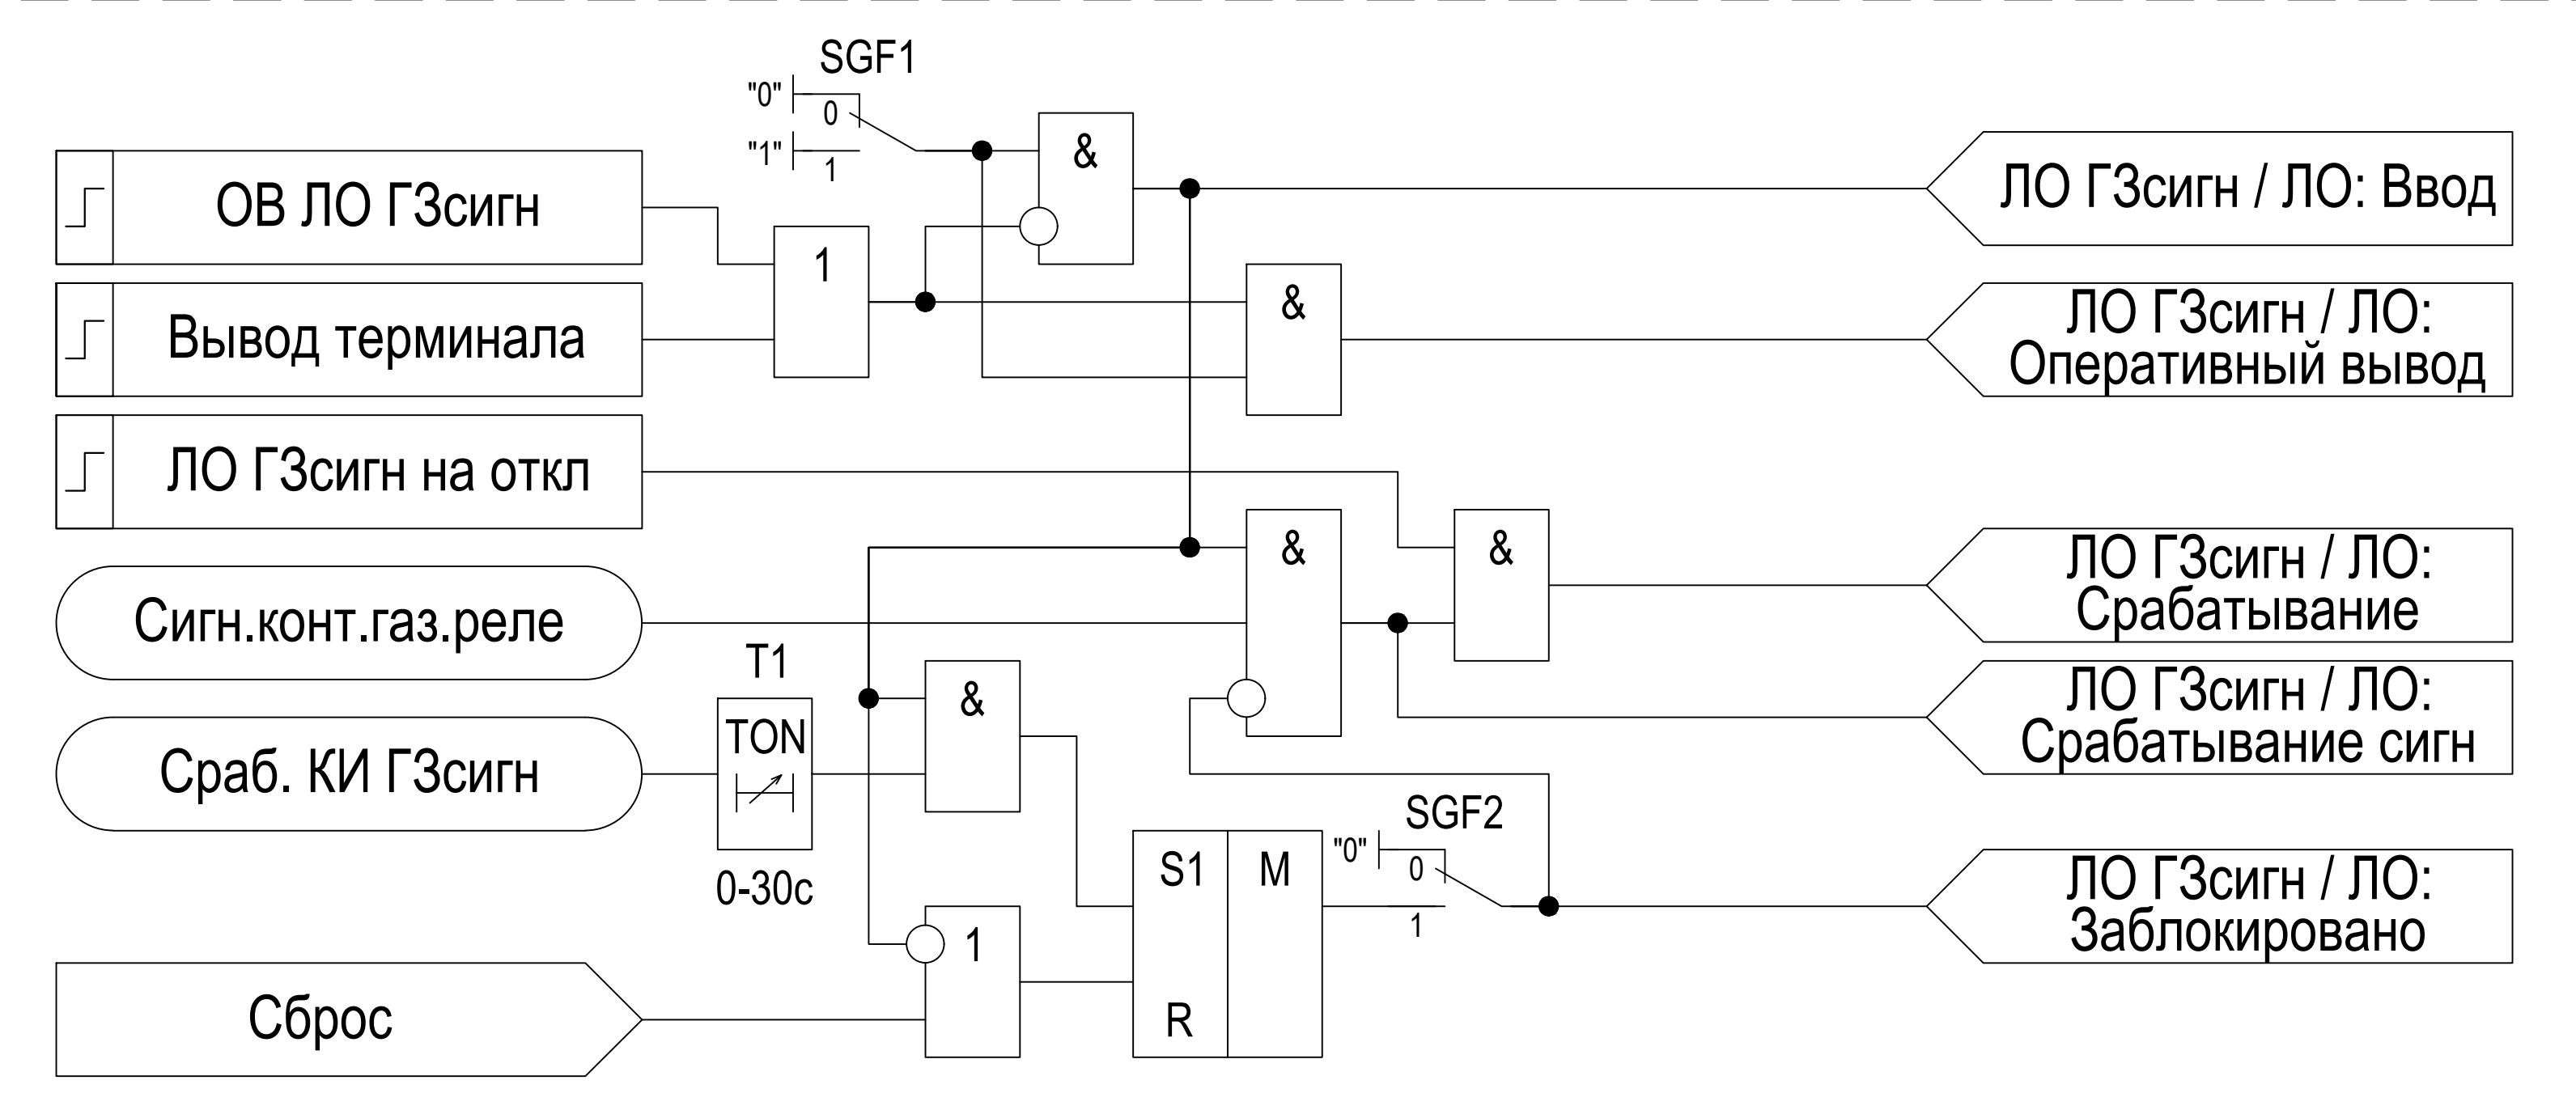

SGF1 - Ввод_функции - Ввод функции в работу (Не предусмотрено/ Предусмотрено)
SGF2 - Блок_от_НИ - Блокировка от низкой изоляции (Не предусмотрено/ Предусмотрено)