



Логика отключения В НН Т 35 (ЛО НН) (LVTCSVOFF)

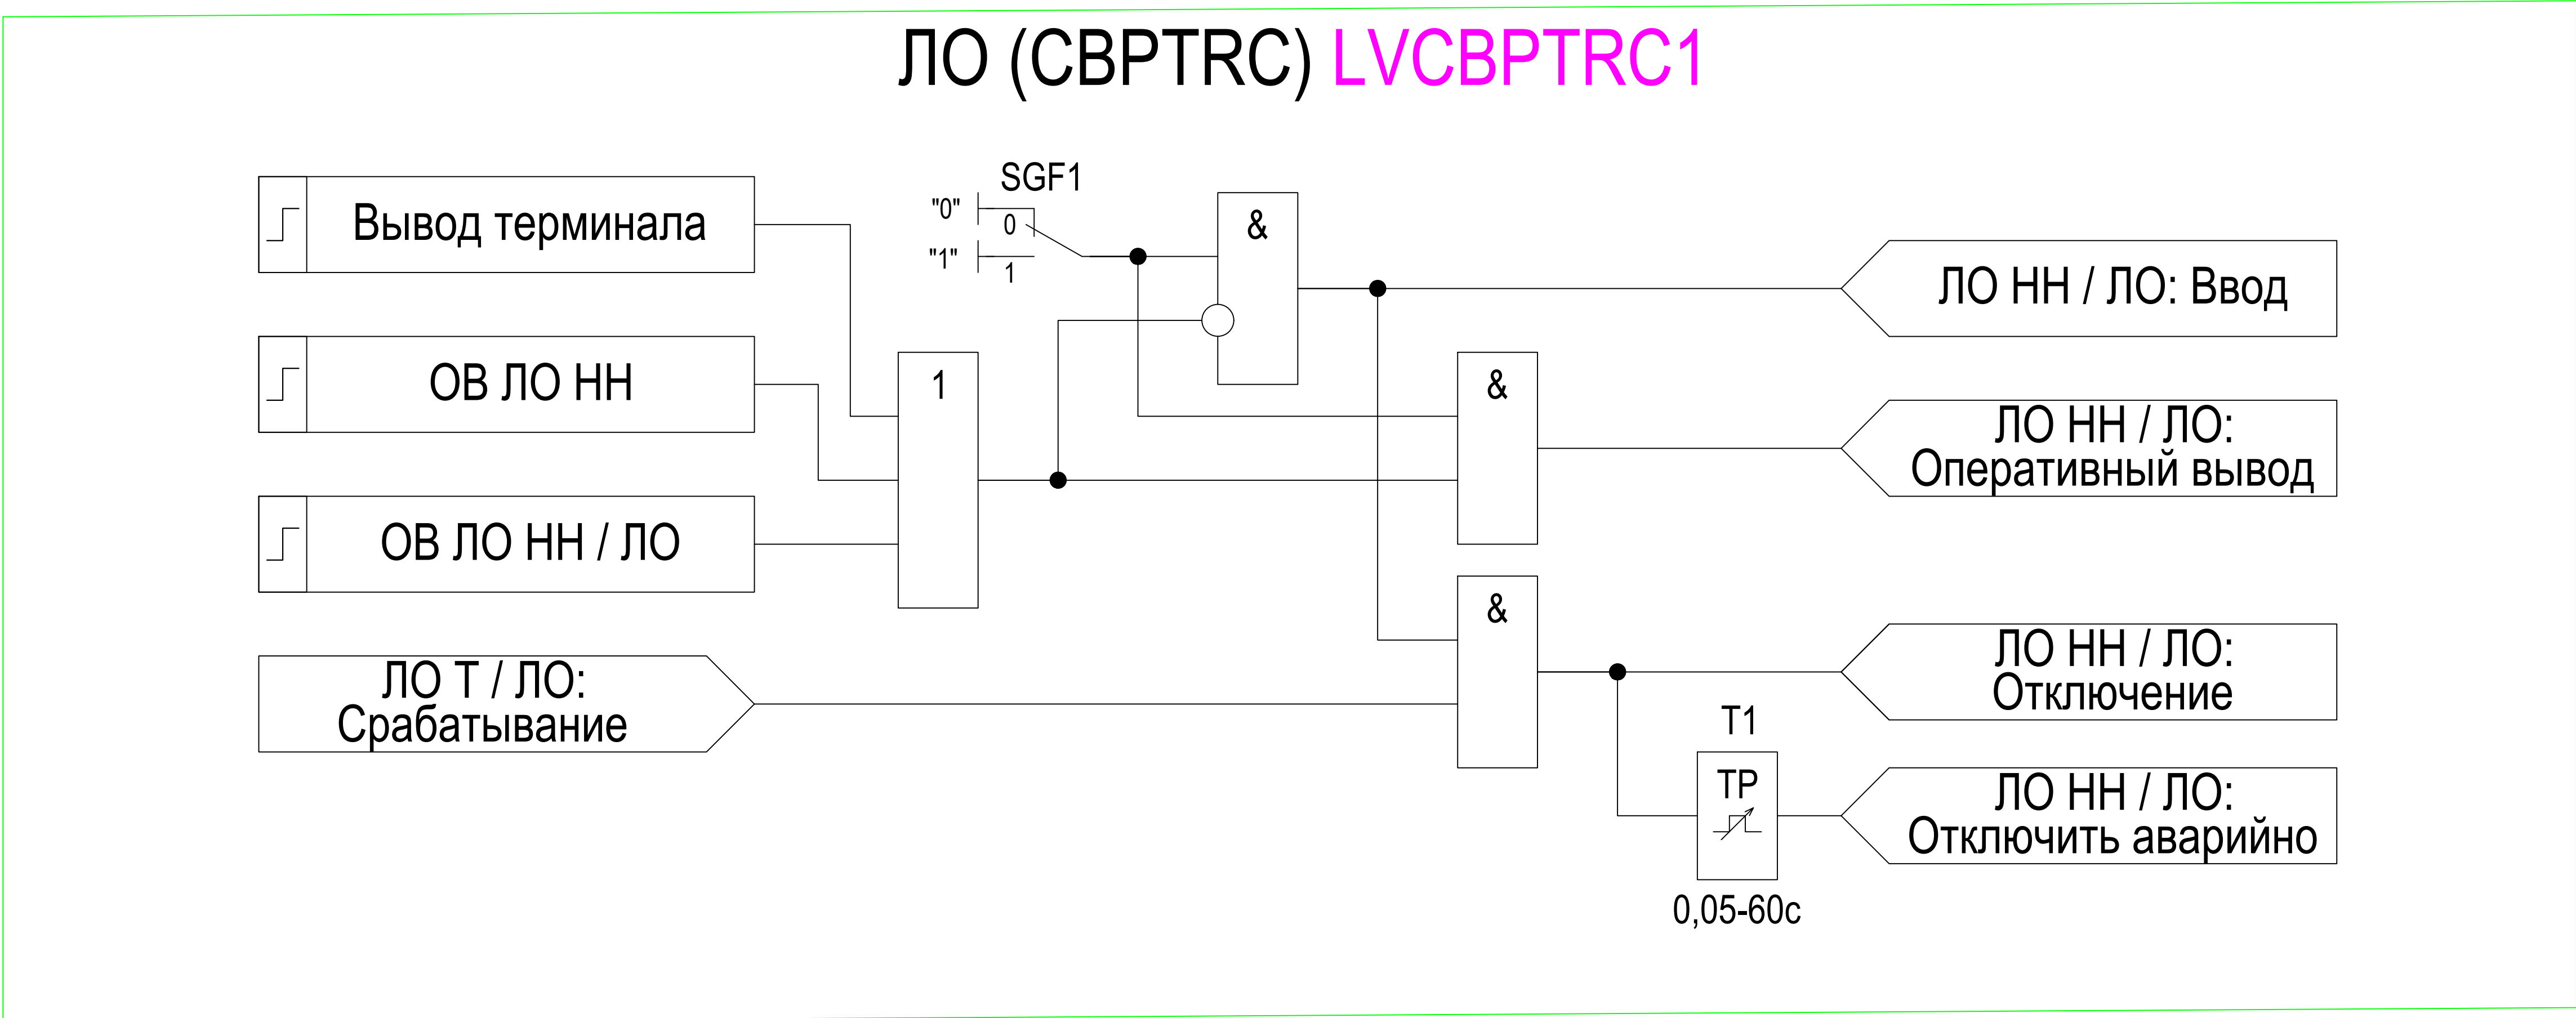

ЗАПВ (JNTRBRE) **LVCBRECRBRE1**

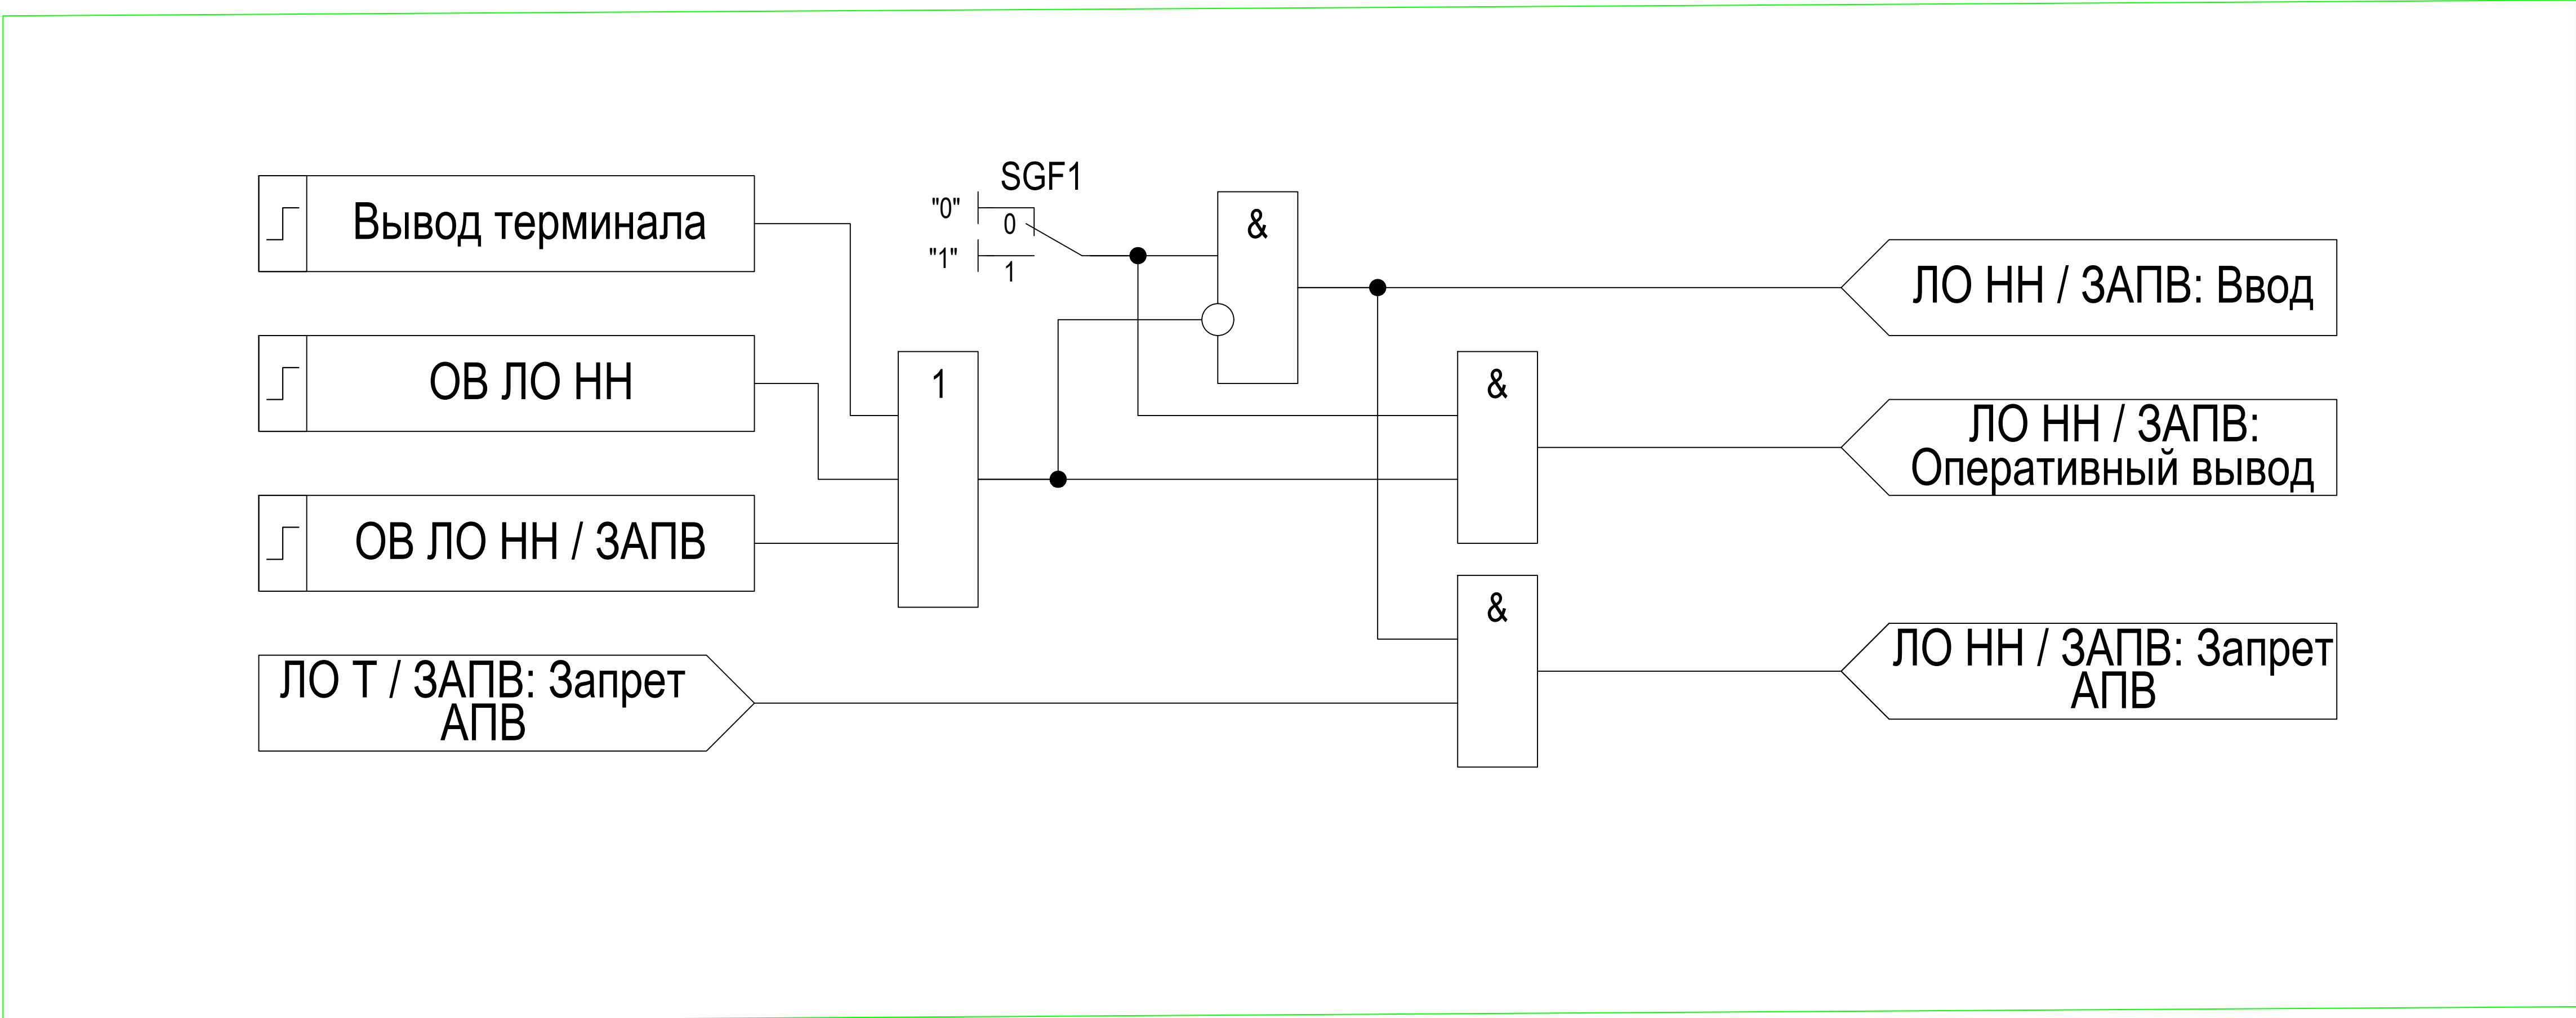

ЗАВР (BTS1RBLC) **LVBTSRBLC1**

