


Для исполнений ЮНИТ-М300-ДЗТ2

Устройство резервирования отказа выключателя стороны ВН (УРОВ ВН) (TPBRF)

Устройство резервирования при отказе выключателя (УРОВ) (TPBRF) RBRF1

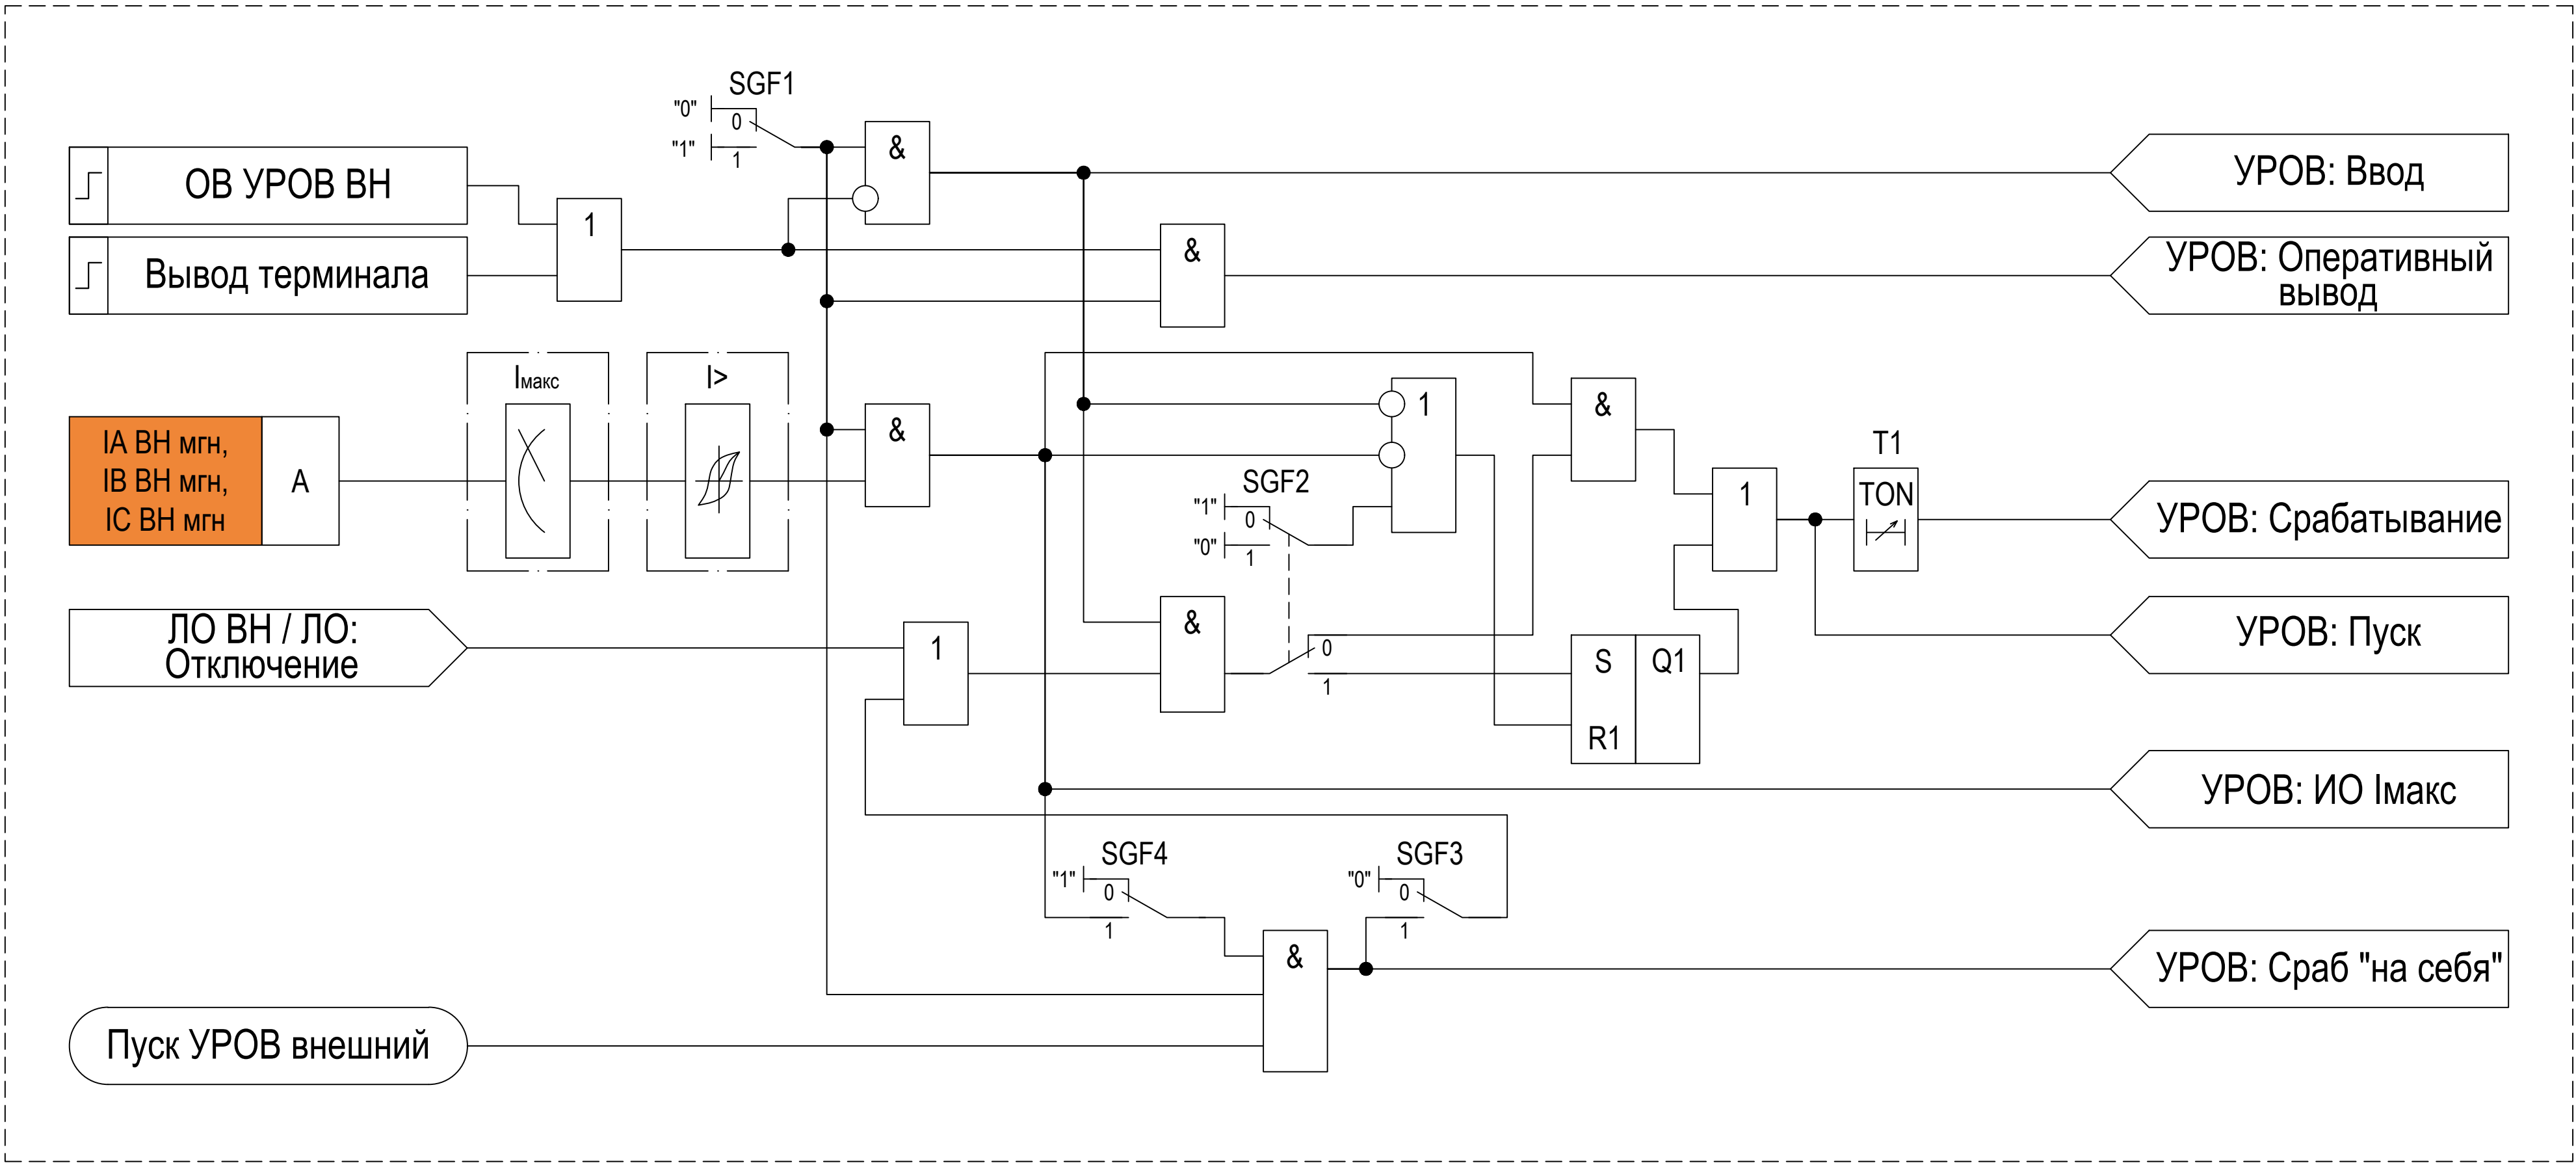

- SGF1 - Ввод функции в работу (Не предусмотрено/ Предусмотрено)
- SGF2 - УРОВ с подхватом по току (Не предусмотрено/ Предусмотрено)
- SGF3 - Действие внешнего УРОВ на вышестоящий выключатель (Не предусмотрено/ Предусмотрено)
- SGF4 - Контроль по току при действии "на себя" (Не предусмотрено/ Предусмотрено)