


Защита от обрыва провода (ЗОП) (LVNSTOC)

Защита от обрыва провода (ЗОП) (LVNSPTOC) NSPTOC1

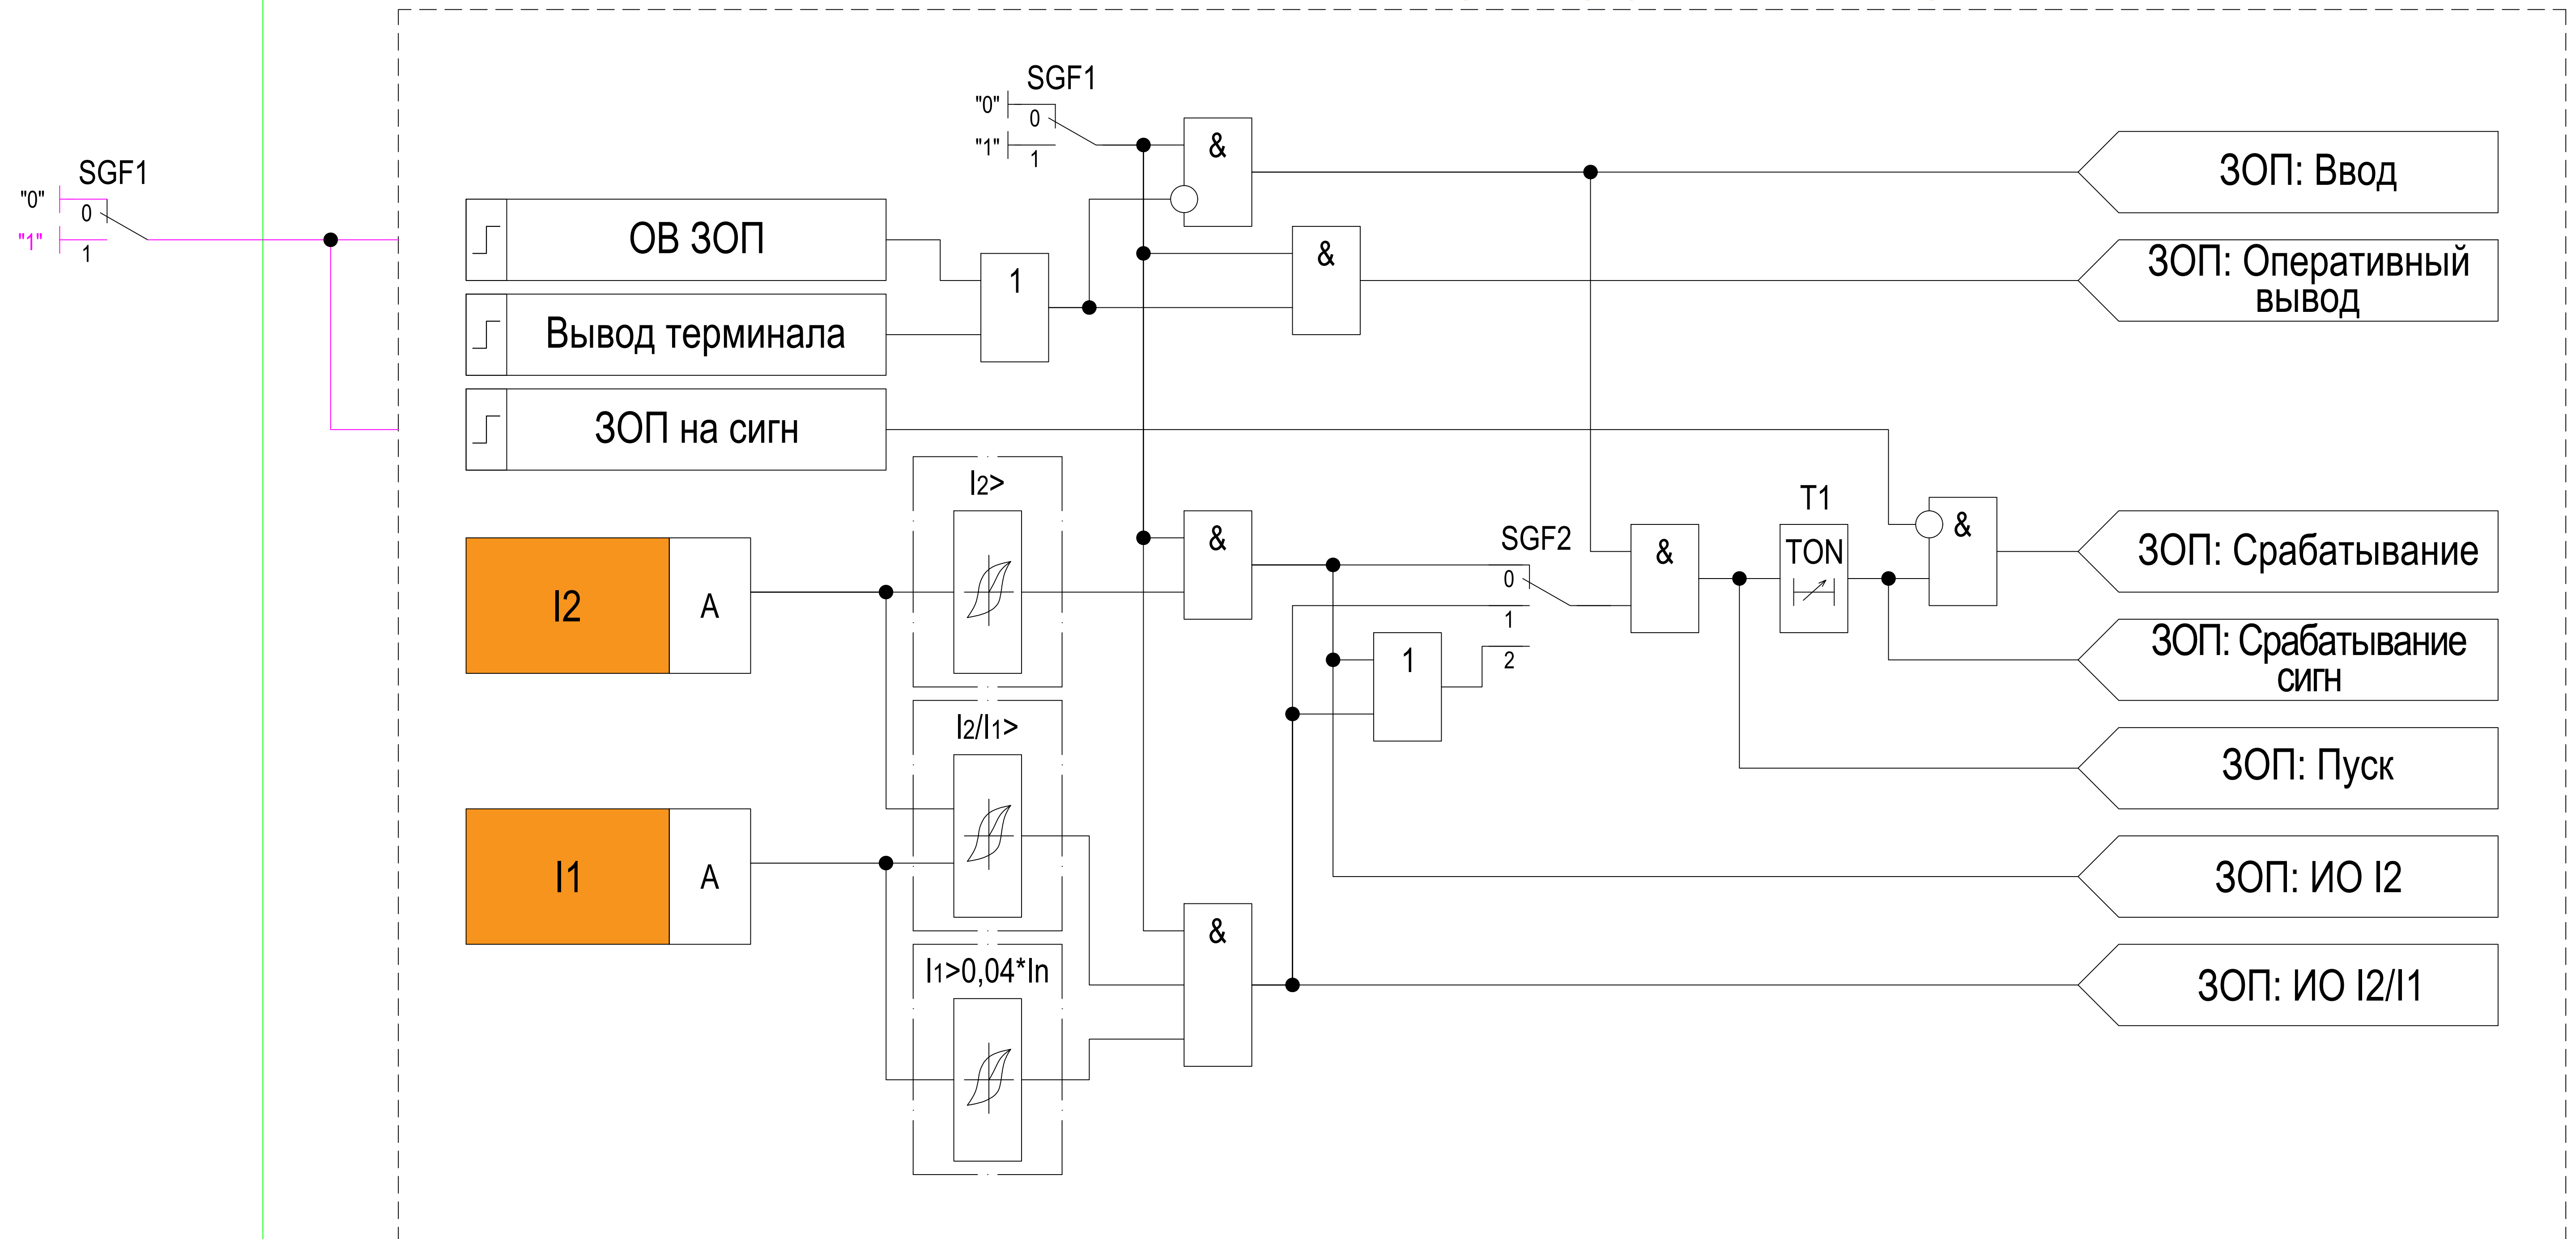

SGF1 - Ввод_функции - Ввод функции в работу (Не предусмотрено/ Предусмотрено)

SGF2 - Реж_ЗОП - Режим работы ЗОП (По току I_2 / По отношению I_2/I_1 / По току I_2 или отношению I_2/I_1)