

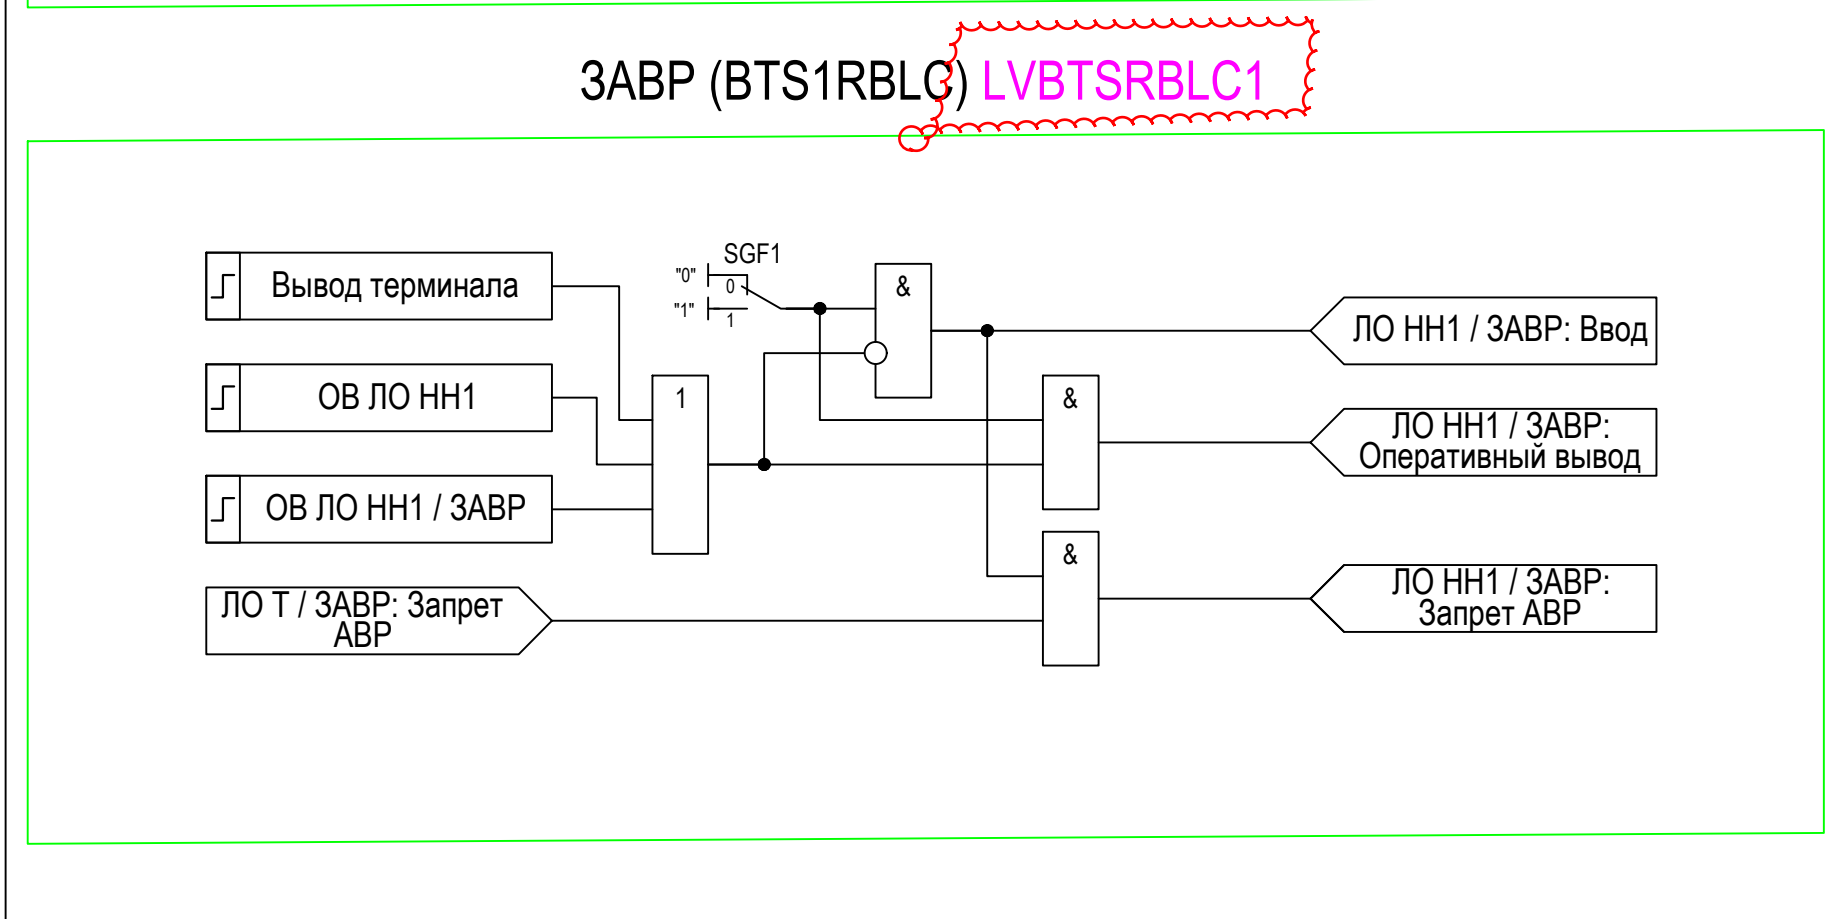


Логика отключения В НН1 Т 35 (ЛО НН1) (LVTRESCBOFF1)

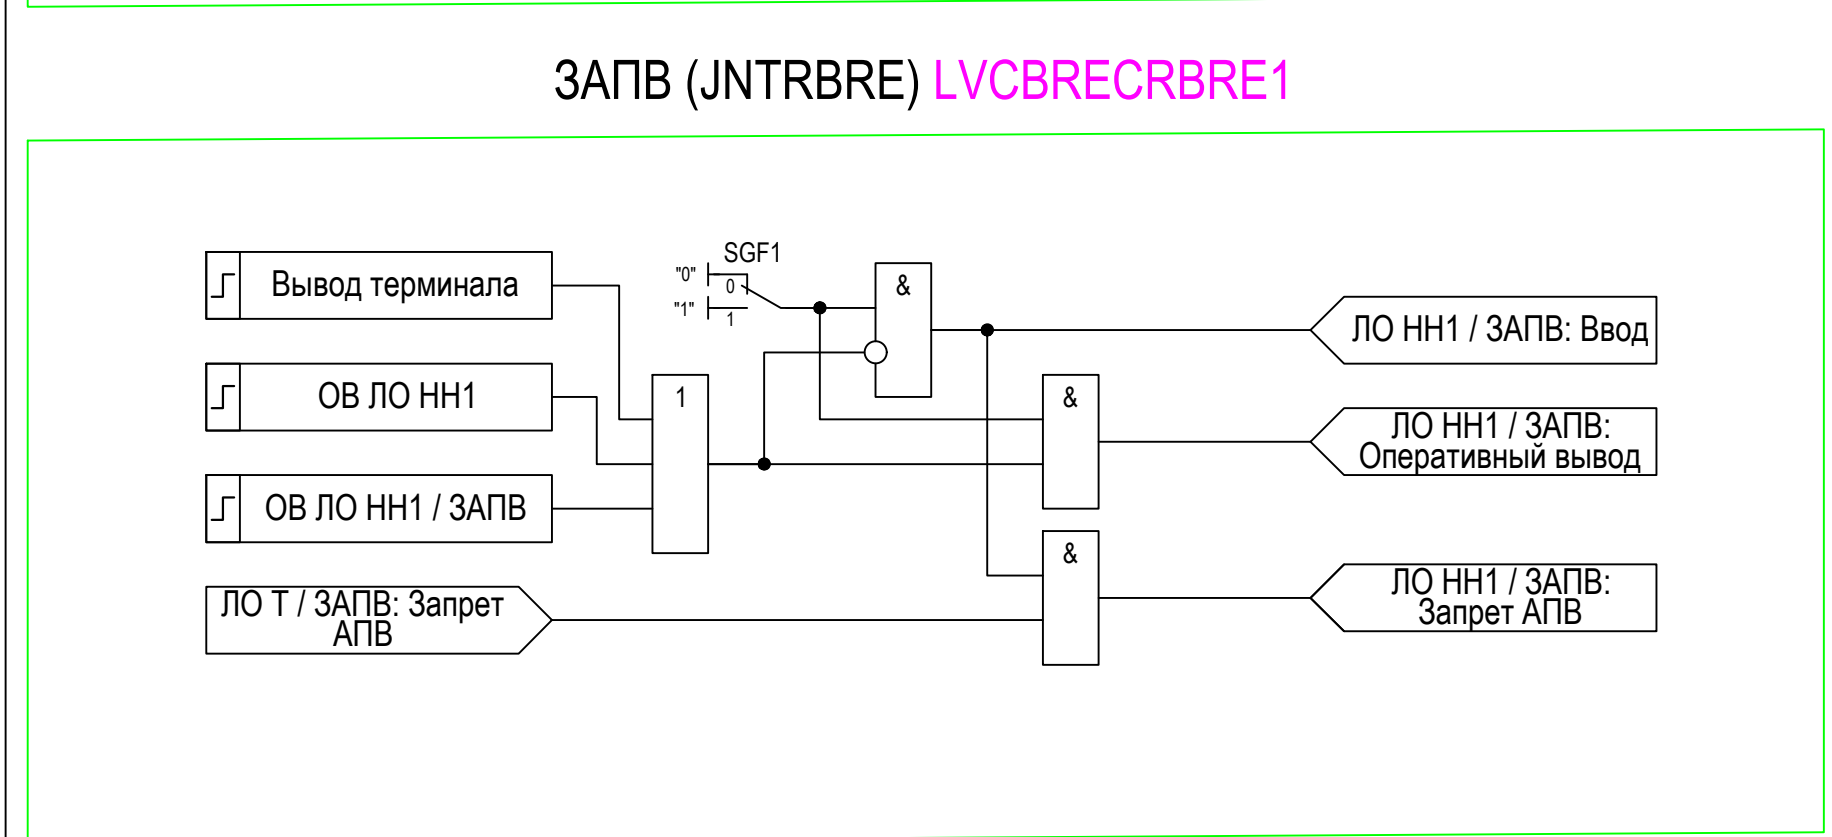

Логика отключения В НН2 Т 35 (ЛО НН2) (LVTRESCBOFF2)

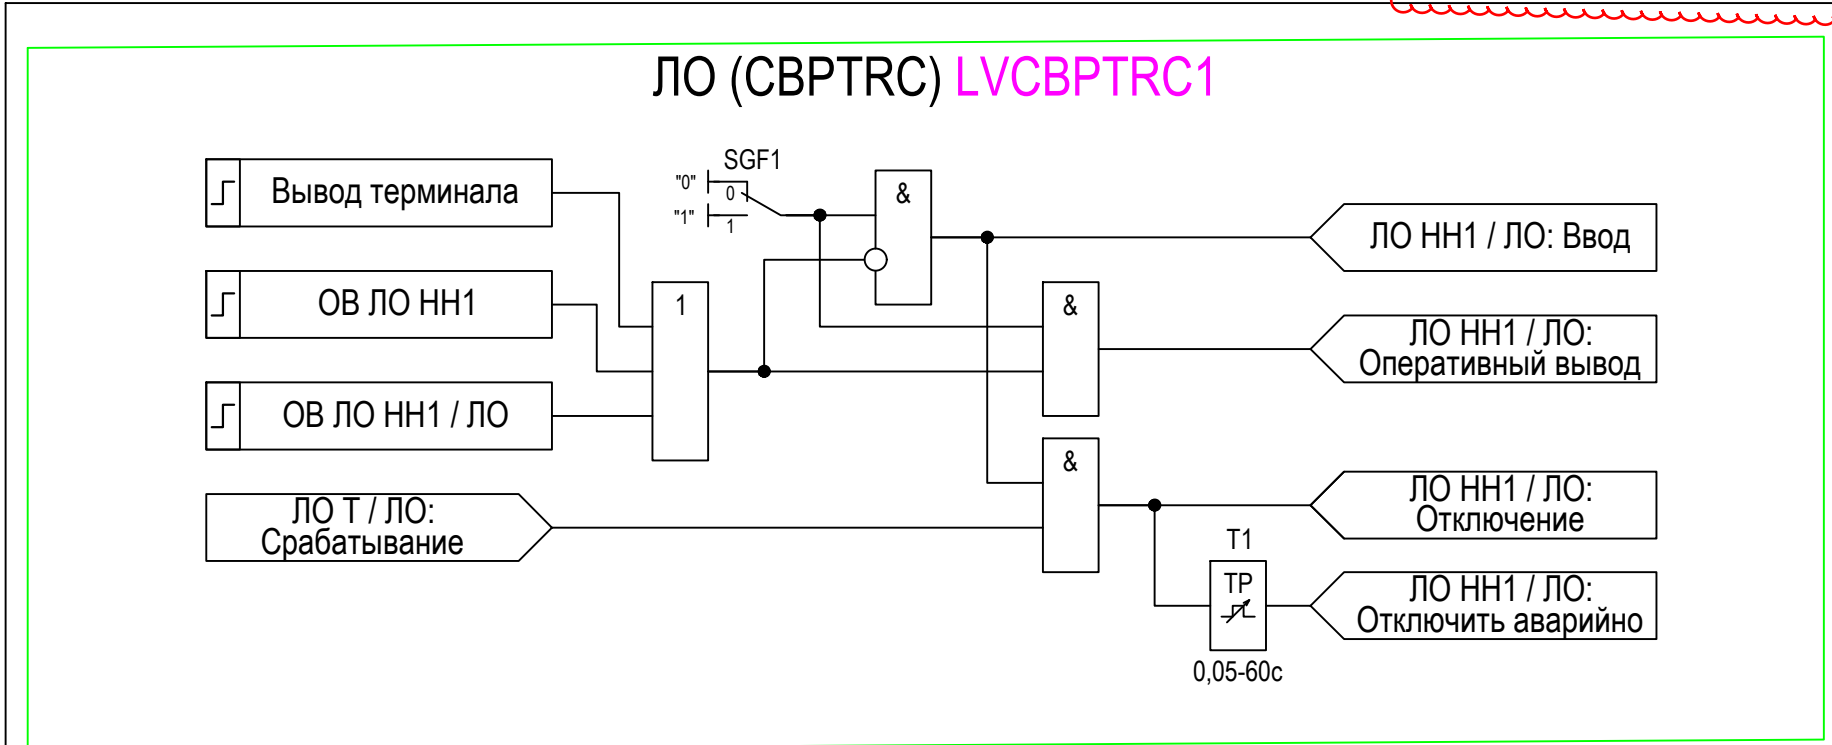