

Поясняющая схема


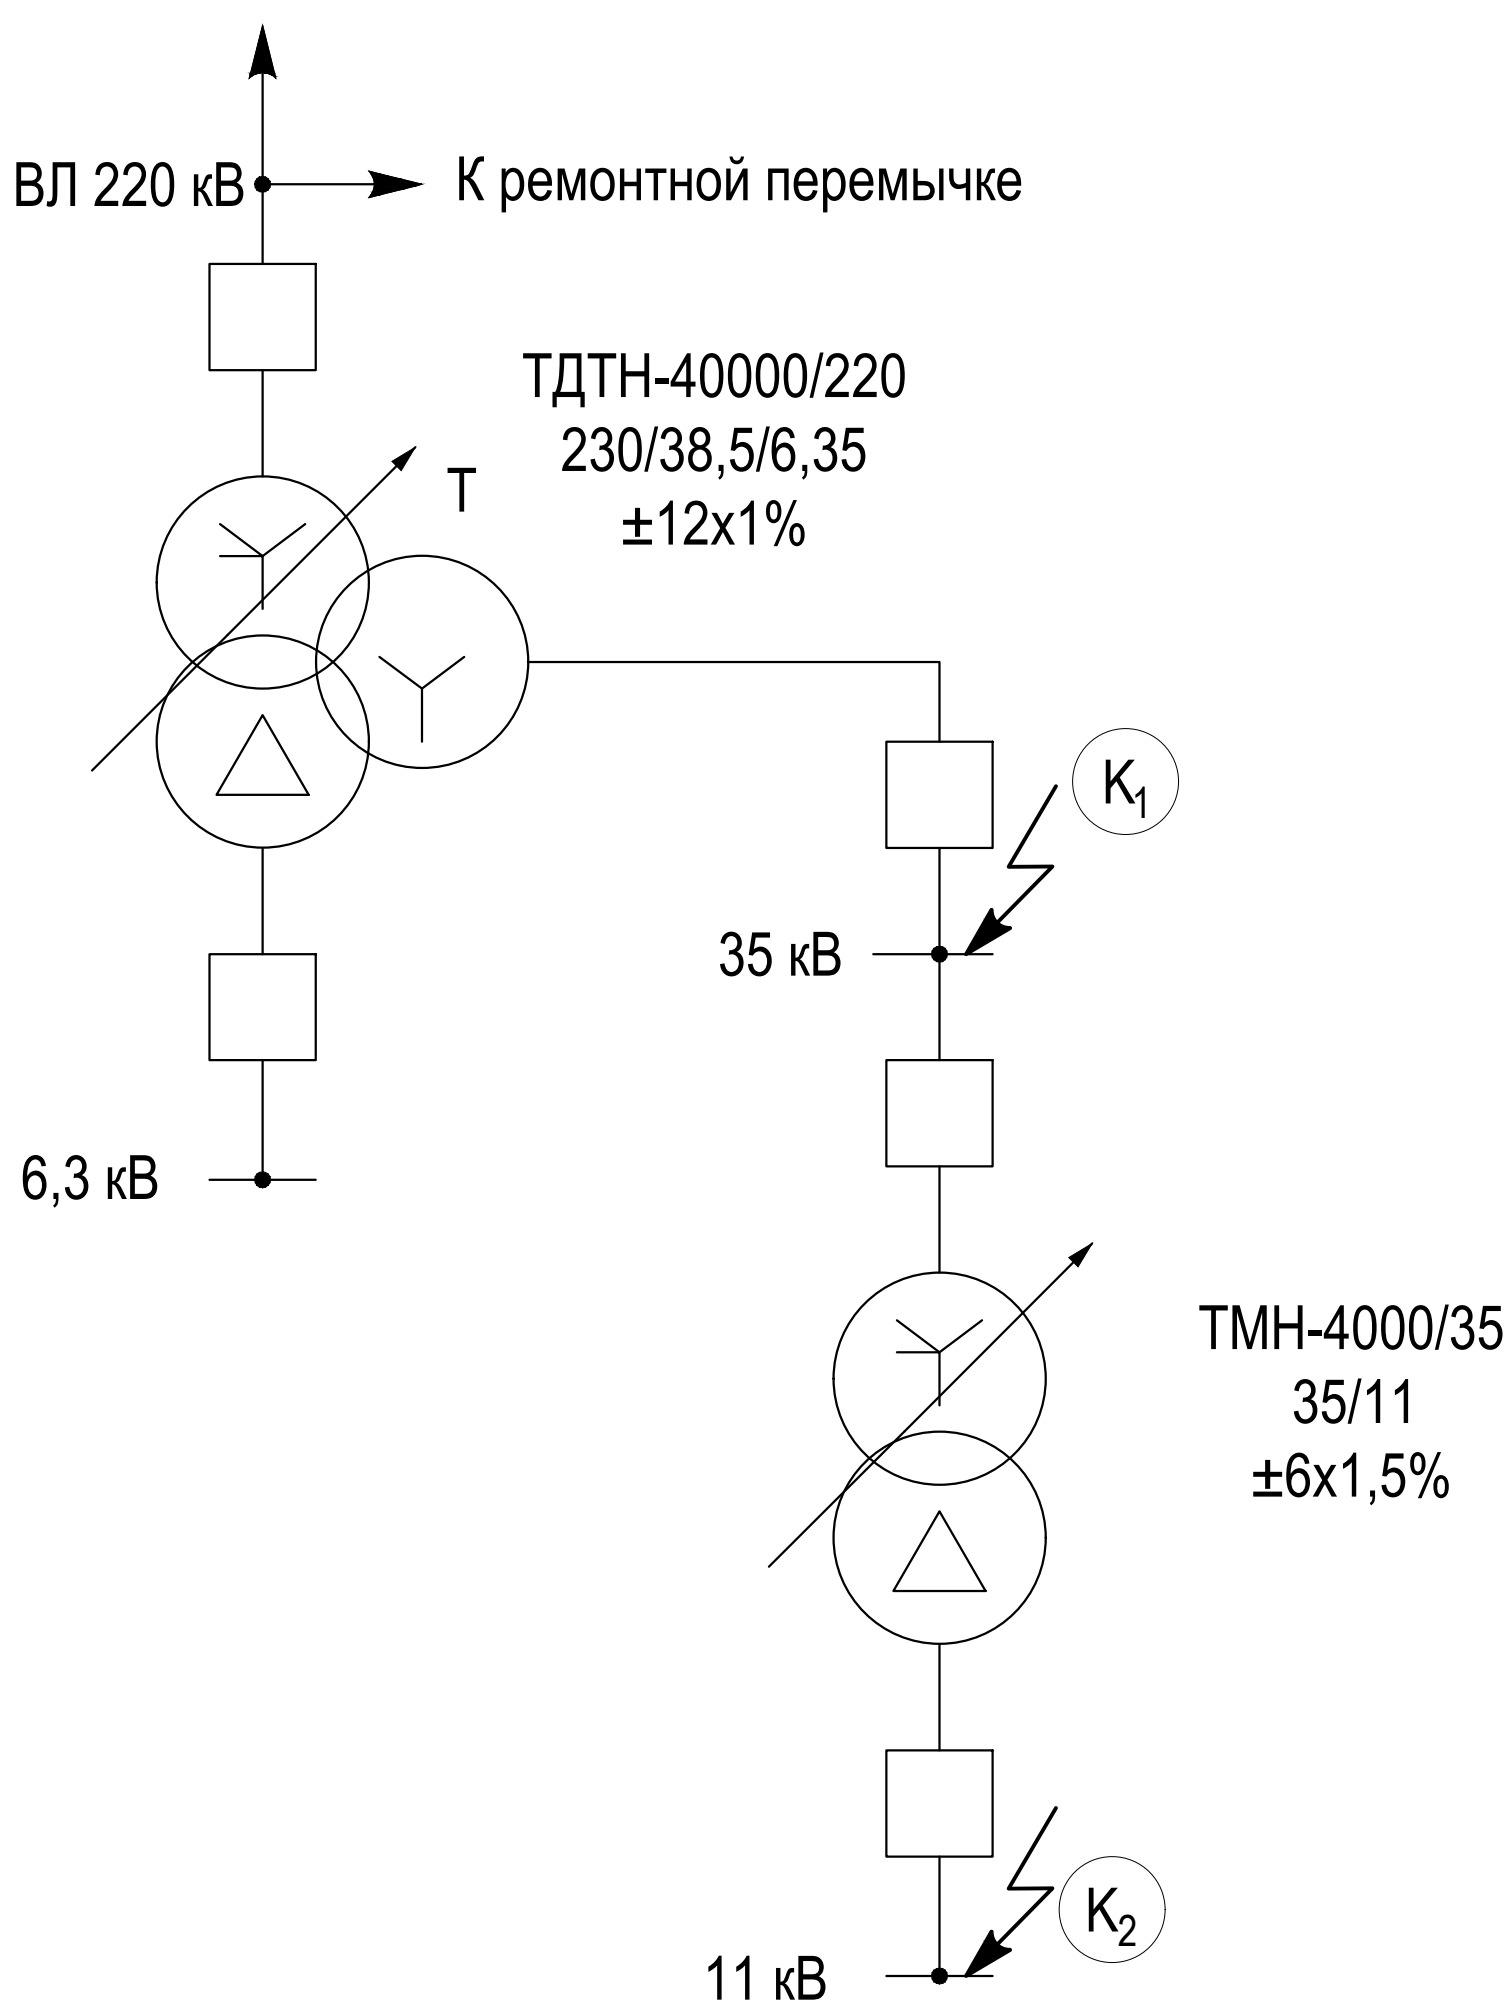


Схема замещения

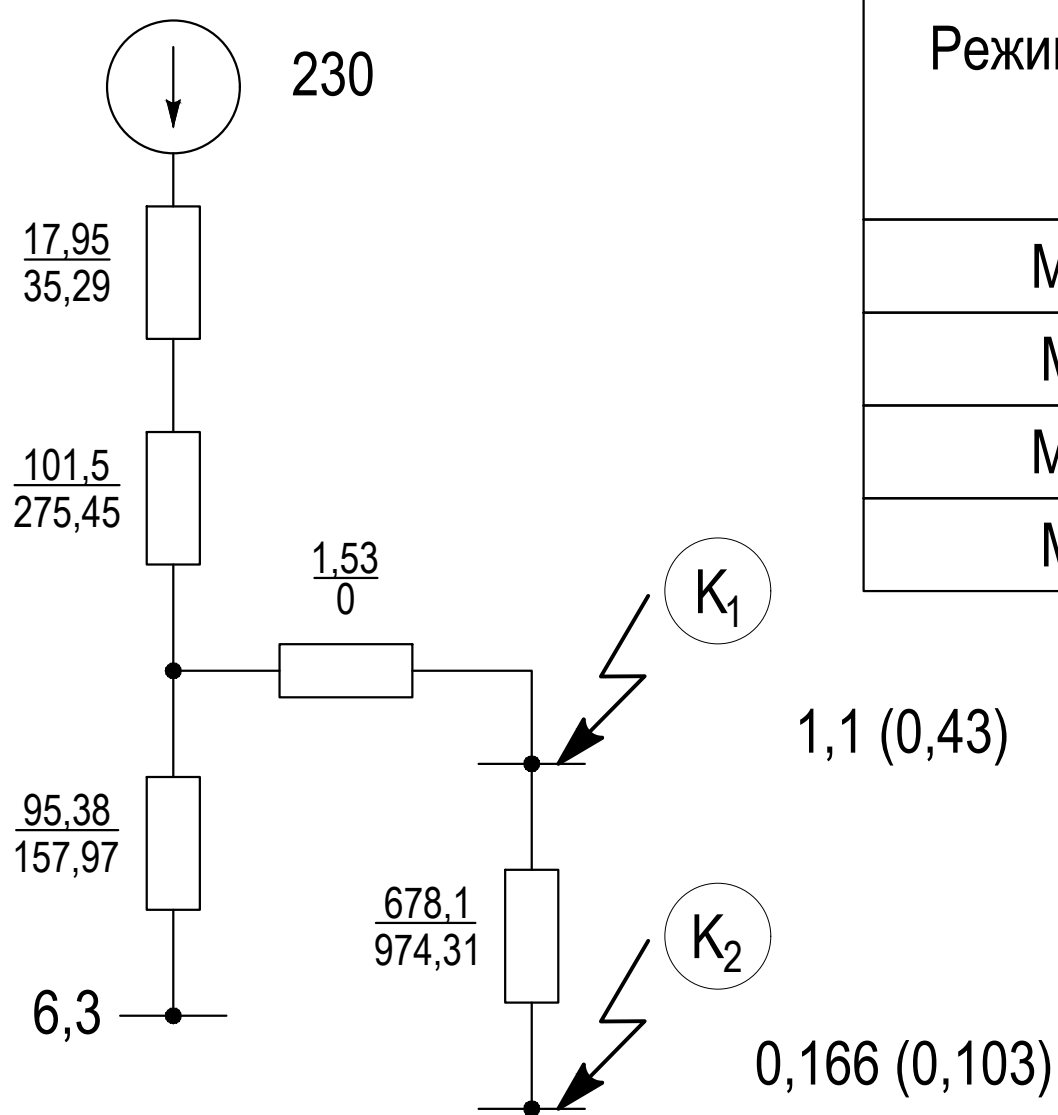

Результаты расчета токов КЗ

Режим работы системы	Точка КЗ	Ток 3х фазного КЗ (А), приведенный к напряжению		
		220 кВ	35 кВ	10 кВ
Максимальный	К2	166	581	3470
Минимальный	К2	103	361	2154
Максимальный	К1	1100	6570	-
Минимальный	К1	430	2570	-

Примечания

1. Сопротивления на схеме замещения указаны в Омах и приведены к напряжению 220 кВ.
2. Значения токов КЗ на рисунке указаны в кА и приведены к стороне 220 кВ. В скобках указаны токи в минимальном режиме.
3. В схеме замещения:
95,38 - сопротивление в максимальном режиме
157,97 - сопротивление в минимальном режиме