

Поясняющая схема


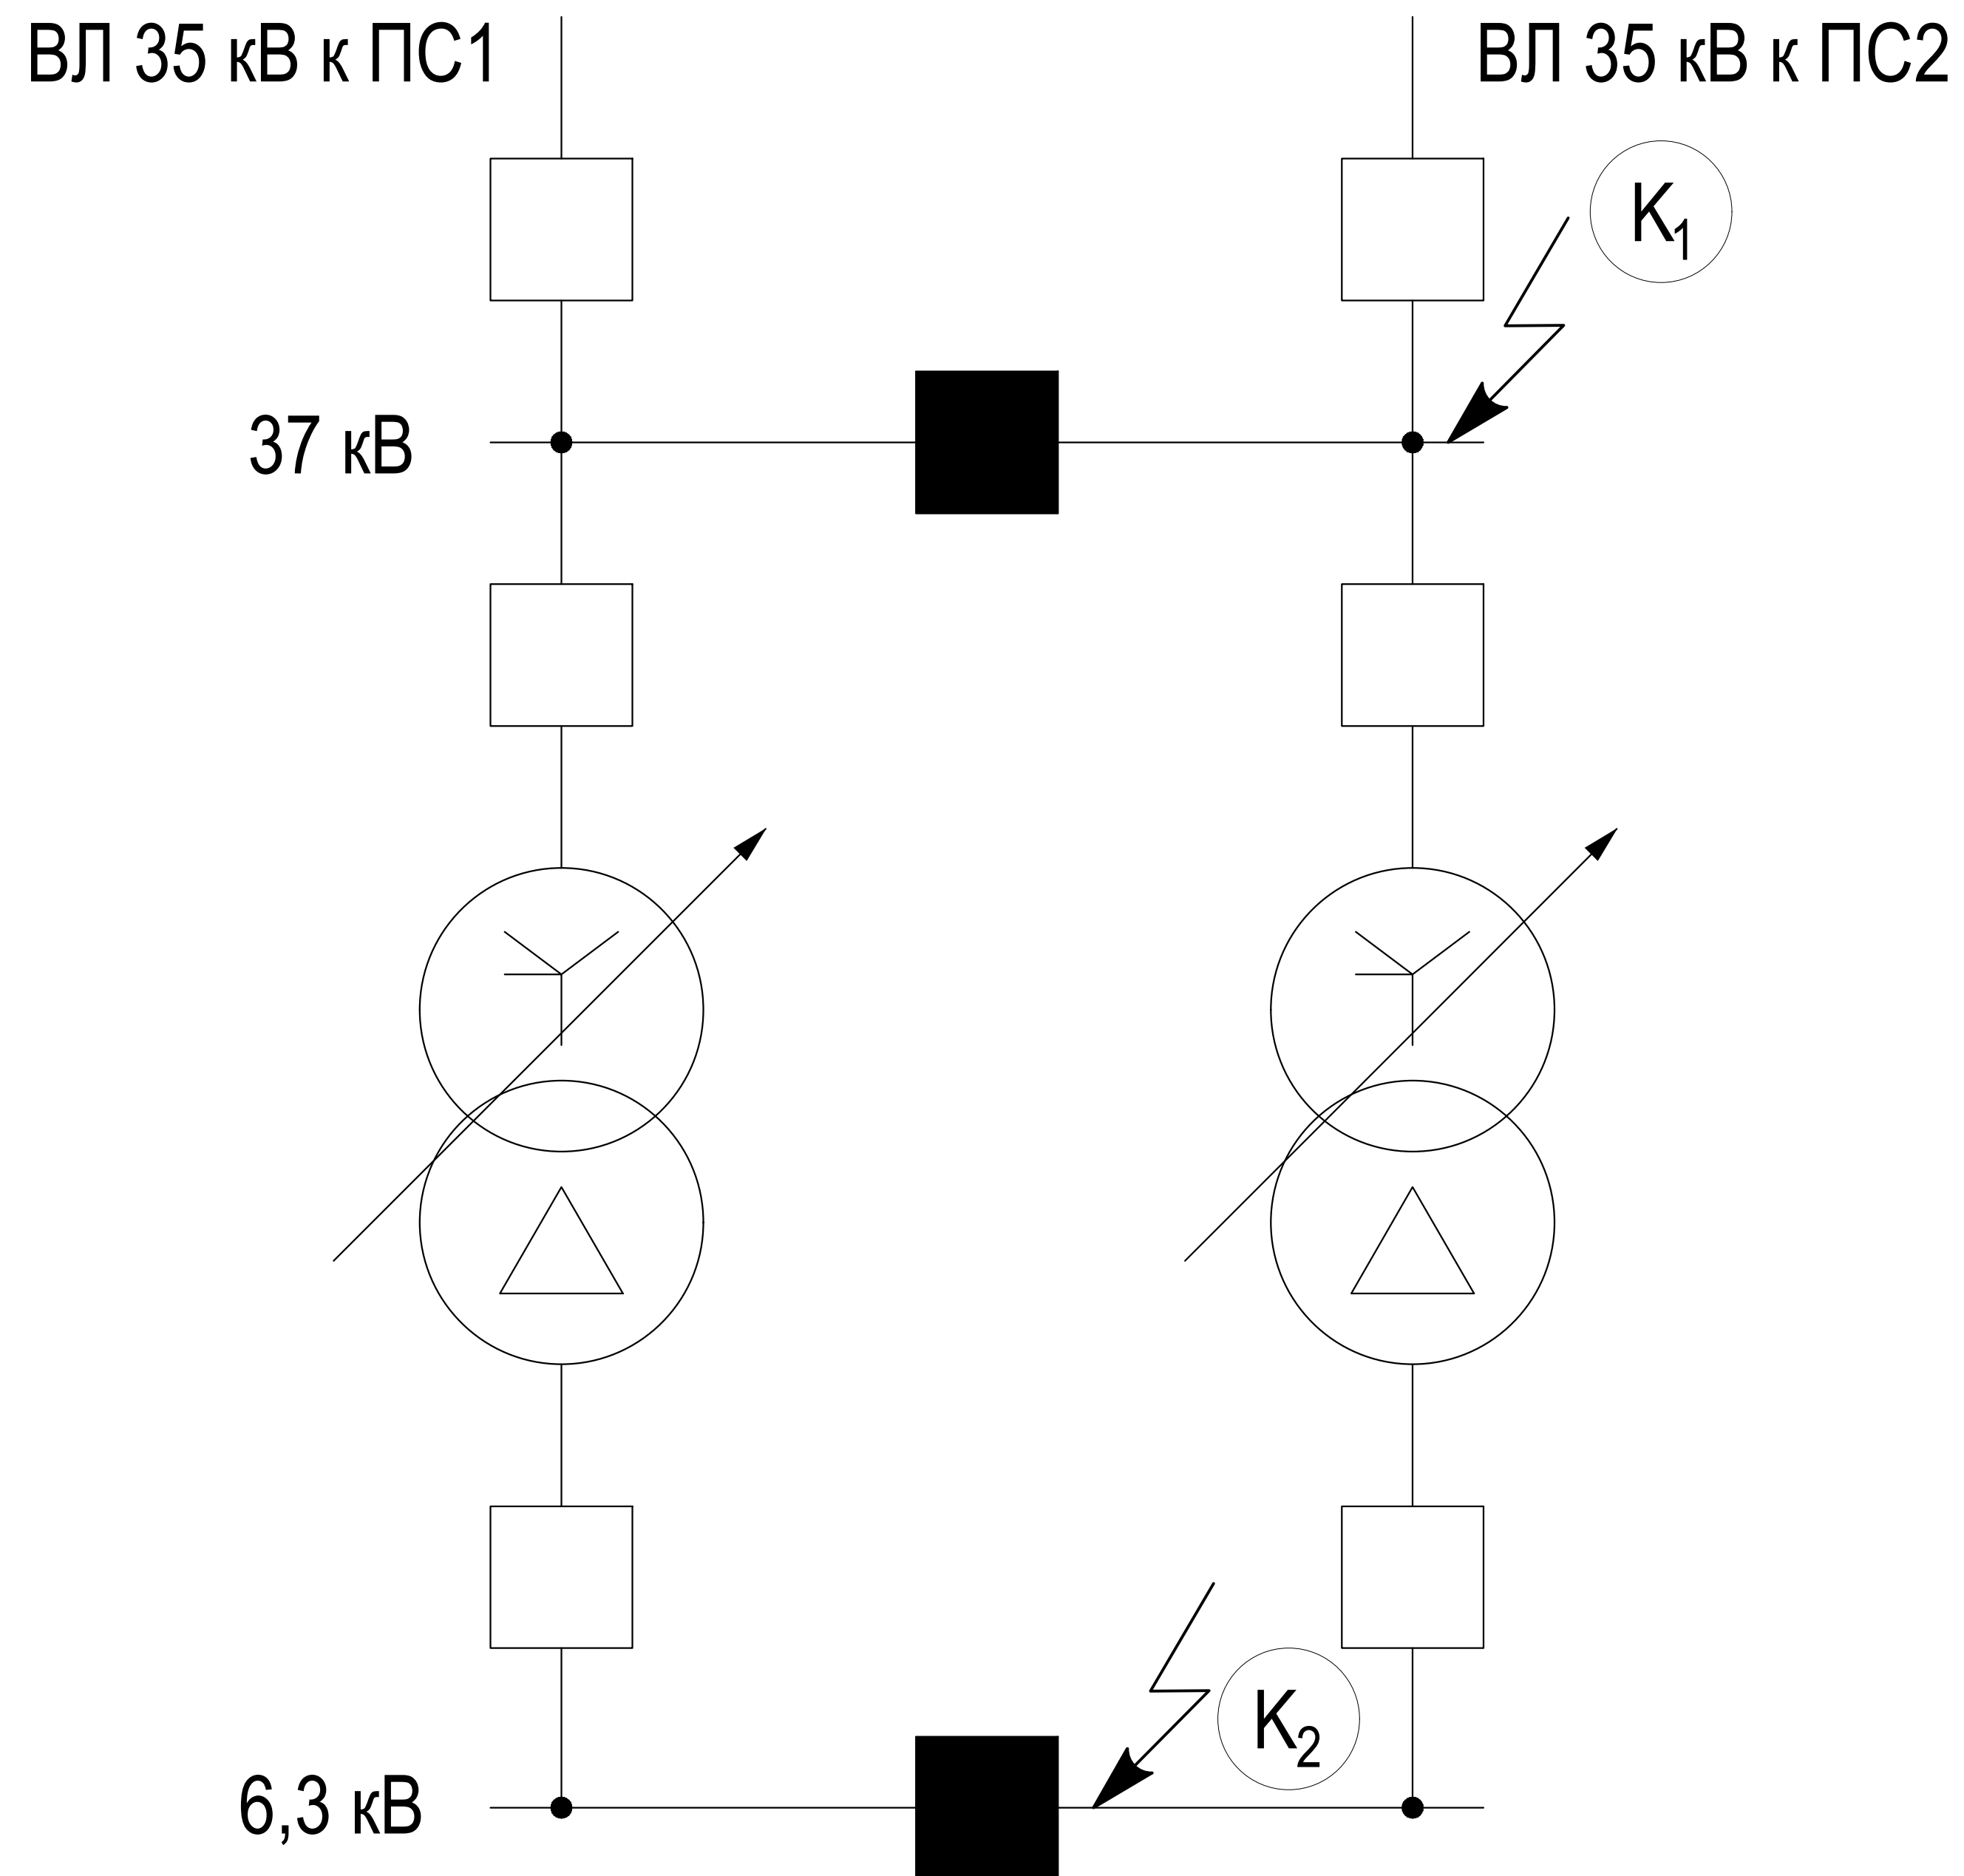


Схема замещения

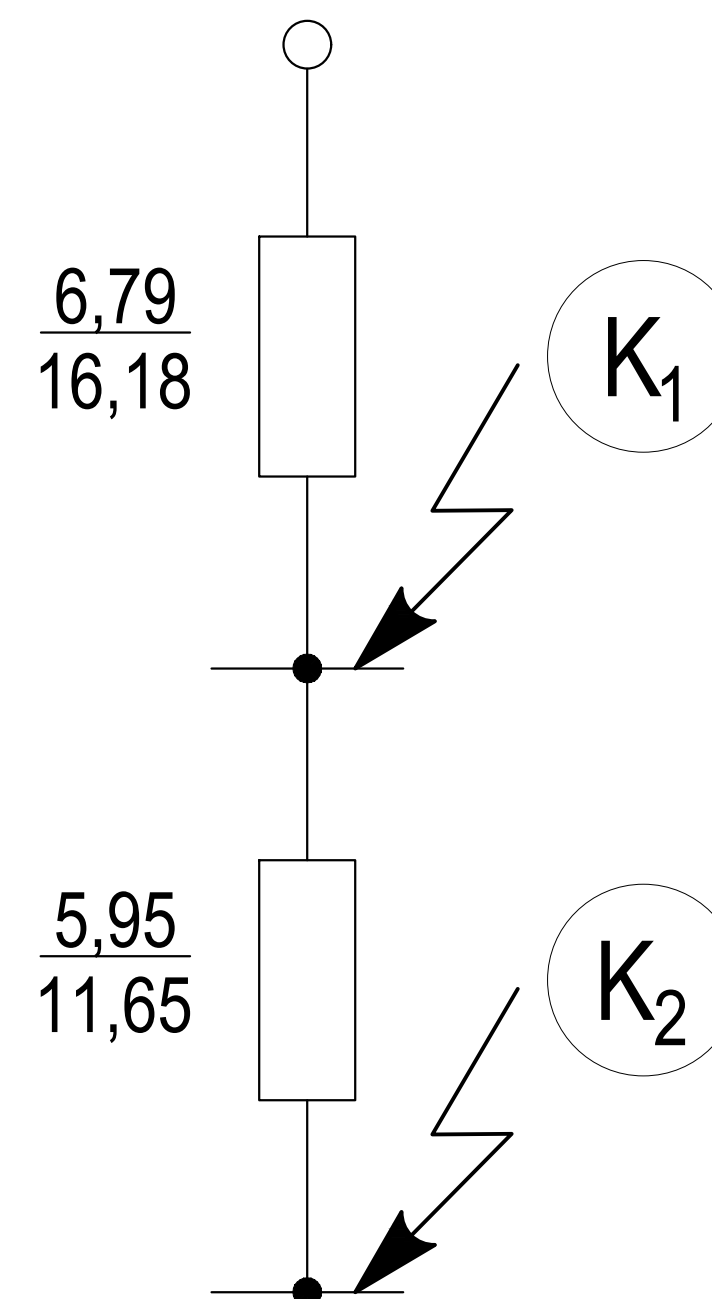

Примечания

1. Сопротивления на схеме замещения указаны в Омах и приведены к напряжению 37 кВ.
2. В схеме замещения:
 $\frac{5,95}{11,65}$ - сопротивление в максимальном режиме
 $\frac{6,79}{16,18}$ - сопротивление в минимальном режиме