


ЗВП (261.0231)

ЗВП сигнальная ступень (0631)

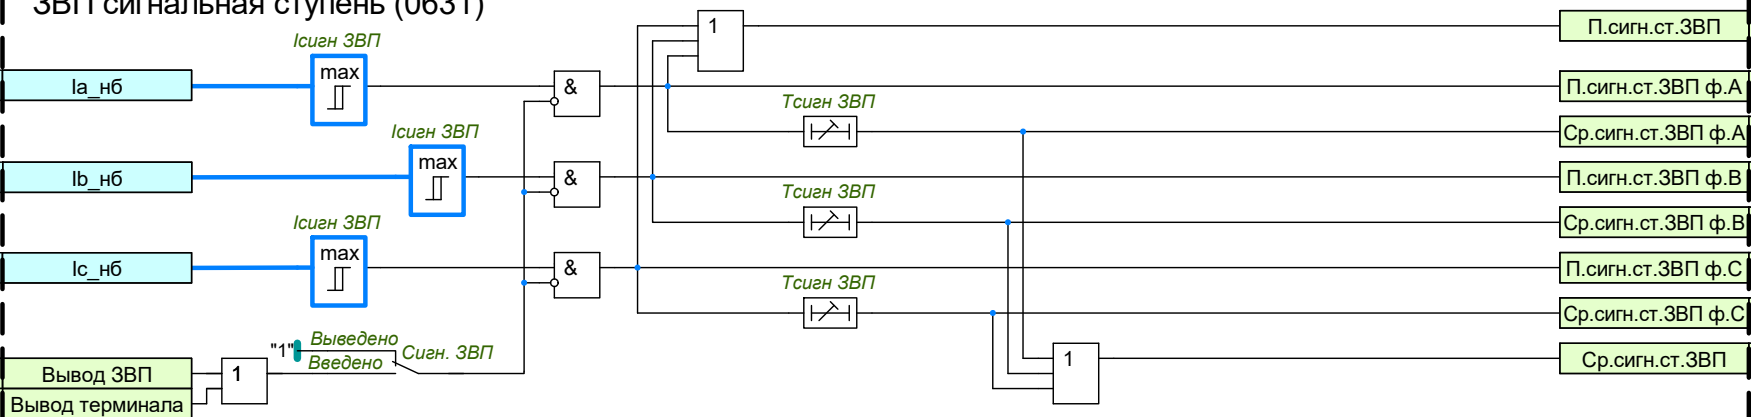

ЗВП отключающая ступень (0632)

