


ЦОС		
XA1:1	la B1*	
XA1:2	la B1	
XA1:3	lb B1*	
XA1:4	lb B1	
XA1:5	lc B1*	
XA1:6	lc B1	
XA1:7	la B2*	
XA1:8	la B2	
XA1:9	lb B2*	
XA1:10	lb B2	
XA1:11	lc B2*	
XA1:12	lc B2	
XA1:13	Ua*	
XA1:14	Ua	
XA1:15	Ub	
XA1:16	Ub*	
XA1:17	Uc	
XA1:18	Uc*	
XA1:19	Ua1*	
XA1:20	Ua1	
XA1:21	Ub1*	
XA1:22	Ub1	
XA1:23	Uc1	
XA1:24	Uc1*	
XA2:1	la3*	
XA2:2	la3	
XA2:3	lb3*	
XA2:4	lb3	
XA2:5	lc3*	
XA2:6	lc3	
XA2:7	Резерв	
XA2:8	Резерв	
XA2:9	Резерв	
XA2:10	Резерв	
XA2:11	Резерв	
XA2:12	Резерв	
XA2:13	Ua2*	
XA2:14	Ua2	
XA2:15	Ub2	
XA2:16	Ub2*	
XA2:17	Uc2	
XA2:18	Uc2*	
XA2:19	Резерв	
XA2:20	Резерв	
XA2:21	Резерв	
XA2:22	Резерв	
XA2:23	Резерв	
XA2:24	Резерв	

la B1
lb B1
lc B1
la B2
lb B2
lc B2
la3
lb3
lc3
la2r/la1r B1
lb2r/lb1r B1
lc2r/lc1r B1
la2r/la1r B2
lb2r/lb1r B2
lc2r/lc1r B2
3l0
l2/l1
lad
lat
lad2r/lad1r
la1
la2
lbд
lbr
lbd2r/lbd1r
lb1
lb2
lсд
lсt
lсd2r/lсd1r
lc1
lc2
Uab
Ubc
Uca
U2
3U0
U T(AT)
Ua1
Ua2

Входы ФСУ	
Общая логика: Контр. ОТ терм	90.501
Общая логика: Цели тока В1	90.502
• • •	
Общая логика: Цели тока В3	90.504
Общая логика: Цели напряжения	90.505
Общая логика: Цели напряжения Э1	90.506
Общая логика: Цели напряжения Э2	90.507
Общая логика: Цели отключения В1	90.508
Общая логика: Цели пуска УРОВ В1	90.509
• • •	
Общая логика: Цели отключения В3	90.513
Общая логика: Цели пуска УРОВ В3	90.514
Общая логика: Цели отключения Т(AT)	90.515
Общая логика: Цели пуска УРОВ Т(AT)	90.516
Общая логика: Контр питания цепей сигн.	90.517
Д3О/ Д3О: Блок. Д3О от КЦТ	0641.1611.501
Д3О/ Д3О: Возврат КЦТ	0641.1621.501
ЛОЧ/ ООЧ: Нормальный режим очув.	1871.5111.501
ЛОЧ/ ООЧ: Оперативный ввод очув.	1871.5111.502
ЛОП: Опробование	1361.501
Пуск УРОВ В1	501
Пуск УРОВ В1 НН	502
Ср. УРОВ В1	503
Пуск УРОВ В2	504
Пуск УРОВ В2 НН	505
Ср. УРОВ В2	506
КСВ В1/ КСН: Внеш. сигнал КС(УС)	3291.6781.501
КСВ В2/ КСН: Внеш. сигнал КС(УС)	3292.6781.501
ЛО СШ/ ЗАПВ: Оперативный запрет АПВ	4241.7781.501
Сброс сигнализации	507
КСВ В1/ Контроль В: Контр. ЭМО1	3371.6571.501
КСВ В1/ Контроль В: Контр. ЭМО1 ф.А	3371.6571.502
КСВ В1/ Контроль В: Контр. ЭМО1 ф.В	3371.6571.503
КСВ В1/ Контроль В: Контр. ЭМО1 ф.С	3371.6571.504
КСВ В1/ Контроль В: Контр. ЭМО2	3371.6571.505
КСВ В1/ Контроль В: Контр. ЭМО2 ф.А	3371.6571.506
КСВ В1/ Контроль В: Контр. ЭМО2 ф.В	3371.6571.507
КСВ В1/ Контроль В: Контр. ЭМО2 ф.С	3371.6571.508
КСВ В1/ Контроль В: Контр. ЭМВ	3371.6571.509
КСВ В1/ Контроль В: Контр. ЭМВ ф.А	3371.6571.510
КСВ В1/ Контроль В: Контр. ЭМВ ф.В	3371.6571.511
КСВ В1/ Контроль В: Контр. ЭМВ ф.С	3371.6571.512
КСВ В1/ Контроль В: Низк. давл. SF6	3371.6571.513
КСВ В1/ Контроль В: Низк. давл. SF6 ф.А	3371.6571.514
КСВ В1/ Контроль В: Низк. давл. SF6 ф.В	3371.6571.515
КСВ В1/ Контроль В: Низк. давл. SF6 ф.С	3371.6571.516
КСВ В1/ Контроль В: Авар. давл. SF6	3371.6571.517
КСВ В1/ Контроль В: Авар. давл. SF6 ф.А	3371.6571.518
КСВ В1/ Контроль В: Авар. давл. SF6 ф.В	3371.6571.519
КСВ В1/ Контроль В: Авар. давл. SF6 ф.С	3371.6571.520
КСВ В1/ Контроль В: Пруж. не заведены	3371.6571.521
КСВ В1/ Контроль В: Пруж. не заведены ф.А	3371.6571.522
КСВ В1/ Контроль В: Пруж. не заведены ф.В	3371.6571.523
КСВ В1/ Контроль В: Пруж. не заведены ф.С	3371.6571.524
КСВ В1/ Контроль В: Неиспр. обогр.	3371.6571.525
КСВ В1/ Контроль В: Автомат ШП	3371.6571.526
КСВ В1/ Контроль В: Контр. ОТ ЭМВ/ЭМО1	3371.6571.527
КСВ В1/ Контроль В: Контр. ОТ ЭМО2	3371.6571.528
КСВ В1/ Контроль В: Контр. ОТ сигн.	3371.6571.529
КСВ В1/ Блокировка упр.: Внеш. блок. упр.	3371.6611.501
КСВ В1/ Блокировка упр.: Внеш. блок. вкл.	3371.6611.502

Входы ФСУ	
КСВ В1/ Контроль ТТ Низк. давл. SF6 ТТ	3371.6581.501
КСВ В1/ Контроль ТТ Низк. давл. SF6 ТТ ф.А	3371.6581.502
КСВ В1/ Контроль ТТ Низк. давл. SF6 ТТ ф.В	3371.6581.503
КСВ В1/ Контроль ТТ Низк. давл. SF6 ТТ ф.С	3371.6581.504
КСВ В1/ Контроль ТТ Авар. давл. SF6 ТТ	3371.6581.505
КСВ В1/ Контроль ТТ Авар. давл. SF6 ТТ ф.А	3371.6581.506
КСВ В1/ Контроль ТТ Авар. давл. SF6 ТТ ф.В	3371.6581.507
КСВ В1/ Контроль ТТ Авар. давл. SF6 ТТ ф.С	3371.6581.508
КСВ В1/ Контроль ТТ Неиспр. обогр. ТТ	3371.6581.509
КСВ В1/ Защита ЭМУ: Работа ЭМВ	3371.6601.501
КСВ В1/ Защита ЭМУ: Работа ЭМВ ф.А	3371.6601.502
КСВ В1/ Защита ЭМУ: Работа ЭМВ ф.В	3371.6601.503
КСВ В1/ Защита ЭМУ: Работа ЭМВ ф.С	3371.6601.504
КСВ В1/ Защита ЭМУ: Работа ЭМО1	3371.6601.505
КСВ В1/ Защита ЭМУ: Работа ЭМО1 ф.А	3371.6601.506
КСВ В1/ Защита ЭМУ: Работа ЭМО1 ф.В	3371.6601.507
КСВ В1/ Защита ЭМУ: Работа ЭМО1 ф.С	3371.6601.508
КСВ В1/ Защита ЭМУ: Работа ЭМО2	3371.6601.509
КСВ В1/ Защита ЭМУ: Работа ЭМО2 ф.А	3371.6601.510
КСВ В1/ Защита ЭМУ: Работа ЭМО2 ф.В	3371.6601.511
КСВ В1/ Защита ЭМУ: Работа ЭМО2 ф.С	3371.6601.512
КСВ В2/ Контроль В: Контр. ЭМО1	3372.6571.501
КСВ В2/ Контроль В: Контр. ЭМО1 ф.А	3372.6571.502
КСВ В2/ Контроль В: Контр. ЭМО1 ф.В	3372.6571.503
КСВ В2/ Контроль В: Контр. ЭМО1 ф.С	3372.6571.504
КСВ В2/ Контроль В: Контр. ЭМО2	3372.6571.505
КСВ В2/ Контроль В: Контр. ЭМО2 ф.А	3372.6571.506
КСВ В2/ Контроль В: Контр. ЭМО2 ф.В	3372.6571.507
КСВ В2/ Контроль В: Контр. ЭМО2 ф.С	3372.6571.508
КСВ В2/ Контроль В: Контр. ЭМВ	3372.6571.509
КСВ В2/ Контроль В: Контр. ЭМВ ф.А	3372.6571.510
КСВ В2/ Контроль В: Контр. ЭМВ ф.В	3372.6571.511
КСВ В2/ Контроль В: Контр. ЭМВ ф.С	3372.6571.512
КСВ В2/ Контроль В: Низк. давл. SF6	3372.6571.513
КСВ В2/ Контроль В: Низк. давл. SF6 ф.А	3372.6571.514
КСВ В2/ Контроль В: Низк. давл. SF6 ф.В	3372.6571.515
КСВ В2/ Контроль В: Низк. давл. SF6 ф.С	3372.6571.516
КСВ В2/ Контроль В: Авар. давл. SF6	3372.6571.517
КСВ В2/ Контроль В: Авар. давл. SF6 ф.А	3372.6571.518
КСВ В2/ Контроль В: Авар. давл. SF6 ф.В	3372.6571.519
КСВ В2/ Контроль В: Авар. давл. SF6 ф.С	3372.6571.520
КСВ В2/ Контроль В: Пруж. не заведены	3372.6571.521
КСВ В2/ Контроль В: Пруж. не заведены ф.А	3372.6571.522
КСВ В2/ Контроль В: Пруж. не заведены ф.В	3372.6571.523
КСВ В2/ Контроль В: Пруж. не заведены ф.С	3372.6571.524
КСВ В2/ Контроль В: Неиспр. обогр.	3372.6571.525
КСВ В2/ Контроль В: Автомат ШП	3372.6571.526
КСВ В2/ Контроль В: Контр. ОТ ЭМВ/ЭМО1	3372.6571.527
КСВ В2/ Контроль В: Контр. ОТ ЭМО2	3372.6571.528
КСВ В2/ Контроль В: Контр. ОТ сигн.	3372.6571.529
КСВ В2/ Блокировка упр.: Внеш. блок. упр.	3372.6611.501
КСВ В2/ Блокировка упр.: Внеш. блок. вкл.	3372.6611.502
КСВ В2/ Контроль ТТ Низк. давл. SF6 ТТ	3372.6581.501
КСВ В2/ Контроль ТТ Низк. давл. SF6 ТТ ф.А	3372.6581.502
КСВ В2/ Контроль ТТ Низк. давл. SF6 ТТ ф.В	3372.6581.503
КСВ В2/ Контроль ТТ Низк. давл. SF6 ТТ ф.С	3372.6581.504
КСВ В2/ Контроль ТТ Авар. давл. SF6 ТТ	3372.6581.505
КСВ В2/ Контроль ТТ Авар. давл. SF6 ТТ ф.А	3372.6581.506
КСВ В2/ Контроль ТТ Авар. давл. SF6 ТТ ф.В	3372.6581.507
КСВ В2/ Контроль ТТ Авар. давл. SF6 ТТ ф.С	3372.6581.508

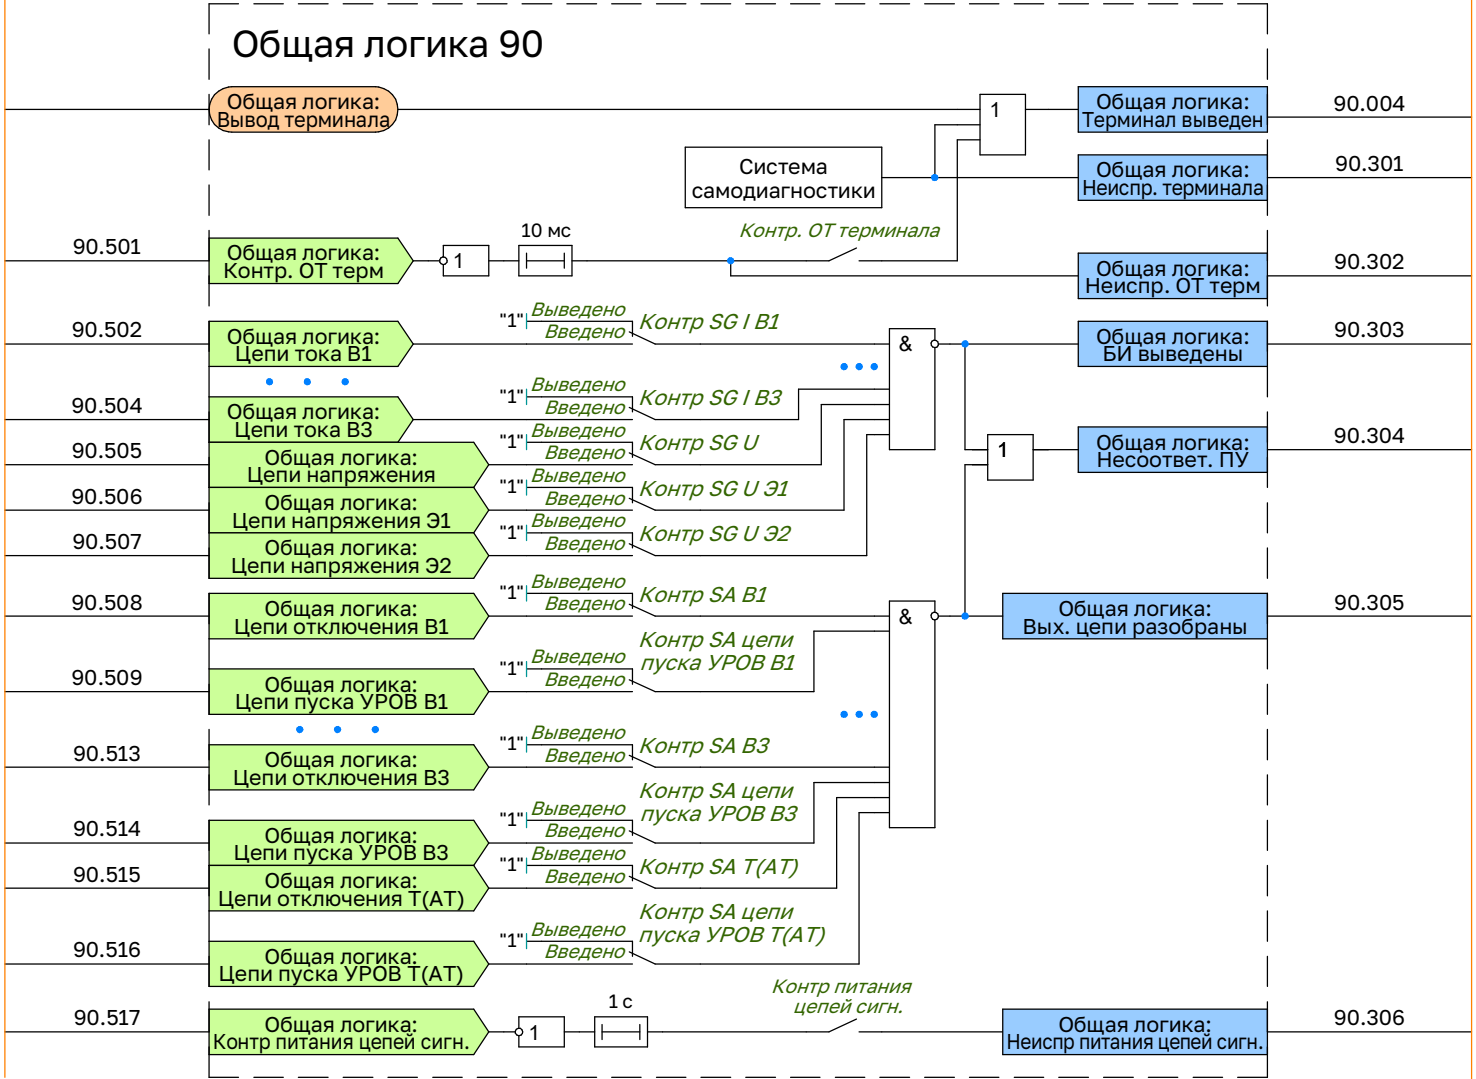

Входы ФСУ		
КСВ В2/ Контроль ТТ Неиспр. обогр.		3372.6581.509
КСВ В2/ Защита ЭМУ: Работа ЭМВ		3372.6601.501
КСВ В2/ Защита ЭМУ: Работа ЭМВ ф.А		3372.6601.502
КСВ В2/ Защита ЭМУ: Работа ЭМВ ф.В		3372.6601.503
КСВ В2/ Защита ЭМУ: Работа ЭМВ ф.С		3372.6601.504
КСВ В2/ Защита ЭМУ: Работа ЭМО1		3372.6601.505
КСВ В2/ Защита ЭМУ: Работа ЭМО1 ф.А		3372.6601.506
КСВ В2/ Защита ЭМУ: Работа ЭМО1 ф.В		3372.6601.507
КСВ В2/ Защита ЭМУ: Работа ЭМО1 ф.С		3372.6601.508
КСВ В2/ Защита ЭМУ: Работа ЭМО2		3372.6601.509
КСВ В2/ Защита ЭМУ: Работа ЭМО2 ф.А		3372.6601.510
КСВ В2/ Защита ЭМУ: Работа ЭМО2 ф.В		3372.6601.511
КСВ В2/ Защита ЭМУ: Работа ЭМО2 ф.С		3372.6601.512
ФПВ В1/ ФПВ: Б/К В вкл		3461.6551.501
ФПВ В1/ ФПВ: Б/К В вкл ф.А		3461.6551.502
ФПВ В1/ ФПВ: Б/К В вкл ф.В		3461.6551.503
ФПВ В1/ ФПВ: Б/К В вкл ф.С		3461.6551.504
ФПВ В1/ ФПВ: Б/К В откл ф.А		3461.6551.505
ФПВ В1/ ФПВ: Б/К В откл ф.В		3461.6551.506
ФПВ В1/ ФПВ: Б/К В откл ф.С		3461.6551.507
ФПВ В1/ ФПВ: Б/К В откл ф.А		3461.6551.508
ФПВ В1/ ФПВ: Б/К В откл ф.В		3461.6551.509
ФПВ В1/ ФПВ: Ремонт		3461.6551.509
ФПВ В1/ Р1: Б/К Р вкл		3461.6531.501
ФПВ В1/ Р1: Б/К Р вкл ф.А		3461.6531.502
ФПВ В1/ Р1: Б/К Р вкл ф.В		3461.6531.503
ФПВ В1/ Р1: Б/К Р вкл ф.С		3461.6531.504
ФПВ В1/ Р1: Б/К Р откл		3461.6531.505
ФПВ В1/ Р1: Б/К Р откл ф.А		3461.6531.506
ФПВ В1/ Р1: Б/К Р откл ф.В		3461.6531.507
ФПВ В1/ Р1: Б/К Р откл ф.С		3461.6531.508
ФПВ В1/ Р2: Б/К Р вкл		3461.6532.501
ФПВ В1/ Р2: Б/К Р вкл ф.А		3461.6532.502
ФПВ В1/ Р2: Б/К Р вкл ф.В		3461.6532.503
ФПВ В1/ Р2: Б/К Р вкл ф.С		3461.6532.504