




Цепи оперативного тока ТЗ АТ /ЛРТ А1

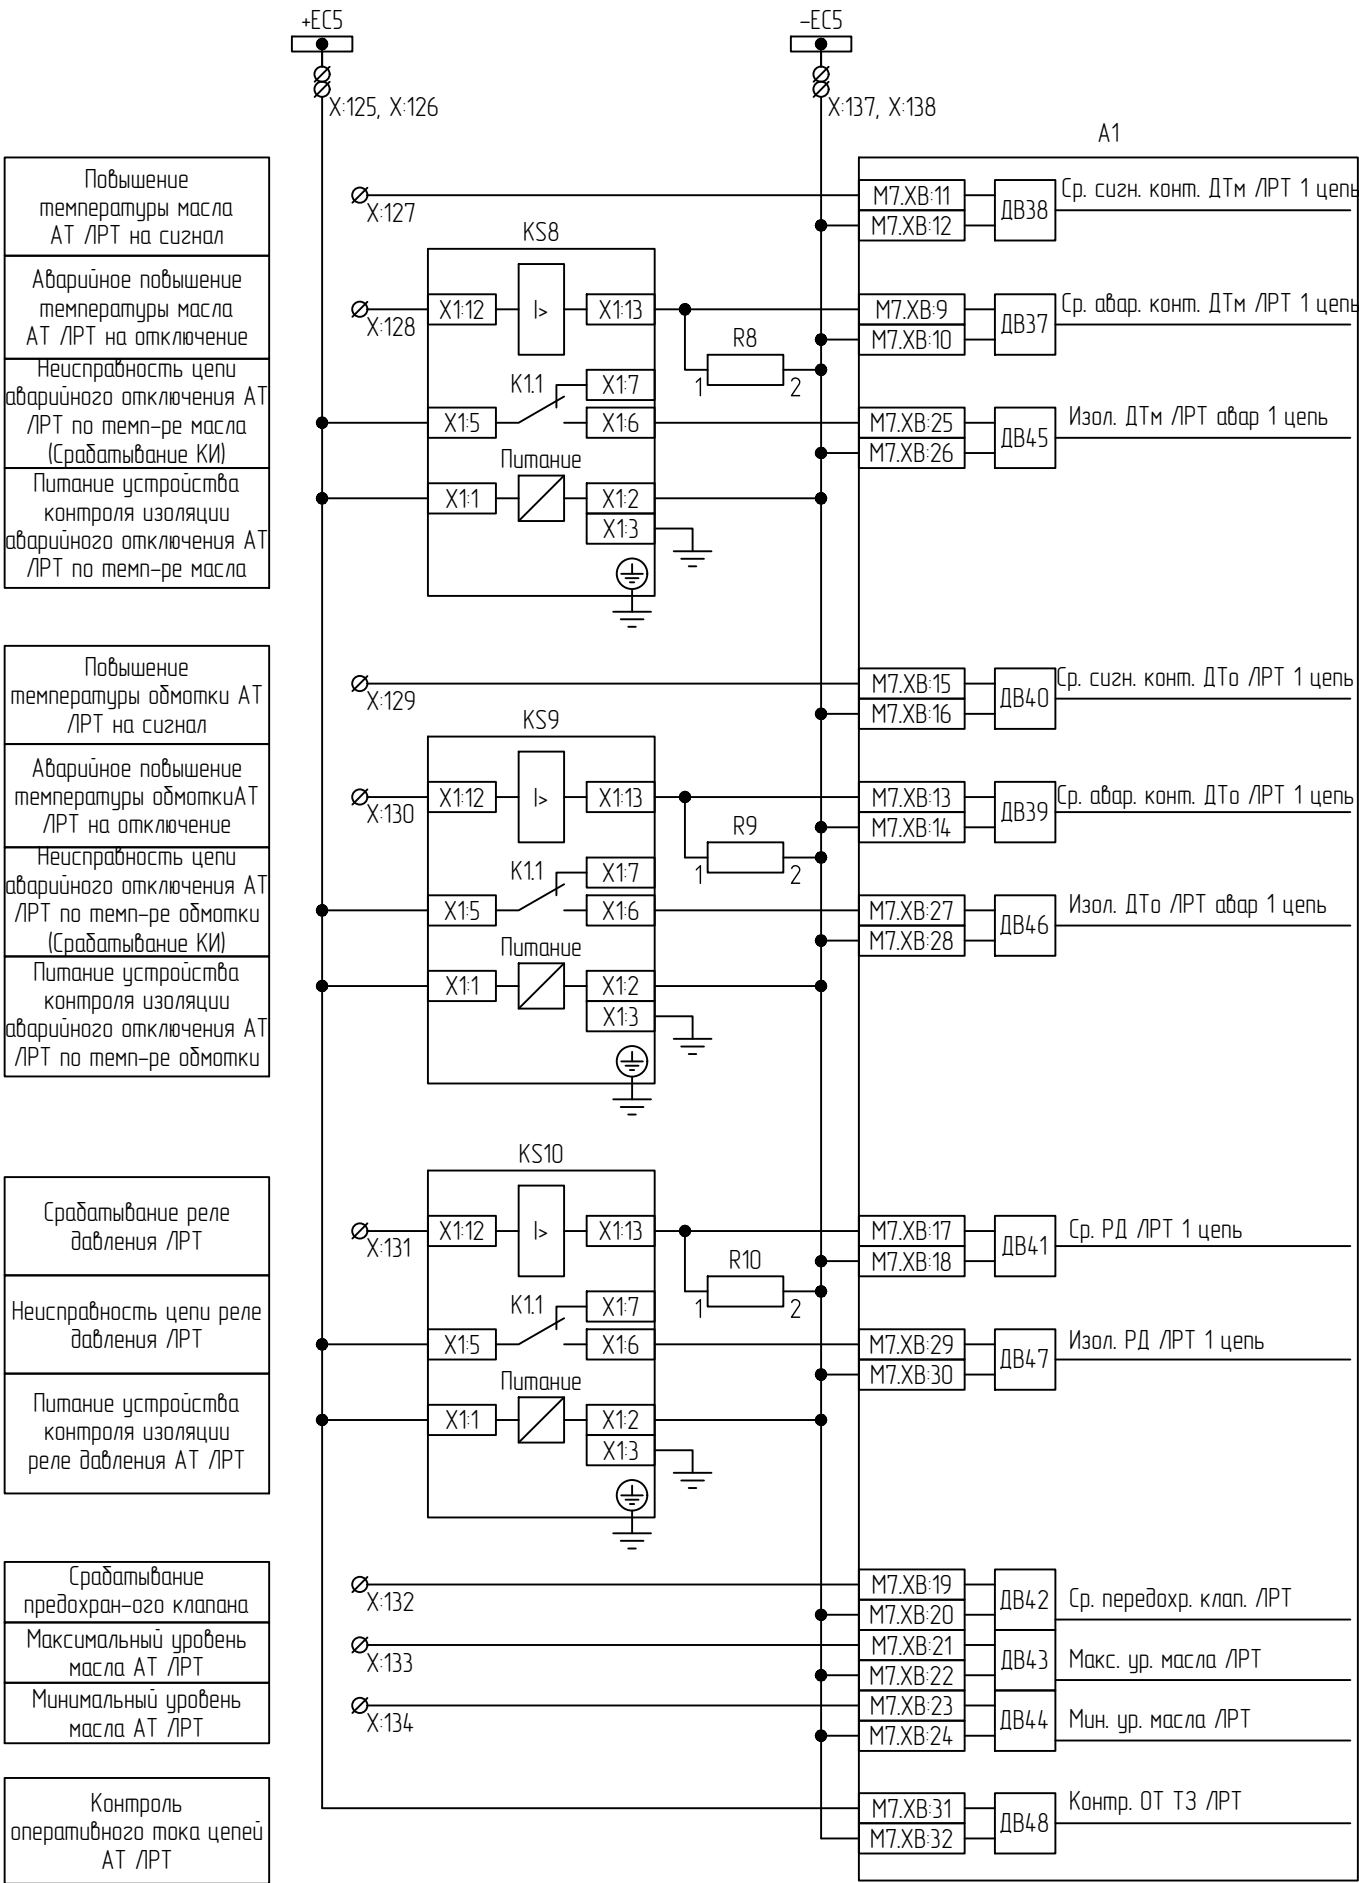


Срабатывание ЗДЗ секции НН1
Контроль опертока ЗДЗ секции НН1

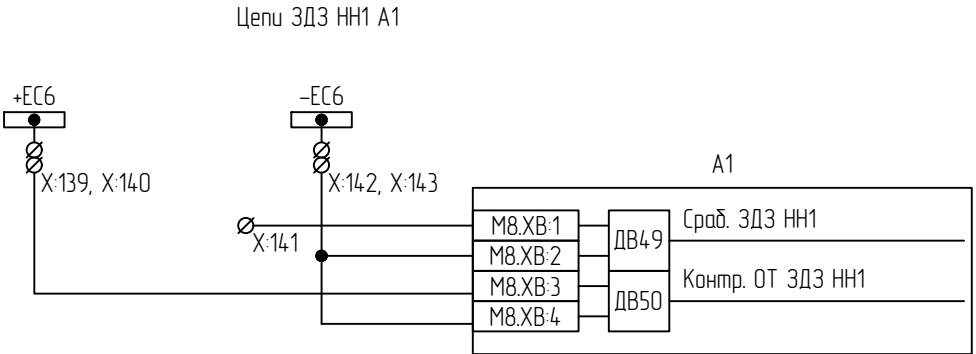

Срабатывание УРОВ ввода НН1
РПВ ввода НН1
Контроль опертока ввода НН1

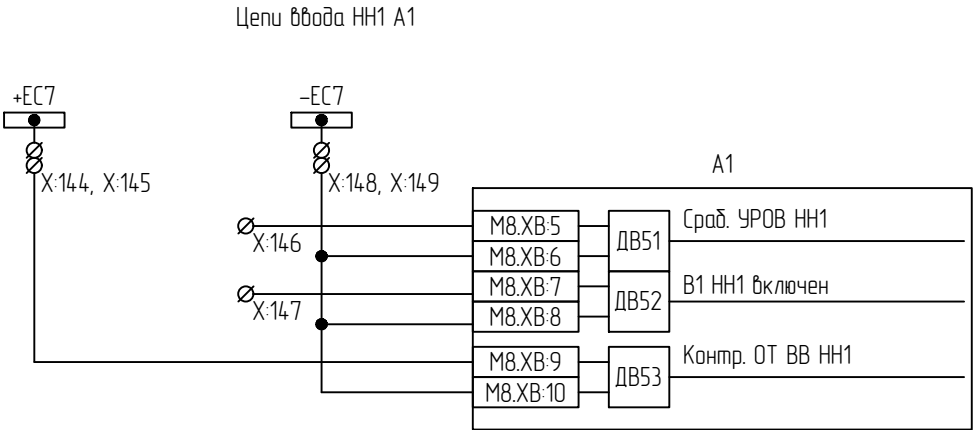

Срабатывание ЗДЗ секции НН2
Контроль опертока ЗДЗ секции НН2

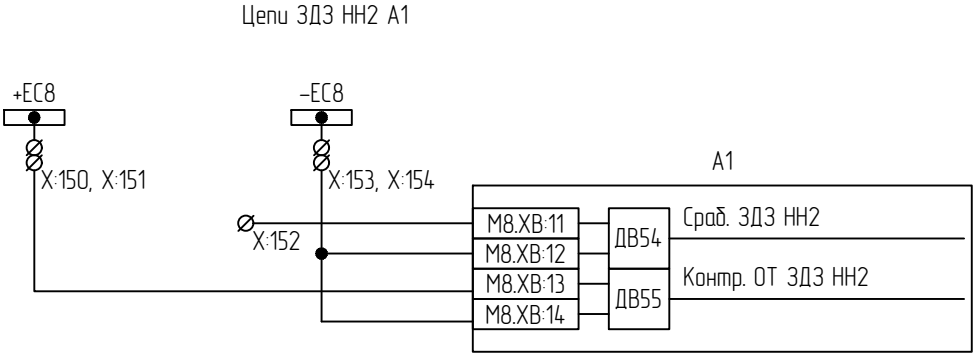

Срабатывание УРОВ ввода НН2
РПВ ввода НН2
Контроль опертока ввода НН2

