




Цепи оперативного тока ТЗ АТ /ЛРТ А1

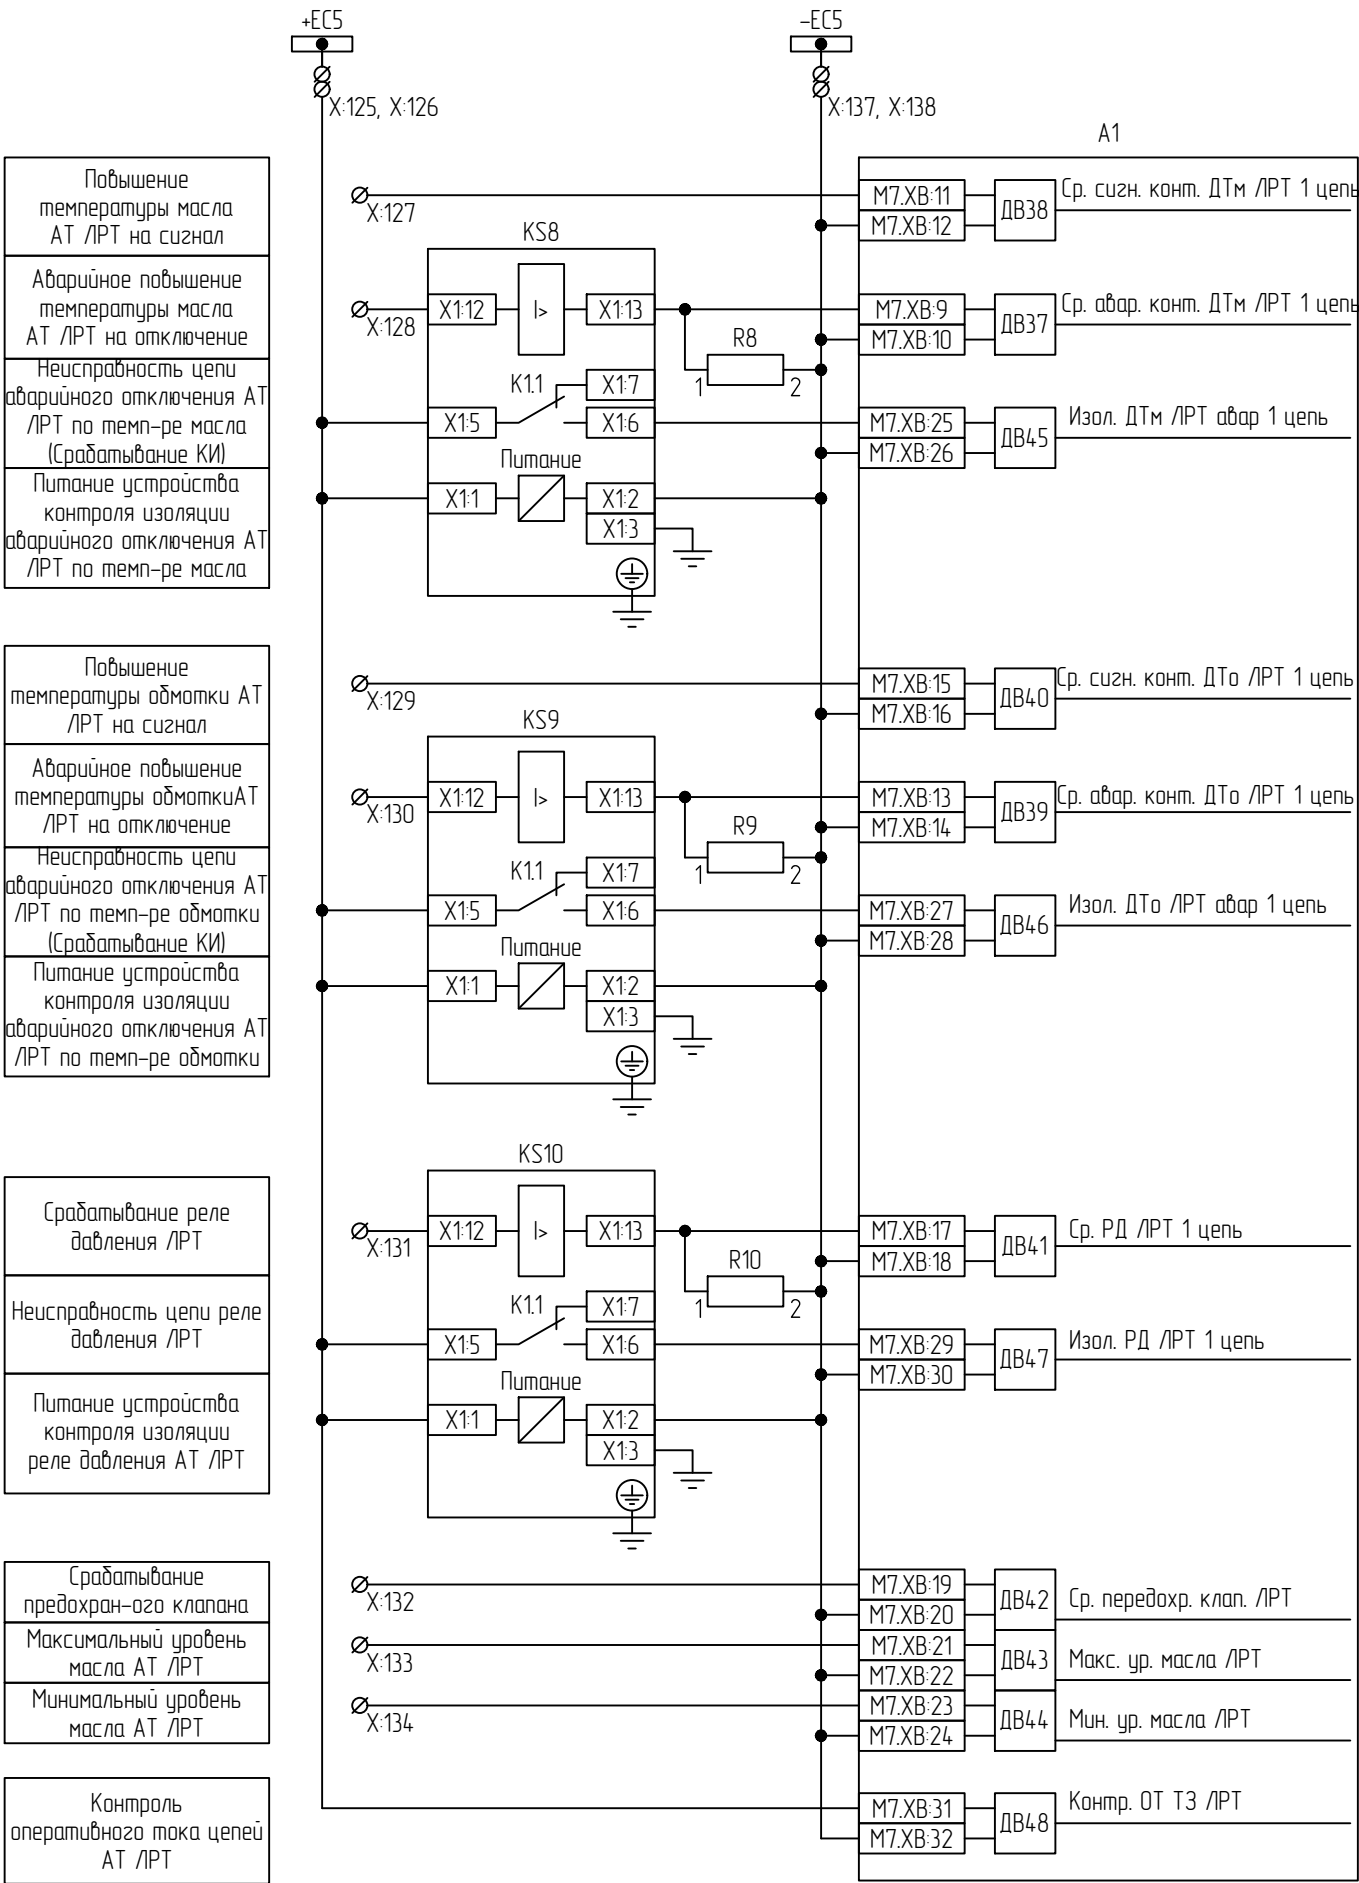


Цепи ЗДЗ НН1 А1

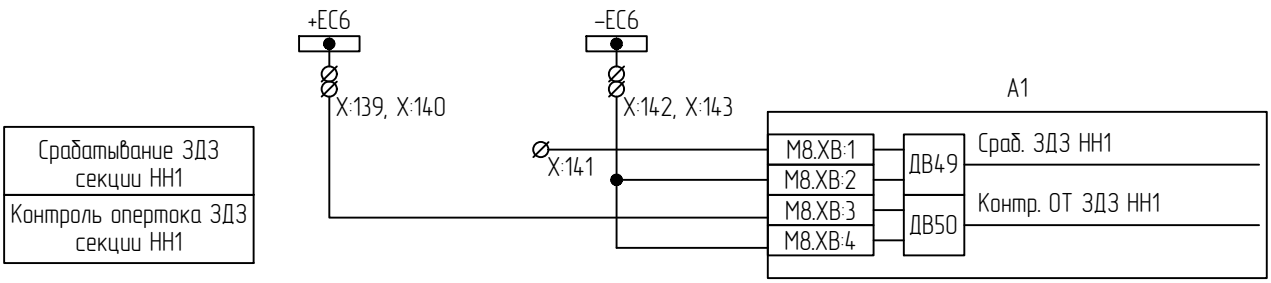

Цепи ввода НН1 А1

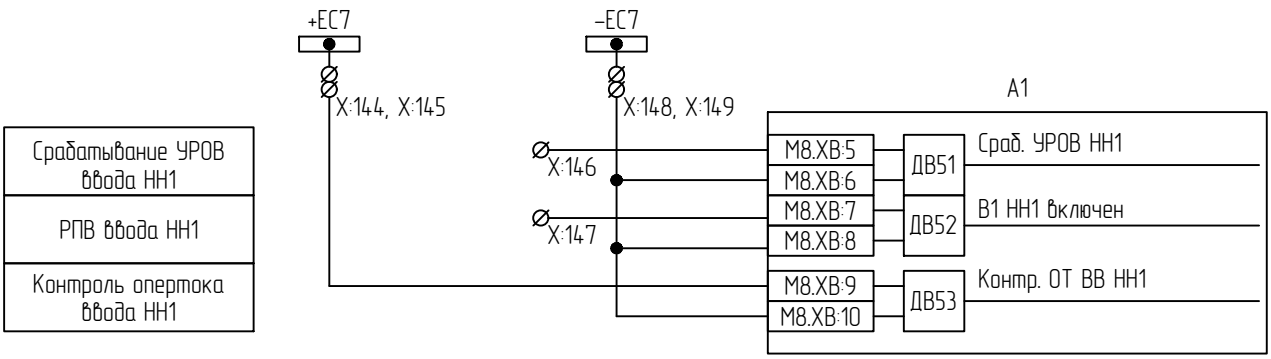

Цепи ЗДЗ НН2 А1

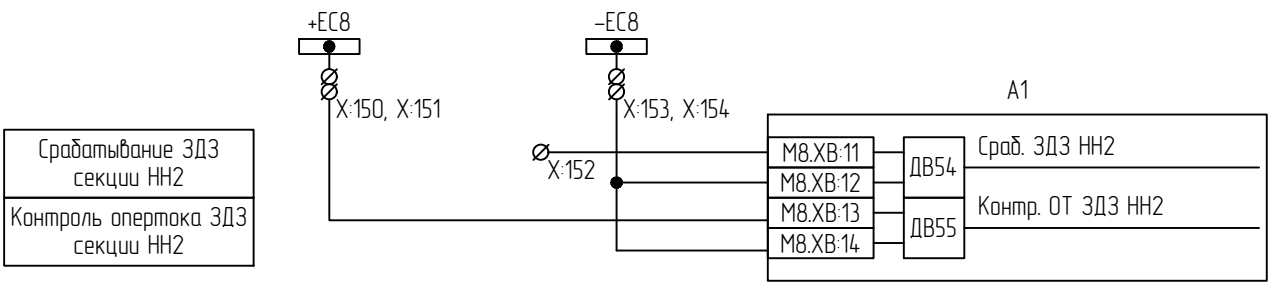

Цепи ввода НН2 А1

