



Выходные цепи

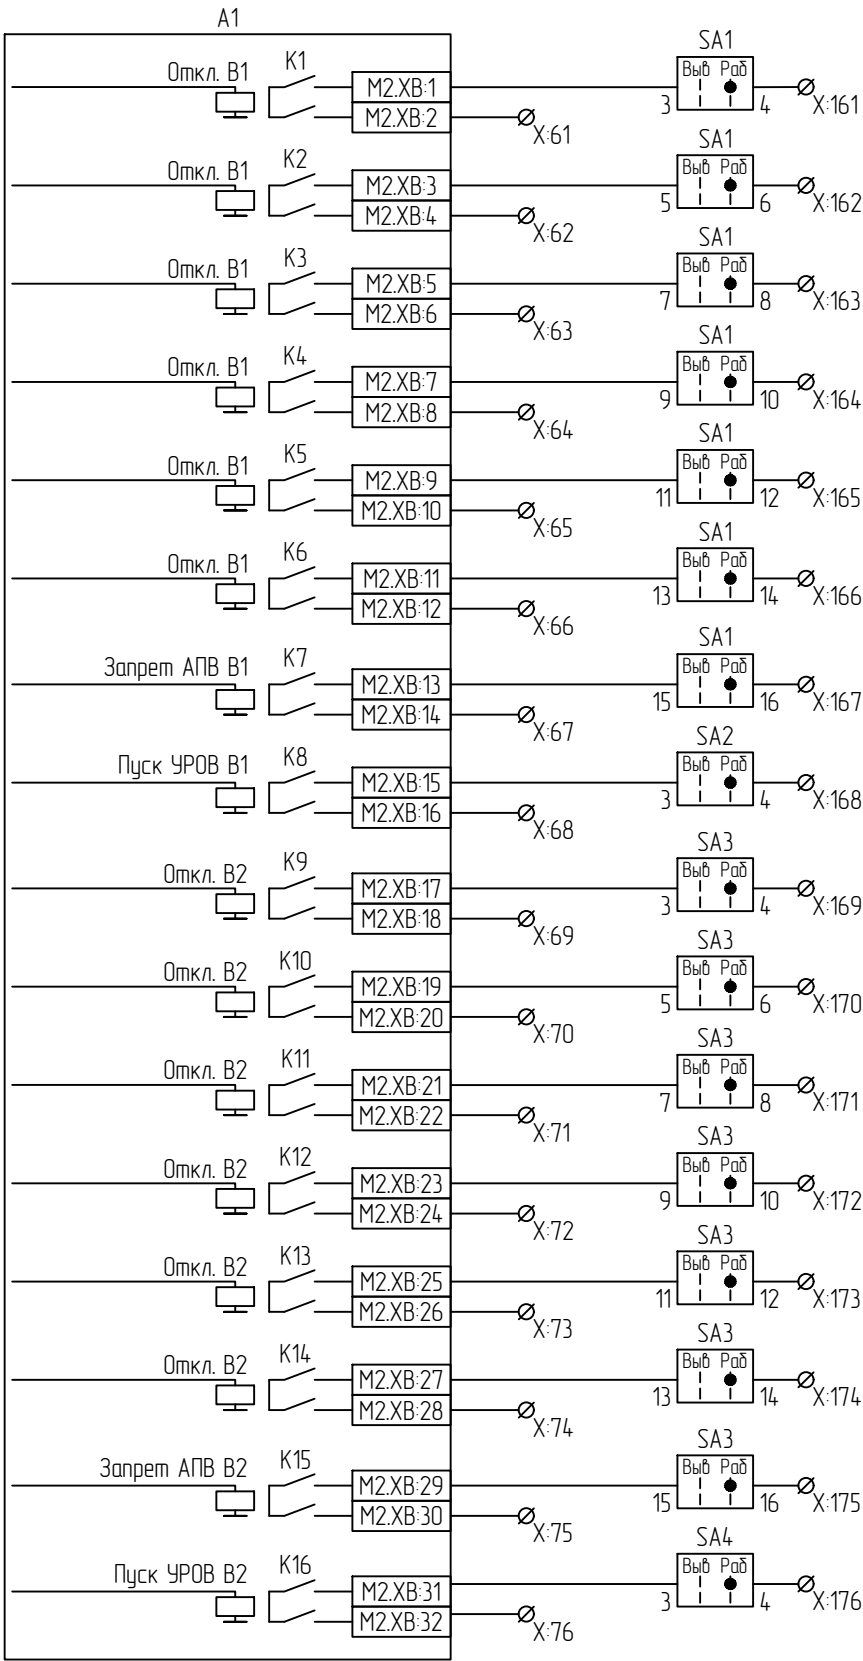

Отключение В1 ВН ф.А через ЭМ01
Отключение В1 ВН ф.В через ЭМ01
Отключение В1 ВН ф.С через ЭМ01
Отключение В1 ВН ф.А через ЭМ02
Отключение В1 ВН ф.В через ЭМ02
Отключение В1 ВН ф.С через ЭМ02
Запрет АПВ В1 ВН
Пуск УРОВ В1 ВН
Отключение В2 ВН ф.А через ЭМ01
Отключение В2 ВН ф.В через ЭМ01
Отключение В2 ВН ф.С через ЭМ01
Отключение В2 ВН ф.А через ЭМ02
Отключение В2 ВН ф.В через ЭМ02
Отключение В2 ВН ф.С через ЭМ02
Запрет АПВ В2 ВН
Пуск УРОВ В2 ВН

Выходные цепи

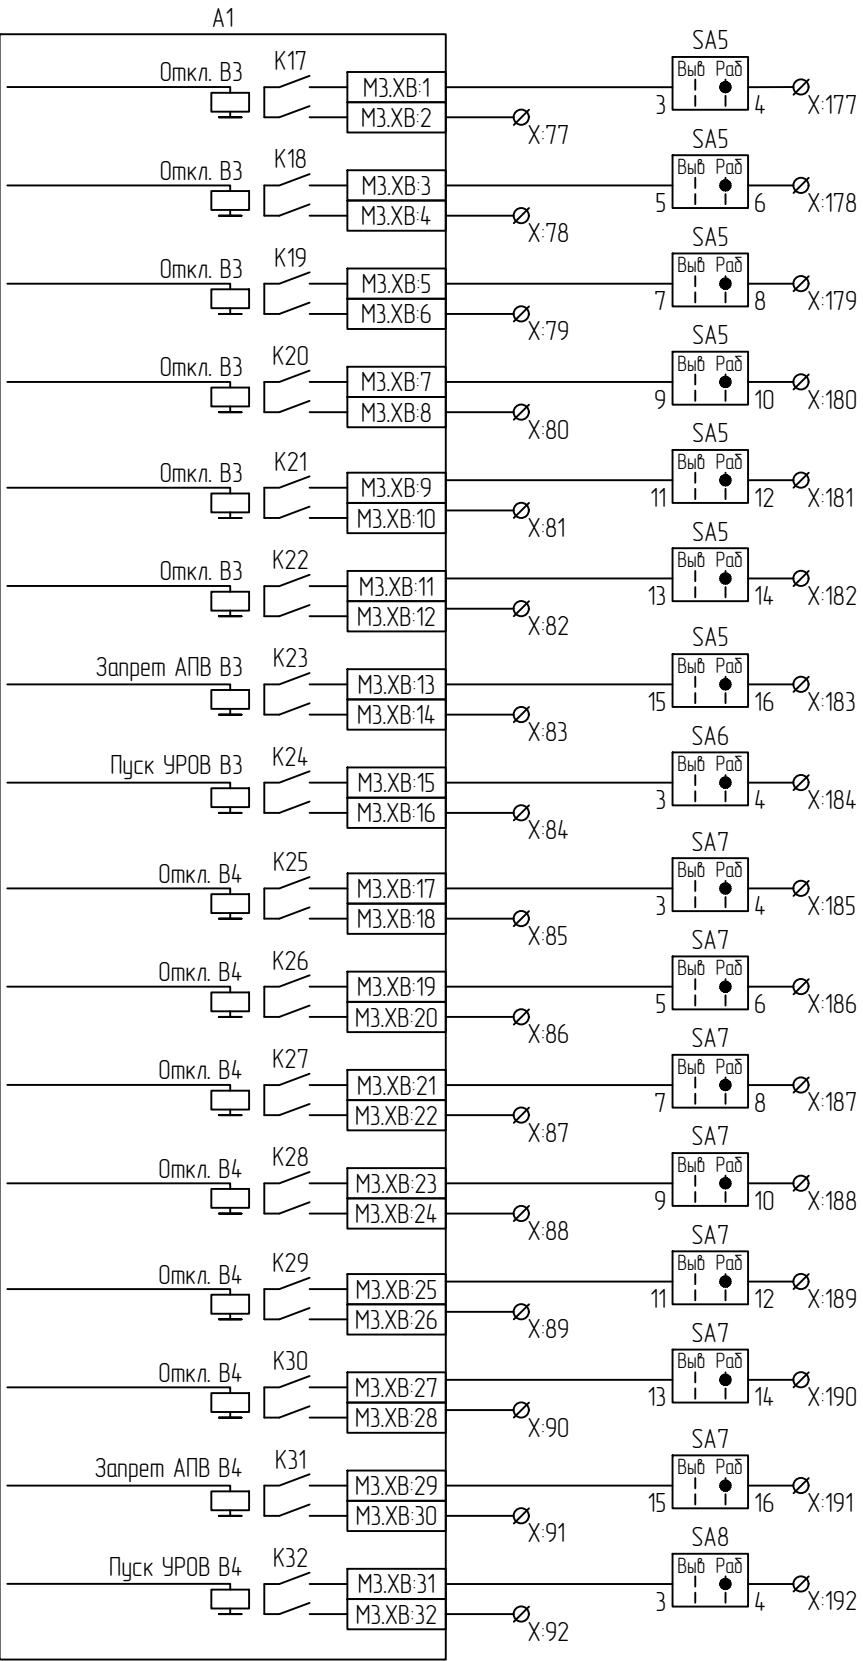

Отключение В3 ВН ф.А через ЭМ01
Отключение В3 ВН ф.В через ЭМ01
Отключение В3 ВН ф.С через ЭМ01
Отключение В3 ВН ф.А через ЭМ02
Отключение В3 ВН ф.В через ЭМ02
Отключение В3 ВН ф.С через ЭМ02
Запрет АПВ В3 ВН
Пуск УРОВ В3 ВН
Отключение В4 ВН ф.А через ЭМ01
Отключение В4 ВН ф.В через ЭМ01
Отключение В4 ВН ф.С через ЭМ01
Отключение В4 ВН ф.А через ЭМ02
Отключение В4 ВН ф.В через ЭМ02
Отключение В4 ВН ф.С через ЭМ02
Запрет АПВ В4 ВН
Пуск УРОВ В4 ВН