




Цепи переменного тока

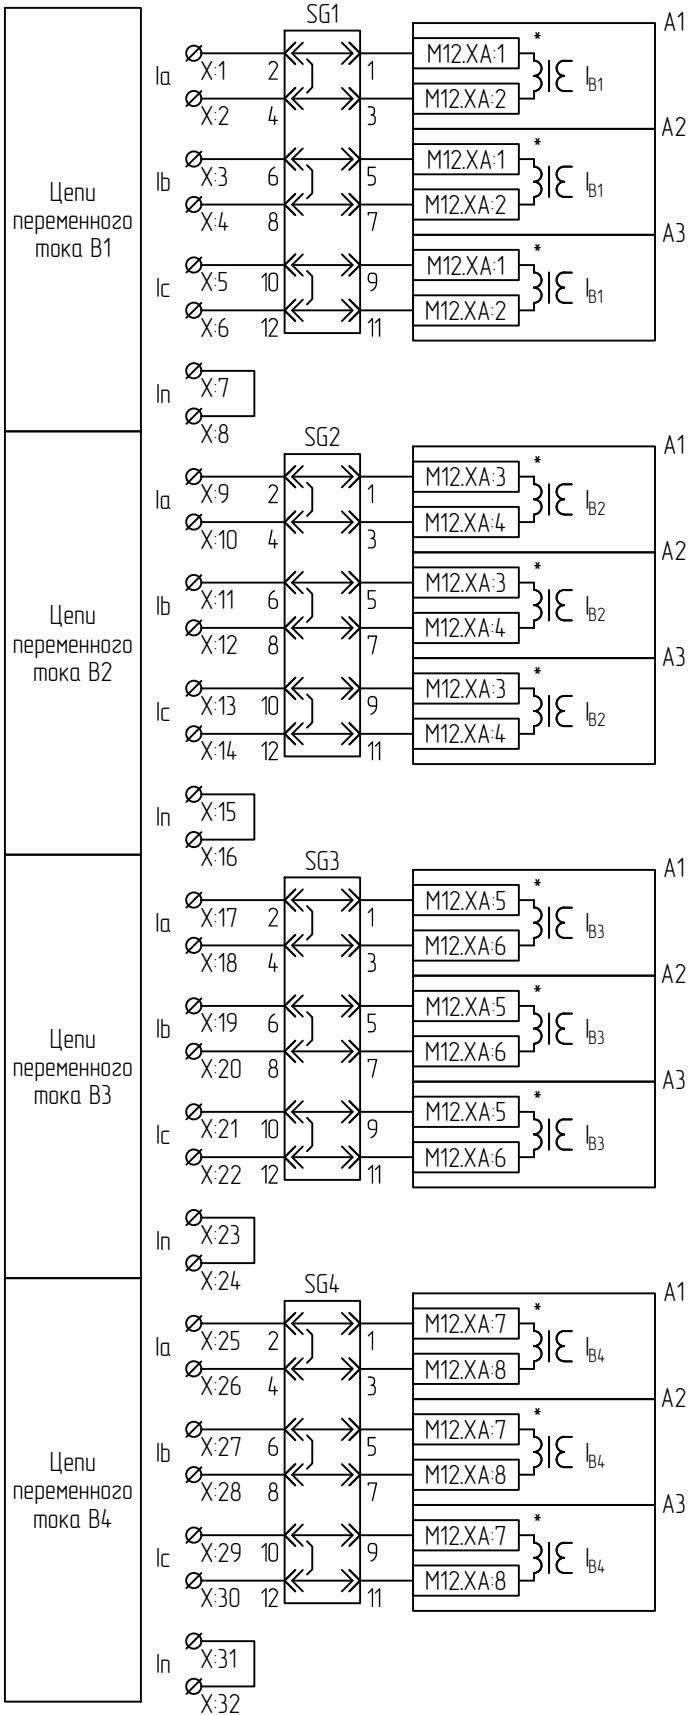


Це
перем

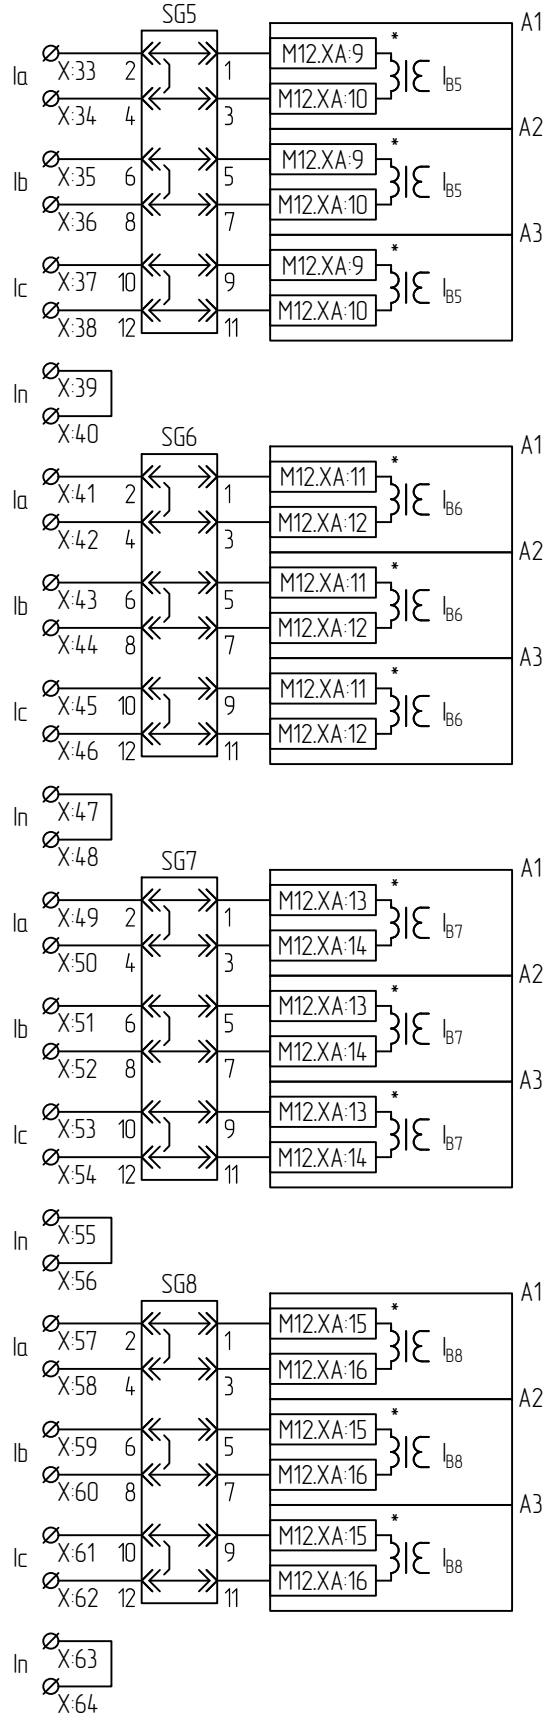


Цены
переменног
тока В9 (0Р

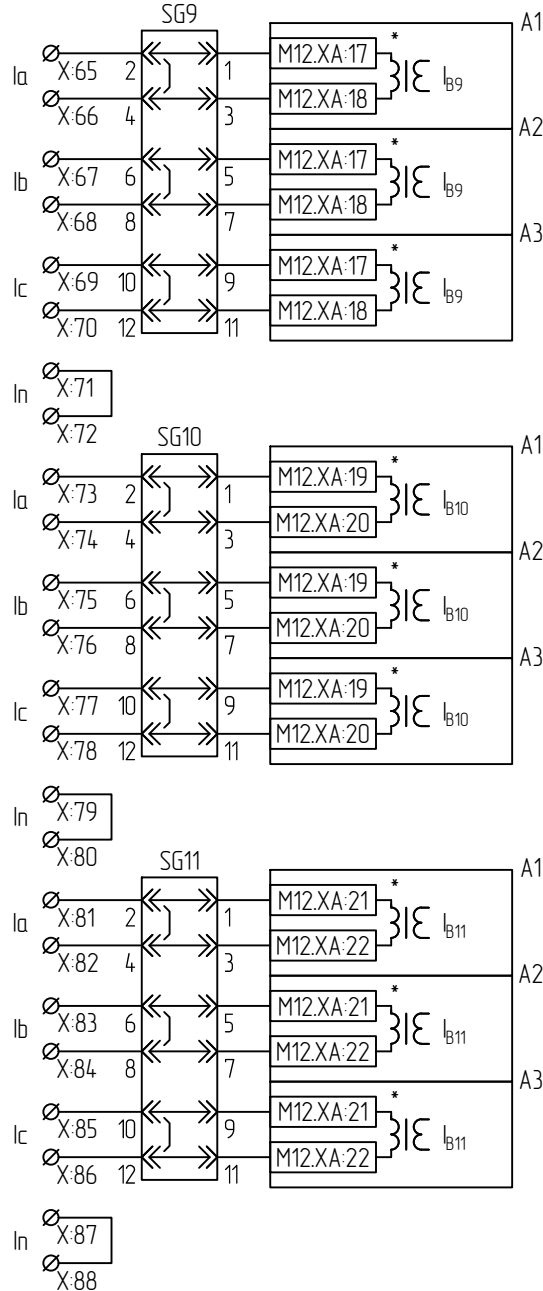

Цепи
переменного
напряжения
1 секции шир

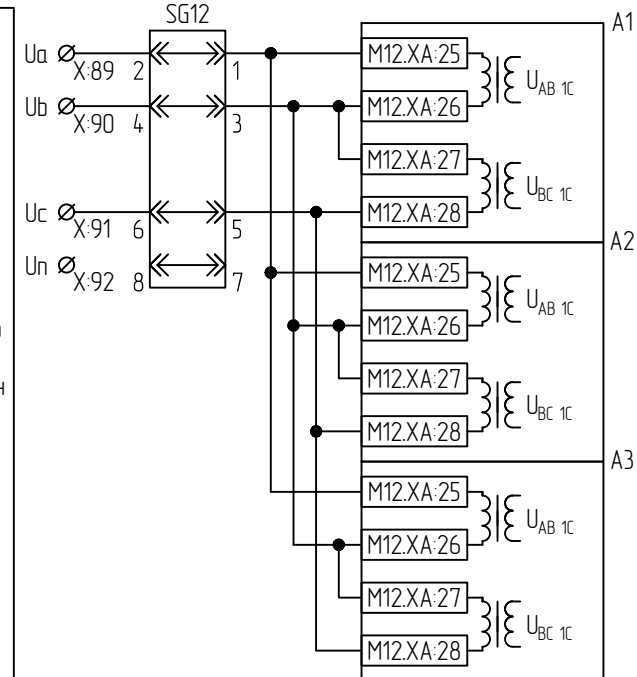

Цепи
переменного
напряжения
2 секции шп

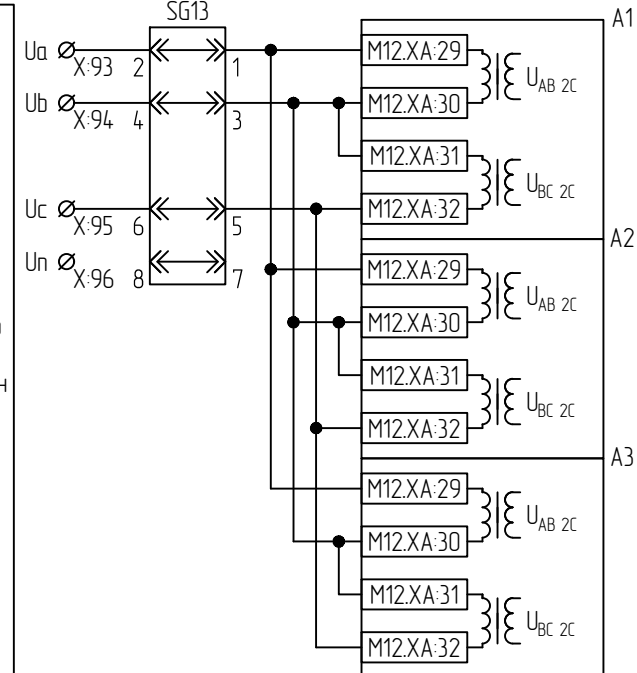

1. Конечное количество портов и тип интерфейсов определяется проектным решением и кодом заказа терминала/шкафа, по согласованию с производителем терминала/шкафа.
2. Конечное количество и функциональное назначение электронных клавиш ИЗУ определяется типом шкафа и проектным решением.