
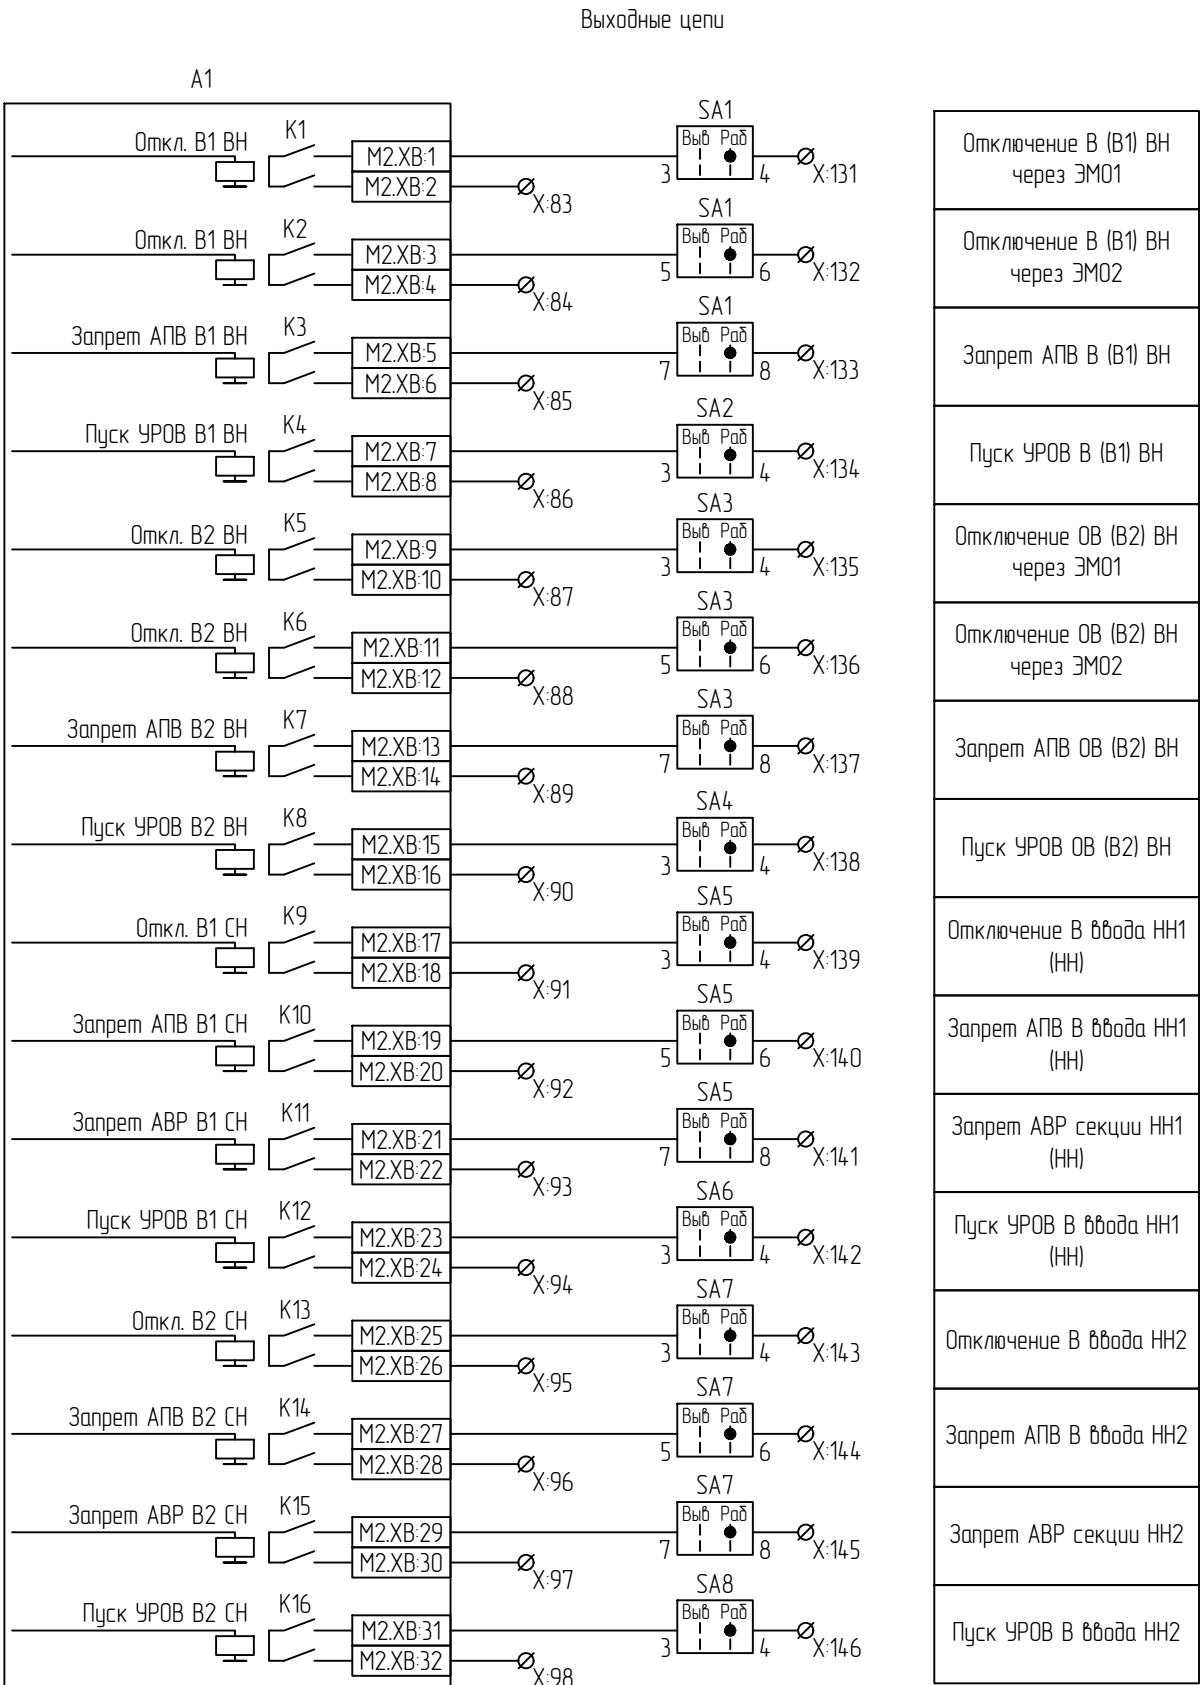
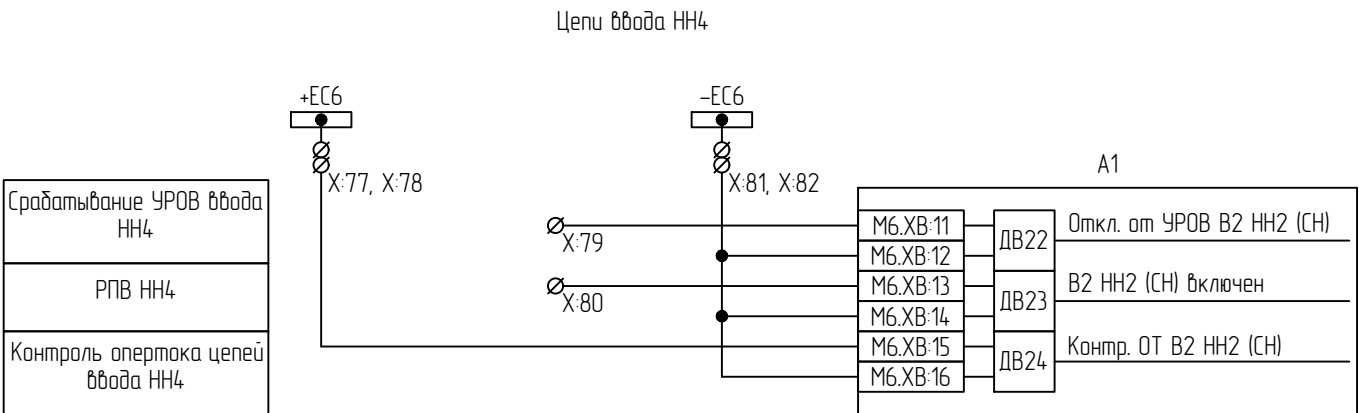
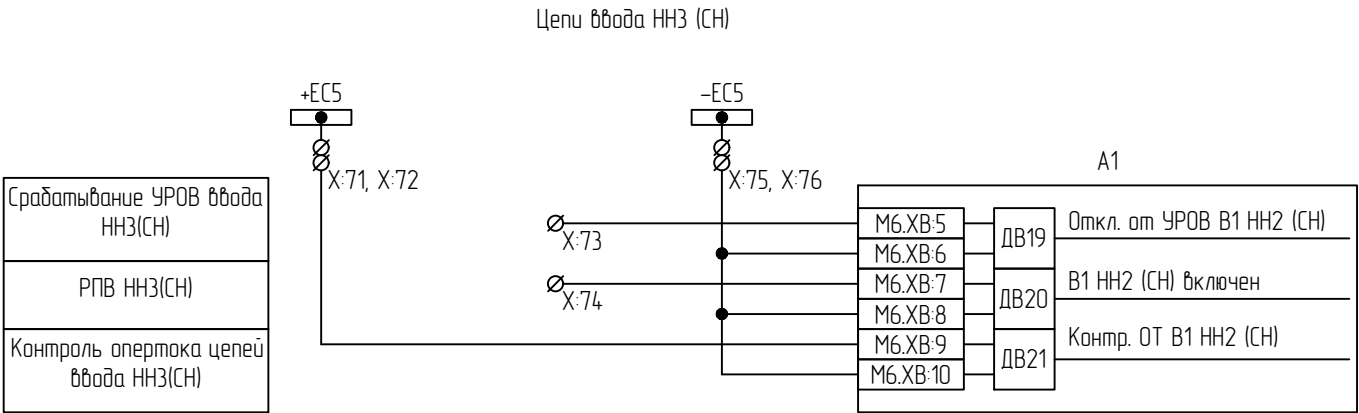
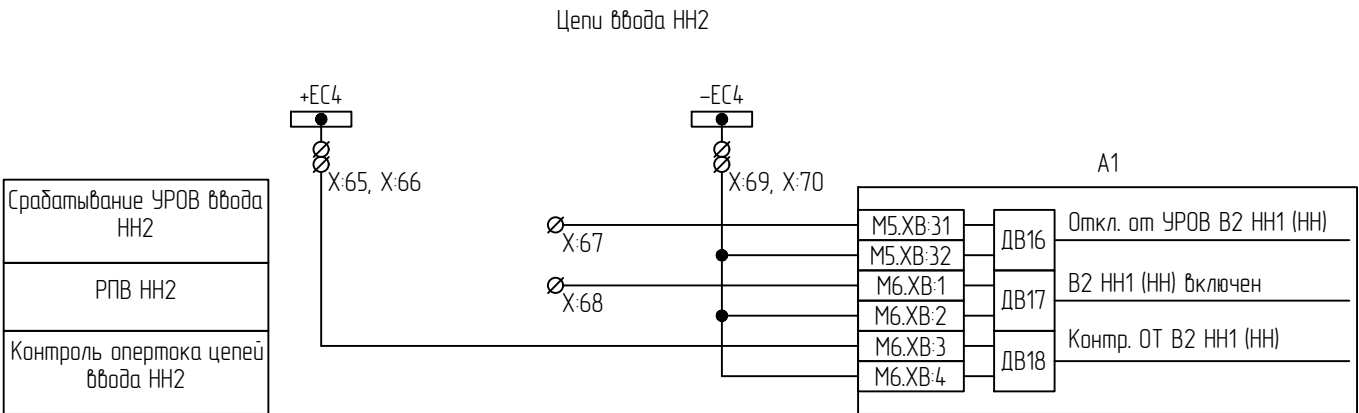


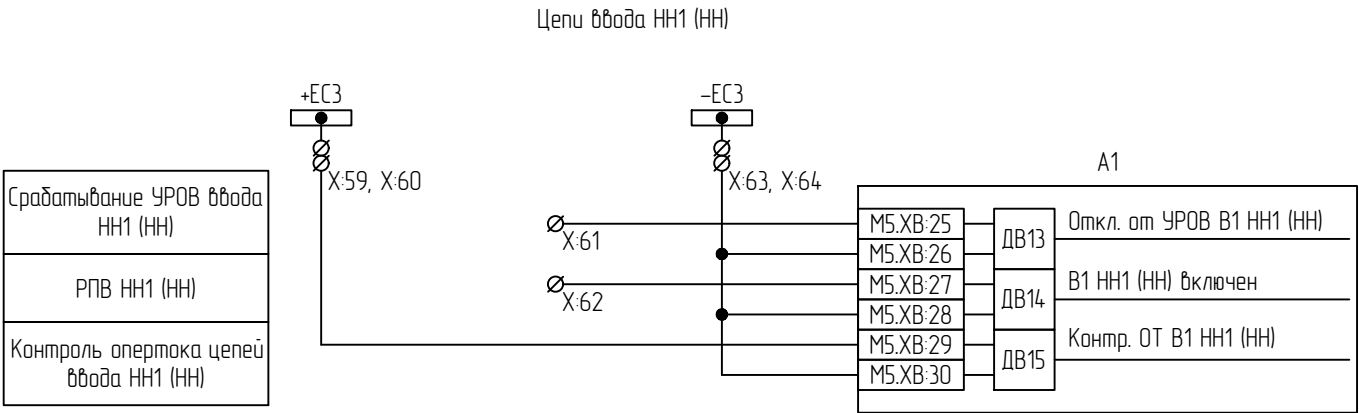

Отключение В (В1) ВН через ЭМО1
Отключение В (В1) ВН через ЭМО2
Запрет АПВ В (В1) ВН
Пуск УРОВ В (В1) ВН
Отключение ОВ (В2) ВН через ЭМО1
Отключение ОВ (В2) ВН через ЭМО2
Запрет АПВ ОВ (В2) ВН
Пуск УРОВ ОВ (В2) ВН
Отключение В ввода НН1 (НН)
Запрет АПВ В ввода НН1 (НН)
Запрет АВР секции НН1 (НН)
Пуск УРОВ В ввода НН1 (НН)
Отключение В ввода НН2
Запрет АПВ В ввода НН2
Запрет АВР секции НН2
Пуск УРОВ В ввода НН2