
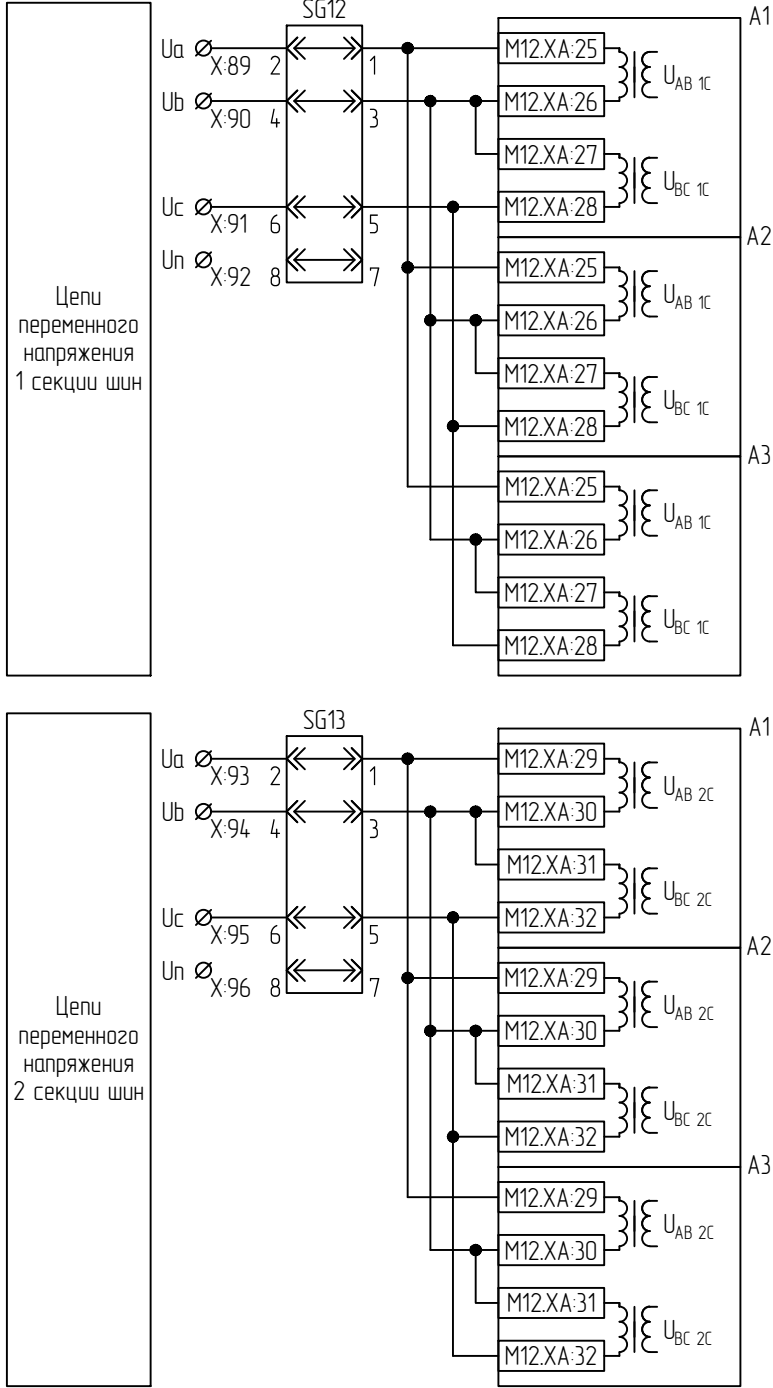
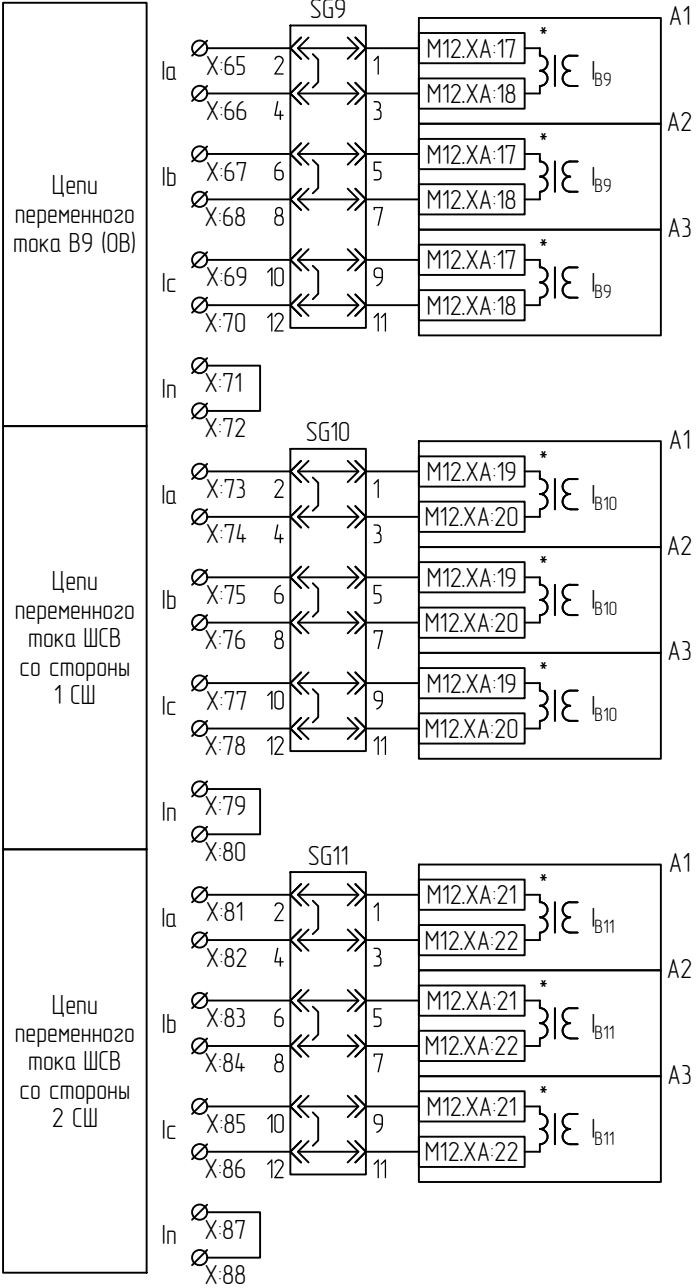
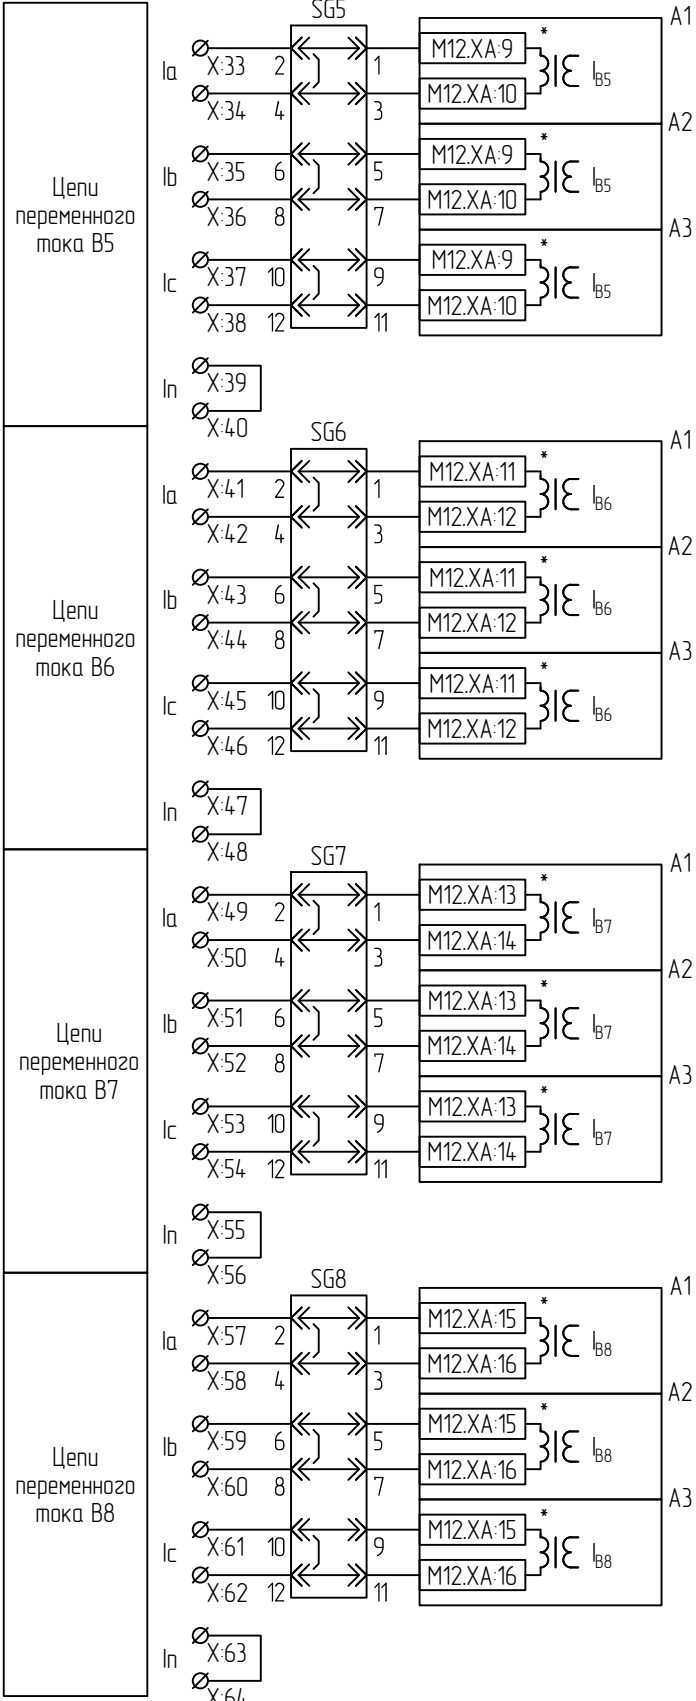


Цепи переменного тока

Цепи переменного напряжения

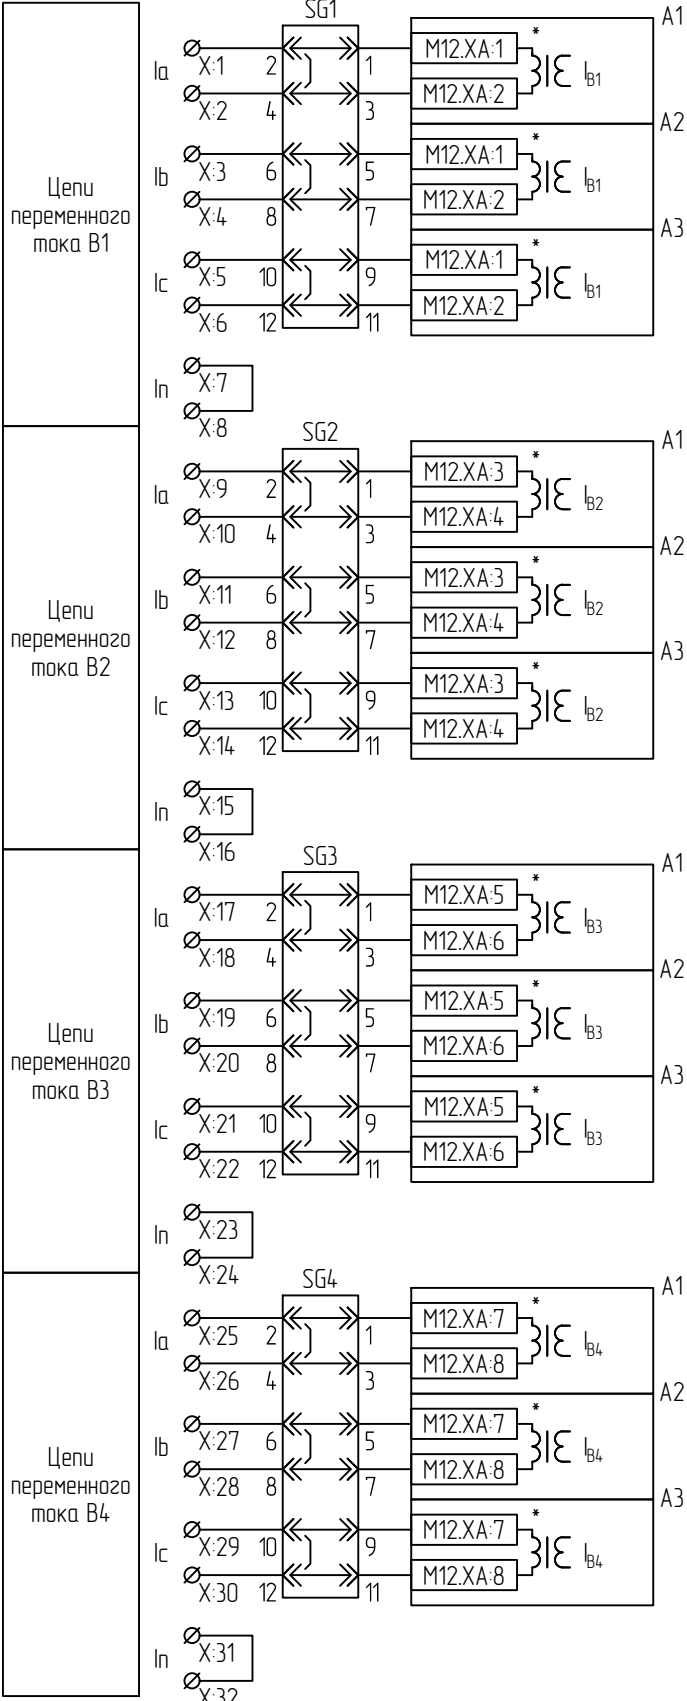

1. Конечное количество портов и тип интерфейсов определяется проектным решением и кодом заказа терминала/шкафа, по согласованию с производителем терминала/шкафа.
2. Конечное количество и функциональное назначение электронных клавиш ИЗУ определяется типом шкафа и проектным решением.