

Цепи оперативного тока

Цепи сигнализации выключателя/ТТ

Питание оперативных цепей, ИЗУ, ИЧМ

Контроль положения испытательных флажков

Контроль положения переключателей

Режим ремонта выключателя

Контроль положения дверей шкафа

Пуск УРОВ В1

Запрет АПВ


Пуск УРОВ НН

Включение от автоматики

Отключение от автоматики

Оперативное включение

Оперативное отключение

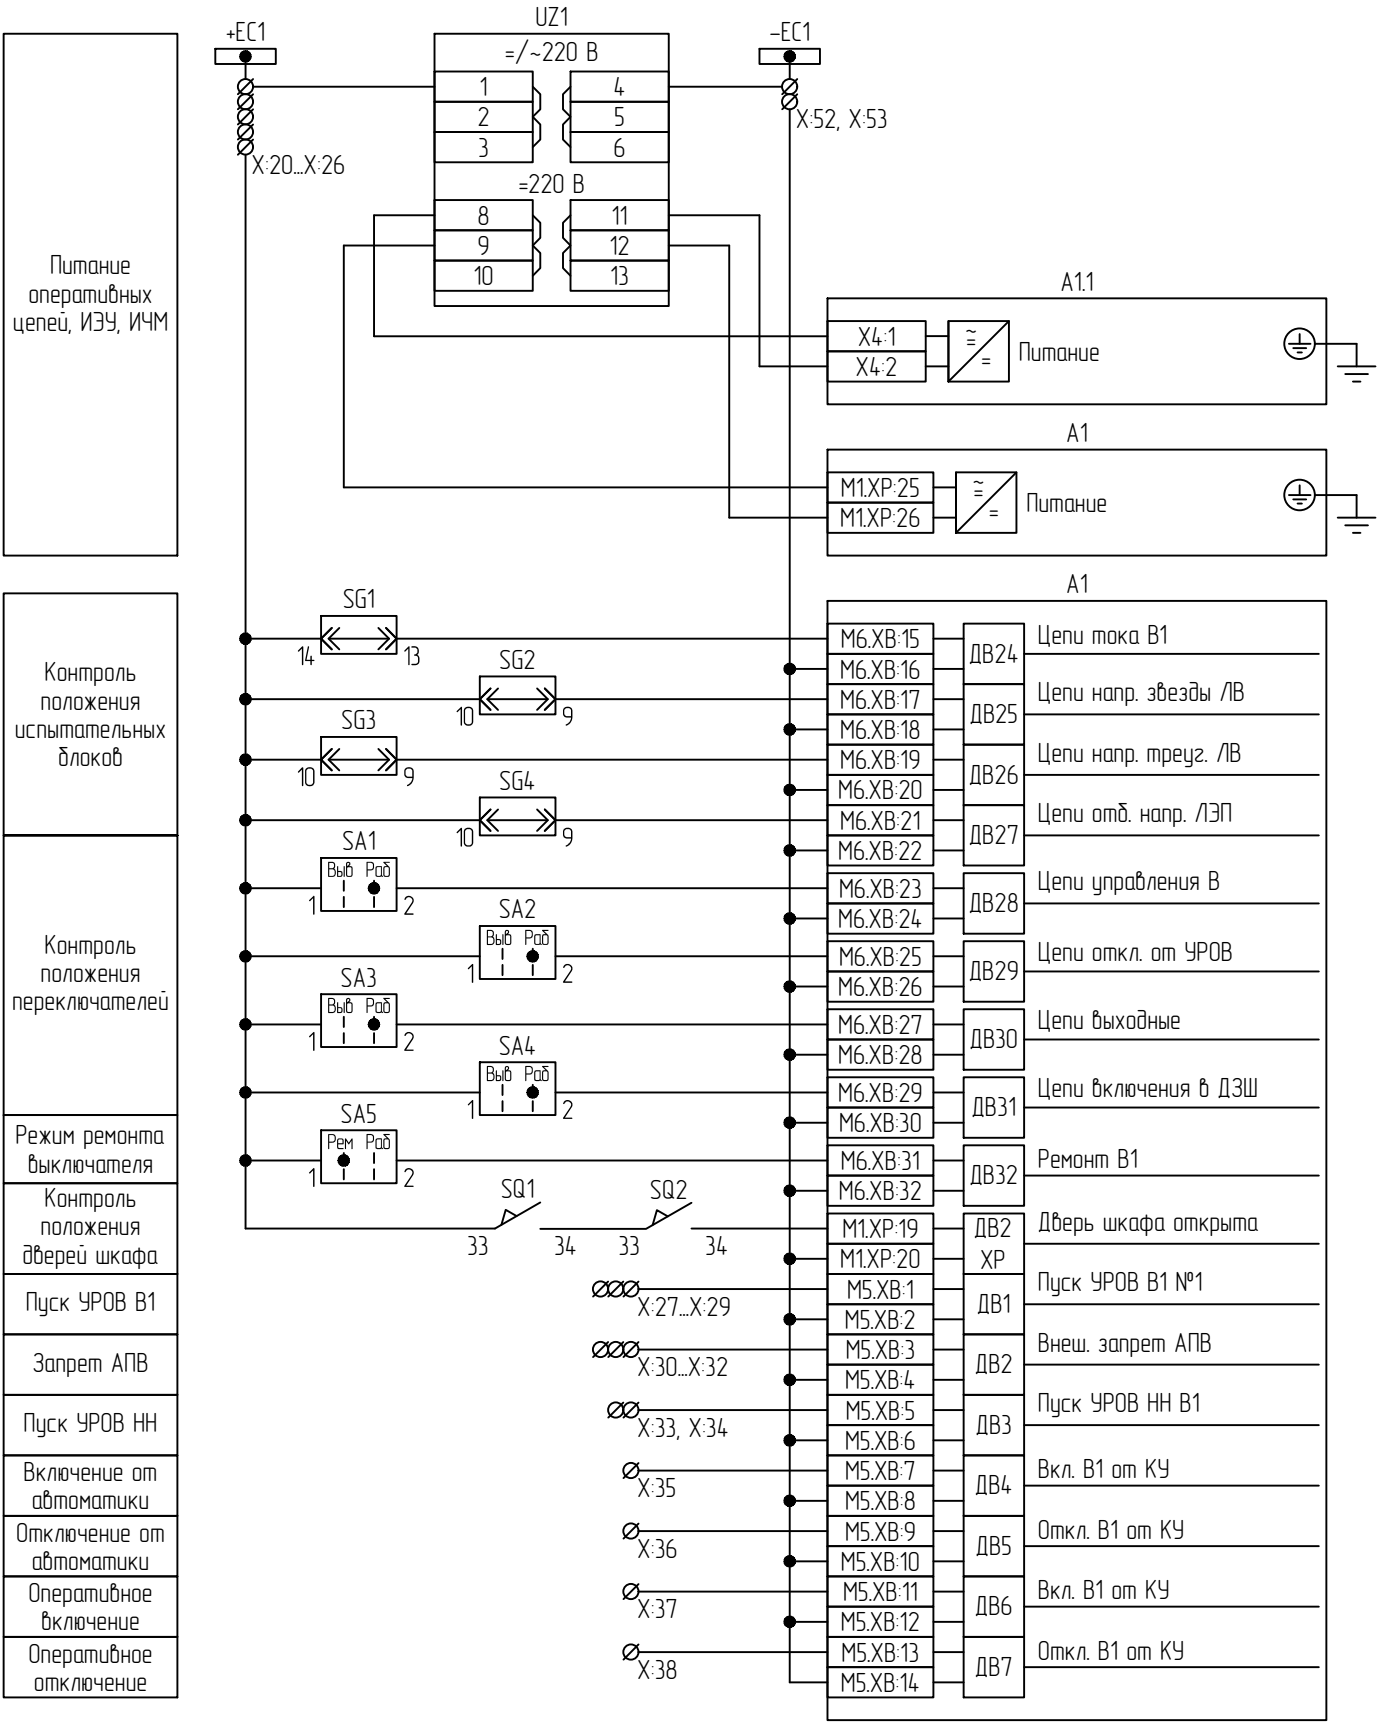

Контроль оперативного тока цепей сигнализации В

РПВ

РПО

Низкая изоляция В

Аварийно низкая изоляция В

Пружины не заведены

Срабатывание ЗНФ

Низкая изоляция ТТ

Аварийно низкая изоляция ТТ

Оперативная фиксация режима ремонта выключателя

РПО от ИЗУ

РПВ от ИЗУ

РПО

РПВ

