


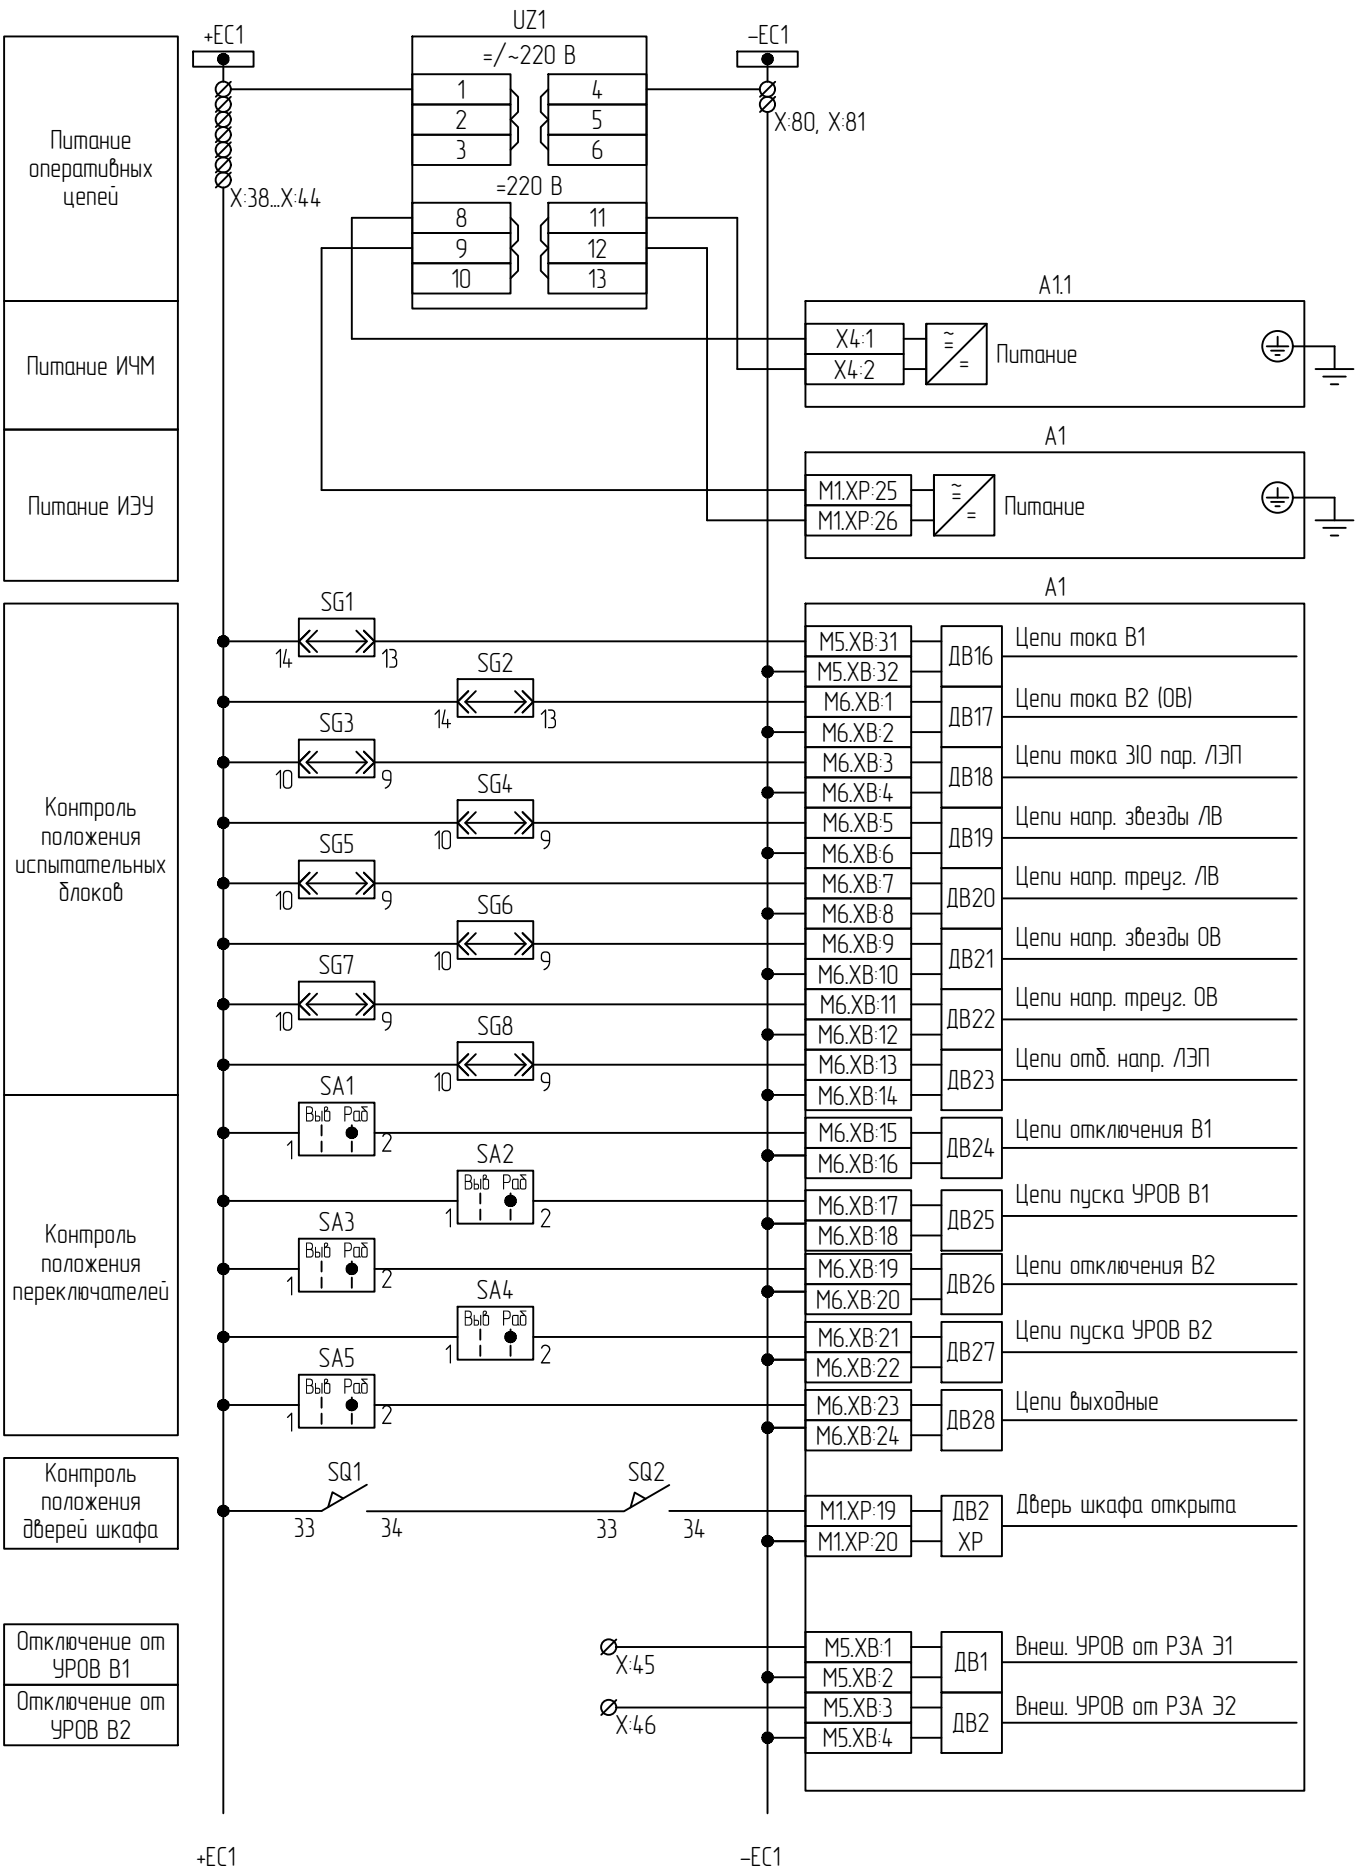

РПВ В1
РПО В1
ЗНФ В1
РПВ В2
РПО В2
ЗНФ В2
РПВ В3
Ускор. от защит парал. линии
РПВ ШСВ
Прием ТО
Прием ТУ ОТФ
Прием ТУ ДЗ
Прием ТУ ТНЗНП

Ø X:47	M5.XB:5	ДВ3	Б/К В1 вкл
Ø X:48	M5.XB:6	ДВ4	Б/К В1 откл
Ø X:49	M5.XB:7	ДВ5	Ср. ЗНФ В1 в ЗНР
Ø X:50	M5.XB:8	ДВ6	Б/К В2 вкл
Ø X:51	M5.XB:9	ДВ7	Б/К В2 откл
Ø X:52	M5.XB:10	ДВ8	Ср. ЗНФ В2 в ЗНР
Ø X:53	M5.XB:11	ДВ9	ВЗ отключен в ЗНР
Ø X:54	M5.XB:12	ДВ10	ПУ от пар. ЛЭП
Ø X:55	M5.XB:13	ДВ11	Б/К ШСВ/СВ вкл
Ø X:56	M5.XB:14	ДВ12	Прием Тоткл
Ø X:57	M5.XB:15	ДВ13	Прием ТУ ОТФ
Ø X:58	M5.XB:16	ДВ14	Прием ТУ ДЗ
Ø X:59	M5.XB:17	ДВ15	Прием ТУ ТНЗНП
	M5.XB:18		
	M5.XB:19		
	M5.XB:20		
	M5.XB:21		
	M5.XB:22		
	M5.XB:23		
	M5.XB:24		
	M5.XB:25		
	M5.XB:26		
	M5.XB:27		
	M5.XB:28		
	M5.XB:29		
	M5.XB:30		