



Цепи оперативного тока Т3 Т А1

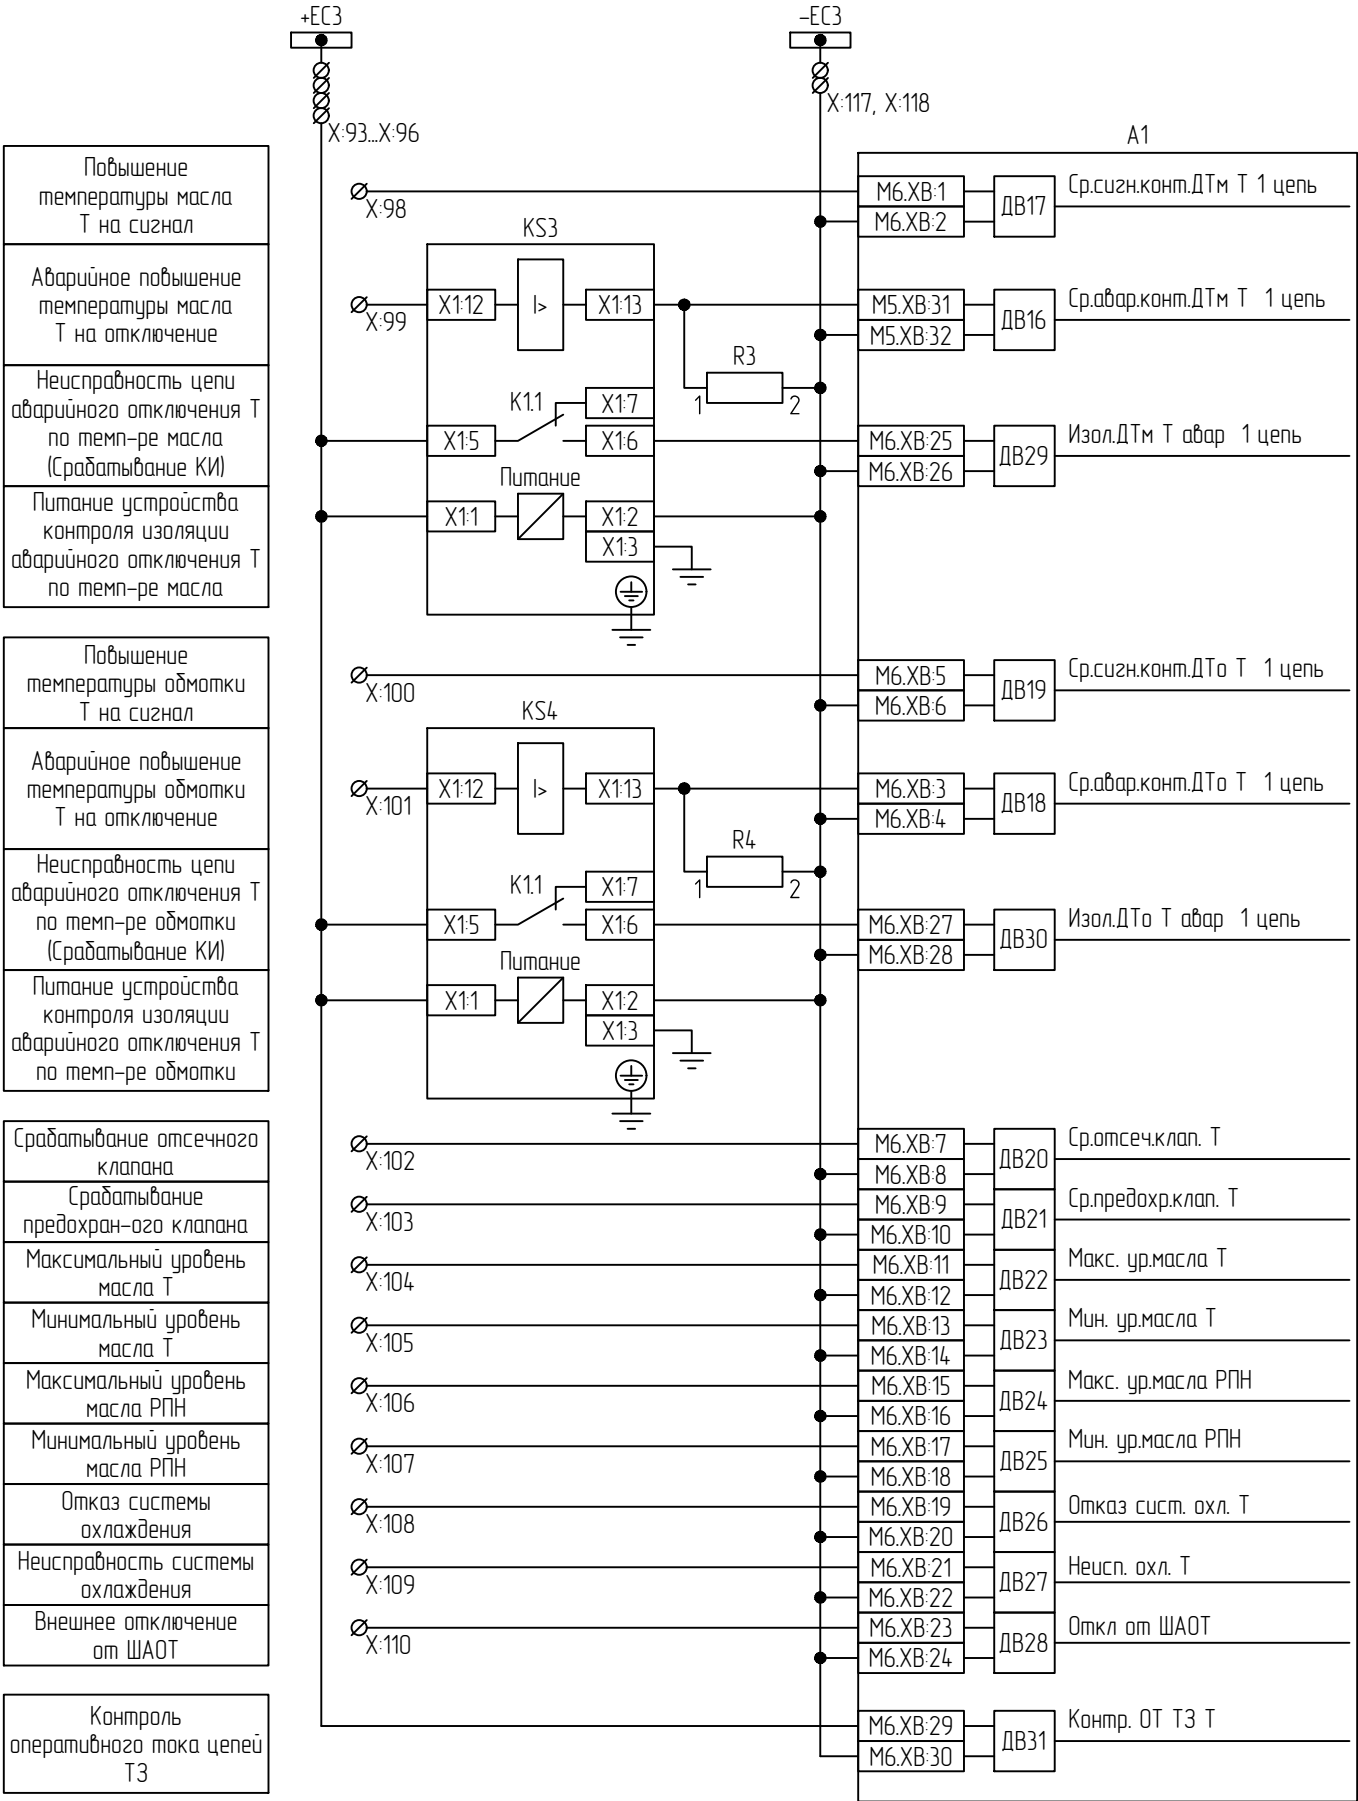


Цепи ЗДЗ (НН, СН) А1

Срабатывание ЗДЗ секции
Контроль опертока ЗДЗ секции

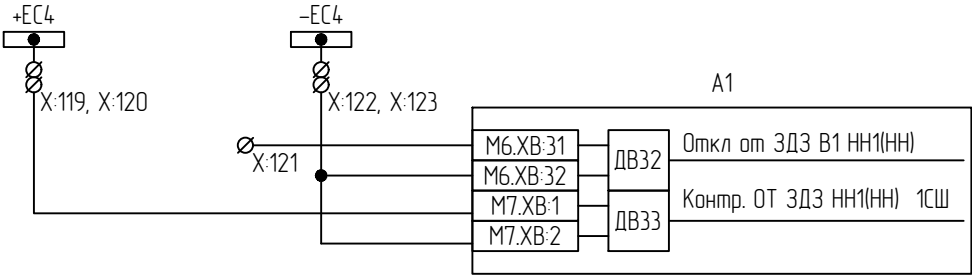


Цепи ввода (НН, СН) А1

Срабатывание УРОВ ввода
РПВ ввода
Контроль опертока ввода

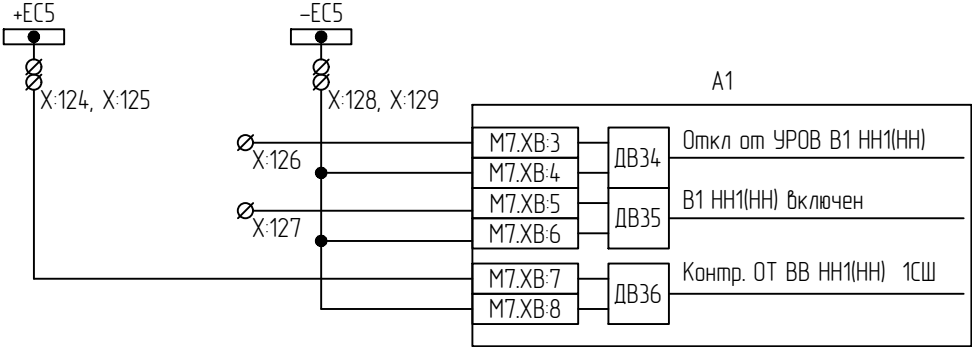

Цепи ЗДЗ (НН, СН) А1

Срабатывание ЗДЗ секции
Контроль опертока ЗДЗ секции

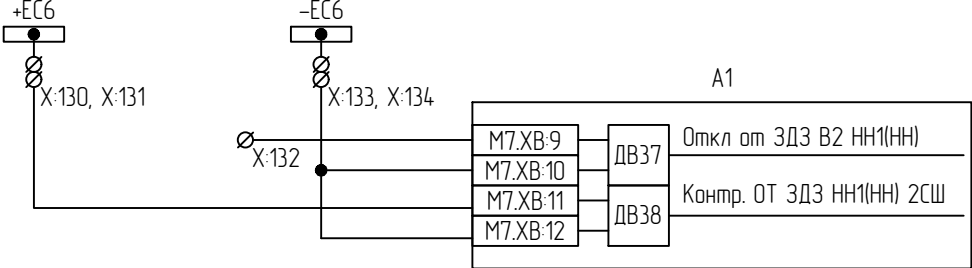

Цепи ввода (НН, СН) А1

Срабатывание УРОВ ввода
РПВ ввода
Контроль опертока ввода

