

Цепи переменного тока ВН


Цепи переменного тока СН

Цепи переменного напряжения НН1 (НН)

Цепи переменного напряжения НН2

Цепи переменного напряжения СН (НН3)

Цепи переменного напряжения НН4

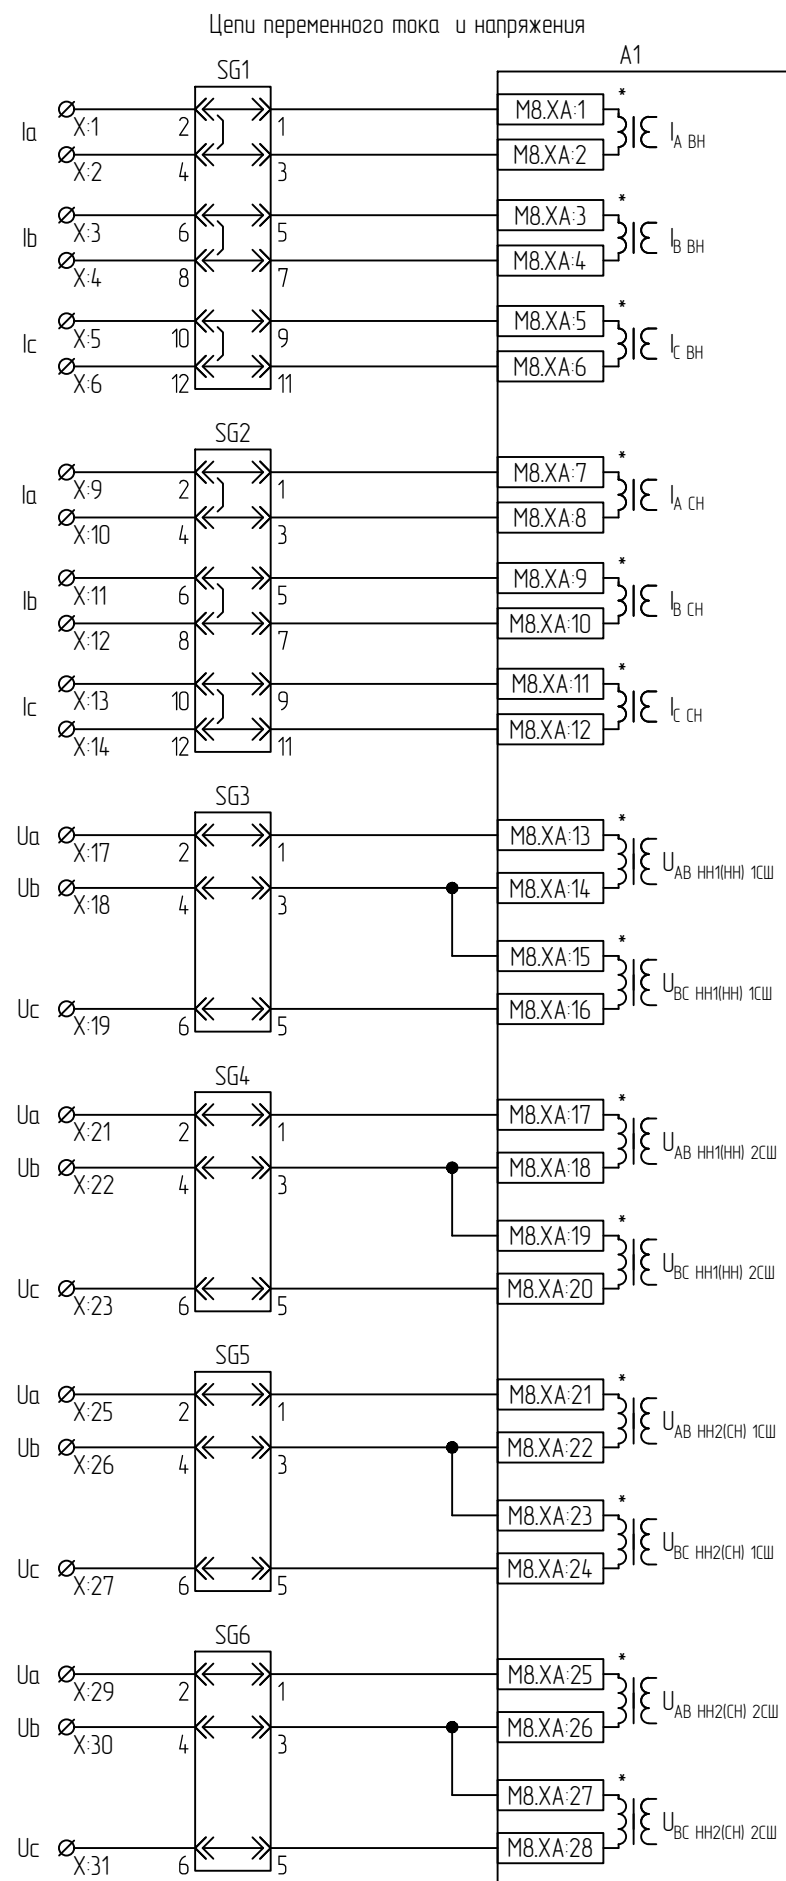


Питание оперативных цепей

Питание ИЧМ

Питание ИЗУ

Контроль положения испытательных блоков

Контроль положения переключателей

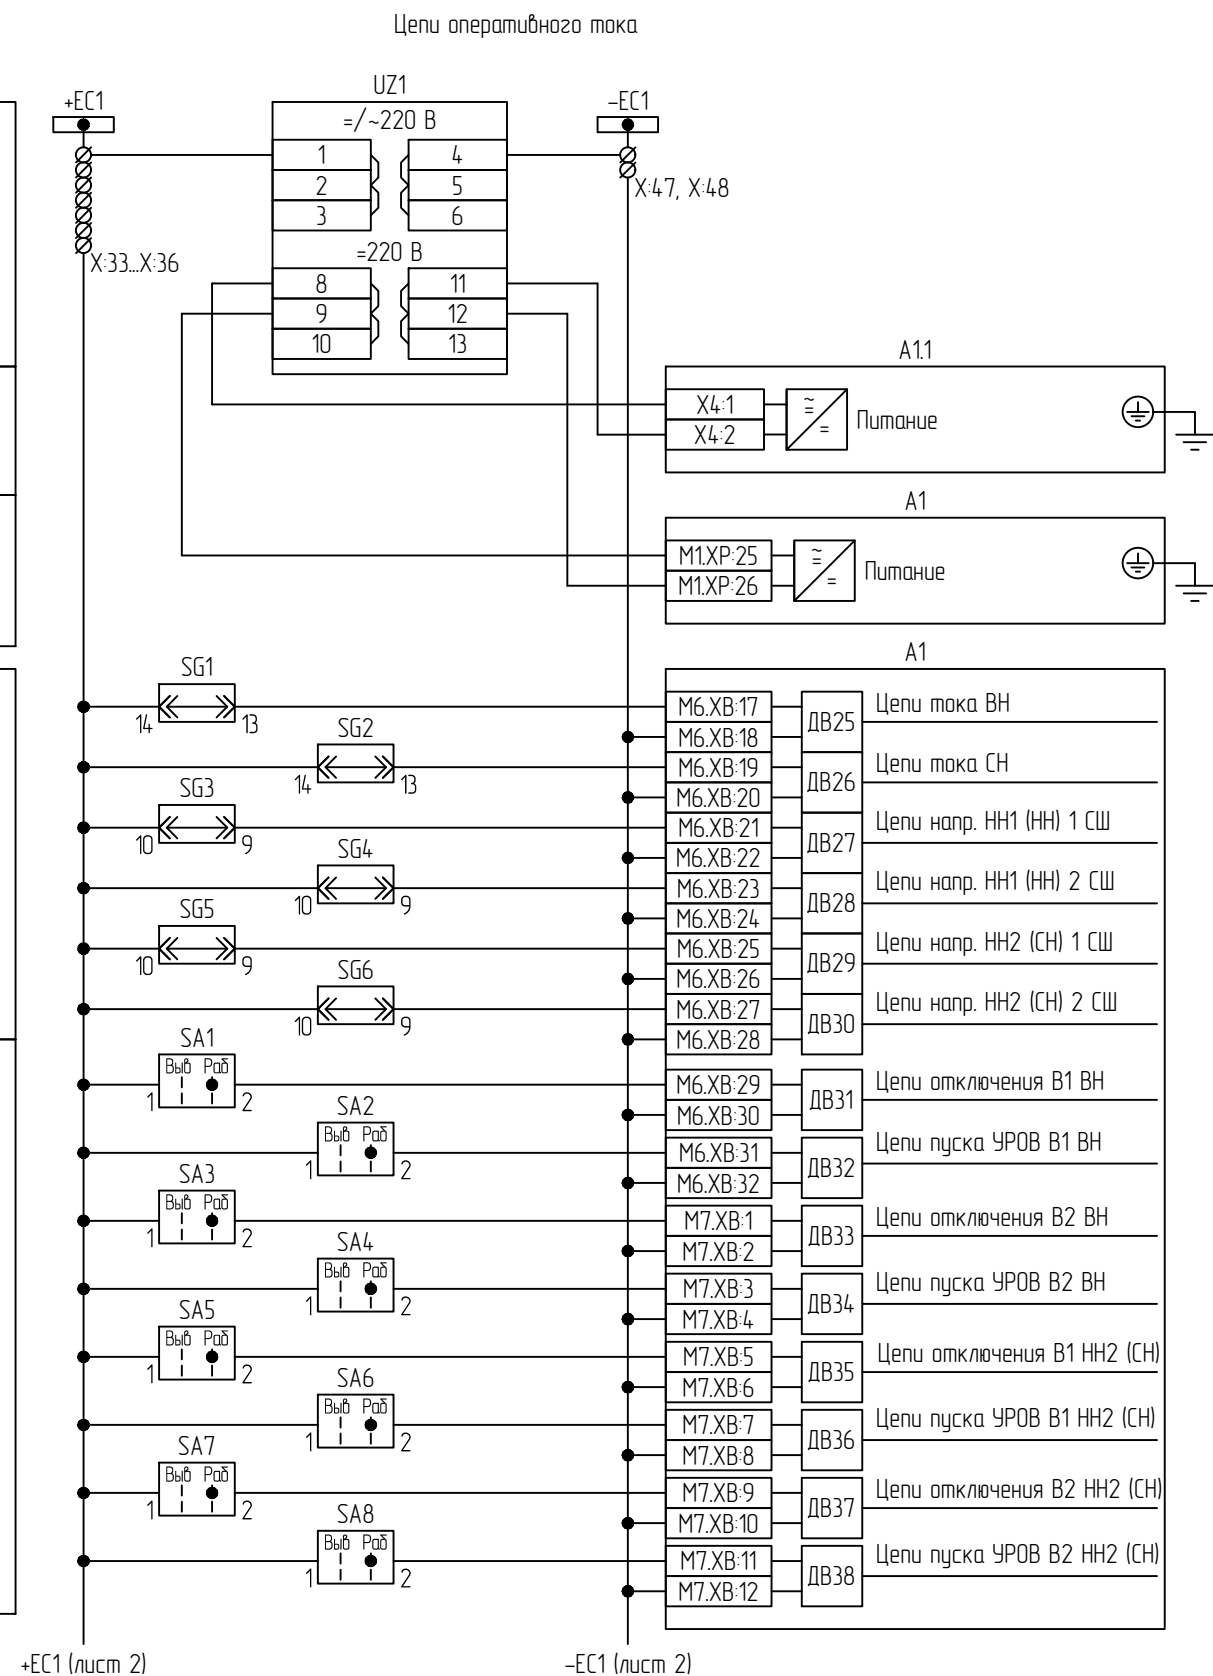

1. Конечное количество портов и тип интерфейсов определяется проектным решением и кодом заказа терминала/шкафа, по согласованию с производителем терминала/шкафа.
2. Конечное количество и функциональное назначение электронных клавиш ИЗУ определяется типом шкафа и проектным решением.