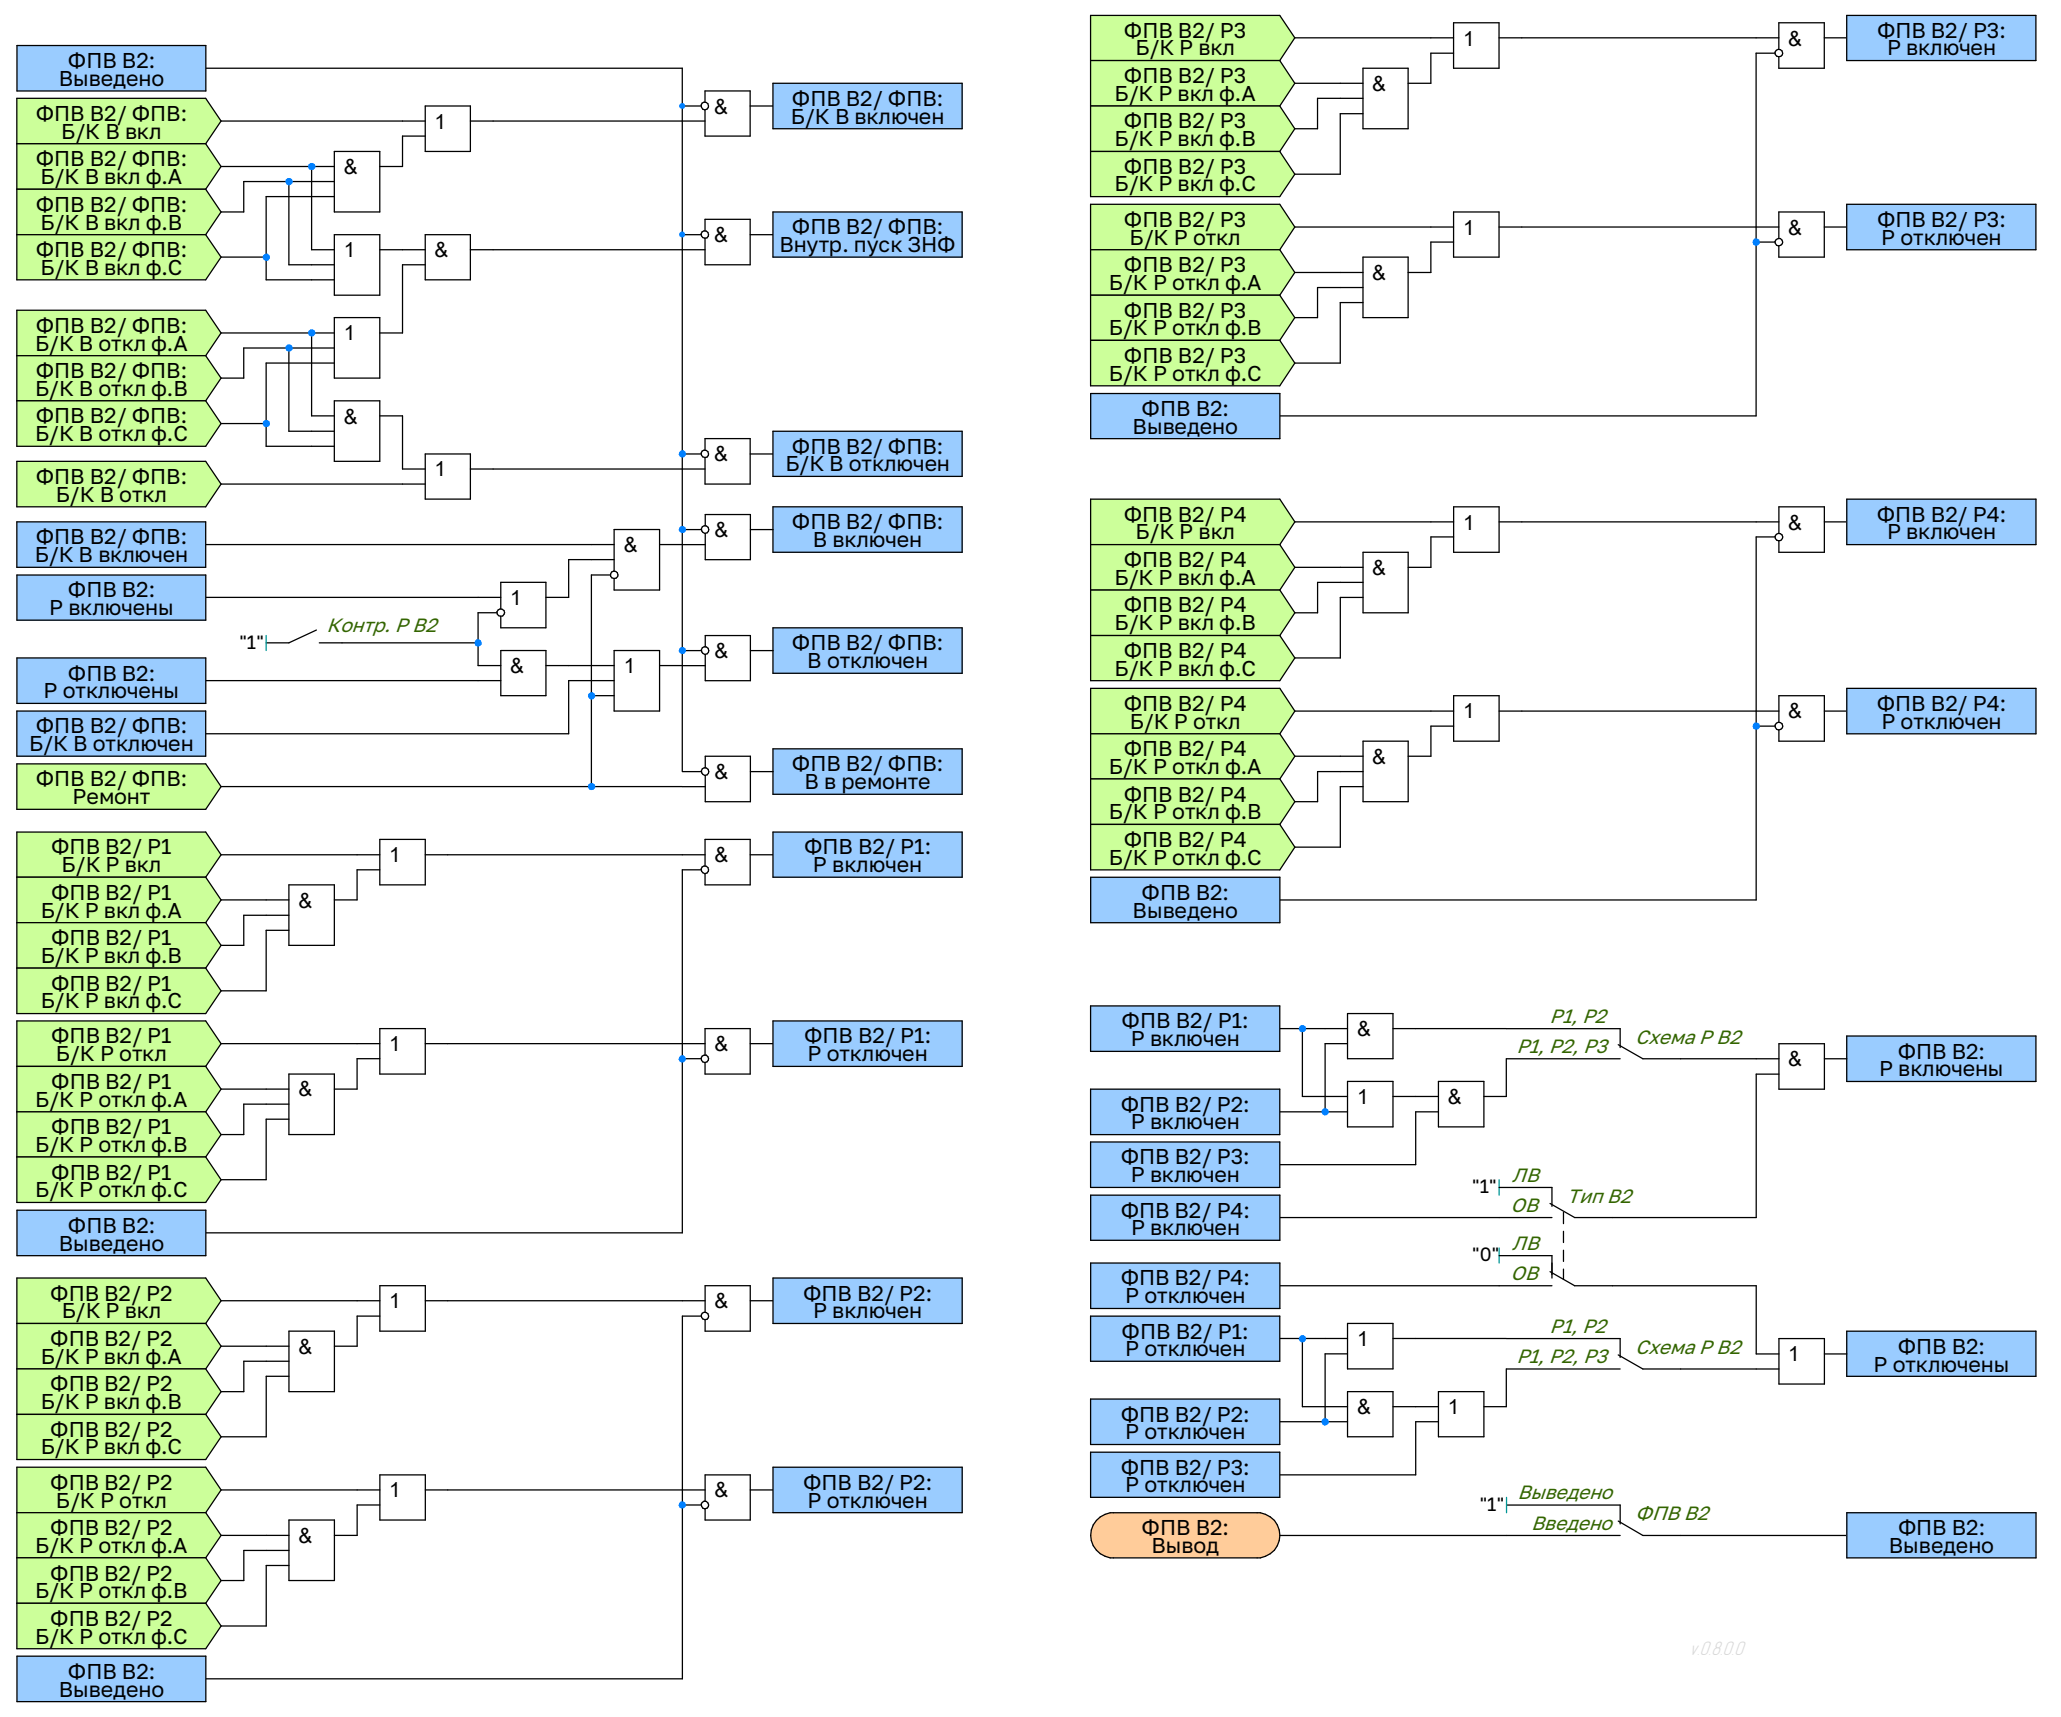
ФПВ В2: Выведено
ФПВ В2/ ФПВ: Б/К В вкл
ФПВ В2/ ФПВ: Б/К В вкл ф.А
ФПВ В2/ ФПВ: Б/К В вкл ф.В
ФПВ В2/ ФПВ: Б/К В вкл ф.С
ФПВ В2/ ФПВ: Б/К В включен
ФПВ В2/ ФПВ: Внутр. пуск ЗНФ
ФПВ В2/ ФПВ: Б/К В откл ф.А
ФПВ В2/ ФПВ: Б/К В откл ф.В
ФПВ В2/ ФПВ: Б/К В откл ф.С
ФПВ В2/ ФПВ: Б/К В откл
ФПВ В2/ ФПВ: Б/К В отключен
ФПВ В2/ ФПВ: Б/К В включен
ФПВ В2: Р включены
"1"
Контр. Р В2
ФПВ В2/ ФПВ: В включен
ФПВ В2: Р отключены
ФПВ В2/ ФПВ: Б/К В отключен
ФПВ В2/ ФПВ: Ремонт
ФПВ В2/ ФПВ: В отключен
ФПВ В2/ ФПВ: В в ремонте
ФПВ В2/ Р1 Б/К Р вкл
ФПВ В2/ Р1 Б/К Р вкл ф.А
ФПВ В2/ Р1 Б/К Р вкл ф.В
ФПВ В2/ Р1 Б/К Р вкл ф.С
ФПВ В2/ Р1: Р включен
ФПВ В2/ Р1 Б/К Р откл
ФПВ В2/ Р1 Б/К Р откл ф.А
ФПВ В2/ Р1 Б/К Р откл ф.В
ФПВ В2/ Р1 Б/К Р откл ф.С
ФПВ В2/ Р1: Р отключен
ФПВ В2: Выведено
ФПВ В2/ Р2 Б/К Р вкл
ФПВ В2/ Р2 Б/К Р вкл ф.А
ФПВ В2/ Р2 Б/К Р вкл ф.В
ФПВ В2/ Р2 Б/К Р вкл ф.С
ФПВ В2/ Р2: Р включен
ФПВ В2/ Р2 Б/К Р откл
ФПВ В2/ Р2 Б/К Р откл ф.А
ФПВ В2/ Р2 Б/К Р откл ф.В
ФПВ В2/ Р2 Б/К Р откл ф.С
ФПВ В2/ Р2: Р отключен
ФПВ В2: Выведено
ФПВ В2/ Р3 Б/К Р вкл
ФПВ В2/ Р3 Б/К Р вкл ф.А
ФПВ В2/ Р3 Б/К Р вкл ф.В
ФПВ В2/ Р3 Б/К Р вкл ф.С
ФПВ В2/ Р3: Р включен
ФПВ В2/ Р3 Б/К Р откл
ФПВ В2/ Р3 Б/К Р откл ф.А
ФПВ В2/ Р3 Б/К Р откл ф.В
ФПВ В2/ Р3 Б/К Р откл ф.С
ФПВ В2/ Р3: Р отключен
ФПВ В2: Выведено
ФПВ В2/ Р4 Б/К Р вкл
ФПВ В2/ Р4 Б/К Р вкл ф.А
ФПВ В2/ Р4 Б/К Р вкл ф.В
ФПВ В2/ Р4 Б/К Р вкл ф.С
ФПВ В2/ Р4: Р включен
ФПВ В2/ Р4 Б/К Р откл
ФПВ В2/ Р4 Б/К Р откл ф.А
ФПВ В2/ Р4 Б/К Р откл ф.В
ФПВ В2/ Р4 Б/К Р откл ф.С
ФПВ В2/ Р4: Р отключен
ФПВ В2: Выведено
ФПВ В2/ Р1: Р включен
ФПВ В2/ Р2: Р включен
ФПВ В2/ Р3: Р включен
ФПВ В2/ Р4: Р включен
Р1, Р2
Р1, Р2, Р3
Схема Р В2
ФПВ В2: Р включены
"1"
ЛВ
ОВ
Тип В2
"0"
ЛВ
ОВ
ФПВ В2/ Р4: Р отключен
ФПВ В2/ Р1: Р отключен
ФПВ В2/ Р2: Р отключен
ФПВ В2/ Р3: Р отключен
Р1, Р2
Р1, Р2, Р3
Схема Р В2
ФПВ В2: Р отключены
"1"
Выведено
Введено
ФПВ В2
ФПВ В2: Вывод
ФПВ В2: Выведено