КСН В1(ЛВ)ВН 3491

КСН 6811

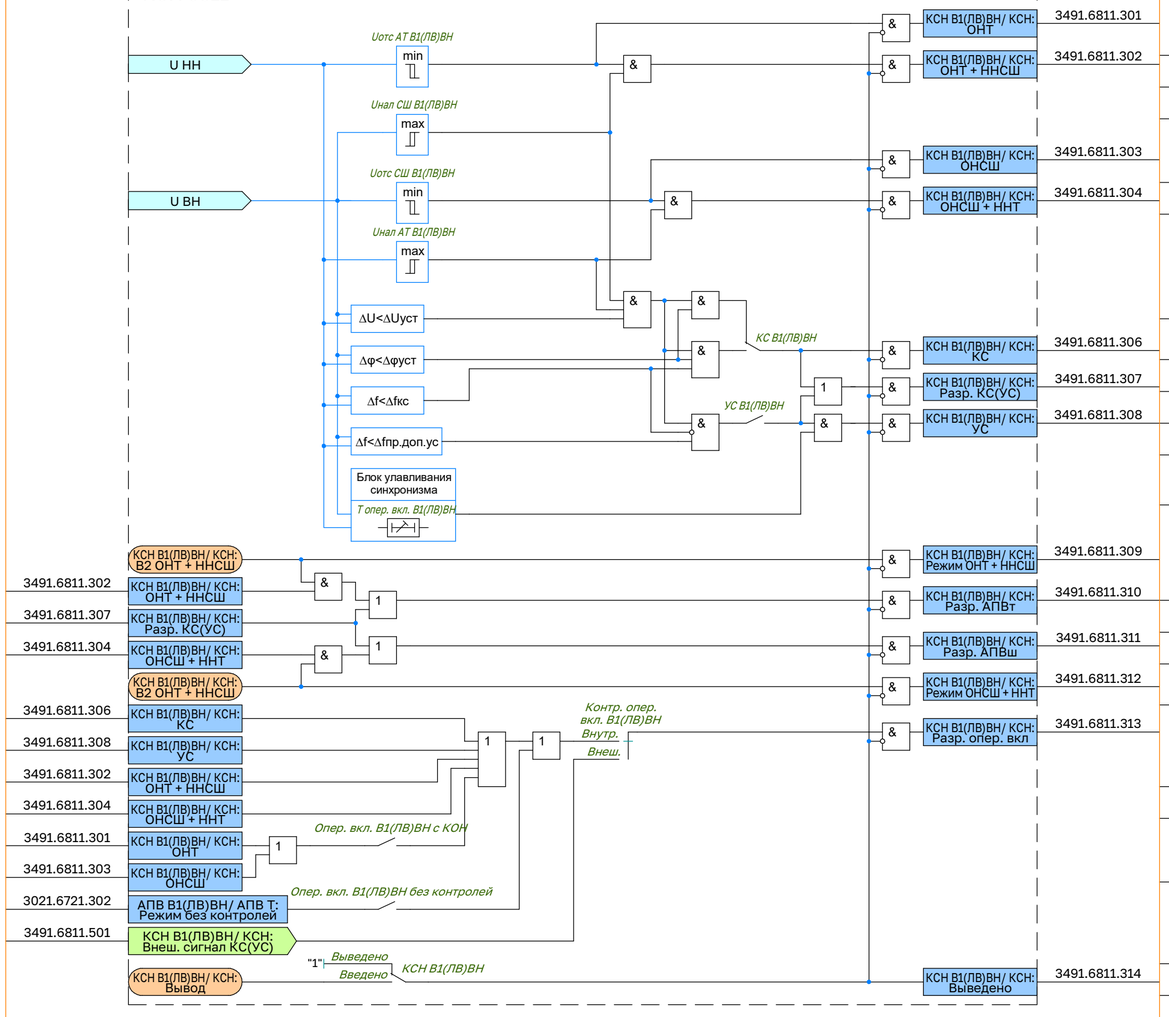

АПВ В1(ЛВ)ВН 3021

АПВ Т 6721

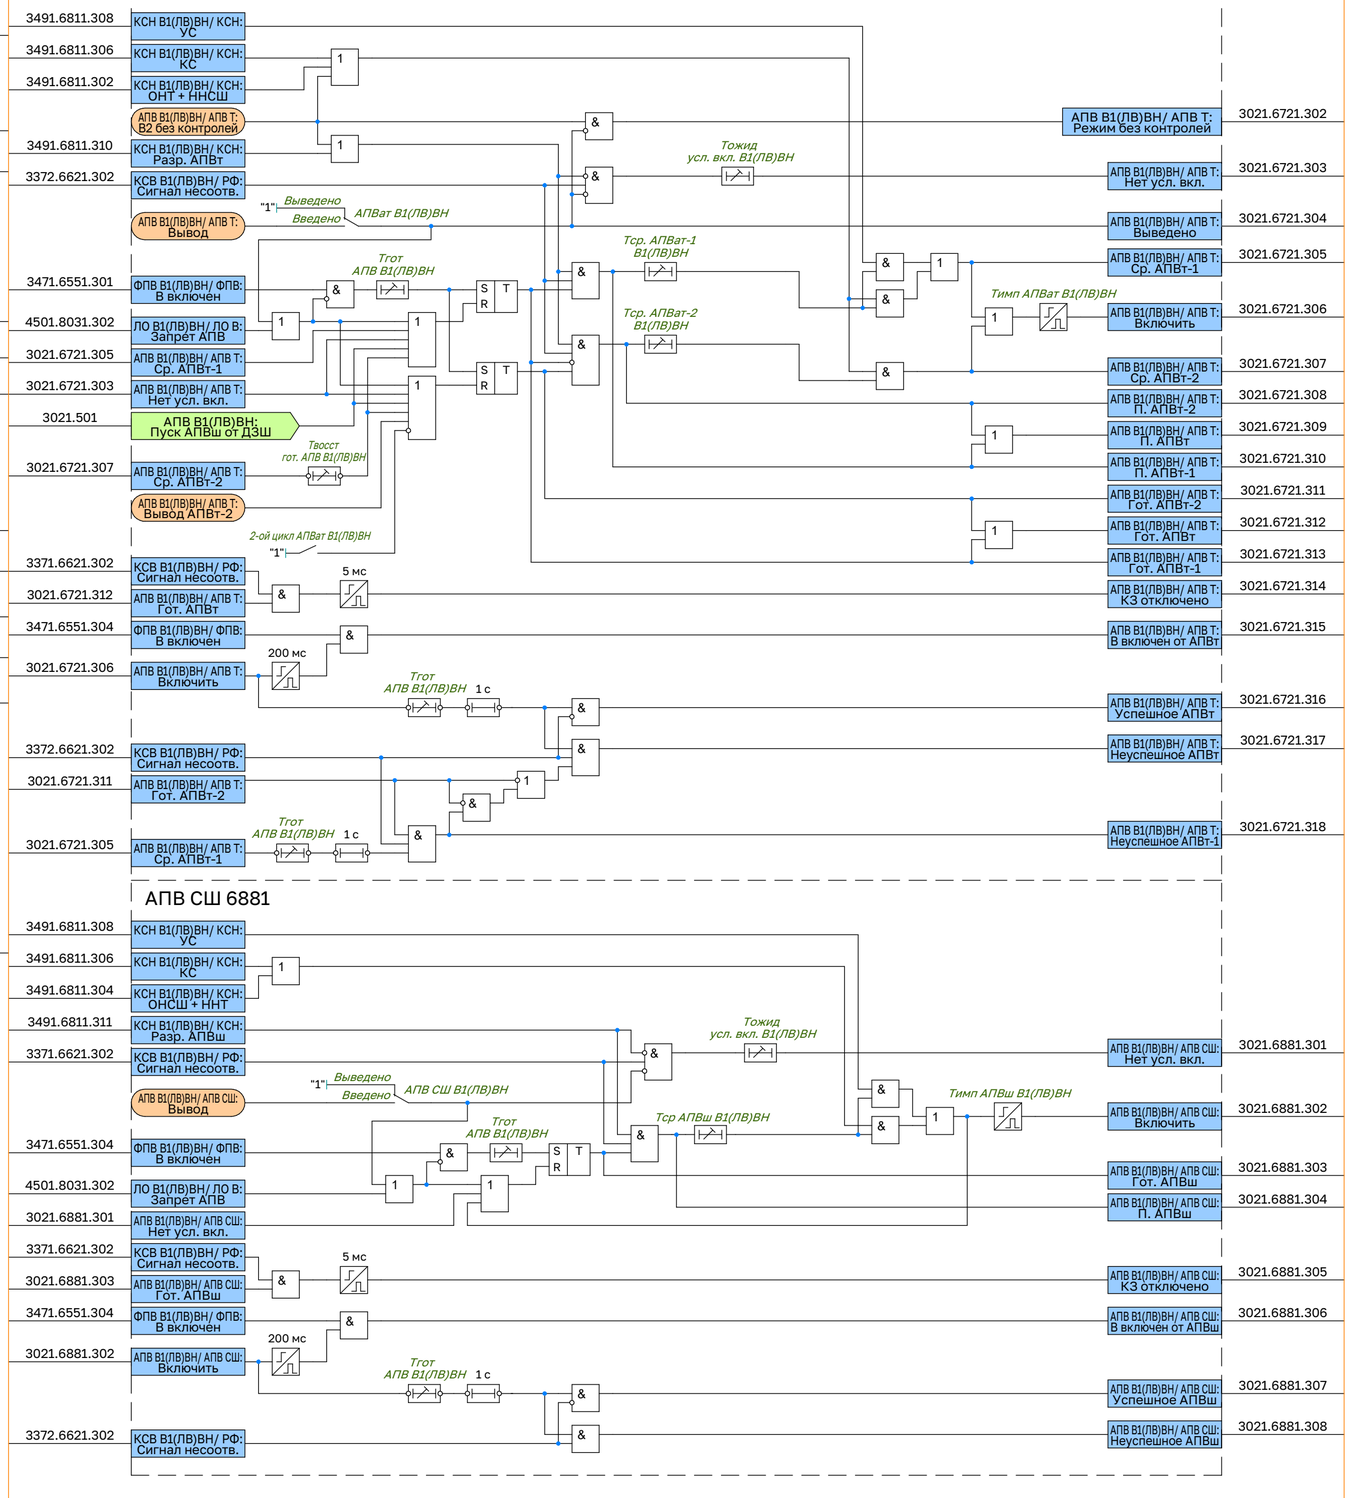

АПВ СШ 6881