



УРОВ В1 3331

УРОВ 6511

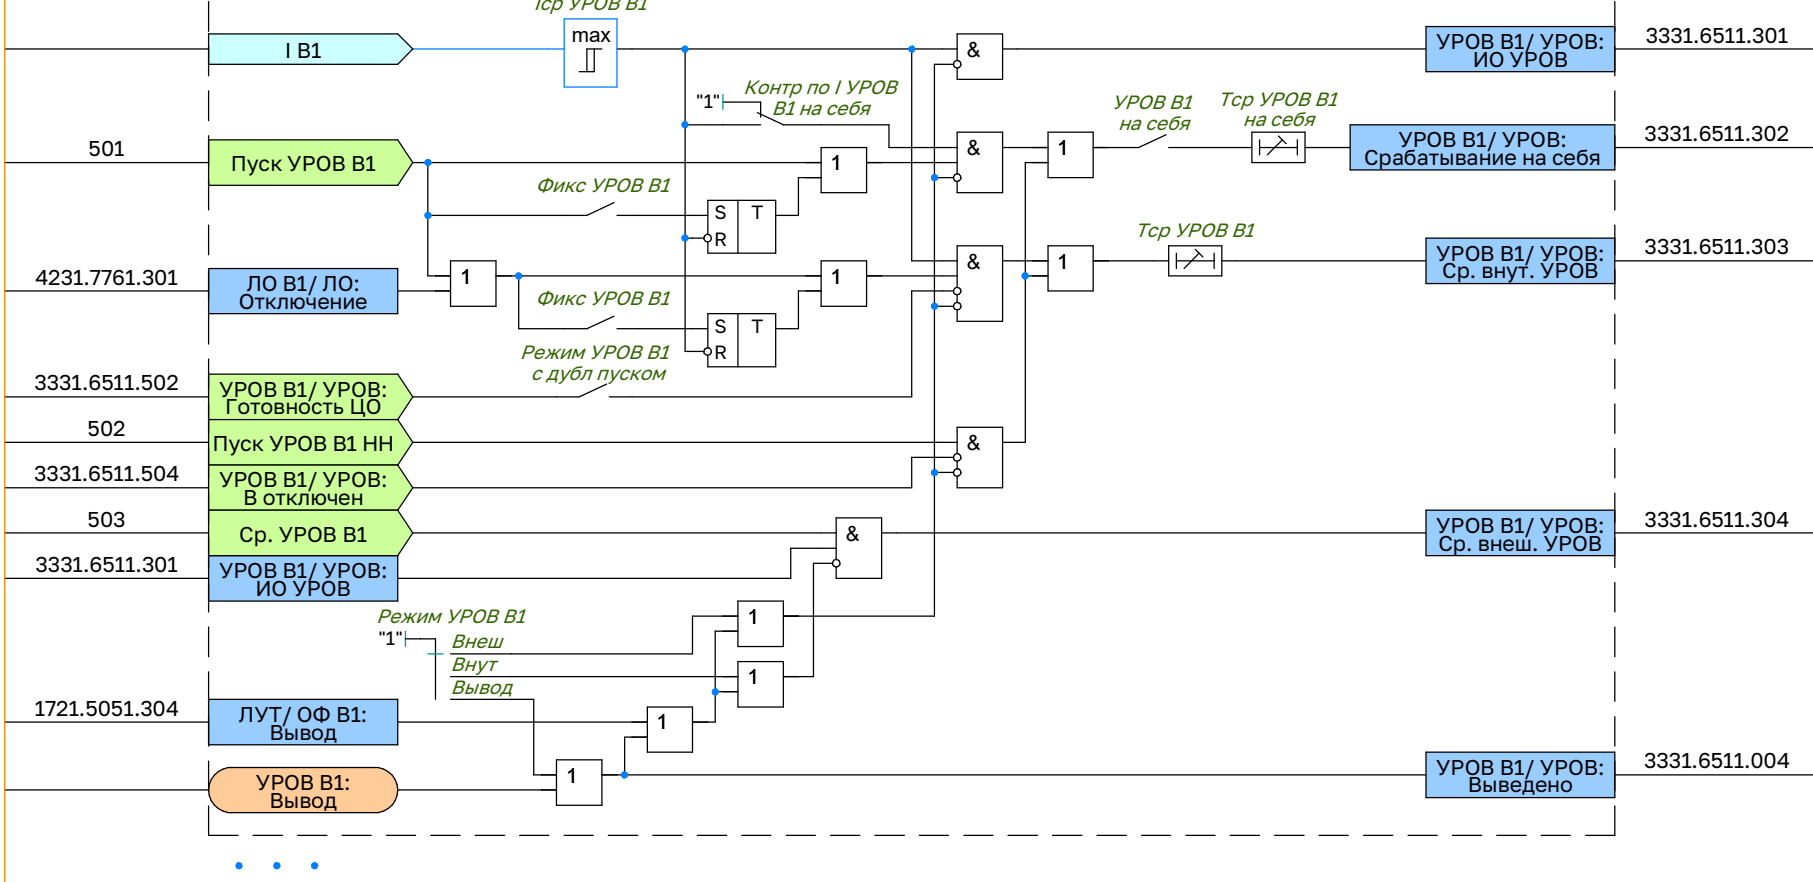

УРОВ В24 33324

УРОВ 6511

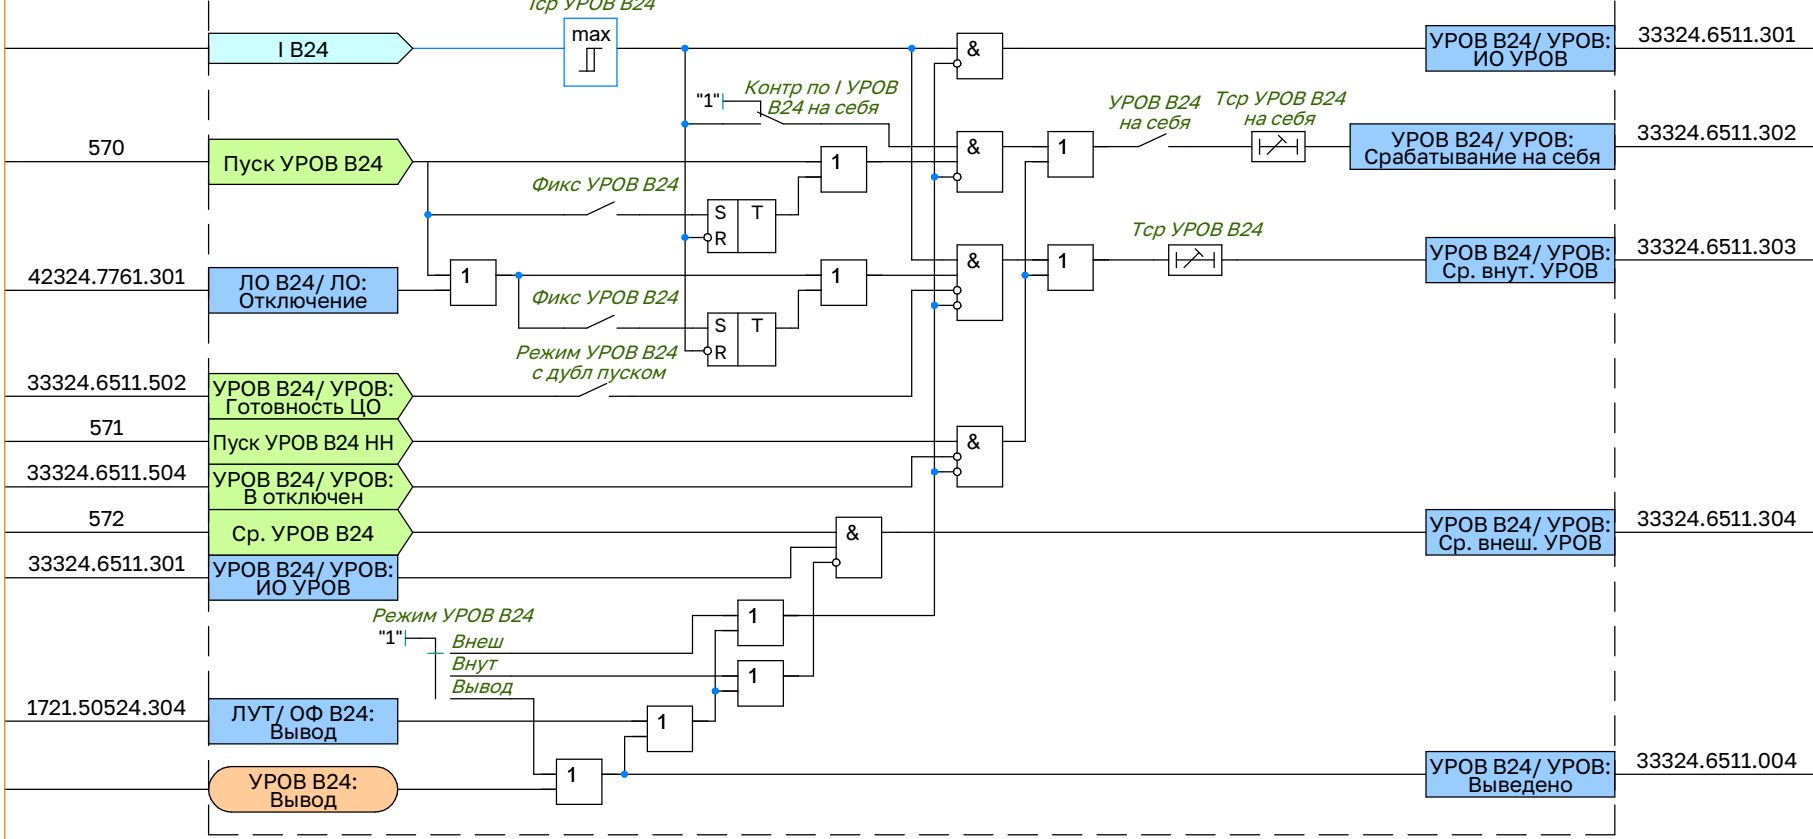

УРОВ СШ 1861

УРОВ 5141

