

ЦОС.ХХ

ХА1:1	IA B(B1) BB*
ХА1:2	IA B(B1) BB
ХА1:3	IB B(B1) BB*
ХА1:4	IB B(B1) BB
ХА1:5	IC B(B1) BB*
ХА1:6	IC B(B1) BB
ХА1:7	IA OB(B2) BB*
ХА1:8	IA OB(B2) BB
ХА1:9	IB OB(B2) BB*
ХА1:10	IB OB(B2) BB
ХА1:11	IC OB(B2) BB*
ХА1:12	IC OB(B2) BB
ХА1:13	I резерв*
ХА1:14	I резерв
ХА1:15	UA*
ХА1:16	UA
ХА1:17	UB*
ХА1:18	UB
ХА1:19	UC*
ХА1:20	UC

ХА2:1	IA HB*
ХА2:2	IA HB
ХА2:3	IB HB*
ХА2:4	IB HB
ХА2:5	IC HB*
ХА2:6	IC HB
ХА2:7	IA СП*
ХА2:8	IA СП
ХА2:9	IB СП*
ХА2:10	IB СП
ХА2:11	IC СП*
ХА2:12	IC СП
ХА2:13	I нейтр*
ХА2:14	I нейтр
ХА2:15	УНИ(УНФ)*
ХА2:16	УНИ(УНФ)
ХА2:17	УИК(УФК)*
ХА2:18	УИК(УФК)
ХА2:19	УИФ(УНК)*
ХА2:20	УИФ(УНК)

Идиф,а ДТЗ (1г)	
Идиф,б ДТЗ (1г)	
Идиф,с ДТЗ (1г)	
Иторм ДЗТ	
K2г (Идиф.а)	
K2г (Идиф.б)	
K2г (Идиф.с)	
K5г (Идиф.а)	
K5г (Идиф.б)	
K5г (Идиф.с)	
Идиф ДТЗ НП	
Иторм ДТЗ НП	
ЗИО ВВ*	
Инейтр*	
Ia_нб	
Ib_нб	
Ic_нб	
Ia ВВ	
Ib ВВ	
Ic ВВ	
Iab ВВ	
Ibc ВВ	
Ica ВВ	
Ia_скз ВВ	
Ib_скз ВВ	
Ic_скз ВВ	
K2r (Ia ВВ)	
K2r (Iab ВВ)	
K2r (Ib ВВ)	
K2r (Ibc ВВ)	
K2r (Ic ВВ)	
K2r (Ica ВВ)	
I2 ВВ	
ЗИО ВВ	
ЗИО HB	
Инейтр	
Ua	
Uab	
Ub	
Ubc	
Uc	
Uca	
dU1	
dI1	
U1	
I1	
Ua	
Ub	
Uc	
I2/I1	
U2/U1	
U2	
ЗИО/I1	
ЗИО звезда	
Убнн	
Уни	
Уиф	
Уфк	
Убнн фА	
Убнн-фВ	
Убнн фС	

Входы ФСУ

Общая логика: Контр. ОТ терм.	90.501
Общая логика: БИ ток B(B1) BB	90.502
Общая логика: БИ ток OB(B2) BB	90.503
Общая логика: БИ ток HB	90.504
Общая логика: БИ ток. СП	90.505
Общая логика: БИ ток. ЗН	90.506
Общая логика: БИ напр. (зв.)	90.507
Общая логика: БИ напр. (тр.)	90.508
Общая логика: SA Откл. B(B1) BH	90.509
Общая логика: SA Откл. OB (B2) BH	90.510
Общая логика: SA УРОВ B(B1) BH	90.511
Общая логика: SA УРОВ OB (B2) BH	90.512
Общая логика: SA Откл. ЗНР	90.513
Общая логика: Вых. цепи разобраны	90.514
ДТЗ/ КЦТ: Сброс	0611.1561.501
БНН/ БНН: Автомат ТН	1511.4531.501
БНН/ БНН: Фикс. неистр. ЦН	1511.4531.502
Сброс	501
Сигнализация: Контр. ОТ терм.	91.502
Сигнализация: Дверь открыта	91.503
ТС ТТ БСК/ КИ ТТ: Низк.ур.изол.ТТ ВВ	1231.3631.501
ТС ТТ БСК/ КИ ТТ: Низк.ур.изол.ТТ HB	1231.3631.502
ТС ТТ БСК/ КИ ТТ: Низк.ур.изол.ТТ HB	1231.3631.503
ТС ТТ БСК/ КИ ТТ: Низк.ур.изол.ТТ нейтр	1231.3631.504
ТС ТТ БСК/ КИ ТТ: Авар.ур.изол.ТТ ВВ	1231.3631.505
ТС ТТ БСК/ КИ ТТ: Авар.ур.изол.ТТ HB	1231.3631.506
ТС ТТ БСК/ КИ ТТ: Авар.ур.изол.ТТ HB	1231.3631.507
ТС ТТ БСК/ КИ ТТ: Авар.ур.изол.ТТ нейтр	1231.3631.508
ФПВ В1(ЛВ)/ ФПВ: Б/К В включен	3381.6551.501
ФПВ В1(ЛВ)/ ФПВ: Б/К В фА включен	3381.6551.502
ФПВ В1(ЛВ)/ ФПВ: Б/К В фВ включен	3381.6551.503
ФПВ В1(ЛВ)/ ФПВ: Б/К В фС включен	3381.6551.504
ФПВ В1(ЛВ)/ ФПВ: Б/К В фА отключен	3381.6551.505
ФПВ В1(ЛВ)/ ФПВ: Б/К В фВ отключен	3381.6551.506
ФПВ В1(ЛВ)/ ФПВ: Б/К В фС отключен	3381.6551.507
ФПВ В1(ЛВ)/ ФПВ: Б/К В отключен	3381.6551.508
ФПВ В1(ЛВ)/ ФПВ: Ремонт	3381.6551.509
ФПВ В1(ЛВ)/ ФПВ: Б/К Р1 включен	3381.6531.501
ФПВ В1(ЛВ)/ ФПВ: Б/К Р1 фА включен	3381.6531.502
ФПВ В1(ЛВ)/ ФПВ: Б/К Р1 фВ включен	3381.6531.503
ФПВ В1(ЛВ)/ ФПВ: Б/К Р1 фС включен	3381.6531.504
ФПВ В1(ЛВ)/ ФПВ: Б/К Р1 отключен	3381.6531.505
ФПВ В1(ЛВ)/ ФПВ: Б/К Р1 фА отключен	3381.6531.506
ФПВ В1(ЛВ)/ ФПВ: Б/К Р1 фВ отключен	3381.6531.507
ФПВ В1(ЛВ)/ ФПВ: Б/К Р1 фС отключен	3381.6531.508
ФПВ В1(ЛВ)/ ФПВ: Б/К Р2 включен	3381.6532.501
ФПВ В1(ЛВ)/ ФПВ: Б/К Р2 фА включен	3381.6532.502
ФПВ В1(ЛВ)/ ФПВ: Б/К Р2 фВ включен	3381.6532.503
ФПВ В1(ЛВ)/ ФПВ: Б/К Р2 фС включен	3381.6532.504
ФПВ В1(ЛВ)/ ФПВ: Б/К Р2 отключен	3381.6532.505
ФПВ В1(ЛВ)/ ФПВ: Б/К Р2 фА отключен	3381.6532.506
ФПВ В1(ЛВ)/ ФПВ: Б/К Р2 фВ отключен	3381.6532.507
ФПВ В1(ЛВ)/ ФПВ: Б/К Р2 фС отключен	3381.6532.508
ФПВ В1(ЛВ)/ ФПВ: Б/К Р3 включен	3381.6533.501
ФПВ В1(ЛВ)/ ФПВ: Б/К Р3 фА включен	3381.6533.502
ФПВ В1(ЛВ)/ ФПВ: Б/К Р3 фВ включен	3381.6533.503
ФПВ В1(ЛВ)/ ФПВ: Б/К Р3 фС включен	3381.6533.504
ФПВ В1(ЛВ)/ ФПВ: Б/К Р3 отключен	3381.6533.505

Входы ФСУ

ФПВ В1(ЛВ)/ ФПВ: Б/К Р3 фА отключен	3381.6533.506
ФПВ В1(ЛВ)/ ФПВ: Б/К Р3 фВ отключен	3381.6533.507
ФПВ В1(ЛВ)/ ФПВ: Б/К Р3 фС отключен	3381.6533.508
ФПВ В2(ОВ)/ ФПВ: Б/К В включен	3471.6551.501
ФПВ В2(ОВ)/ ФПВ: Б/К В фА включен	3471.6551.502
ФПВ В2(ОВ)/ ФПВ: Б/К В фВ включен	3471.6551.503
ФПВ В2(ОВ)/ ФПВ: Б/К В фС включен	3471.6551.504
ФПВ В2(ОВ)/ ФПВ: Б/К В фА отключен	3471.6551.505
ФПВ В2(ОВ)/ ФПВ: Б/К В фВ отключен	3471.6551.506
ФПВ В2(ОВ)/ ФПВ: Б/К В фС отключен	3471.6551.507
ФПВ В2(ОВ)/ ФПВ: Б/К В отключен	3471.6551.508
ФПВ В2(ОВ)/ ФПВ: Ремонт	3471.6551.509
ФПВ В2(ОВ)/ ФПВ: Б/К Р1 включен	3471.6531.501
ФПВ В2(ОВ)/ ФПВ: Б/К Р1 фА включен	3471.6531.502
ФПВ В2(ОВ)/ ФПВ: Б/К Р1 фВ включен	3471.6531.503
ФПВ В2(ОВ)/ ФПВ: Б/К Р1 фС включен	3471.6531.504
ФПВ В2(ОВ)/ ФПВ: Б/К Р1 отключен	3471.6531.505
ФПВ В2(ОВ)/ ФПВ: Б/К Р1 фА отключен	3471.6531.506
ФПВ В2(ОВ)/ ФПВ: Б/К Р1 фВ отключен	3471.6531.507
ФПВ В2(ОВ)/ ФПВ: Б/К Р1 фС отключен	3471.6531.508
ФПВ В2(ОВ)/ ФПВ: Б/К Р2 включен	3471.6532.501
ФПВ В2(ОВ)/ ФПВ: Б/К Р2 фА включен	3471.6532.502
ФПВ В2(ОВ)/ ФПВ: Б/К Р2 фВ включен	3471.6532.503
ФПВ В2(ОВ)/ ФПВ: Б/К Р2 фС включен	3471.6532.504
ФПВ В2(ОВ)/ ФПВ: Б/К Р2 отключен	3471.6532.505
ФПВ В2(ОВ)/ ФПВ: Б/К Р2 фА отключен	3471.6532.506
ФПВ В2(ОВ)/ ФПВ: Б/К Р2 фВ отключен	3471.6532.507
ФПВ В2(ОВ)/ ФПВ: Б/К Р2 фС отключен	3471.6532.508
ФПВ В2(ОВ)/ ФПВ: Б/К Р3 включен	3471.6533.501
ФПВ В2(ОВ)/ ФПВ: Б/К Р3 фА включен	3471.6533.502
ФПВ В2(ОВ)/ ФПВ: Б/К Р3 фВ включен	3471.6533.503
ФПВ В2(ОВ)/ ФПВ: Б/К Р3 фС включен	3471.6533.504
ФПВ В2(ОВ)/ ФПВ: Б/К Р3 отключен	3471.6533.505
ФПВ В2(ОВ)/ ФПВ: Б/К Р3 фА отключен	3471.6533.506
ФПВ В2(ОВ)/ ФПВ: Б/К Р3 фВ отключен	3471.6533.507
ФПВ В2(ОВ)/ ФПВ: Б/К Р3 фС отключен	3471.6533.508
ФПВ В2(ОВ)/ ФПВ: Б/К Р4 включен	3471.6543.501
ФПВ В2(ОВ)/ ФПВ: Б/К Р4 фА включен	3471.6543.502
ФПВ В2(ОВ)/ ФПВ: Б/К Р4 фВ включен	3471.6543.503
ФПВ В2(ОВ)/ ФПВ: Б/К Р4 фС включен	3471.6543.504
ФПВ В2(ОВ)/ ФПВ: Б/К Р4 отключен	3471.6543.505
ФПВ В2(ОВ)/ ФПВ: Б/К Р4 фА отключен	3471.6543.506
ФПВ В2(ОВ)/ ФПВ: Б/К Р4 фВ отключен	3471.6543.507
ФПВ В2(ОВ)/ ФПВ: Б/К Р4 фС отключен	3471.6543.508
ФПВ В3/ ФПВ: Б/К В включен	3382.6551.501
ФПВ В3/ ФПВ: Б/К В фА включен	3382.6551.502
ФПВ В3/ ФПВ: Б/К В фВ включен	3382.6551.503
ФПВ В3/ ФПВ: Б/К В фС включен	3382.6551.504
ФПВ В3/ ФПВ: Б/К В фА отключен	3382.6551.505
ФПВ В3/ ФПВ: Б/К В фВ отключен	3382.6551.506
ФПВ В3/ ФПВ: Б/К В фС отключен	3382.6551.507
ФПВ В3/ ФПВ: Б/К В отключен	3382.6551.508
ФПВ В3/ ФПВ: Ремонт	3382.6551.509
ФПВ В3/ ФПВ: Б/К Р1 включен	3382.6531.501
ФПВ В3/ ФПВ: Б/К Р1 фА включен	3382.6531.502
ФПВ В3/ ФПВ: Б/К Р1 фВ включен	3382.6531.503
ФПВ В3/ ФПВ: Б/К Р1 фС включен	3382.6531.504
ФПВ В3/ ФПВ: Б/К Р1 отключен	3382.6531.505


Входы ФСУ

ФПВ В3/ ФПВ: Б/К Р1 фА отключен	3382.6531.506
ФПВ В3/ ФПВ: Б/К Р1 фВ отключен	3382.6531.507
ФПВ В3/ ФПВ: Б/К Р1 фС отключен	3382.6531.508
ФПВ В3/ ФПВ: Б/К Р2 включен	3382.6532.501
ФПВ В3/ ФПВ: Б/К Р2 фА включен	3382.6532.502
ФПВ В3/ ФПВ: Б/К Р2 фВ включен	3382.6532.503
ФПВ В3/ ФПВ: Б/К Р2 фС включен	3382.6532.504
ФПВ В3/ ФПВ: Б/К Р2 отключен	3382.6532.505
ФПВ В3/ ФПВ: Б/К Р2 фА отключен	3382.6532.506
ФПВ В3/ ФПВ: Б/К Р2 фВ отключен	3382.6532.507
ФПВ В3/ ФПВ: Б/К Р2 фС отключен	3382.6532.508
ФПВ В3/ ФПВ: Б/К Р3 включен	3382.6533.501
ФПВ В3/ ФПВ: Б/К Р3 фА включен	3382.6533.502
ФПВ В3/ ФПВ: Б/К Р3 фВ включен	3382.6533.503
ФПВ В3/ ФПВ: Б/К Р3 фС включен	3382.6533.504
ФПВ В3/ ФПВ: Б/К Р3 отключен	3382.6533.505
ФПВ В3/ ФПВ: Б/К Р3 фА отключен	3382.6533.506
ФПВ В3/ ФПВ: Б/К Р3 фВ отключен	3382.6533.507
ФПВ В3/ ФПВ: Б/К Р3 фС отключен	3382.6533.508
ЗНР:	0221.0881.501
ЗНФ В1	0221.0881.502
ЗНР:	
ЗНФ В2	0221.0881.503
ЗНР:	
В3 отключен	502
Контр. ЭМО1	503
Контр. ЭМО1 ф.А	504
Контр. ЭМО1 ф.В	505
Контр. ЭМО1 ф.С	506
Контр. ЭМВ	507
Контр. ЭМВ ф.А	508
Контр. ЭМВ ф.С	509
Контр. ЭМО2	510
Контр. ЭМО2 ф.А	511
Контр. ЭМО2 ф.В	512
Контр. ЭМО2 ф.С	513
КСВ/ Контроль В: Неистр. обогр.	3071.6861.501
КСВ/ Контроль В: Автомат ШП	3071.6861.502
КСВ/ Контроль В: Низк. давл. SF6	3071.6861.503
КСВ/ Контроль В: Низк. давл. SF6 ф.А	3071.6861.504
КСВ/ Контроль В: Низк. давл. SF6 ф.В	3071.6861.505
КСВ/ Контроль В: Низк. давл. SF6 ф.С	3071.6861.506
КСВ/ Контроль В: Авар. давл. SF6	3071.6861.507
КСВ/ Контроль В: Авар. давл. SF6 ф.А	3071.6861.508
КСВ/ Контроль В: Авар. давл. SF6 ф.В	3071.6861.509
КСВ/ Контроль В: Авар. давл. SF6 ф.С	3071.6861.510
КСВ/ Контроль В: Пруж. не заведены	3071.6861.511
КСВ/ Контроль В: Пруж. не заведены ф.А	3071.6861.512
КСВ/ Контроль В: Пруж. не заведены ф.В	3071.6861.513
КСВ/ Контроль В: Пруж. не заведены ф.С	3071.6861.514
КСВ/ Контроль В: Контр. ОТ ЭМВ/ЭМО1	3071.6861.515
КСВ/ Контроль В: Контр. ОТ ЭМО2	3071.6861.516
КСВ/ Контроль ТТ Низк. давл. SF6 ТТ	3071.6581.501
КСВ/ Контроль ТТ Низк. давл. SF6 ТТ ф.А	3071.6581.502
КСВ/ Контроль ТТ Низк. давл. SF6 ТТ ф.В	3071.6581.503
КСВ/ Контроль ТТ Низк. давл. SF6 ТТ ф.С	3071.6581.504
КСВ/ Контроль ТТ Авар. давл. SF6 ТТ	3071.6581.505
КСВ/ Контроль ТТ Авар. давл. SF6 ТТ ф.А	3071.6581.506
КСВ/ Контроль ТТ Авар. давл. SF6 ТТ ф.В	3071.6581.507
КСВ/ Контроль ТТ Авар. давл. SF6 ТТ ф.С	3071.6581.508


Входы ФСУ

КСВ/ Контроль ТТ Неистр. обогр. ТТ	3071.6581.509
Работа ЭМВ	514
Работа ЭМВ ф.А	515
Работа ЭМВ ф.В	516
Работа ЭМВ ф.С	517
Работа ЭМО1	518
Работа ЭМО1 ф.А	519
Работа ЭМО1 ф.В	520
Работа ЭМО1 ф.С	521
Работа ЭМО2	522
Работа ЭМО2 ф.А	523
Работа ЭМО2 ф.В	524
Работа ЭМО2 ф.С	525
БКУ/ БКУ : Ком. опер. вкл.	3431.6661.501
БКУ/ БКУ : Ком. опер. откл.	3431.6661.502
БКУ/ БКУ : Ком. вкл. СКРМ	3432.6661.501
БКУ/ БКУ Ав.СКРМ: Ком. откл.	3432.6661.502
КСВ/ Блокировка управления: Внеш. блок. вкл.	3071.6901.502
КСВ/ Блокировка управления: Авар. давл. SF6	3071.6901.503
КСВ/ Блокировка управления: Внеш. блок. упр.	3071.6901.504
КСВ/ Блокировка управления: Пруж. не заведены ф.А	3071.6901.505
КСВ/ Блокировка управления: Внеш. блок. вкл. ф.А	3071.6901.506
КСВ/ Блокировка управления: Авар. давл. SF6 ф.А	3071.6901.507
КСВ/ Блокировка управления: Внеш. блок. упр. ф.А	3071.6901.508
КСВ/ Блокировка управления: Пруж. не заведены ф.В	3071.6901.509
КСВ/ Блокировка управления: Внеш. блок. вкл. ф.В	3071.6901.510
КСВ/ Блокировка управления: Авар. давл. SF6 ф.В	3071.6901.511
КСВ/ Блокировка управления: Внеш. блок. упр. ф.В	3071.6901.512
КСВ/ Блокировка управления: Пруж. не заведены ф.С	3071.6901.513
КСВ/ Блокировка управления: Внеш. блок. вкл. ф.С	3071.6901.514
КСВ/ Блокировка управления: Авар. давл. SF6 ф.С	3071.6901.515
КСВ/ Блокировка управления: Внеш. блок. упр. ф.С	3071.6901.516
КСВ: Ср. РЗ КР	3071.501
КСВ: Разр. вкл. САУ	3071.503
УВ УПНКП/ УВ УПНКП: Ср. РЗ ЛЭП	3081.6911.502
УВ/ УВ: Ср. РЗ ЛЭП	3091.6921.502
УВ/ УВ: Ср. РЗ КР	3091.6921.504
Вкл. АПВ	526
	527


Блоки управления функциями

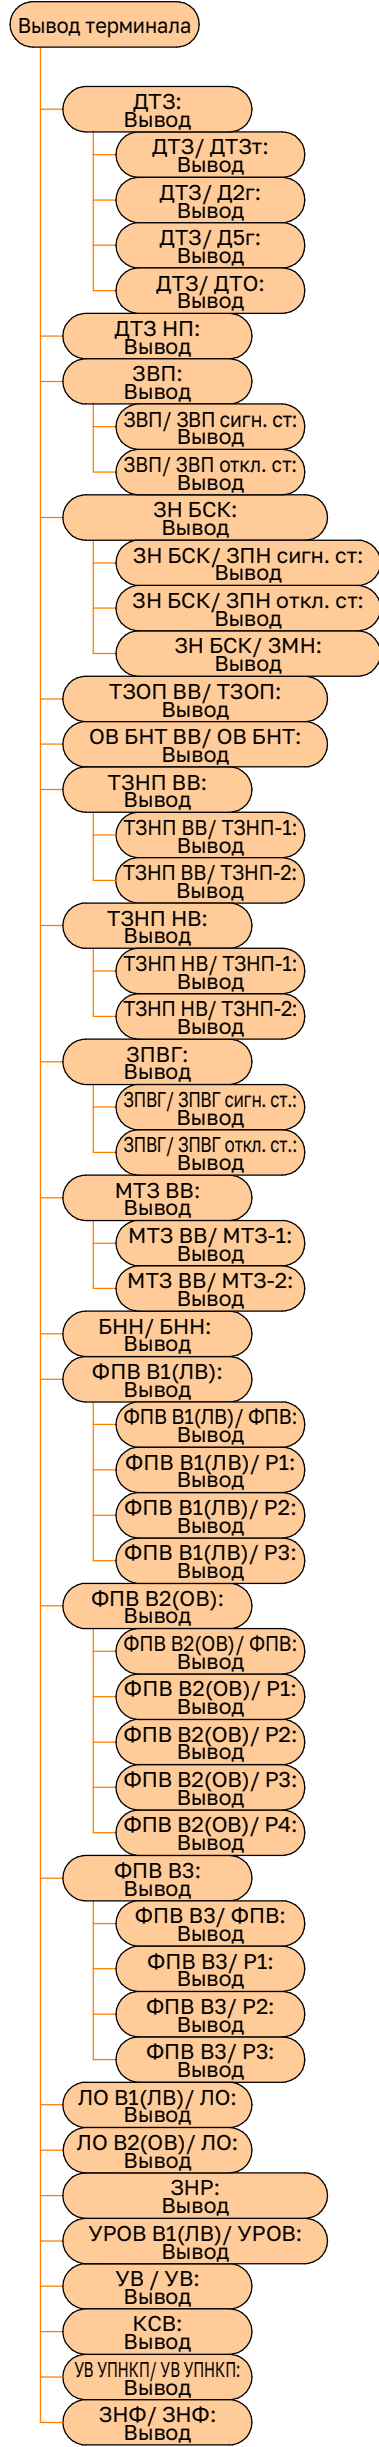

Общая логика (90)

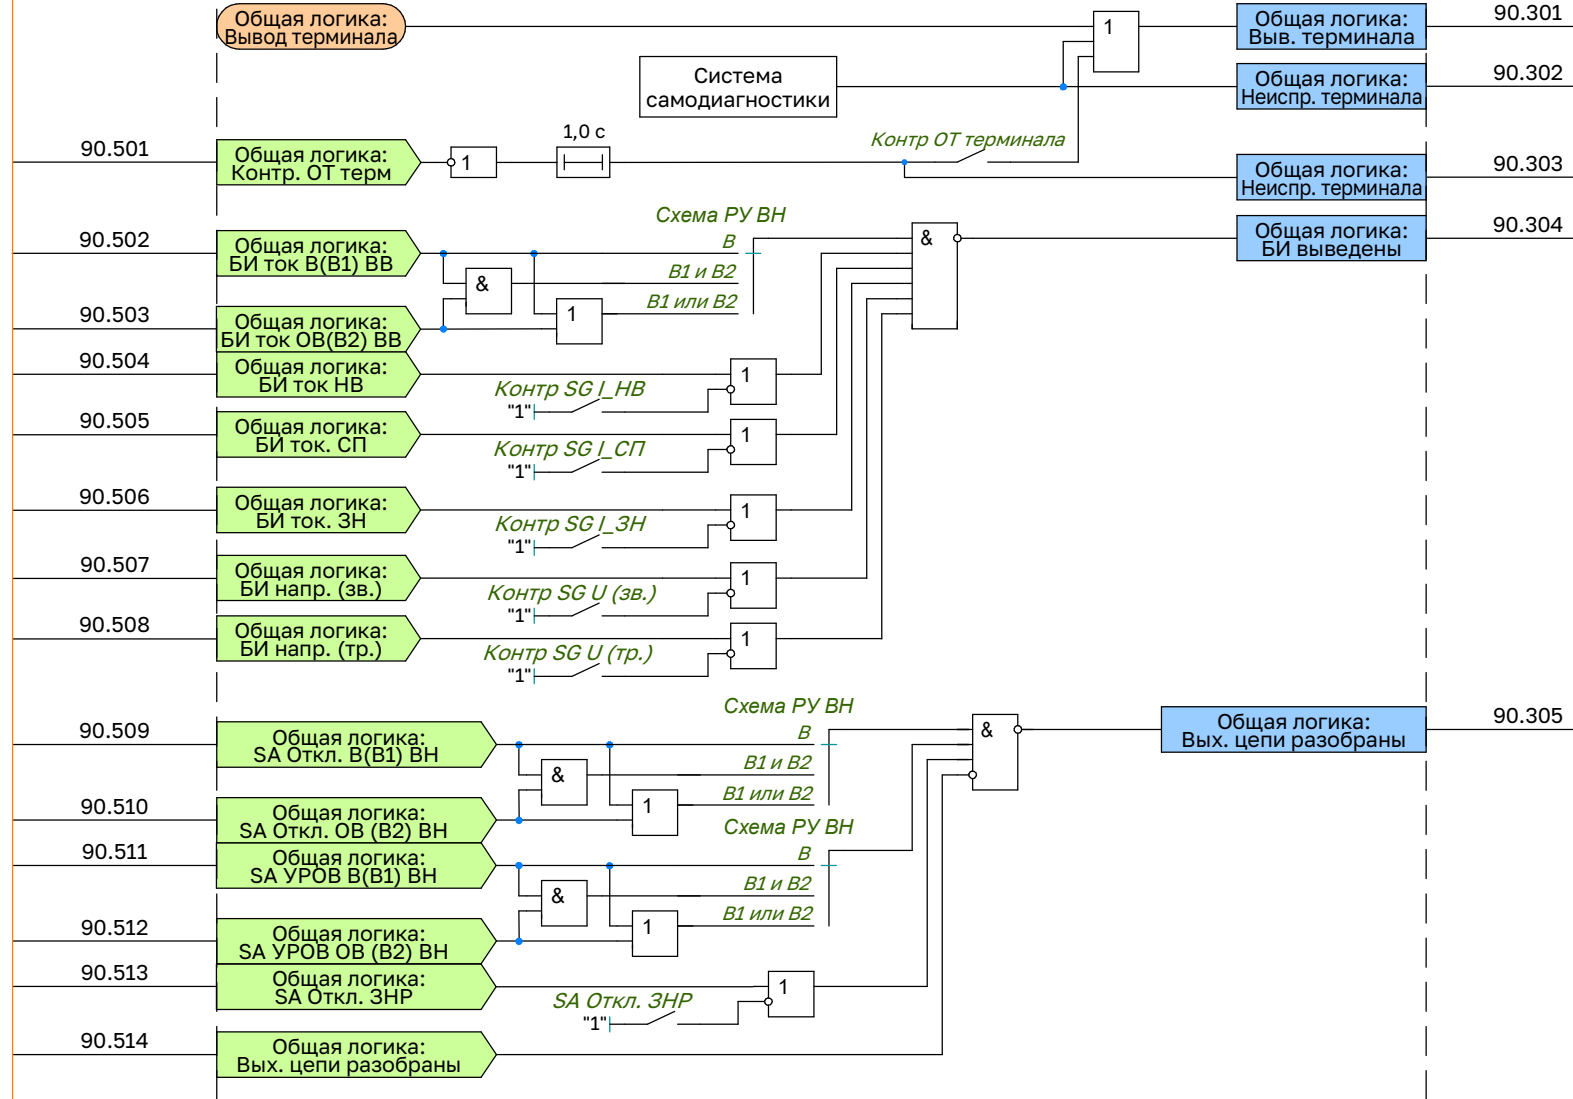


Сигнализации 91

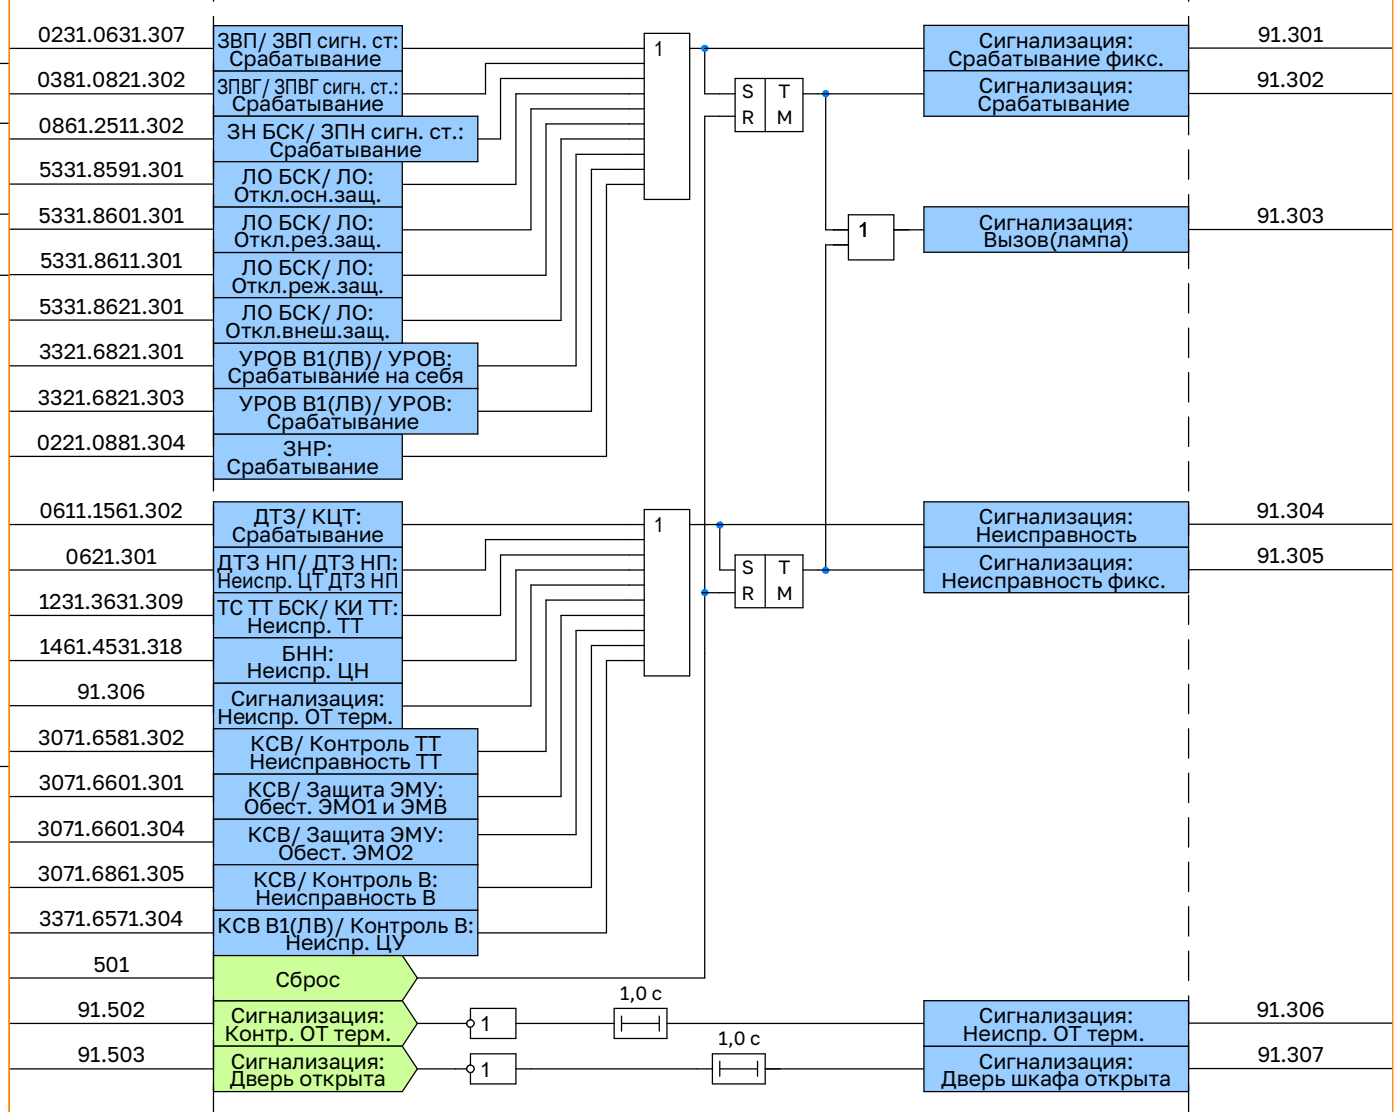


ДТЗ 0611


ДТЗт 1521

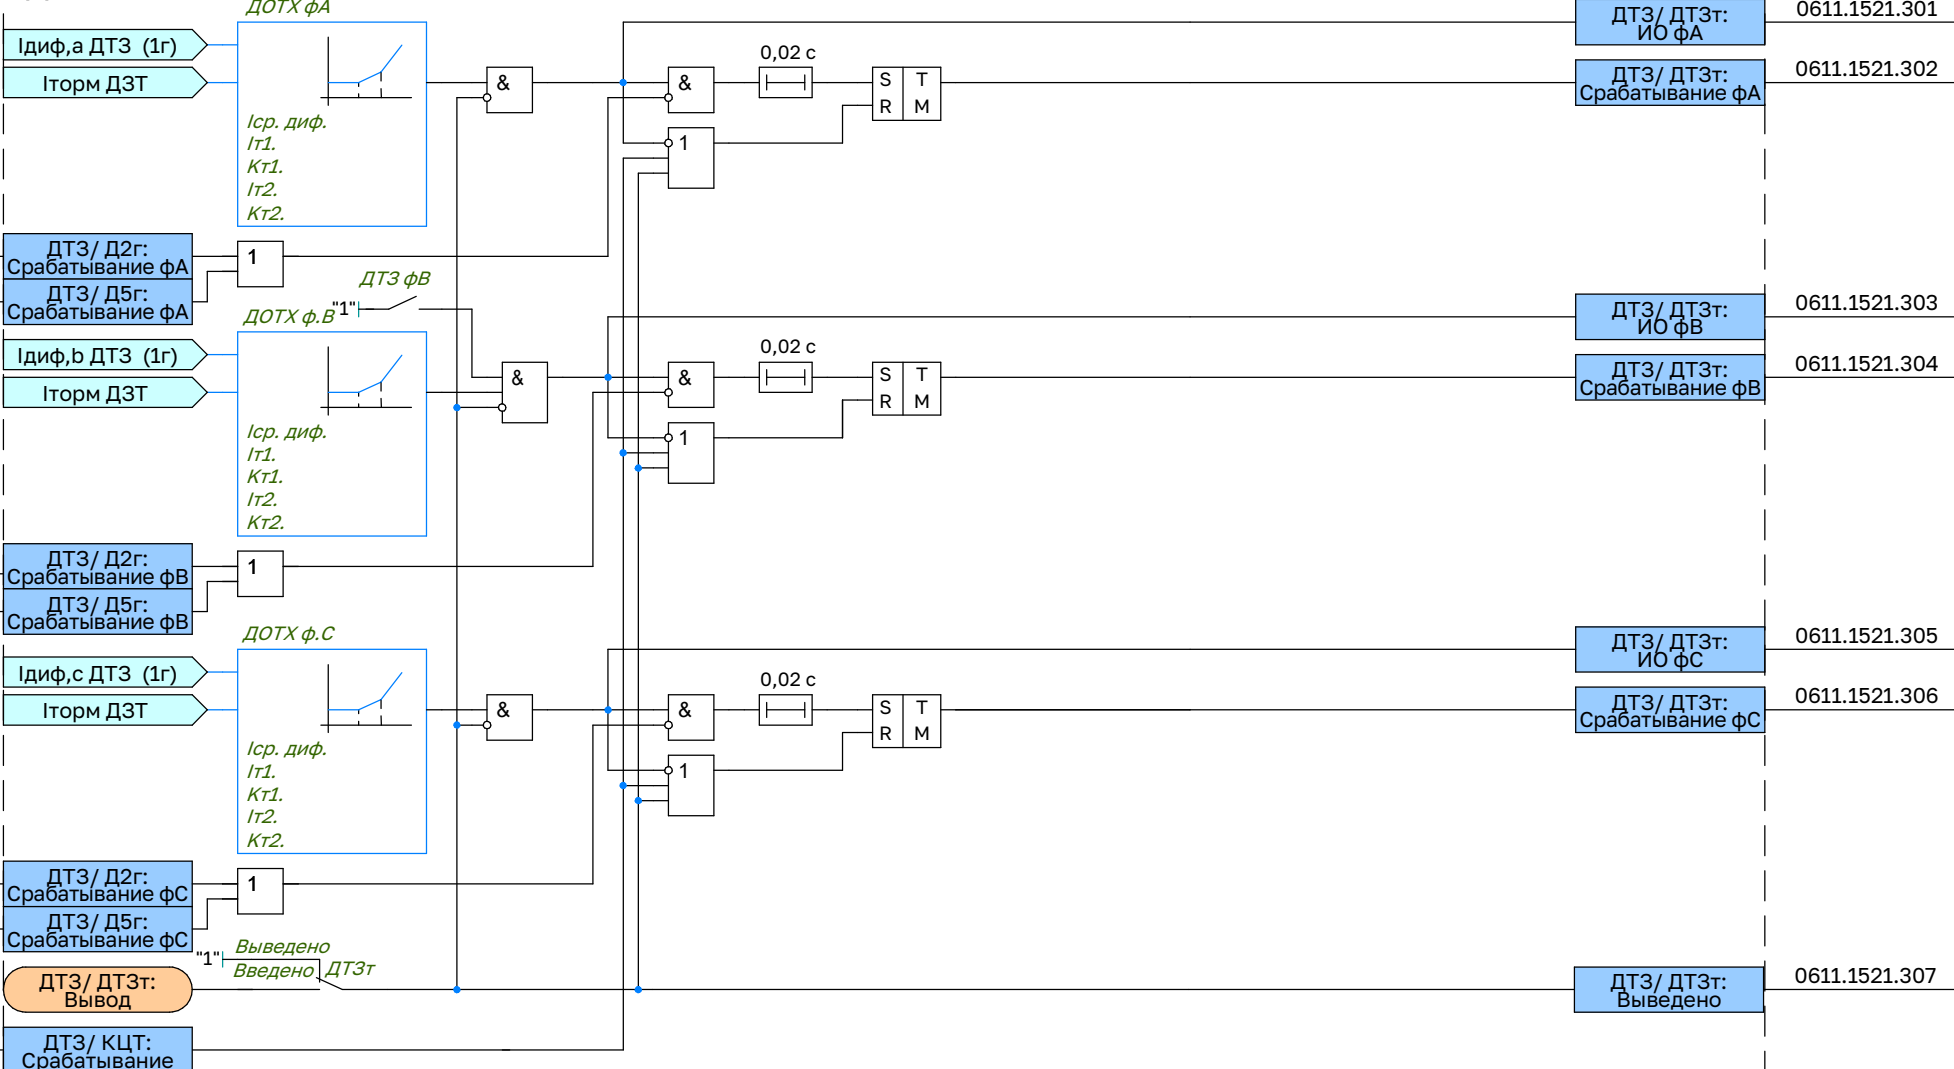

Д2г 1541

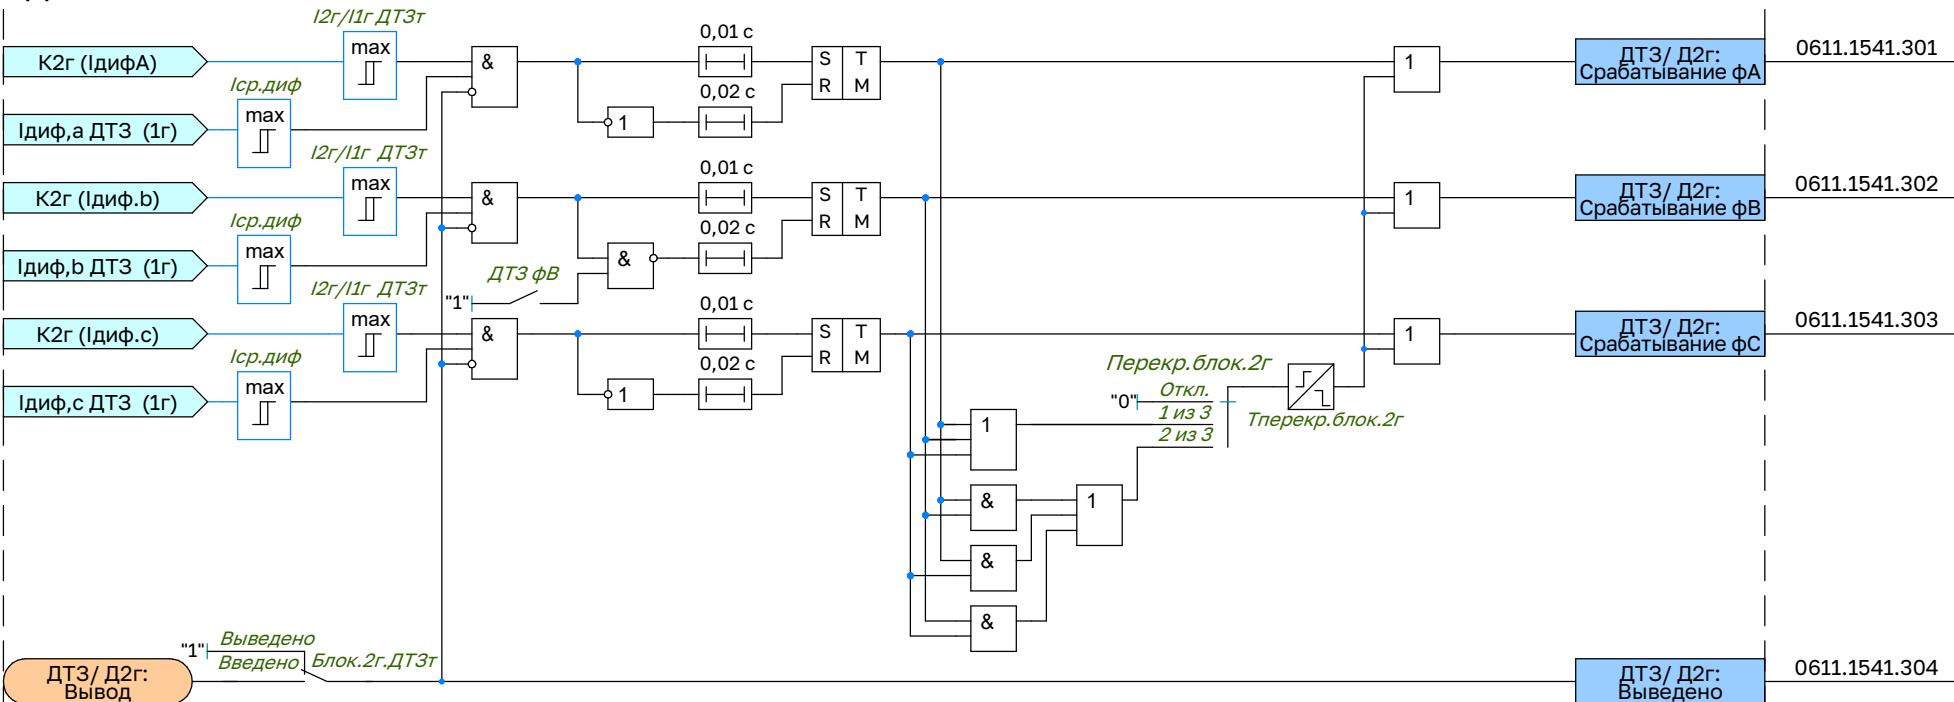


Д5г 1542

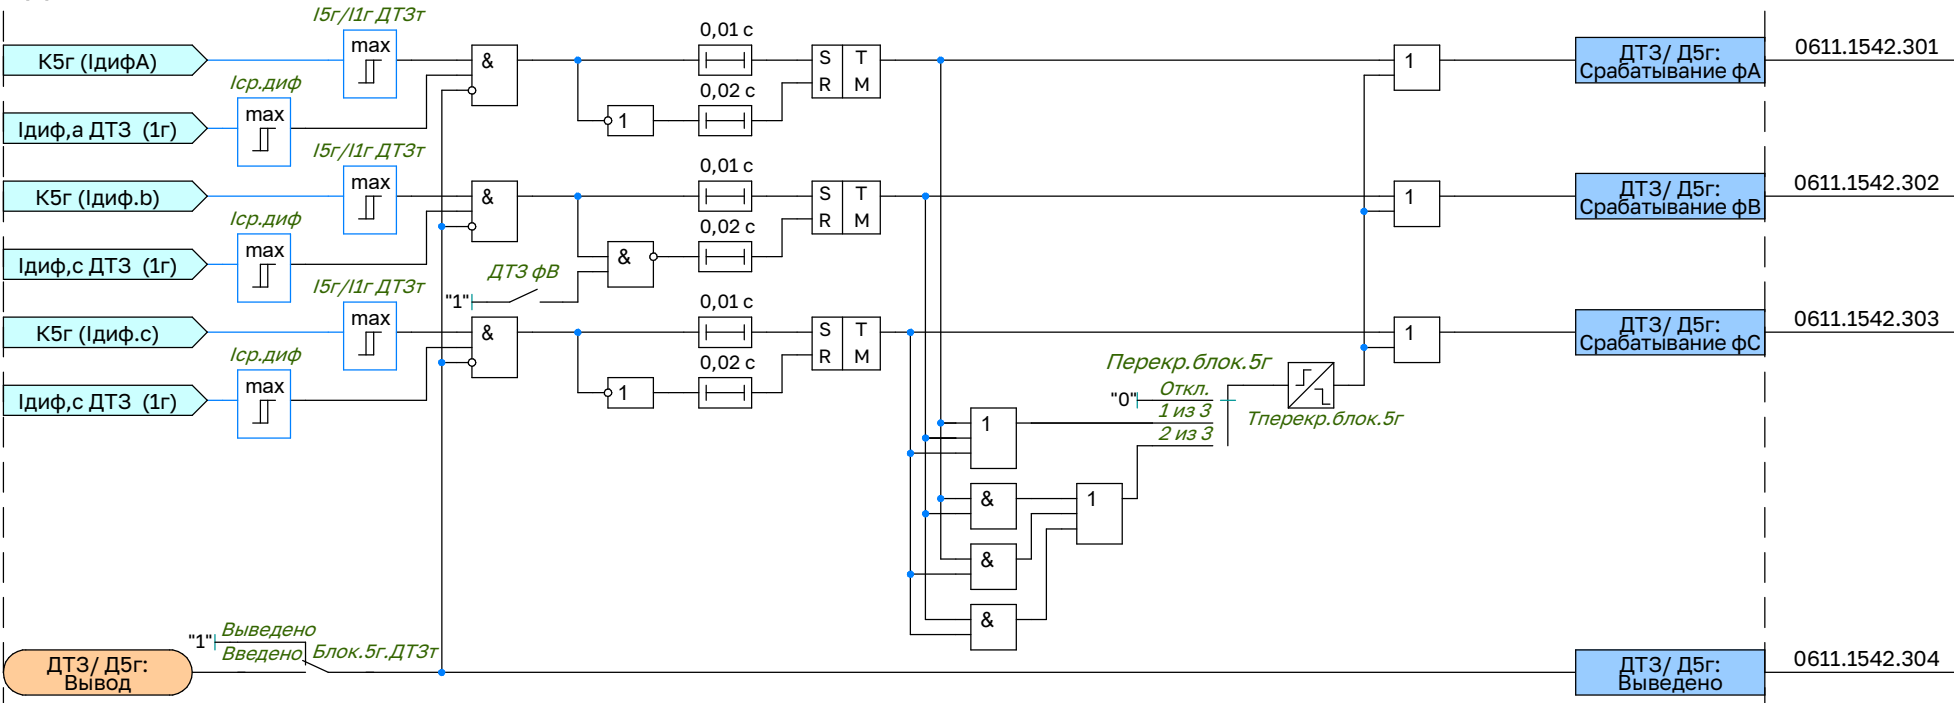


ДТЗ 0611

ДТО 1511

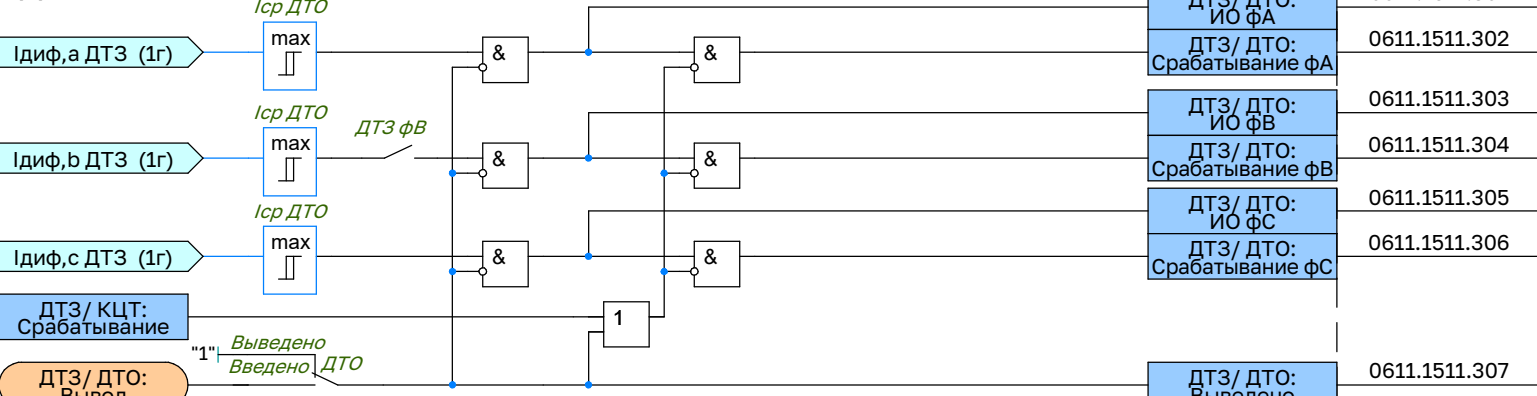


КЦТ 1561

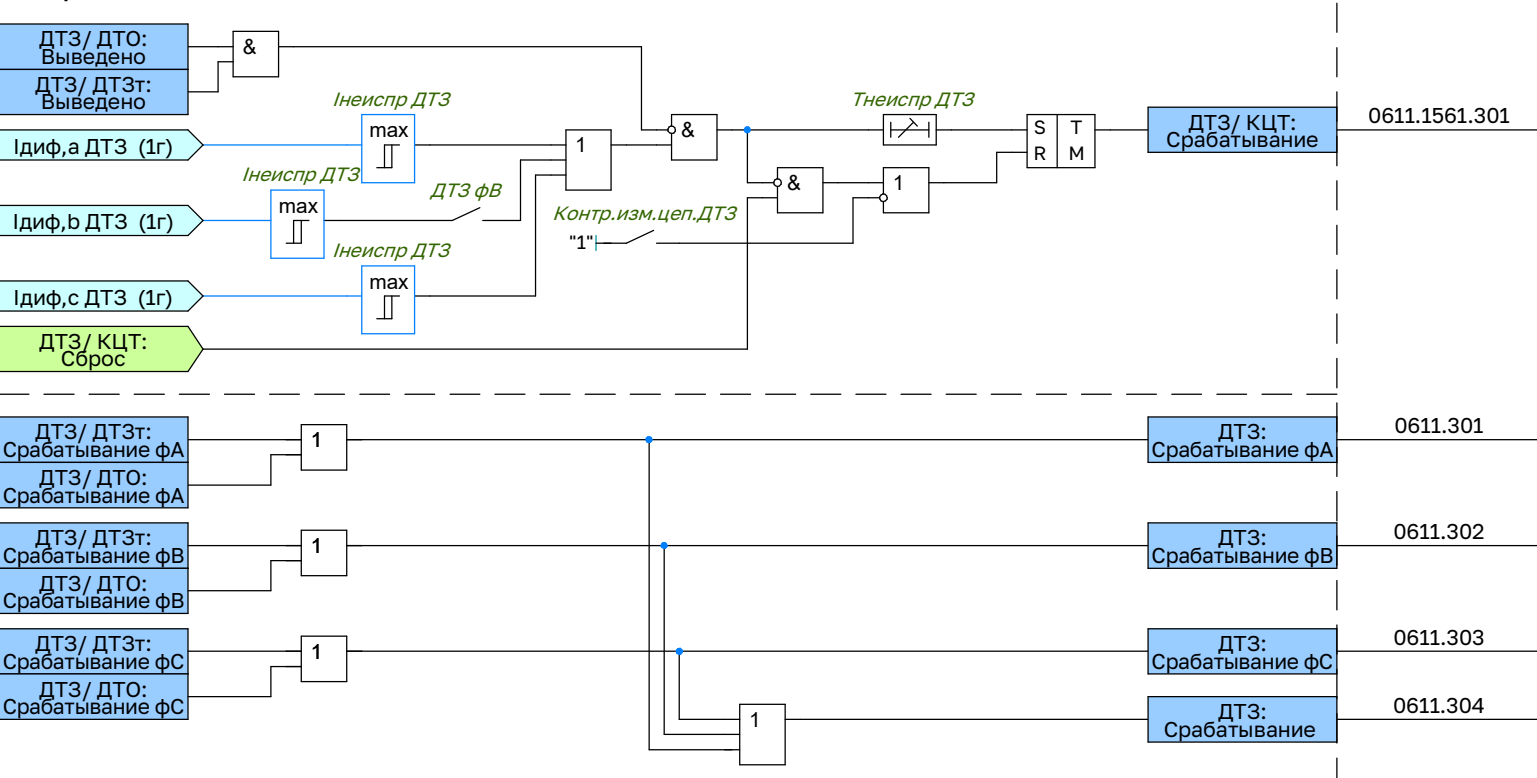


ДТЗ НП 0621

ДТЗ НП 1631

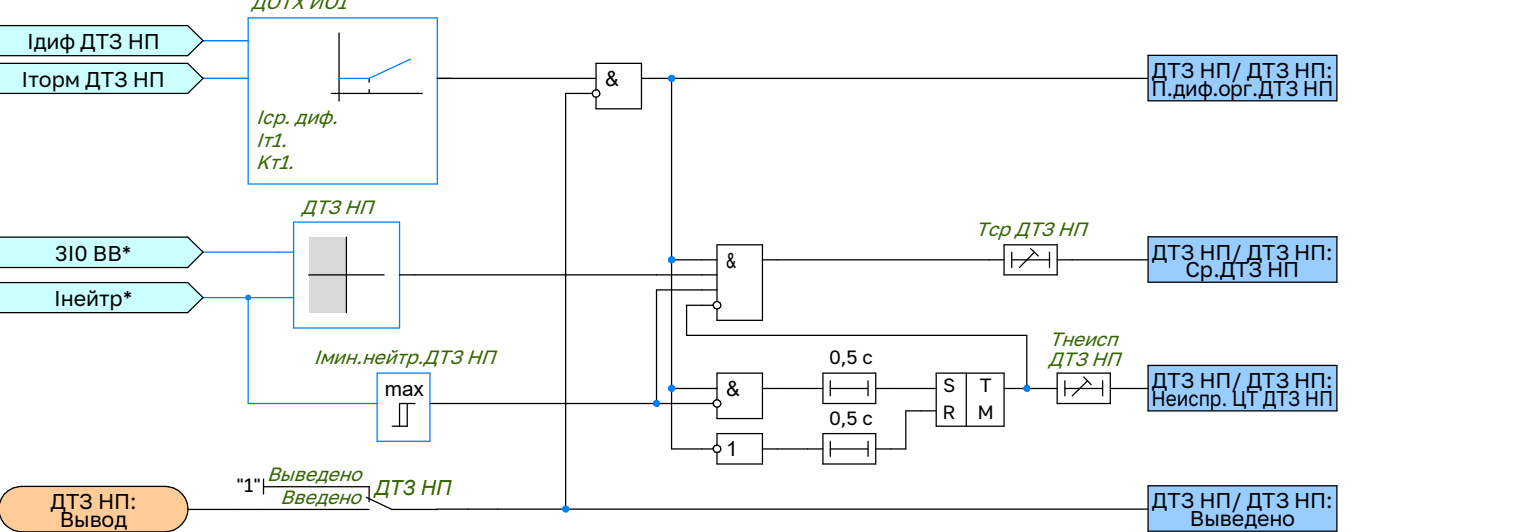


ЗВП (Защита от внутренних повреждений) 0231

ЗВП сигн. ст. (Защита от внутренних повреждений сигнальная ступень) 0631

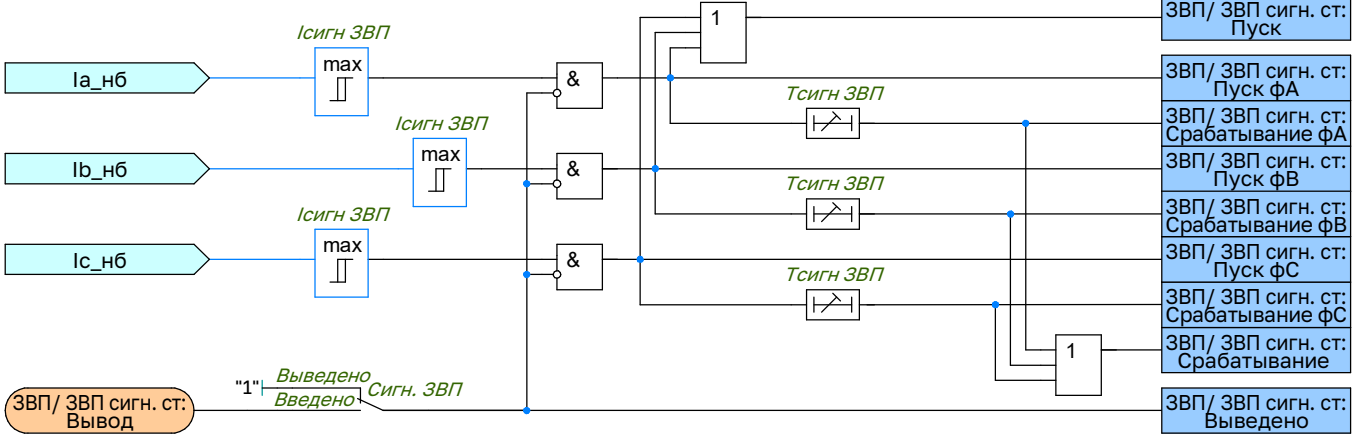


ЗВП откл. ст. (Защита от внутренних повреждений отключающая ступень) 0632

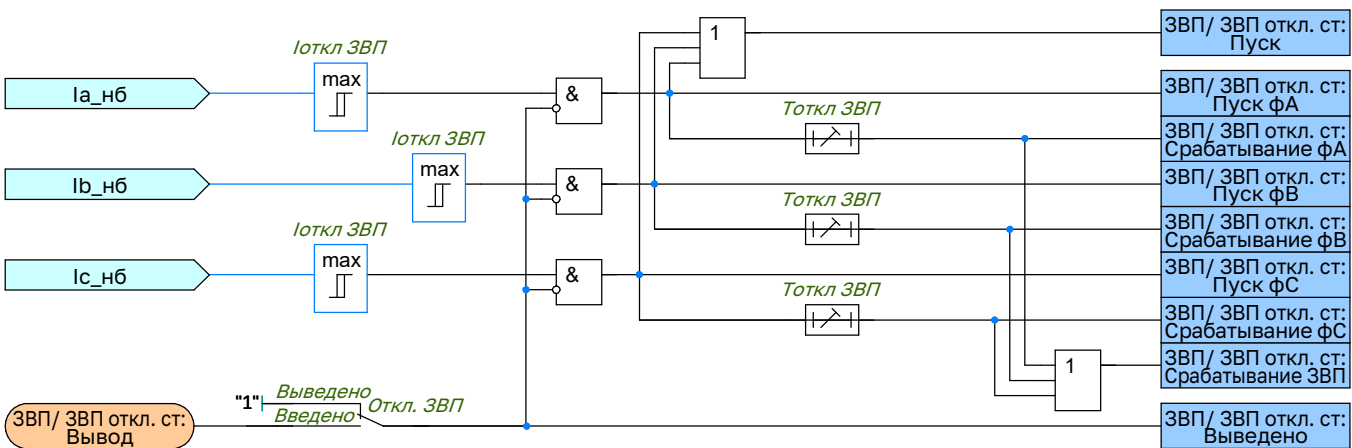


ЗН БСК (Защиты по напряжению БСК) 0861


ЗПН сигн. ст. (Защита от повышения напряжения сигнальная ступень) 2511

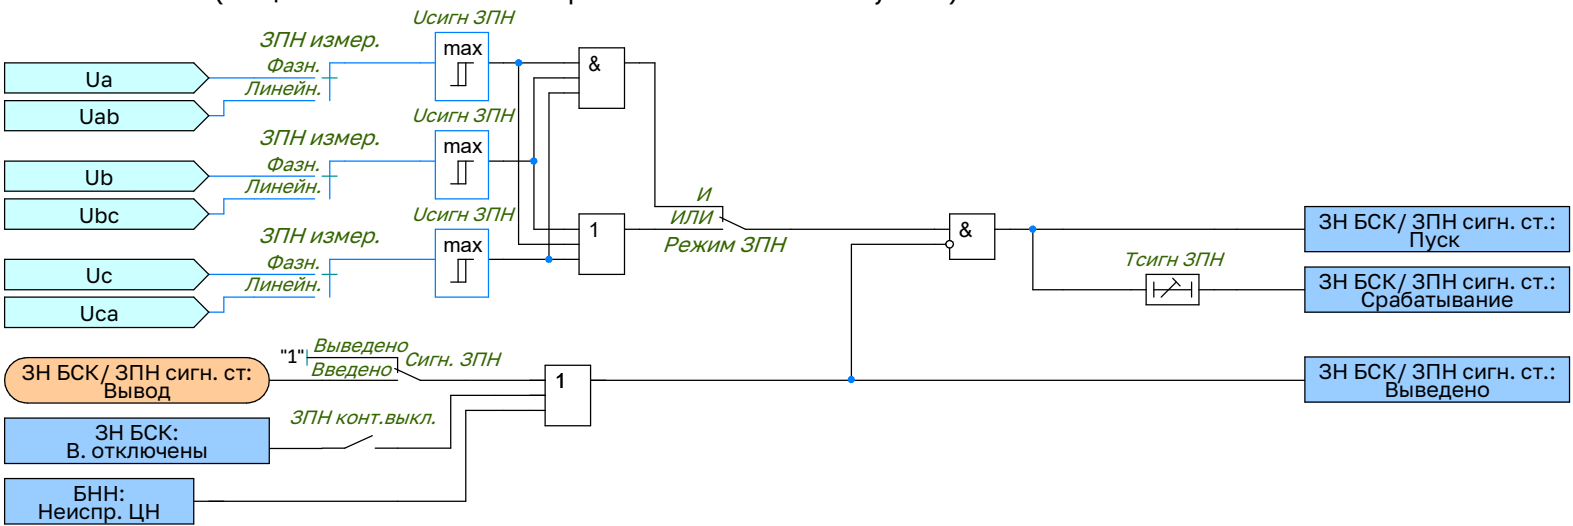

ЗПН откл. ст. (Защита от повышения напряжения отключающая ступень) 2512

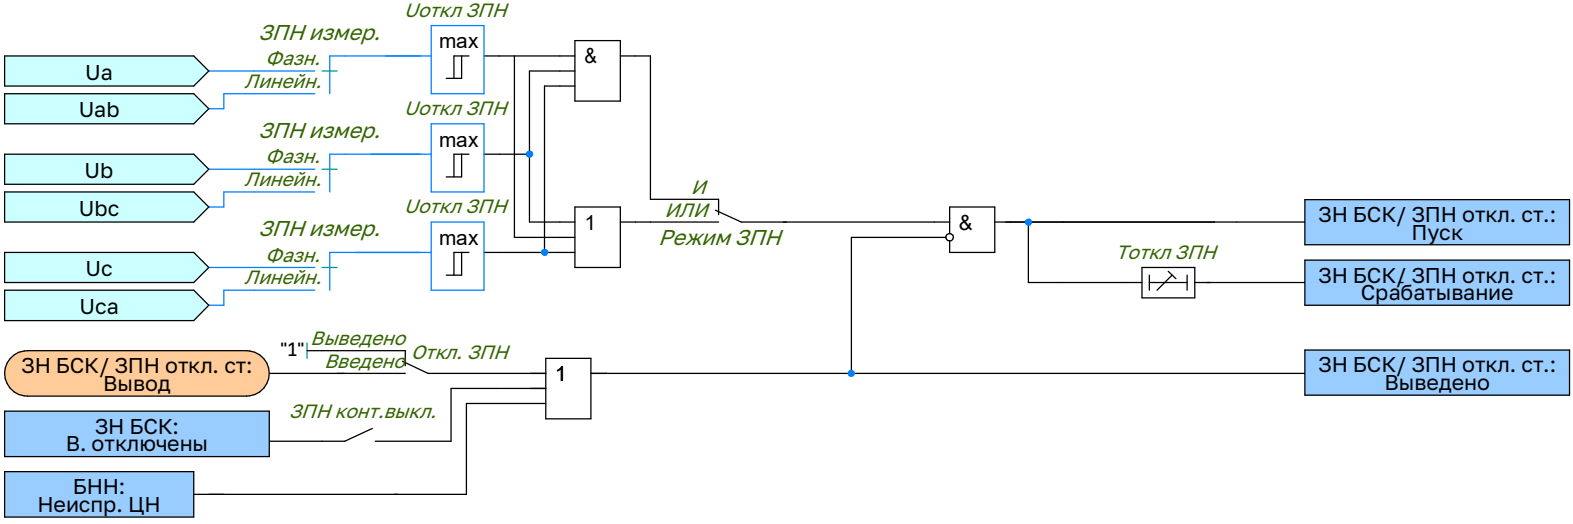


ЗМН (Защита минимального напряжения) 2521

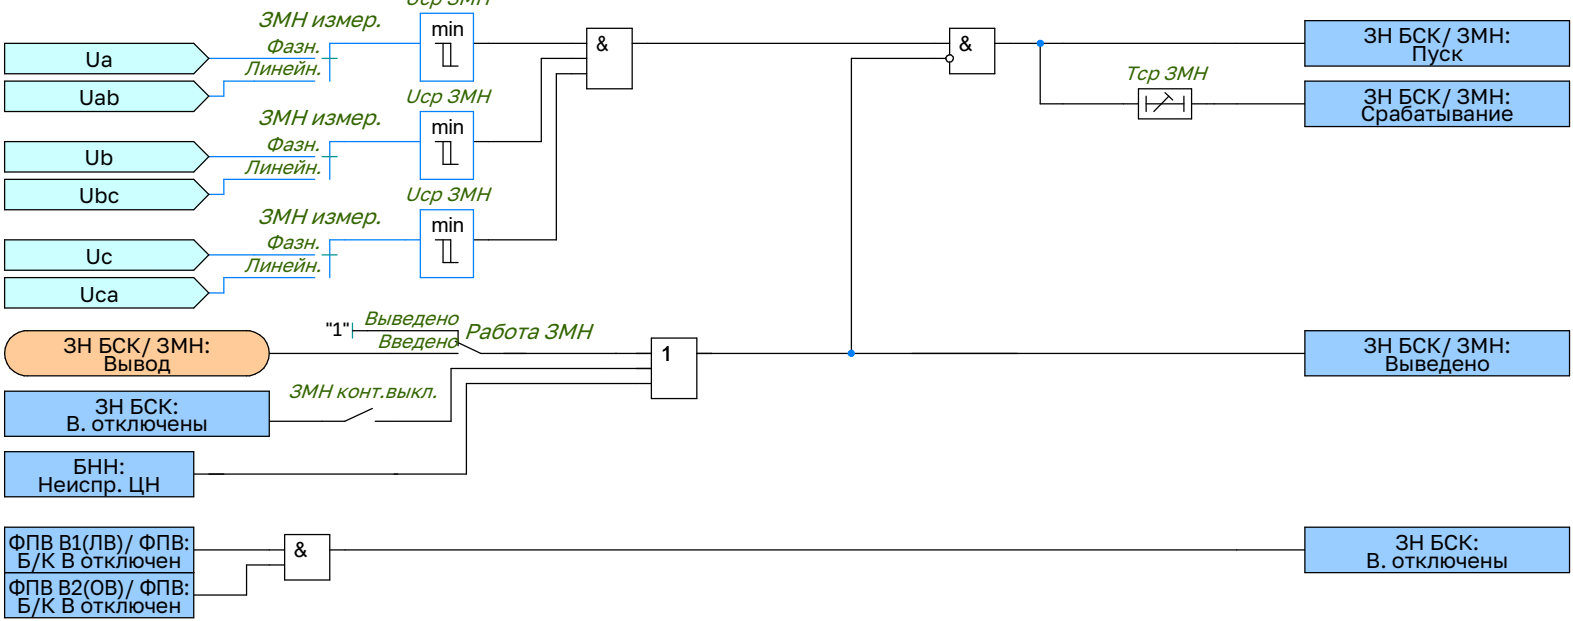


ТЗОП ВВ 0291

ТЗОП 0611

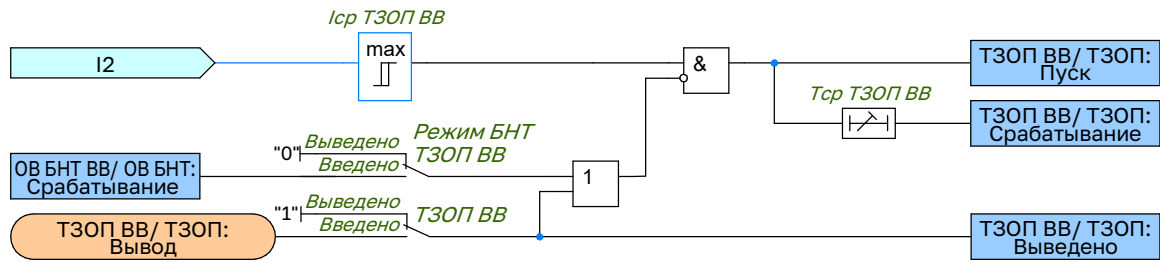


ОВ БНТ ВВ 0391

ОВ БНТ 0791

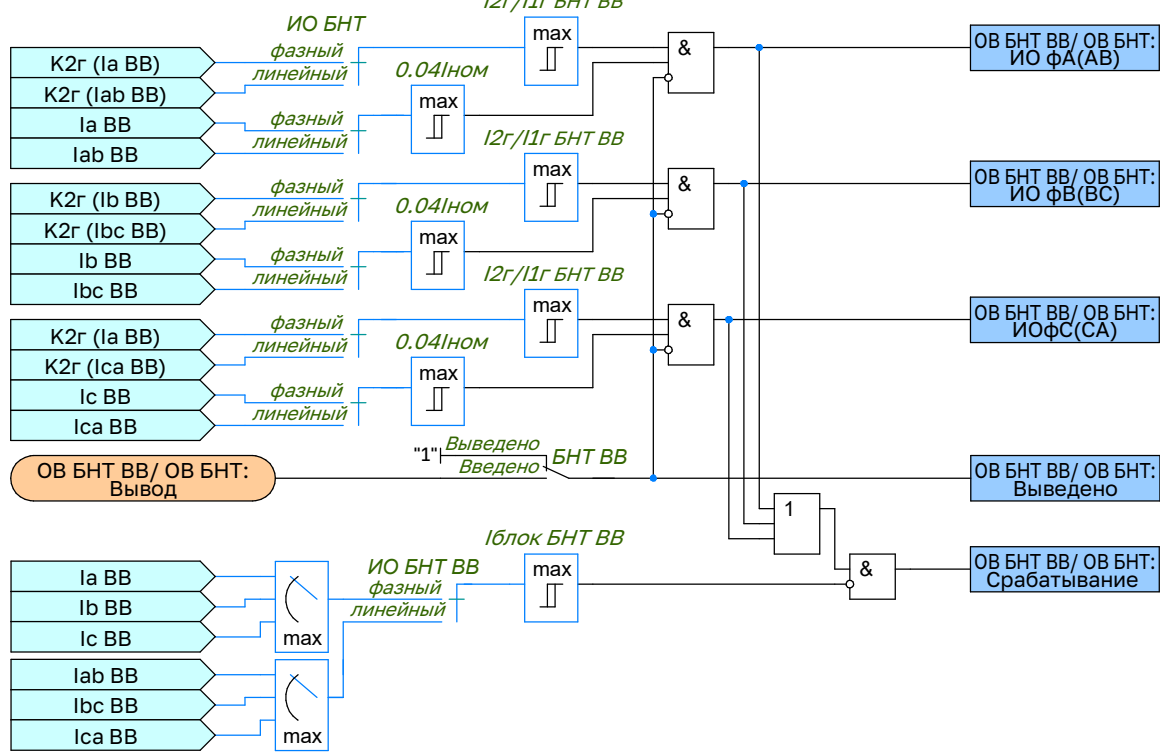


ТЗНП ВВ 0241

ТЗНП - 1 0571

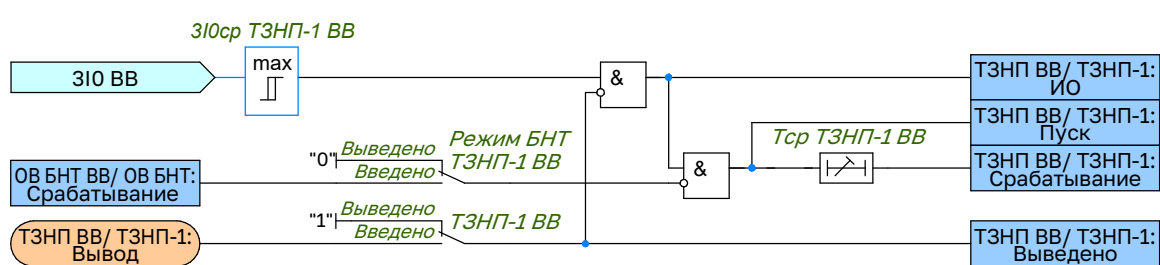


ТЗНП - 2 0572

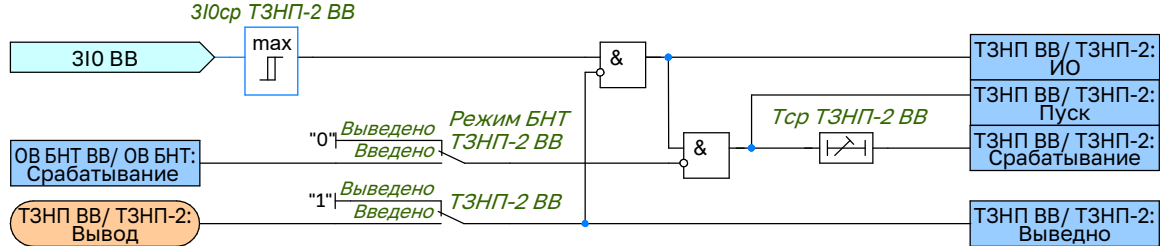


ТЗНП НВ 0251

ТЗНП - 1 0581

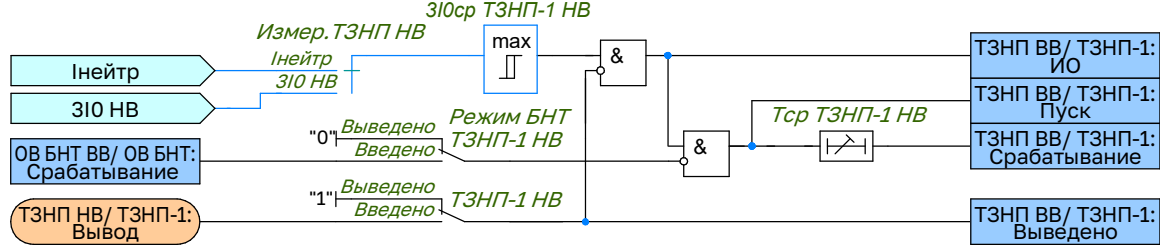


ТЗНП - 2 0582

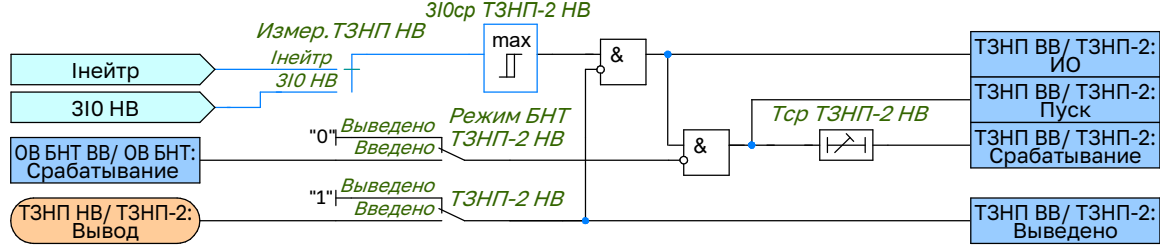


ЗПВГ (защита от перегрузки токами высших гармонических составляющих) 0381

ЗПВГ сигн. ст. (ЗПВГ сигнальная ступень) 0821

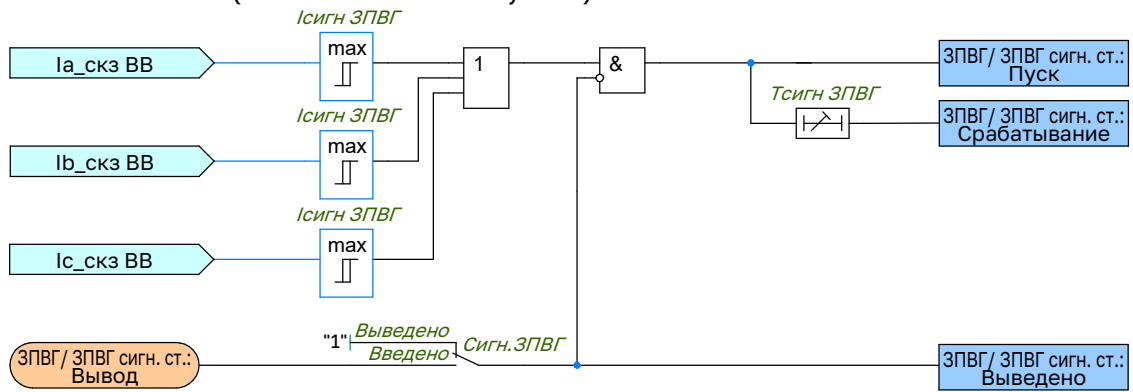


ЗПВГ откл. ст. (ЗПВГ отключающая ступень) 0822

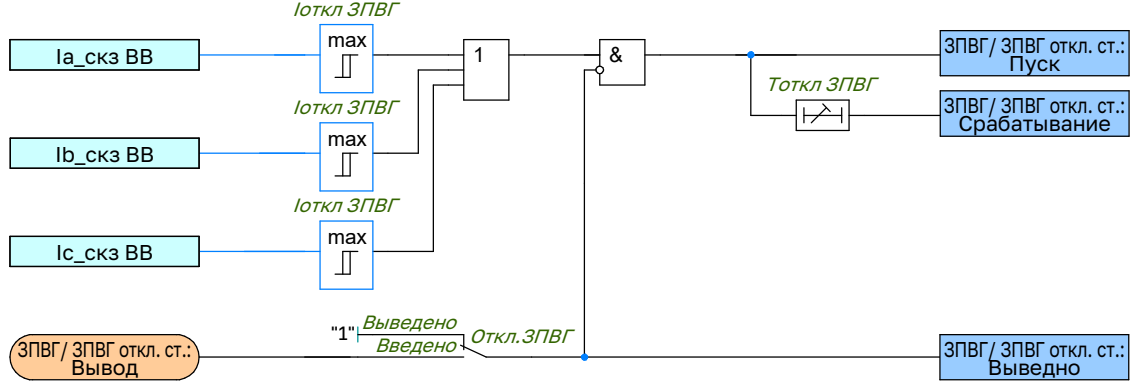


МТЗ ВВ 0281

МТЗ - 1 0521

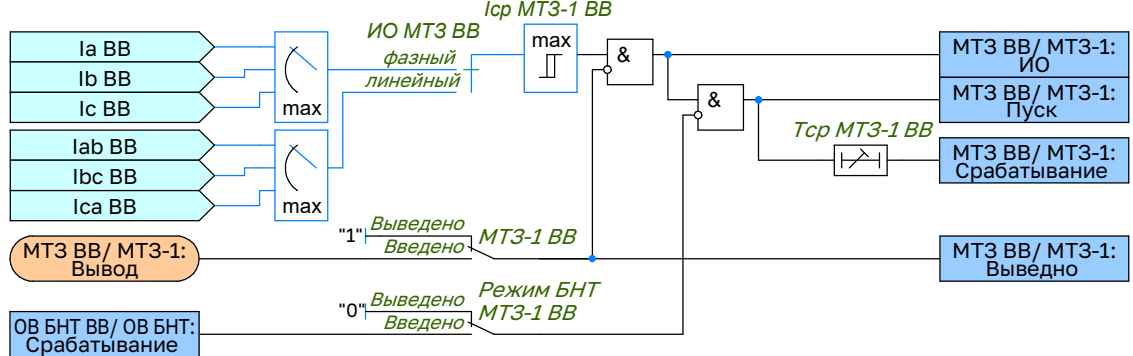


МТЗ - 2 0522

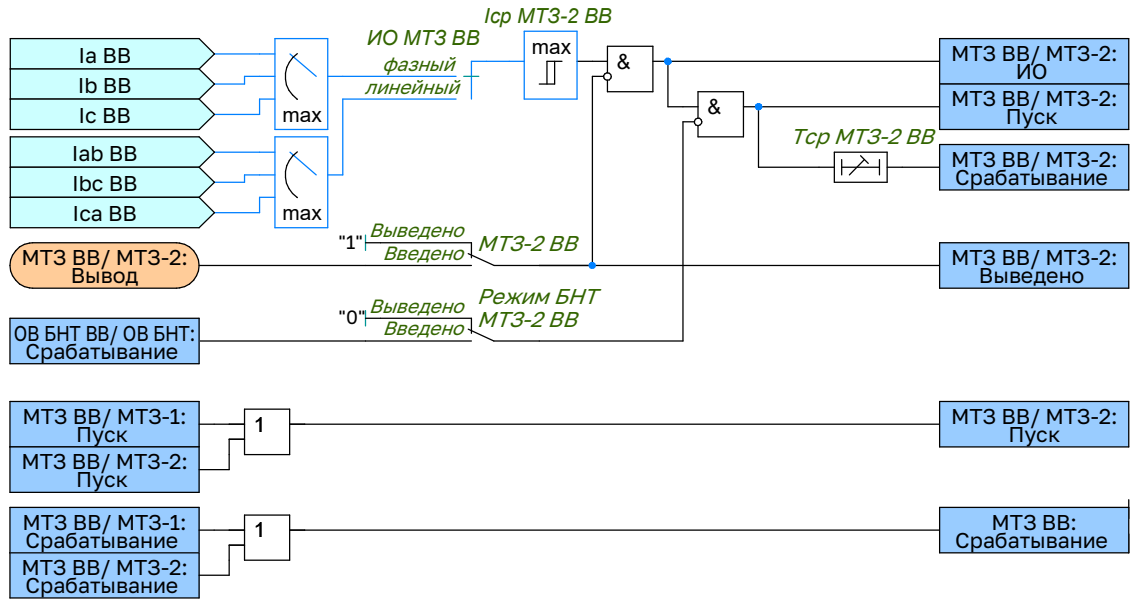


БНН 1511

БНН 4531

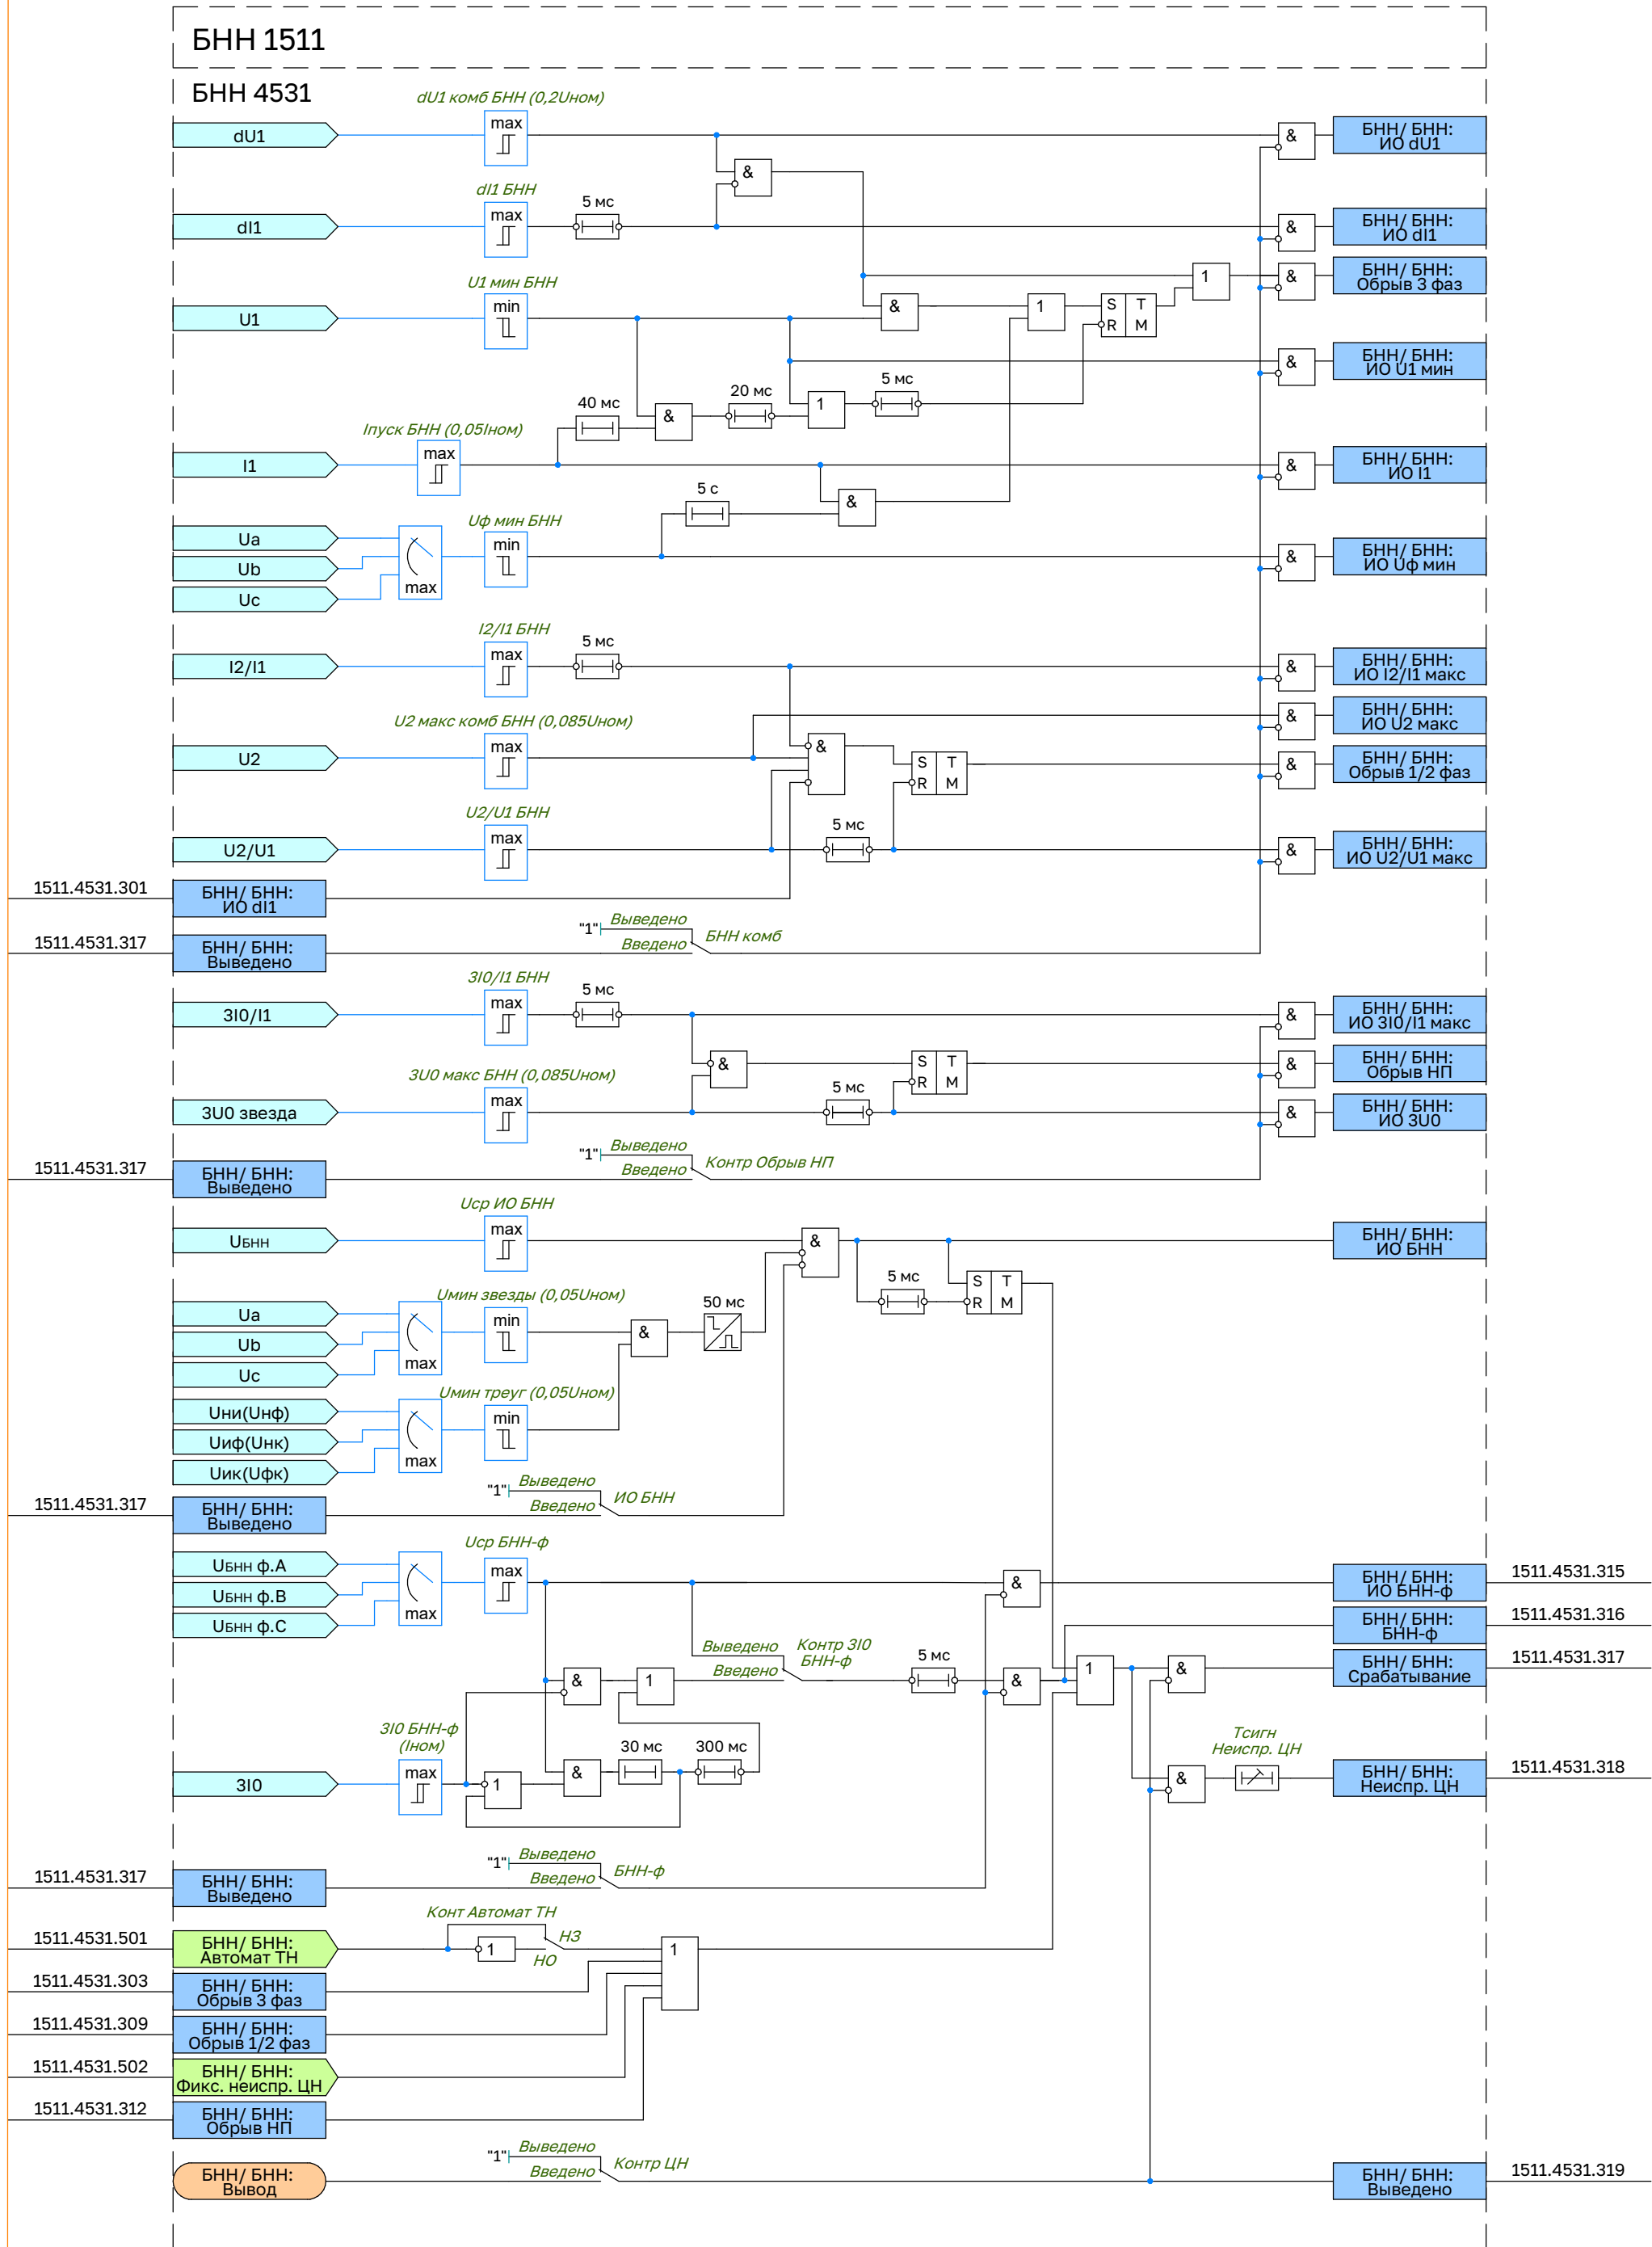


УРОВ В1(ЛВ) 3321

УРОВ 6821

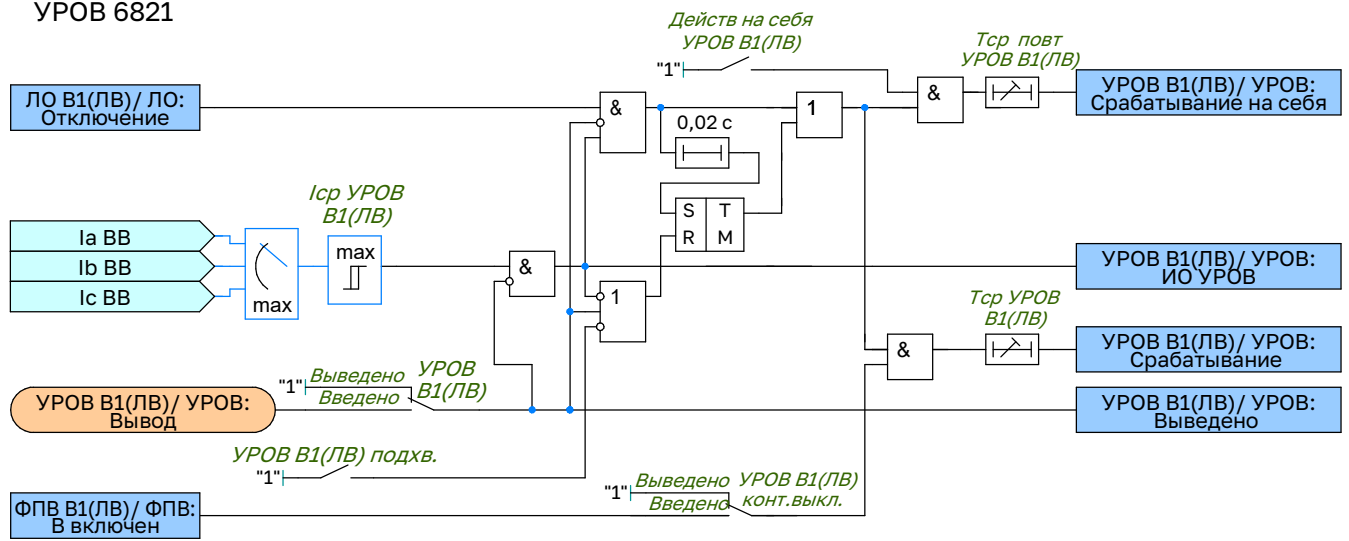


ЗНФ ВН 3541


ЗНФ 6701

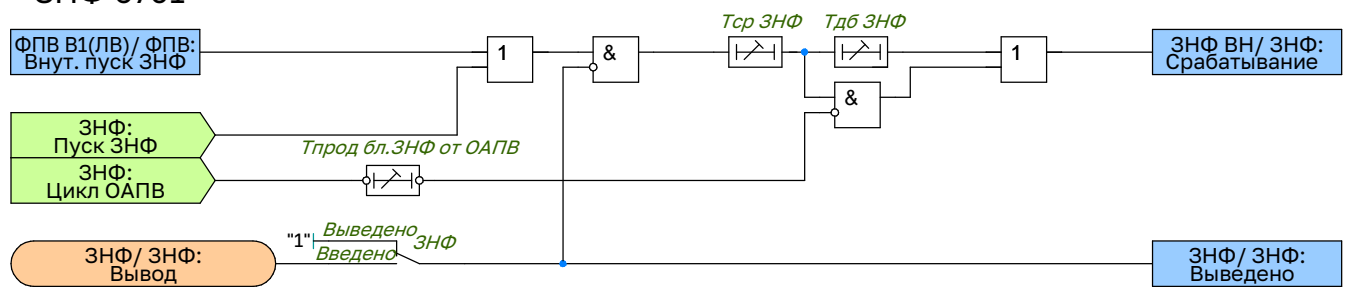


ТС ТТ БСК (Технологическая сигнализация ТТ БСК) 1231

КИ ТТ (Контроль изоляции ТТ) 3631

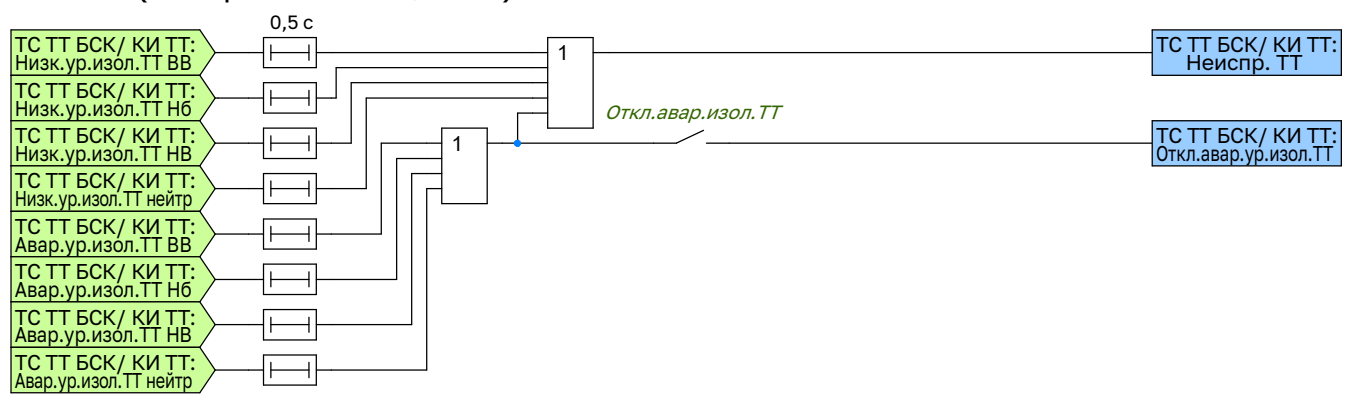


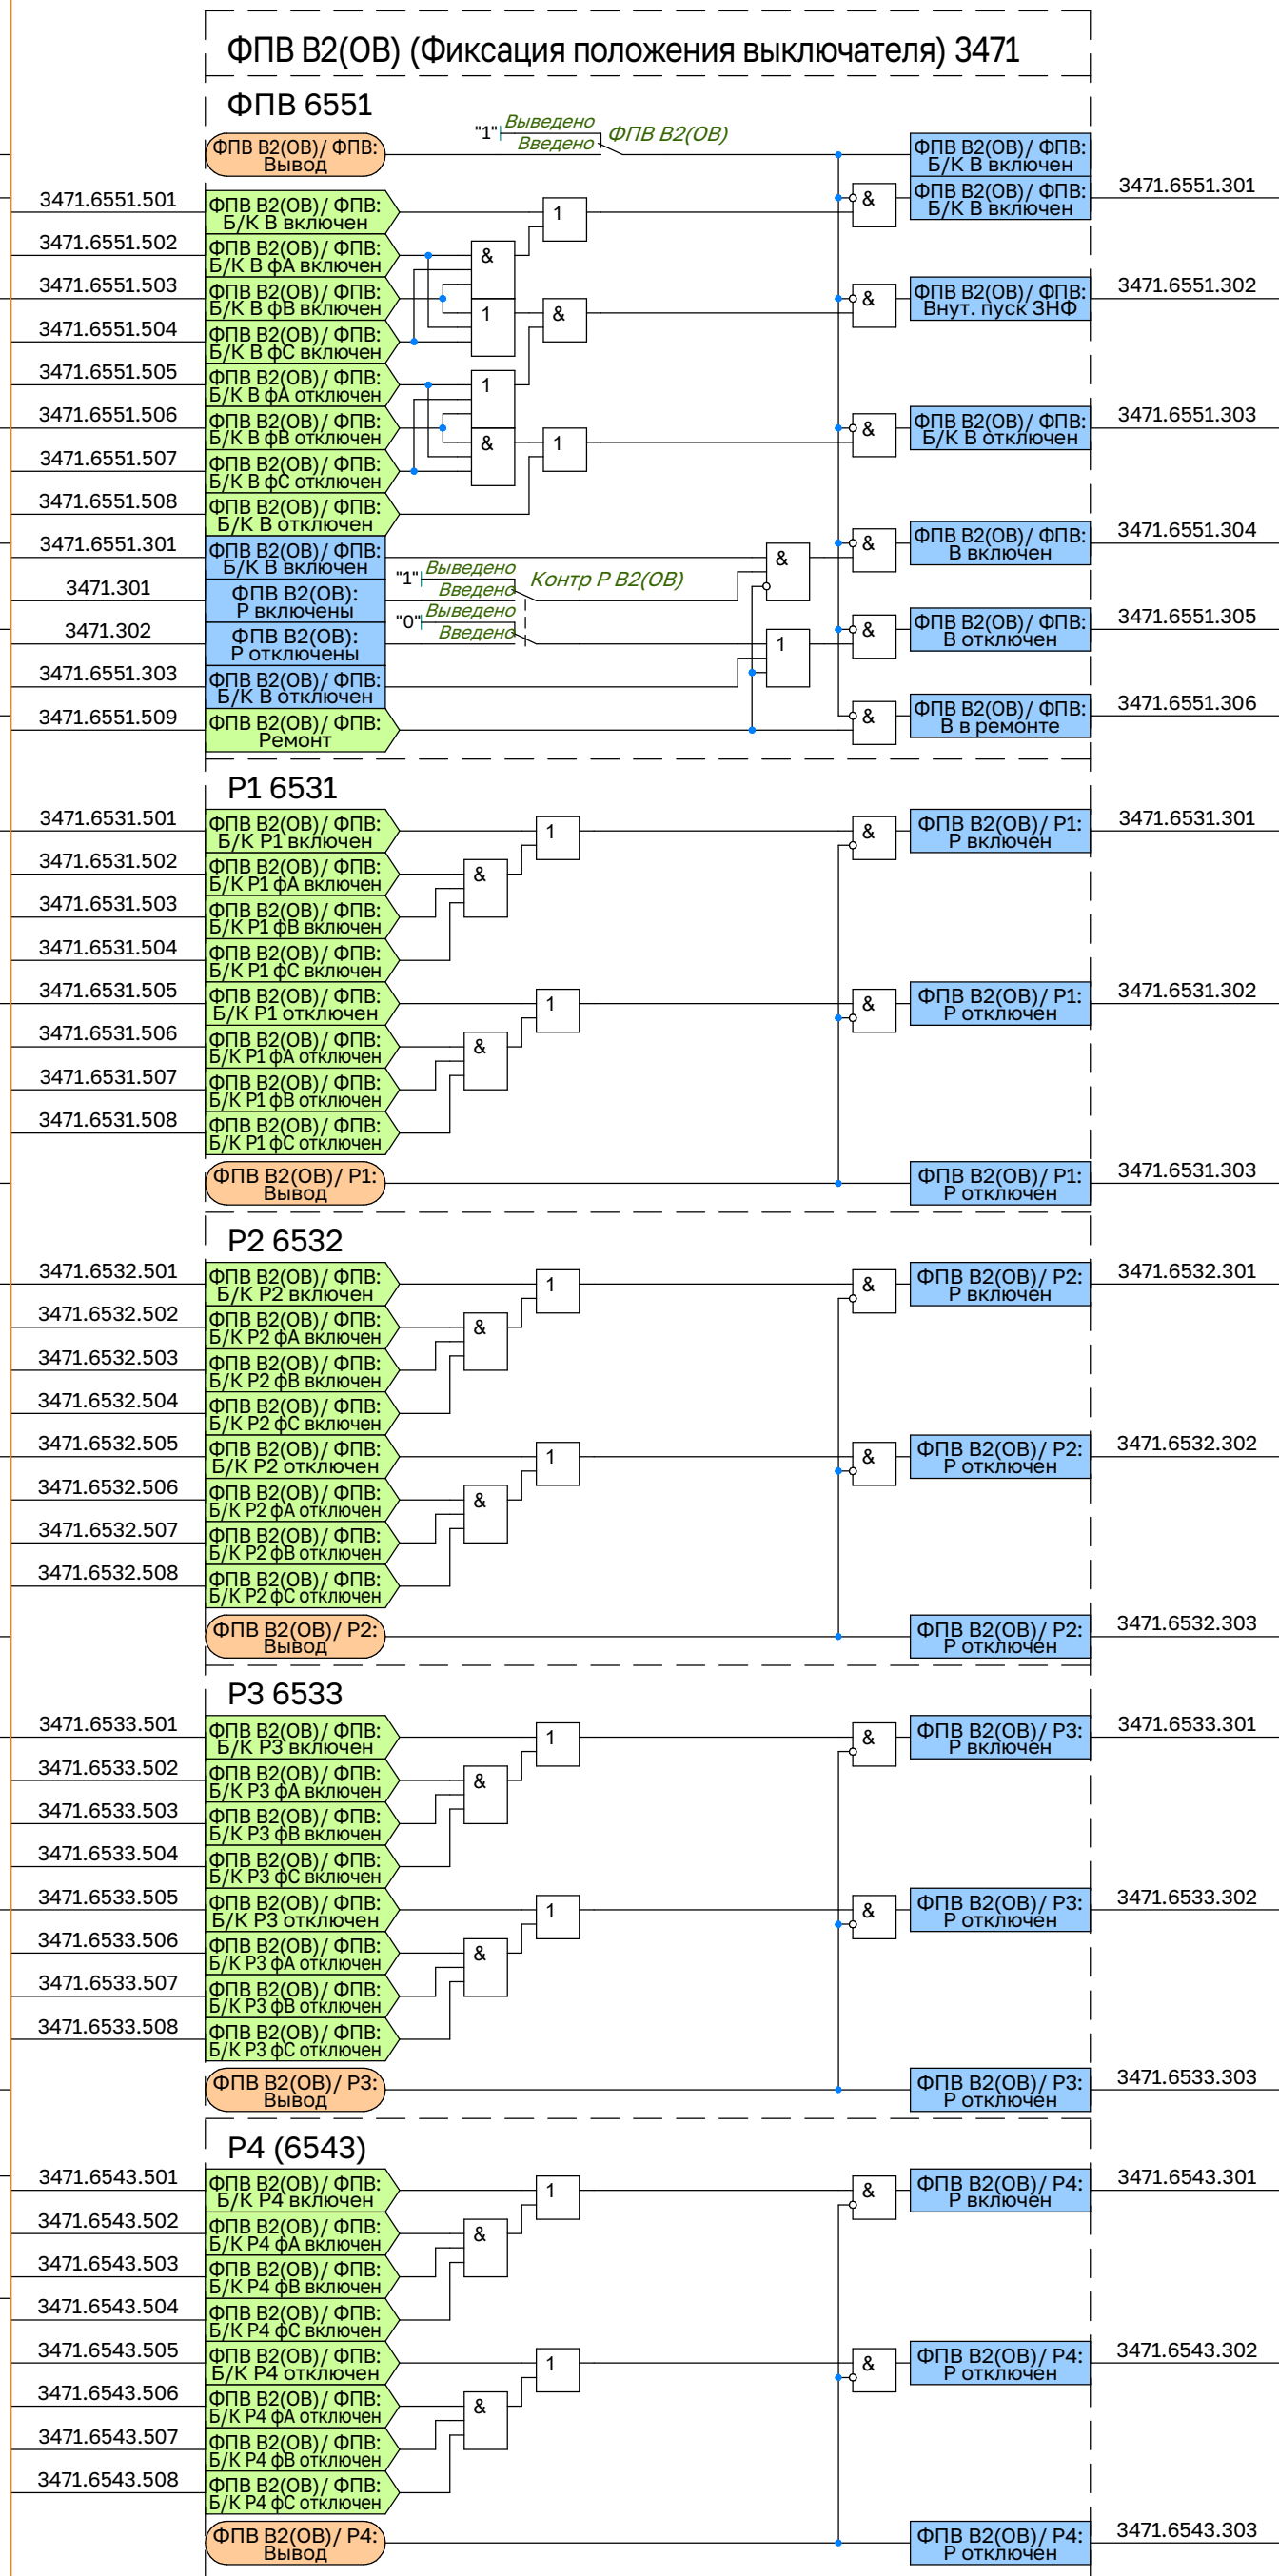


Контроль В 6861

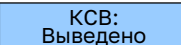


Контроль ТТ 6581

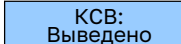


Работа ЭМВ

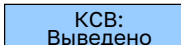


БКУ Опер./ БКУ:
РКВ

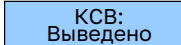

БКУ 6661

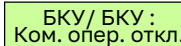

БКУ 6661

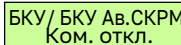

Блокировка управления 6901



YB 6921

