

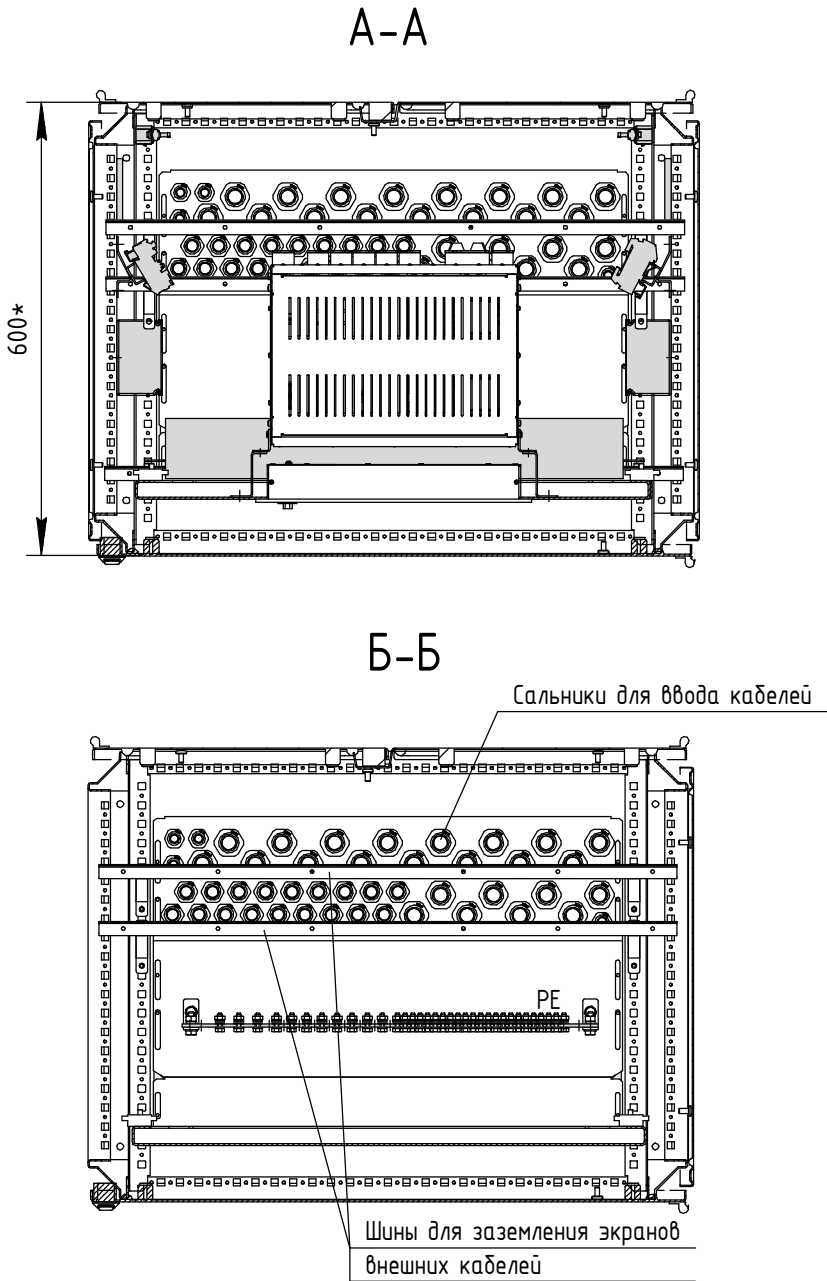


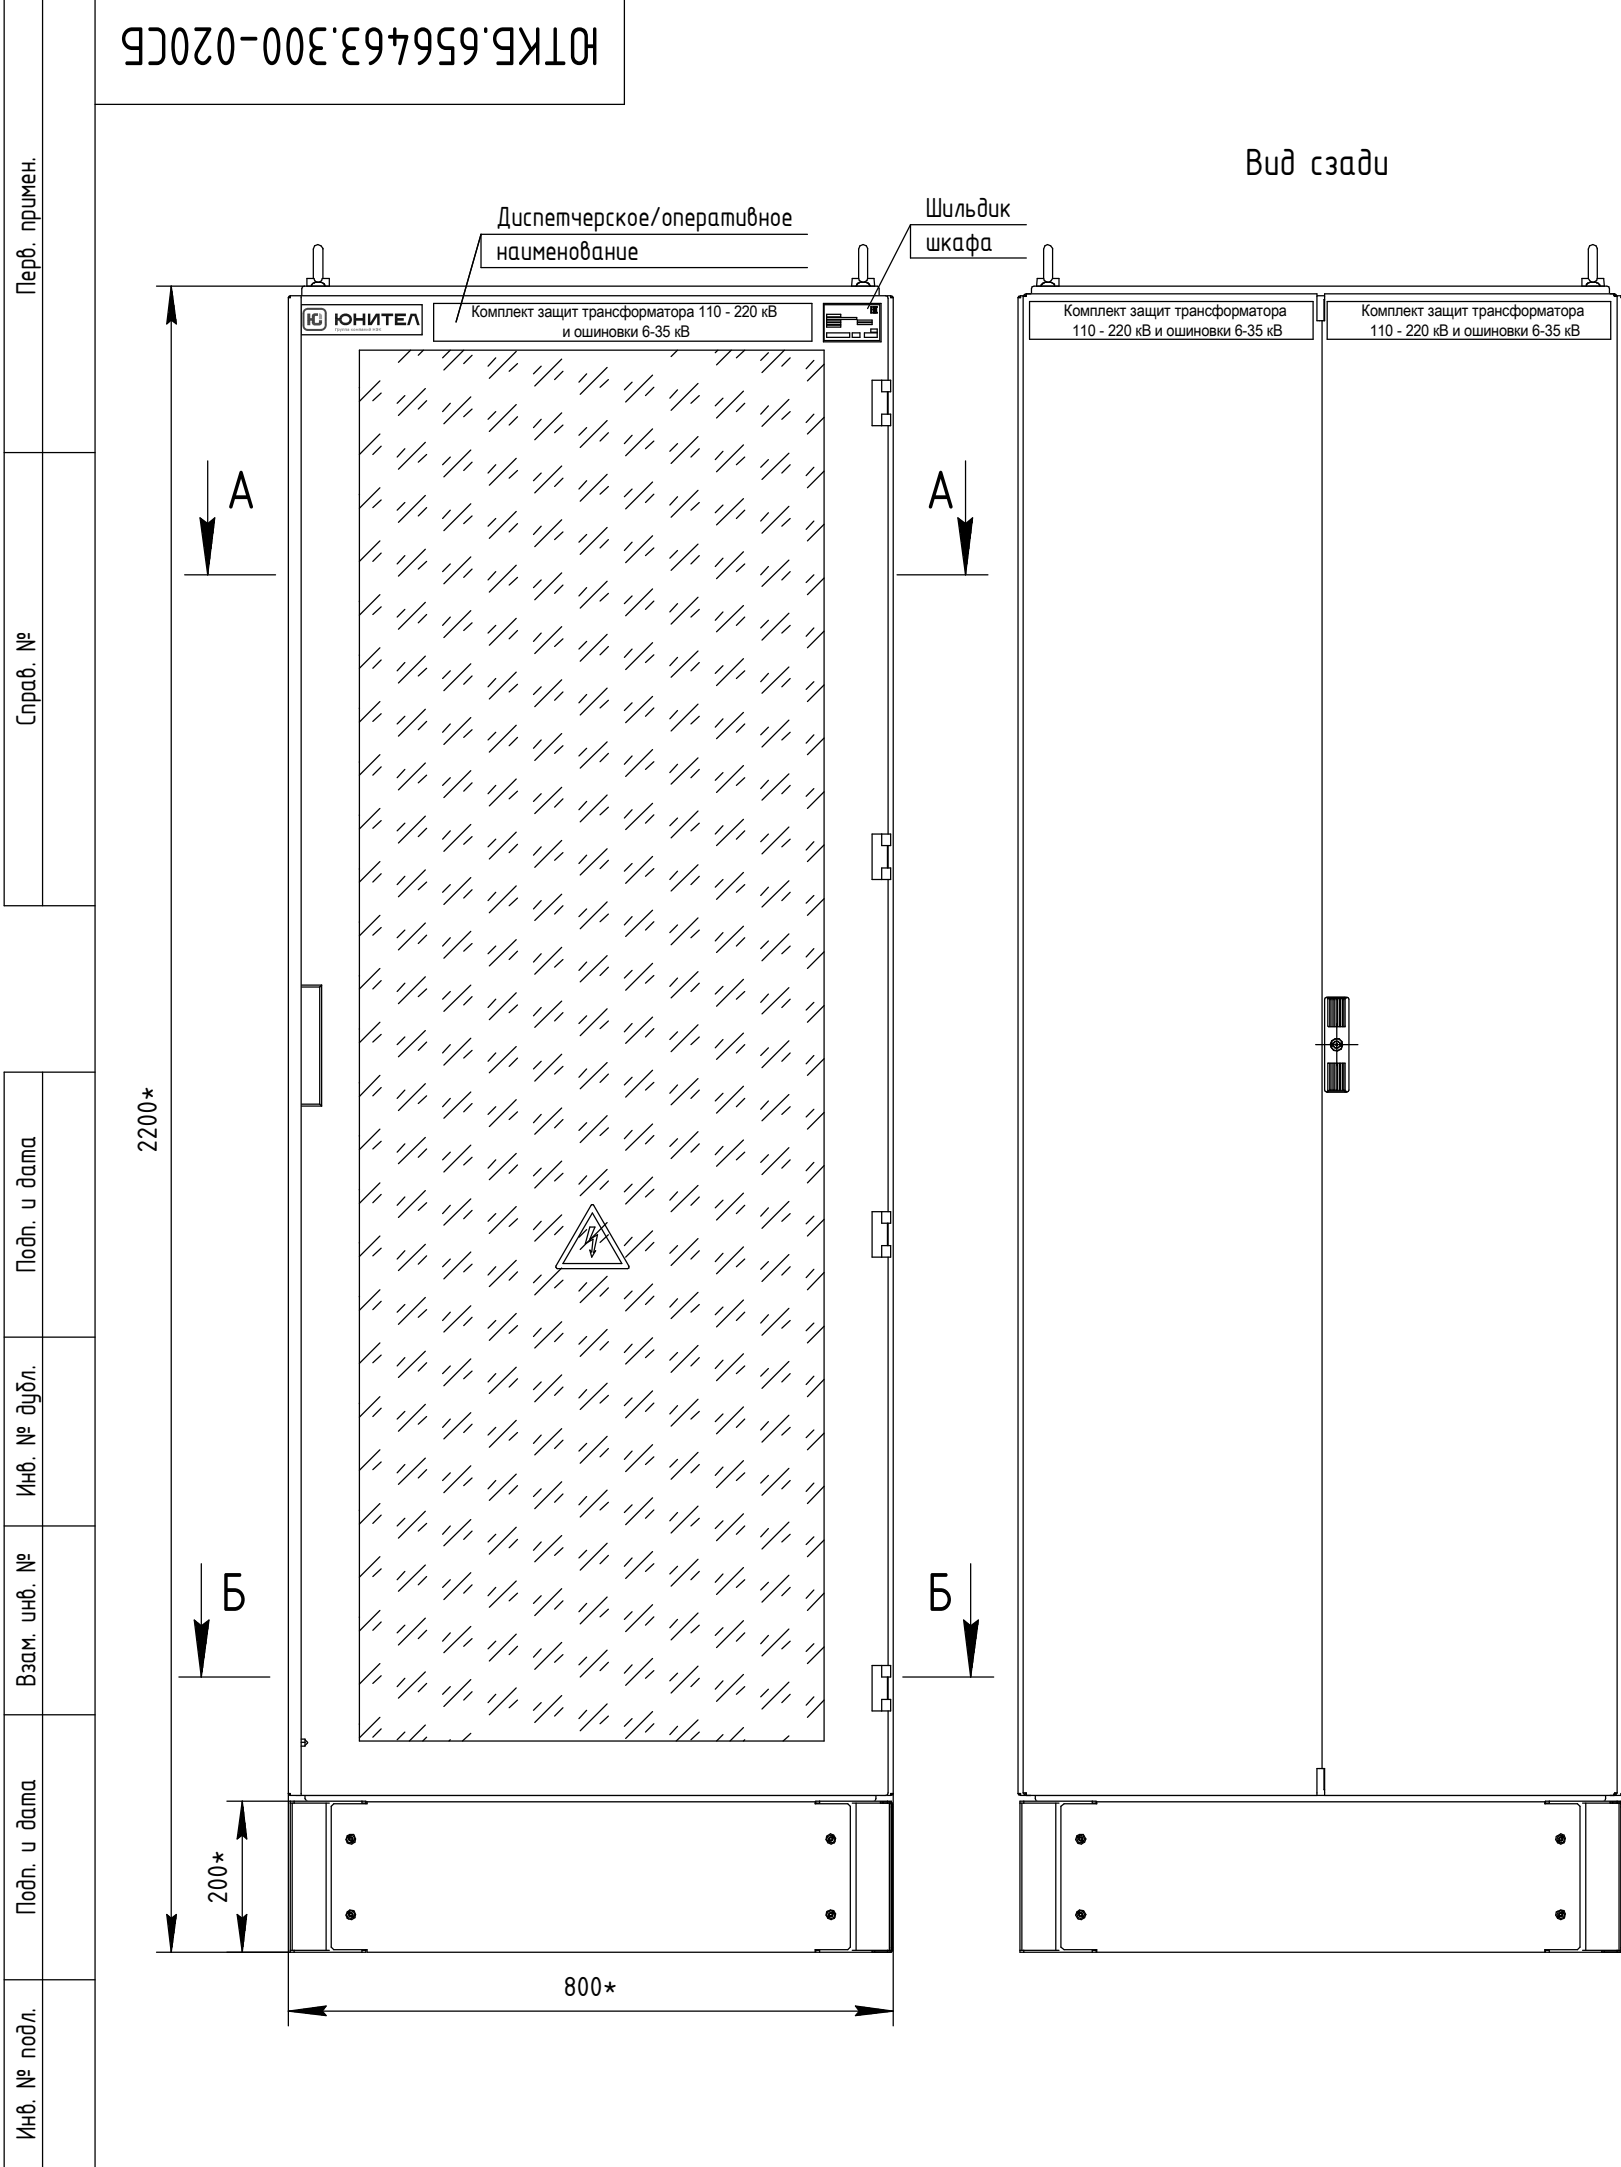


- 1 \* Указаны типовые габариты шкафов. Фактические размеры металлоконструкции могут отличаться в пределах +10 мм. Размеры даны без учета выступающих частей (ручек, петель и т.д.).
- 2 \*\* Указана расчетная масса изделия. Фактическая масса изделия определяется взвешиванием.
- 3 Общие допуски ± IT14/2 по ГОСТ 30893.1-2002.
- 4 Степень защиты шкафа IP54.
- 5 Подвод внешних кабелей снизу.
- 6 Монтаж оборудования в шкафу выполнить по нормам фирмы-изготовителя.
- 7 Позиционные обозначения аппаратов соответствуют перечню элементов ЮТКБ.656463.300-020ПЭЗ.

|          |      |              |                                                                                       |            |   |   |  |       |         |   |  |  |  |  |  |
|----------|------|--------------|---------------------------------------------------------------------------------------|------------|---|---|--|-------|---------|---|--|--|--|--|--|
|          |      |              |                                                                                       |            | ЮТКБ.656463.300-020СБ                                                                               |   |  |       |         |   |  |  |  |  |  |
|          |      |              |                                                                                       |            | Шкаф защит трансформатора 110-220 кВ<br>и ошиновки 6-35 кВ<br>ШЭТ 210.01-0-ЮИРЗ<br>Сборочный чертеж | Лист.   |  | Масса | Масштаб |   |  |  |  |  |  |
|          |      |              |                                                                                       |            |   |   |  | 200** | 1:10    |   |  |  |  |  |  |
| Изм.     | Лист | № докум.     | Подп.                                                                                 | Дата       |   |   |  |       |         |   |  |  |  |  |  |
| Разраб.  |      | Александрова |  | 18.06.2026 |   |   |  |       |         |   |  |  |  |  |  |
| Пров.    |      | Черемисова   |  | 18.06.2026 |   |   |  |       |         |   |  |  |  |  |  |
| Т.контр. |      |              |                                                                                       |            |   | Лист   |  | 1     | Листов  | 2 |  |  |  |  |  |
|          |      |              |                                                                                       |            |   |  <b>НЭК</b><br><b>ЮНИТЕЛ</b> |  |       |         |   |  |  |  |  |  |
| Н.контр. |      |              |                                                                                       |            |   |   |  |       |         |   |  |  |  |  |  |
| Утв.     |      |              |                                                                                       |            |   |   |  |       |         |   |  |  |  |  |  |
|          |      | Ильин        |  | 18.06.2026 |   |   |  |       |         |   |  |  |  |  |  |

Вид спереди  
Дверь условно не показана

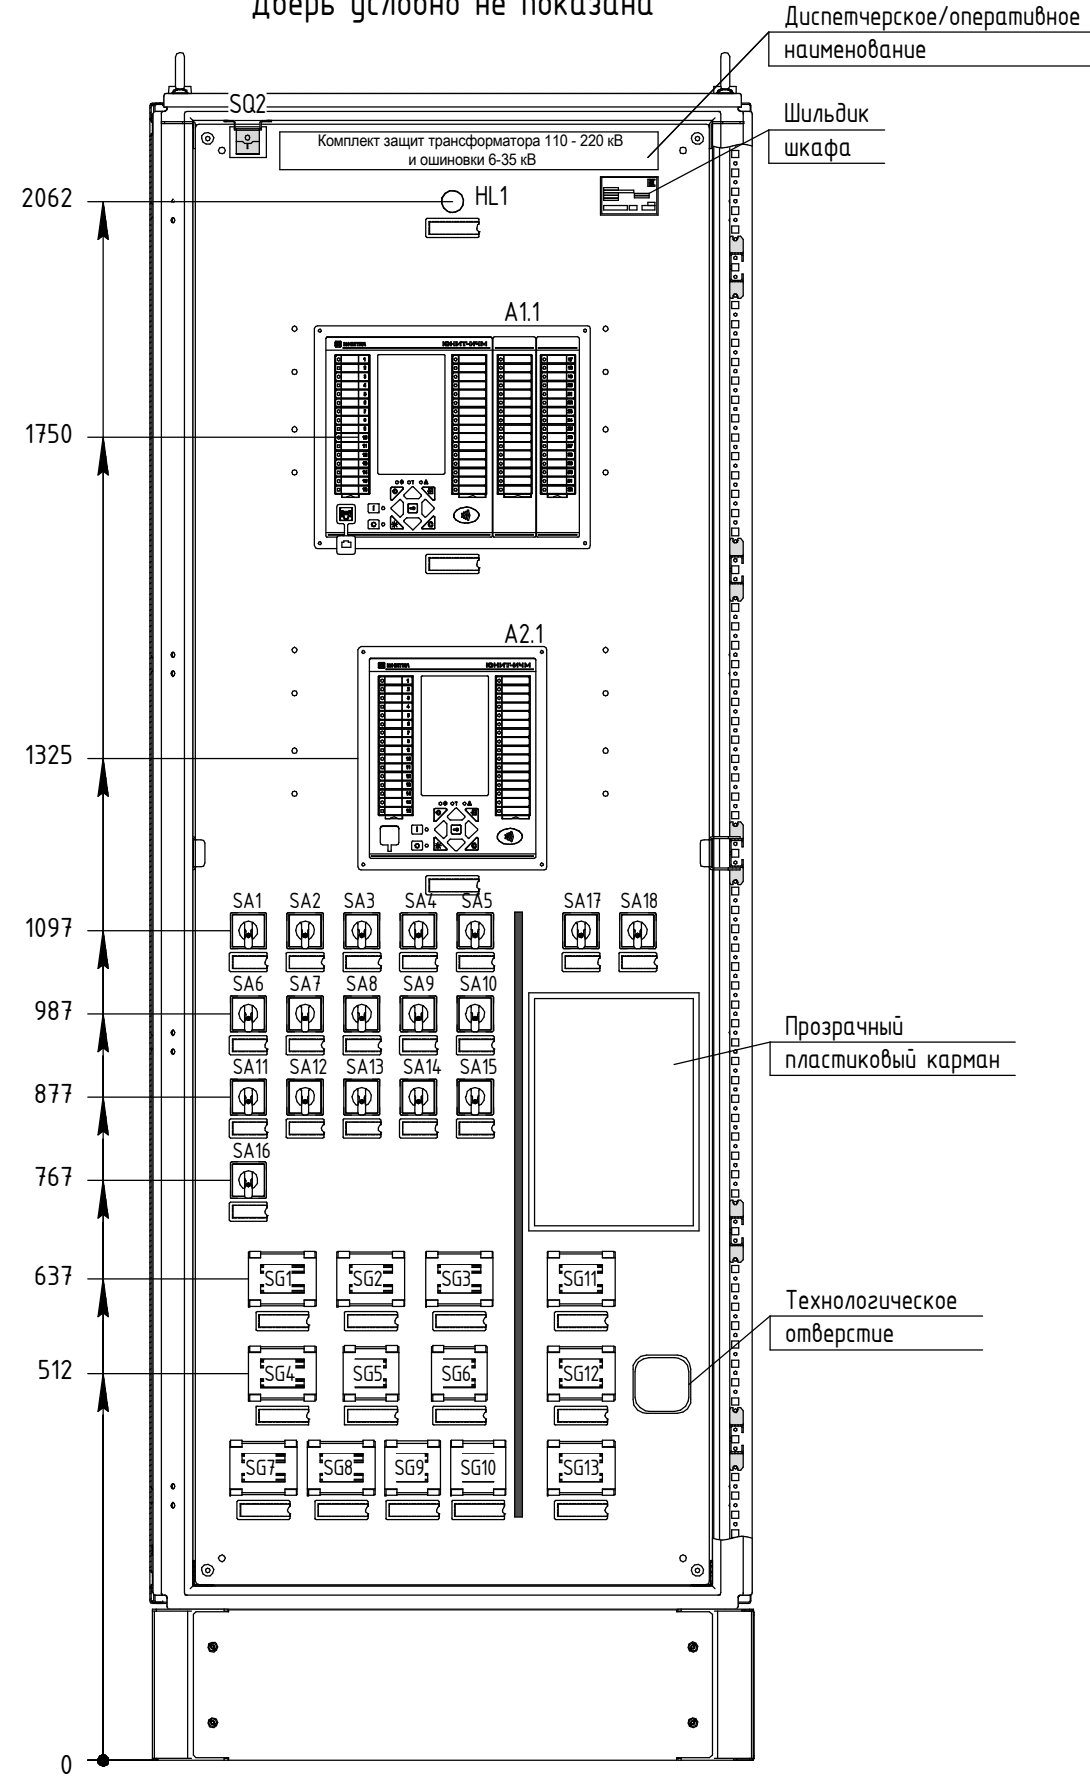


Г-Г

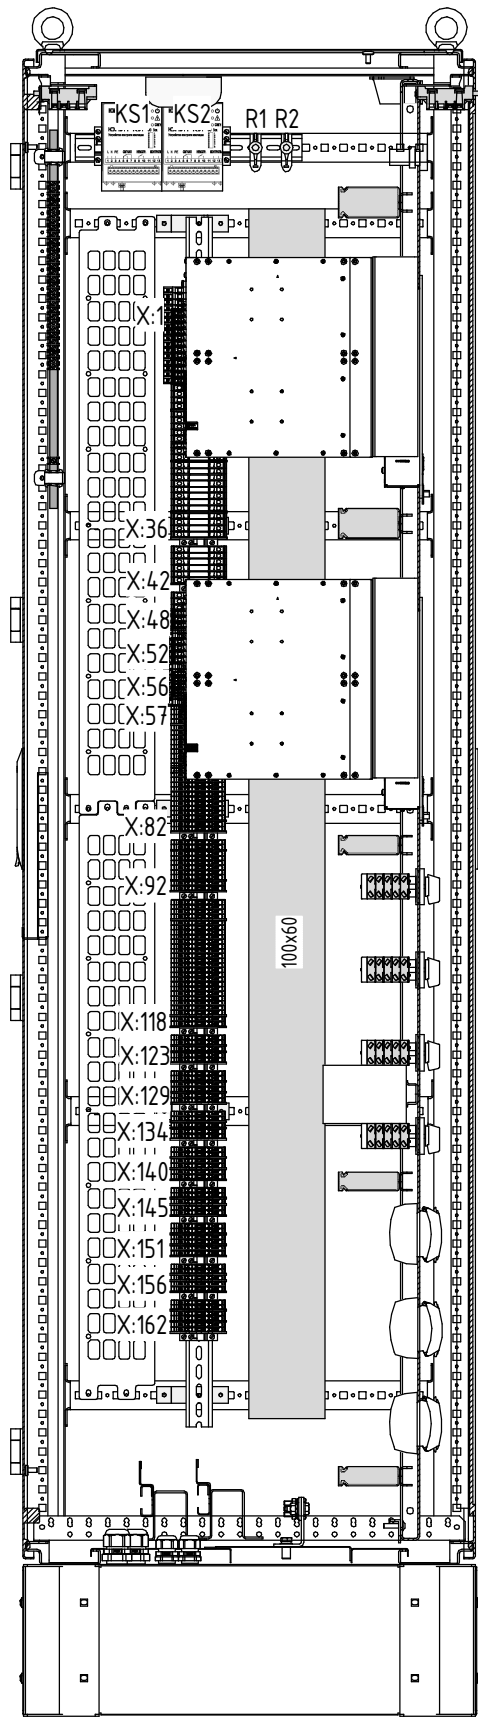


Вид сзади  
Дверь, ряды зажимов и вертикальные корпуса условно не показаны

В Г

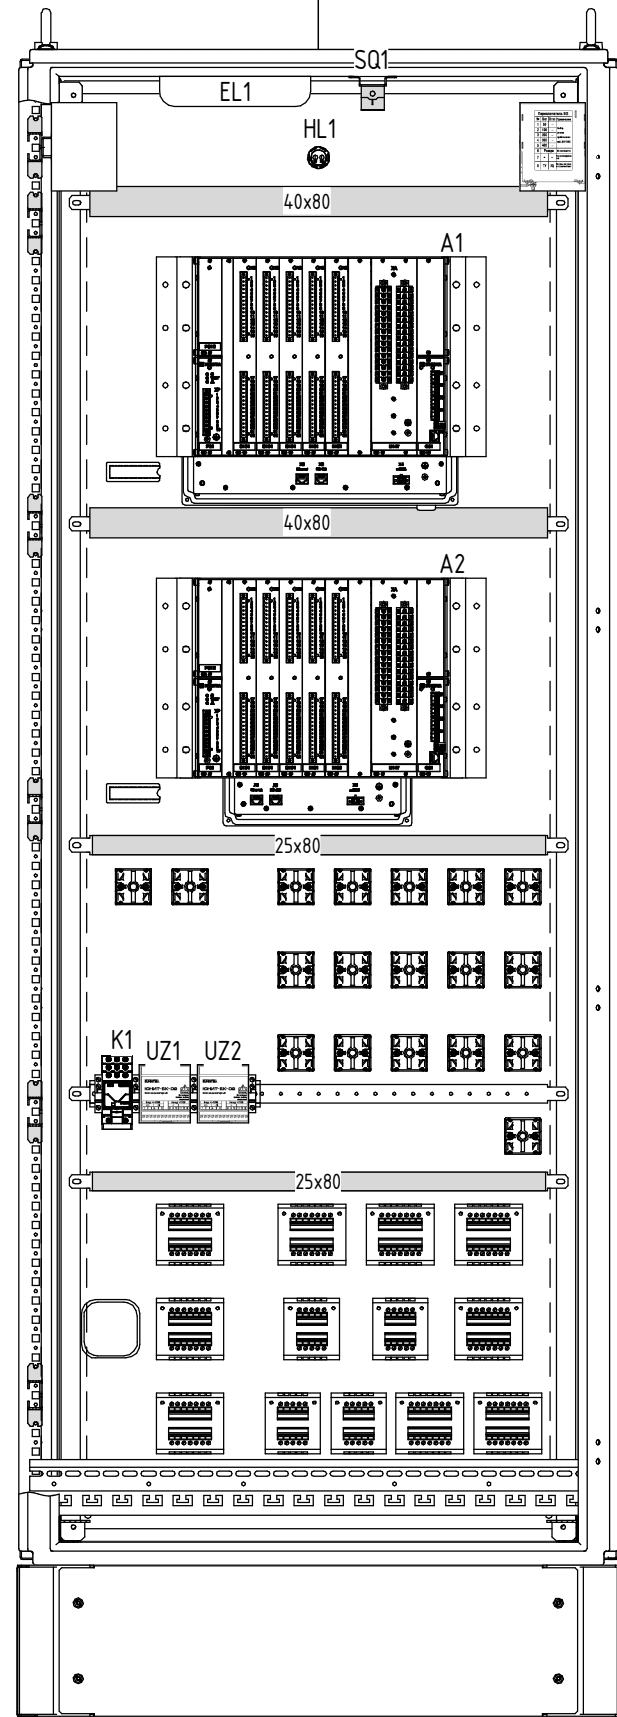

В Г

В-В

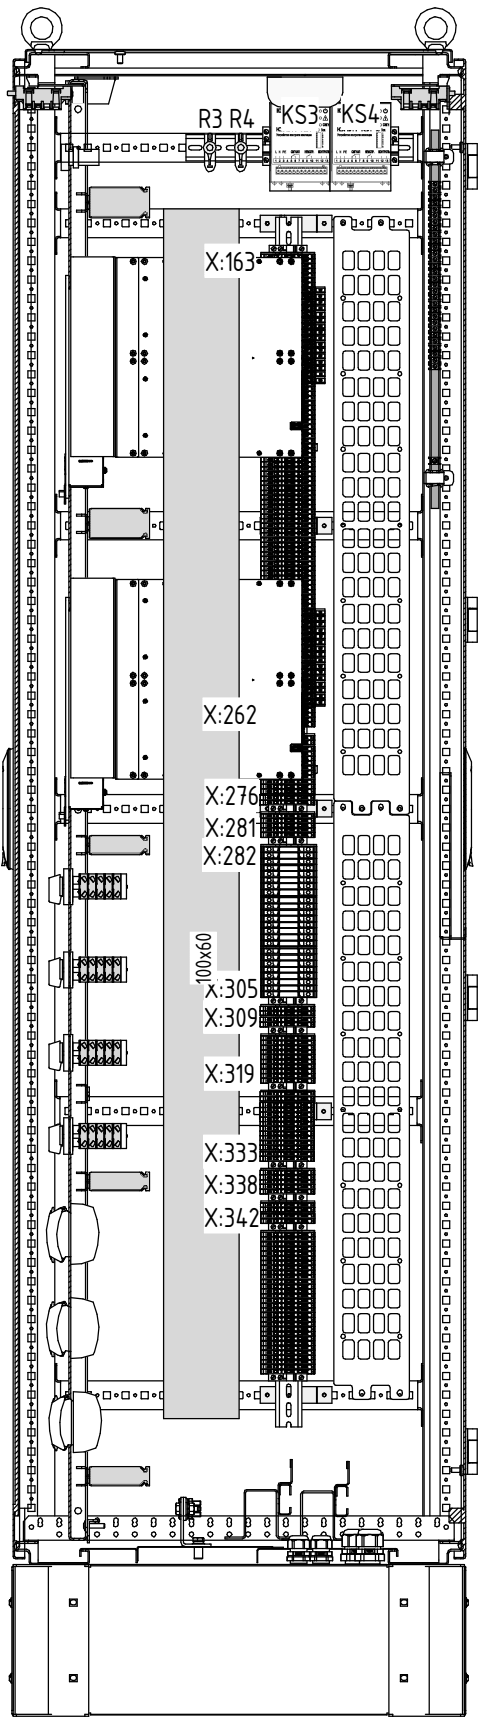

| Инв. № подл. | Подп. и дата | Взам. инв. № | Инв. № дубл. | Подп. и дата |
|--------------|--------------|--------------|--------------|--------------|
|              |              |              |              |              |

|      |      |          |       |      |
|------|------|----------|-------|------|
| Изм. | Лист | № докум. | Подп. | Дата |
|      |      |          |       |      |