



ФПВ СВ (Фиксация положения выключателя) 3461


ФПВ 6551

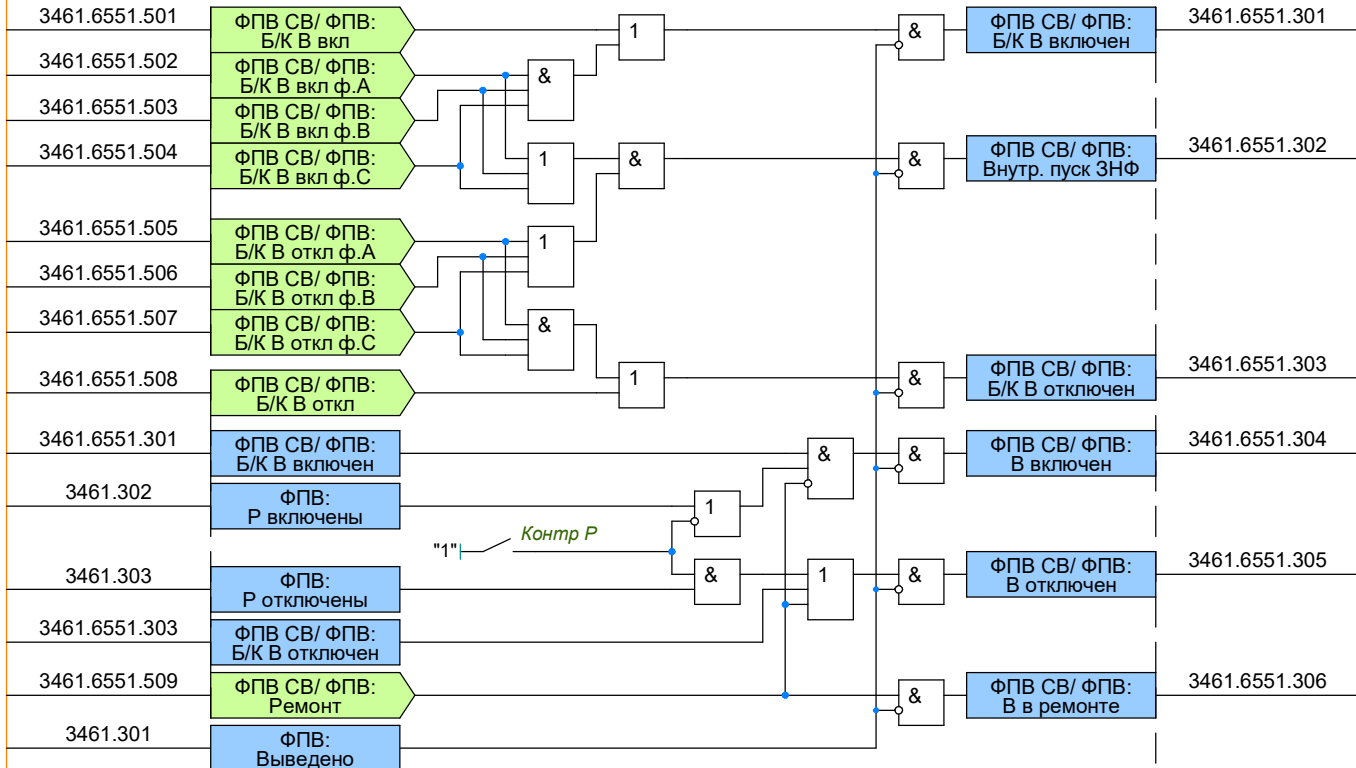

Р1 6531

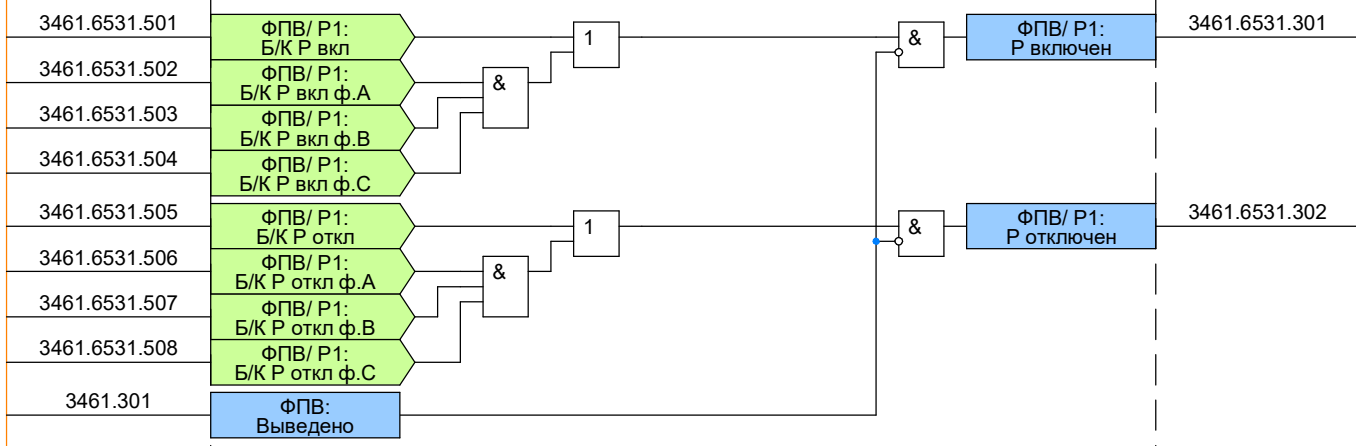

Р2 6532

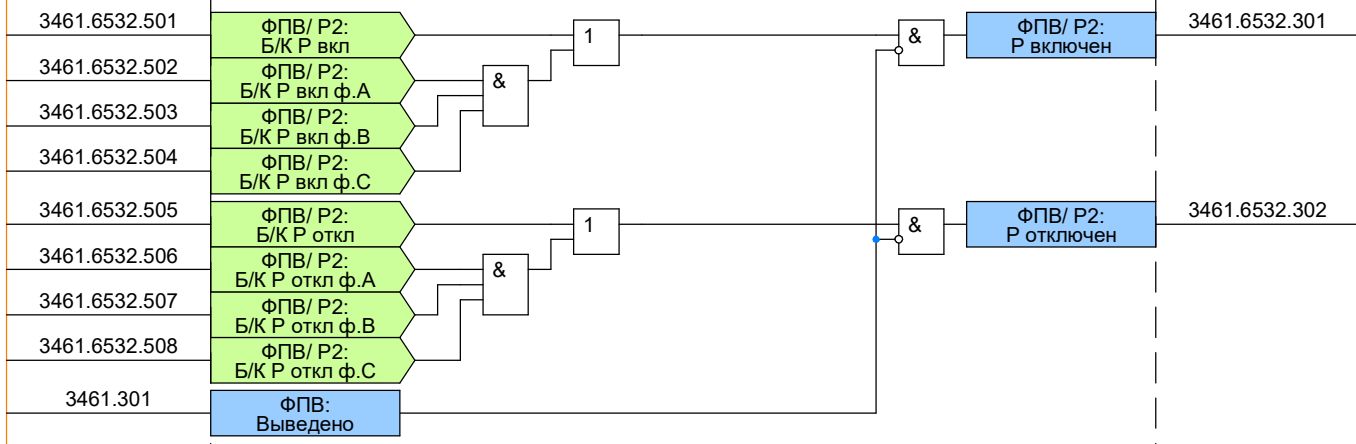


ФПВ: Вывод




Коммутация

Коммутация

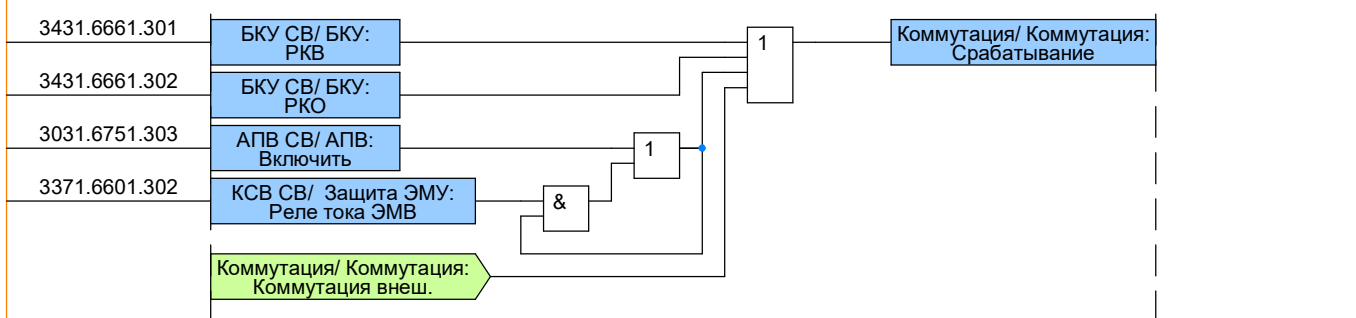

Общая логика

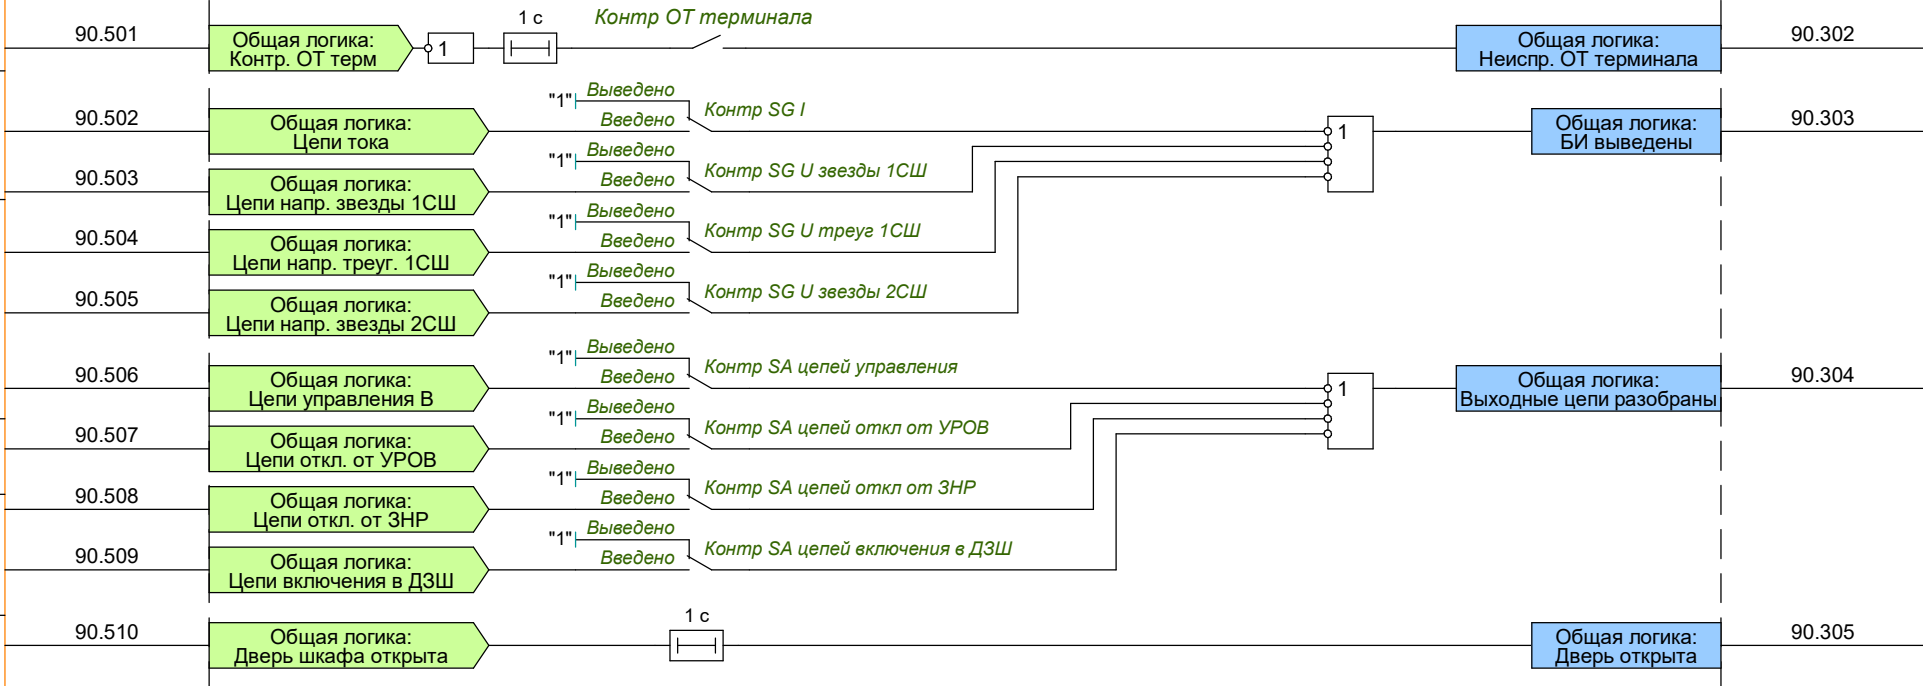

Сигнализация

