

ЦОС.13

XA1:1	la*
XA1:2	la
XA1:3	lb*
XA1:4	lb
XA1:5	lc*
XA1:6	lc
XA1:7	Ua 1C*
XA1:8	Ua 1C
XA1:9	Ub 1C*
XA1:10	Ub 1C
XA1:11	Uc 1C*
XA1:12	Uc 1C
XA1:13	Уни(Унф)*
XA1:14	Уни(Унф)
XA1:15	Уик(Уфк)*
XA1:16	Уик(Уфк)
XA1:17	Уиф(Унк)*
XA1:18	Уиф(Унк)
XA1:19	Ua 2C*
XA1:20	Ua 2C
XA1:21	Ub 2C*
XA1:22	Ub 2C
XA1:23	Uc 2C*
XA1:24	Uc 2C
XA1:25	резерв или не исп.
XA1:26	резерв или не исп.
XA1:27	резерв или не исп.
XA1:28	резерв или не исп.
XA1:29	резерв или не исп.
XA1:30	резерв или не исп.
XA1:31	резерв или не исп.
XA1:32	резерв или не исп.

Ua 1CШ
Ub 1CШ
Uc 1CШ
Uab 1CШ
Ubc 1CШ
Uca 1CШ
U1 1CШ
U2 1CШ
3U0 1CШ звезда
U2/U1 1CШ
dU1 1CШ
Uин(Унф) 1CШ
Uиф(Унф) 1CШ
Uик(Уфк) 1CШ
3U0 1CШ треуго.

Ua 2CШ
Ub 2CШ
Uc 2CШ
Uab 2CШ
Ubc 2CШ
Uca 2CШ
U1 2CШ
U2 2CШ
3U0 2CШ звезда
U2/U1 2CШ
dU1 2CШ
Ua'k 2CШ
Uинн 1CШ
Uинн ф.А 1CШ
Uинн ф.В 1CШ
Uинн ф.С 1CШ

0161.501

АМТЗ: Опер. ввод	0161.501
БНН 1СШ/ БНН: Автомат ТН	1511.4531.501
БНН 1СШ/ БНН: Фикс. неиспр. ЦН	1511.4531.502
БНН 2СШ/ БНН: Автомат ТН	1501.4571.501
БНН 2СШ/ БНН: Фикс. неиспр. ЦН	1501.4571.502
ЗНР СВ/ ЗНР: Ср. ЗНР В в ЗНР	0201.0851.501
ЗНФ СВ/ ЗНФ: Пуск	3441.6521.501
ЗНФ СВ/ ЗНФ: Блокировка	3441.6521.502
КСВ СВ/ КСВ: Внеш. сигнал КС(УС)	3361.6741.501
УРОВ СВ/ УРОВ: Внеш. пуск УРОВ от РЗА 1СШ	3301.6801.501
УРОВ СВ/ УРОВ: Внеш. пуск УРОВ от РЗА 2СШ	3301.6801.502
УРОВ СВ/ УРОВ: Пуск УРОВ НН 1СШ	3301.6801.503
УРОВ СВ/ УРОВ: Пуск УРОВ НН 2СШ	3301.6801.504
КСВ СВ/ Контроль В: Контр. ЭМО1	3371.6571.501
КСВ СВ/ Контроль В: Контр. ЭМО1 ф.А	3371.6571.502
КСВ СВ/ Контроль В: Контр. ЭМО1 ф.В	3371.6571.503
КСВ СВ/ Контроль В: Контр. ЭМО1 ф.С	3371.6571.504
КСВ СВ/ Контроль В: Контр. ЭМО2	3371.6571.505
КСВ СВ/ Контроль В: Контр. ЭМО2 ф.А	3371.6571.506
КСВ СВ/ Контроль В: Контр. ЭМО2 ф.В	3371.6571.507
КСВ СВ/ Контроль В: Контр. ЭМО2 ф.С	3371.6571.508
КСВ СВ/ Контроль В: Контр. ЭМВ	3371.6571.509
КСВ СВ/ Контроль В: Контр. ЭМВ ф.А	3371.6571.510
КСВ СВ/ Контроль В: Контр. ЭМВ ф.В	3371.6571.511
КСВ СВ/ Контроль В: Контр. ЭМВ ф.С	3371.6571.512
КСВ СВ/ Контроль В: Низк. давл. SF6	3371.6571.513
КСВ СВ/ Контроль В: Низк. давл. SF6 ф.А	3371.6571.514
КСВ СВ/ Контроль В: Низк. давл. SF6 ф.В	3371.6571.515
КСВ СВ/ Контроль В: Низк. давл. SF6 ф.С	3371.6571.516
КСВ СВ/ Контроль В: Авар. давл. SF6	3371.6571.517
КСВ СВ/ Контроль В: Авар. давл. SF6 ф.А	3371.6571.518
КСВ СВ/ Контроль В: Авар. давл. SF6 ф.В	3371.6571.519
КСВ СВ/ Контроль В: Авар. давл. SF6 ф.С	3371.6571.520
КСВ СВ/ Контроль В: Пруж. не заведены	3371.6571.521
КСВ СВ/ Контроль В: Пруж. не заведены ф.А	3371.6571.522
КСВ СВ/ Контроль В: Пруж. не заведены ф.В	3371.6571.523
КСВ СВ/ Контроль В: Пруж. не заведены ф.С	3371.6571.524
КСВ СВ/ Контроль В: Неиспр. обогр.	3371.6571.525
КСВ СВ/ Контроль В: Автомат ШП	3371.6571.526
КСВ СВ/ Контроль В: Контр. ОТ ЭМВ ЭМО1	3371.6571.527
КСВ СВ/ Контроль В: Контр. ОТ ЭМО2	3371.6571.528
КСВ СВ/ Контроль В: Контр. ОТ сигн.	3371.6571.529
КСВ СВ/ Блокировка упр.: Внеш. блок. упр.	3371.6611.501
КСВ СВ/ Блокировка упр.: Внеш. блок. вкл.	3371.6611.502
КСВ СВ/ Контроль ТТ Низк. давл. SF6 ТТ	3371.6581.501
КСВ СВ/ Контроль ТТ Низк. давл. SF6 ТТ ф.А	3371.6581.502
КСВ СВ/ Контроль ТТ Низк. давл. SF6 ТТ ф.В	3371.6581.503
КСВ СВ/ Контроль ТТ Низк. давл. SF6 ТТ ф.С	3371.6581.504
КСВ СВ/ Контроль ТТ Авар. давл. SF6 ТТ	3371.6581.505
КСВ СВ/ Контроль ТТ Авар. давл. SF6 ТТ ф.А	3371.6581.506
КСВ СВ/ Контроль ТТ Авар. давл. SF6 ТТ ф.В	3371.6581.507
КСВ СВ/ Контроль ТТ Авар. давл. SF6 ТТ ф.С	3371.6581.508


3371.658


КСВ СВ/ Контроль ТТ Неиспр. обгор. ТТ	3371.6581.509
КСВ СВ/ Защита ЭМУ: Работа ЭМВ	3371.6601.501
КСВ СВ/ Защита ЭМУ: Работа ЭМВ ф.А	3371.6601.502
КСВ СВ/ Защита ЭМУ: Работа ЭМВ ф.В	3371.6601.503
КСВ СВ/ Защита ЭМУ: Работа ЭМВ ф.С	3371.6601.504
КСВ СВ/ Защита ЭМУ: Работа ЭМО1	3371.6601.505
КСВ СВ/ Защита ЭМУ: Работа ЭМО1 ф.А	3371.6601.506
КСВ СВ/ Защита ЭМУ: Работа ЭМО1 ф.В	3371.6601.507
КСВ СВ/ Защита ЭМУ: Работа ЭМО1 ф.С	3371.6601.508
КСВ СВ/ Защита ЭМУ: Работа ЭМО2	3371.6601.509
КСВ СВ/ Защита ЭМУ: Работа ЭМО2 ф.А	3371.6601.510
КСВ СВ/ Защита ЭМУ: Работа ЭМО2 ф.В	3371.6601.511
КСВ СВ/ Защита ЭМУ: Работа ЭМО2 ф.С	3371.6601.512
БКУ СВ/ БКУ: Опер. вкл.	3431.6661.501
БКУ СВ/ БКУ: Опер. откл.	3431.6661.502
ЛО: Внеш. откл. от РЗА 1СШ	5121.8811.501
ЛО: Внеш. откл. от РЗА 2СШ	5121.8811.502
ЛО: Внеш. откл. от РЗА 1СШ	5121.8821.501
ЛО: Внеш. откл. от РЗА 2СШ	5121.8821.502
ЛО/ Запрет АПВ: Внеш. запрет АПВ от РЗА 1СШ	5121.8821.503
ЛО/ Запрет АПВ: Внеш. запрет АПВ от РЗА 2СШ	5121.8821.504
ЛО/ Запрет АПВ: Ключ МУ	5121.8821.505
Сигнализация: Внеш. неиспр.	91.502
ФПВ СВ/ ФПВ: Б/К В вкл	3461.6551.501
ФПВ СВ/ ФПВ: Б/К В вкл ф.А	3461.6551.502
ФПВ СВ/ ФПВ: Б/К В вкл ф.В	3461.6551.503
ФПВ СВ/ ФПВ: Б/К В вкл ф.С	3461.6551.504
ФПВ СВ/ ФПВ: Б/К В откл ф.А	3461.6551.505
ФПВ СВ/ ФПВ: Б/К В откл ф.В	3461.6551.506
ФПВ СВ/ ФПВ: Б/К В откл ф.С	3461.6551.507
ФПВ СВ/ ФПВ: Б/К В откл	3461.6551.508
ФПВ СВ/ ФПВ: Ремонт	3461.6551.509
ФПВ/ Р1: Б/К Р вкл	3461.6531.501
ФПВ/ Р1: Б/К Р вкл ф.А	3461.6531.502
ФПВ/ Р1: Б/К Р вкл ф.В	3461.6531.503
ФПВ/ Р1: Б/К Р вкл ф.С	3461.6531.504
ФПВ/ Р1: Б/К Р откл	3461.6531.505
ФПВ/ Р1: Б/К Р откл ф.А	3461.6531.506
ФПВ/ Р1: Б/К Р откл ф.В	3461.6531.507
ФПВ/ Р1: Б/К Р откл ф.С	3461.6531.508
ФПВ/ Р2: Б/К Р вкл	3461.6532.501
ФПВ/ Р2: Б/К Р вкл ф.А	3461.6532.502
ФПВ/ Р2: Б/К Р вкл ф.В	3461.6532.503
ФПВ/ Р2: Б/К Р вкл ф.С	3461.6532.504
ФПВ/ Р2: Б/К Р откл	3461.6532.505
ФПВ/ Р2: Б/К Р откл ф.А	3461.6532.506
ФПВ/ Р2: Б/К Р откл ф.В	3461.6532.507
ФПВ/ Р2:	3461.6532.508



91.501



Сигнализация: Сброс	91.501
Общая логика: Контр. ОТ терм	90.501
Общая логика: Цепи тока	90.502
Общая логика: Цепи напр. звезды 1СШ	90.503
Общая логика: Цепи напр. трех. 1СШ	90.504
Общая логика: Цепи напр. звезды 2СШ	90.505
Общая логика: Цепи управления В	90.506
Общая логика: Цепи откл. от УРОВ	90.507
Общая логика: Цепи откл. от ЧР	90.508
Общая логика: Цепи включения в ДЗШ	90.509
Общая логика: Дверь шкафа открыта	90.510

Вывод терминала

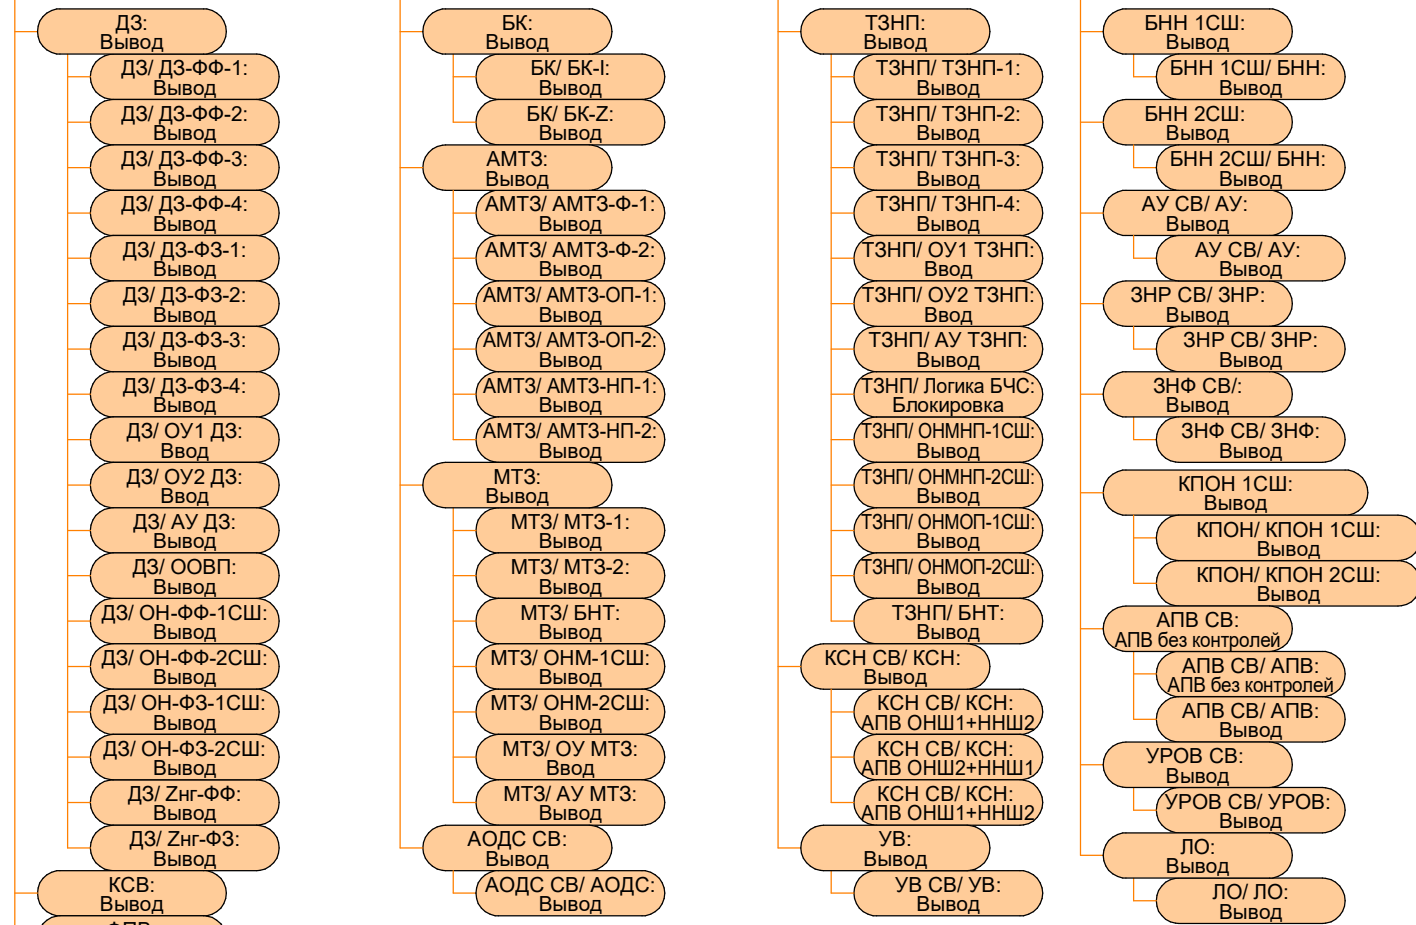

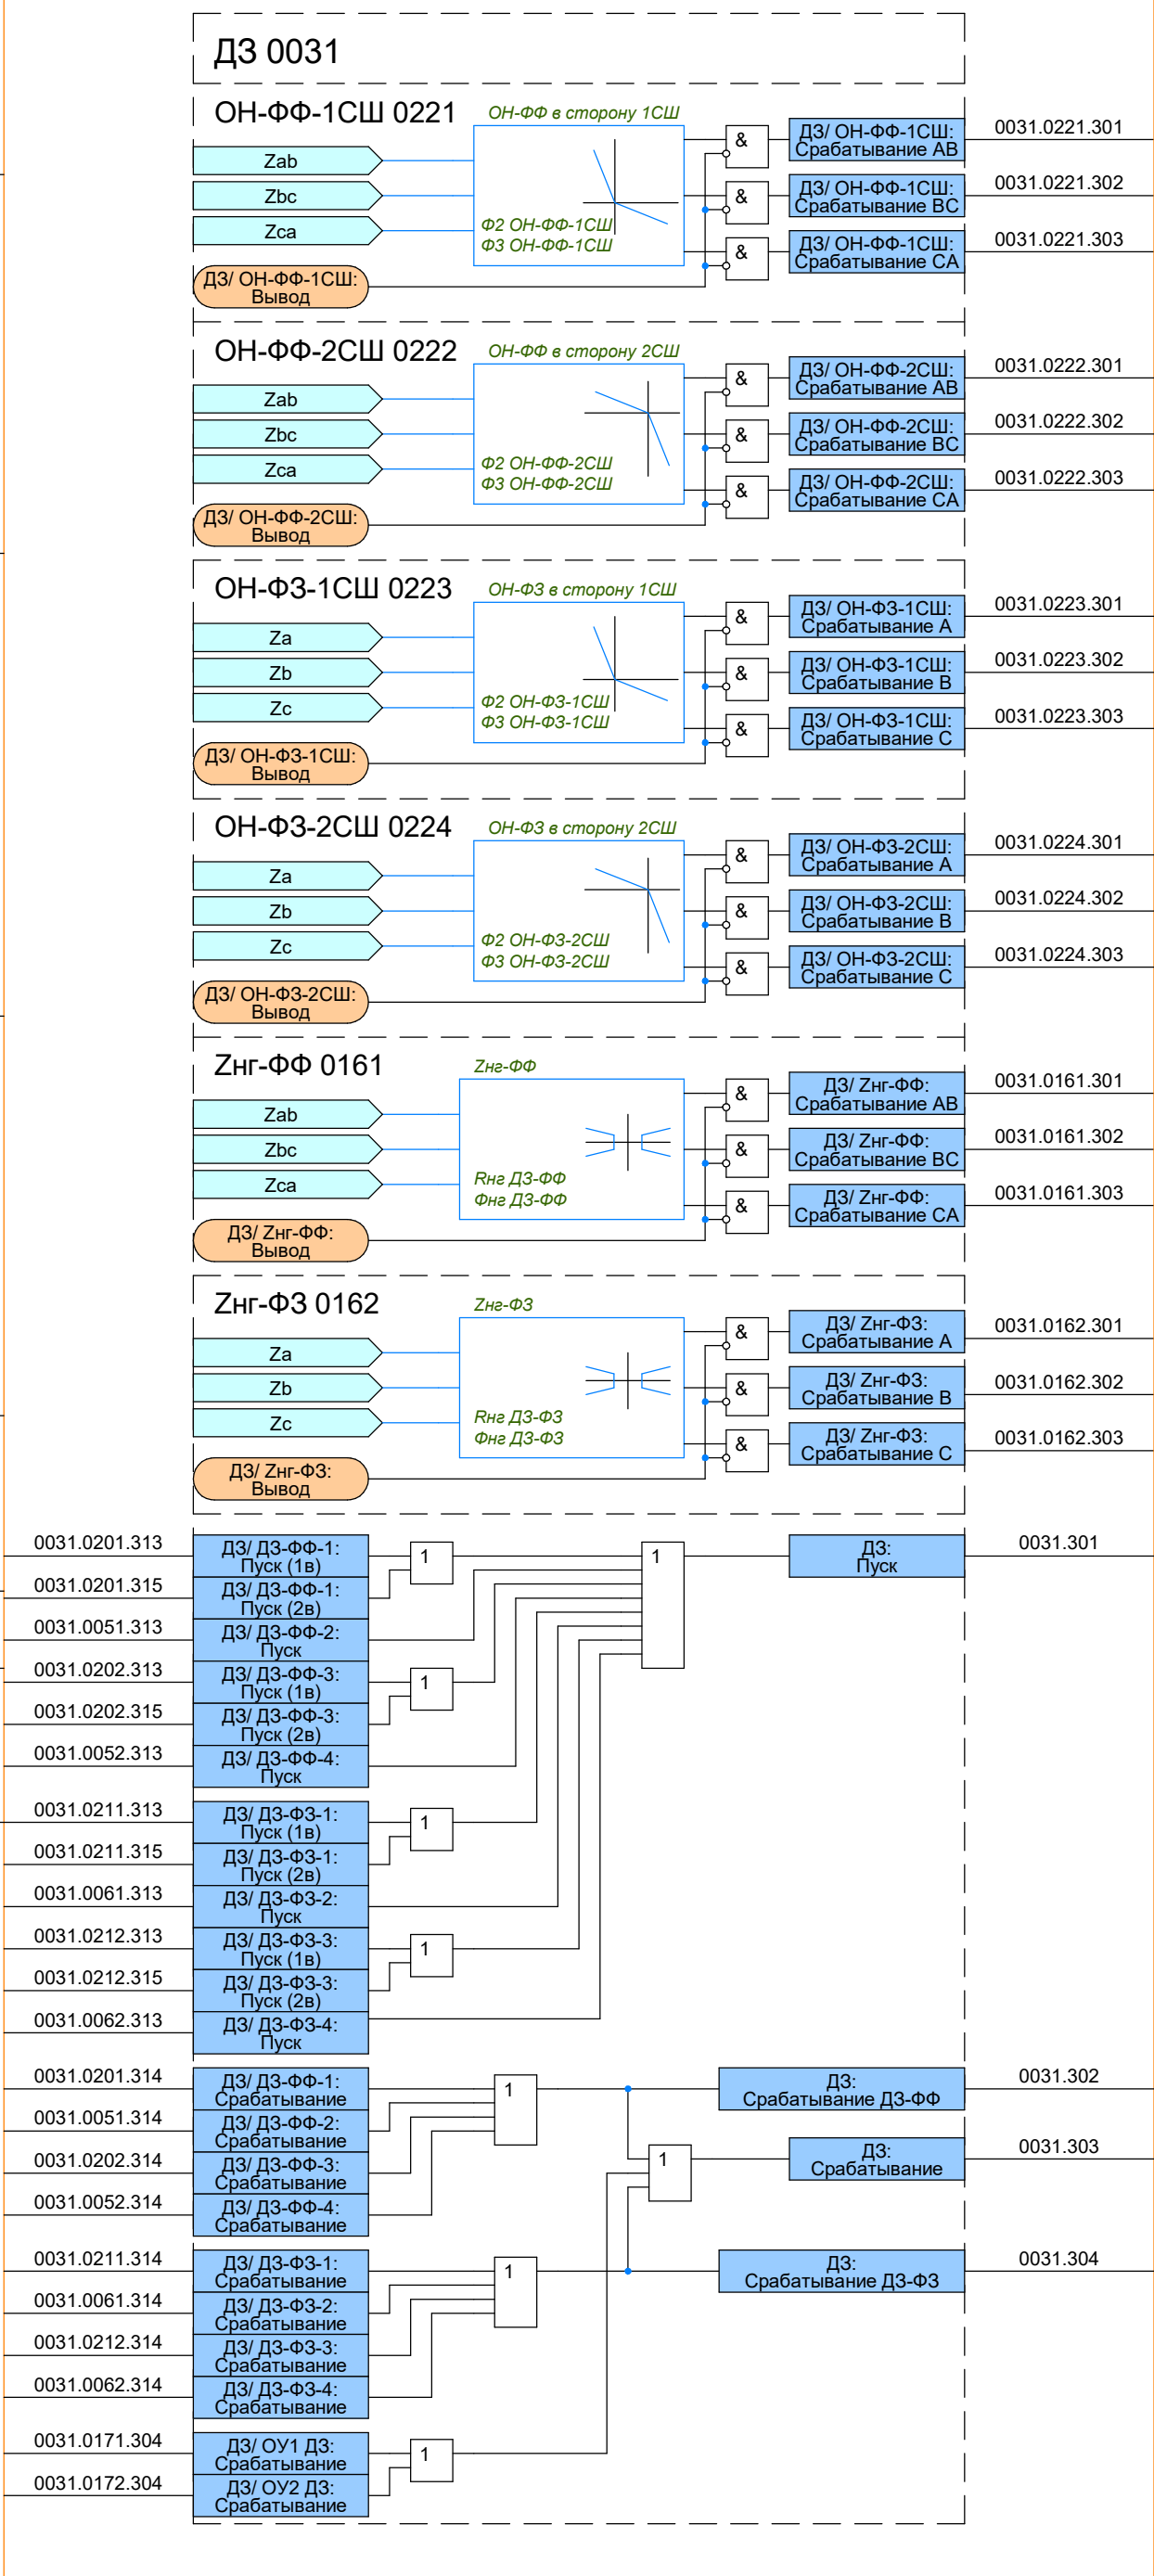


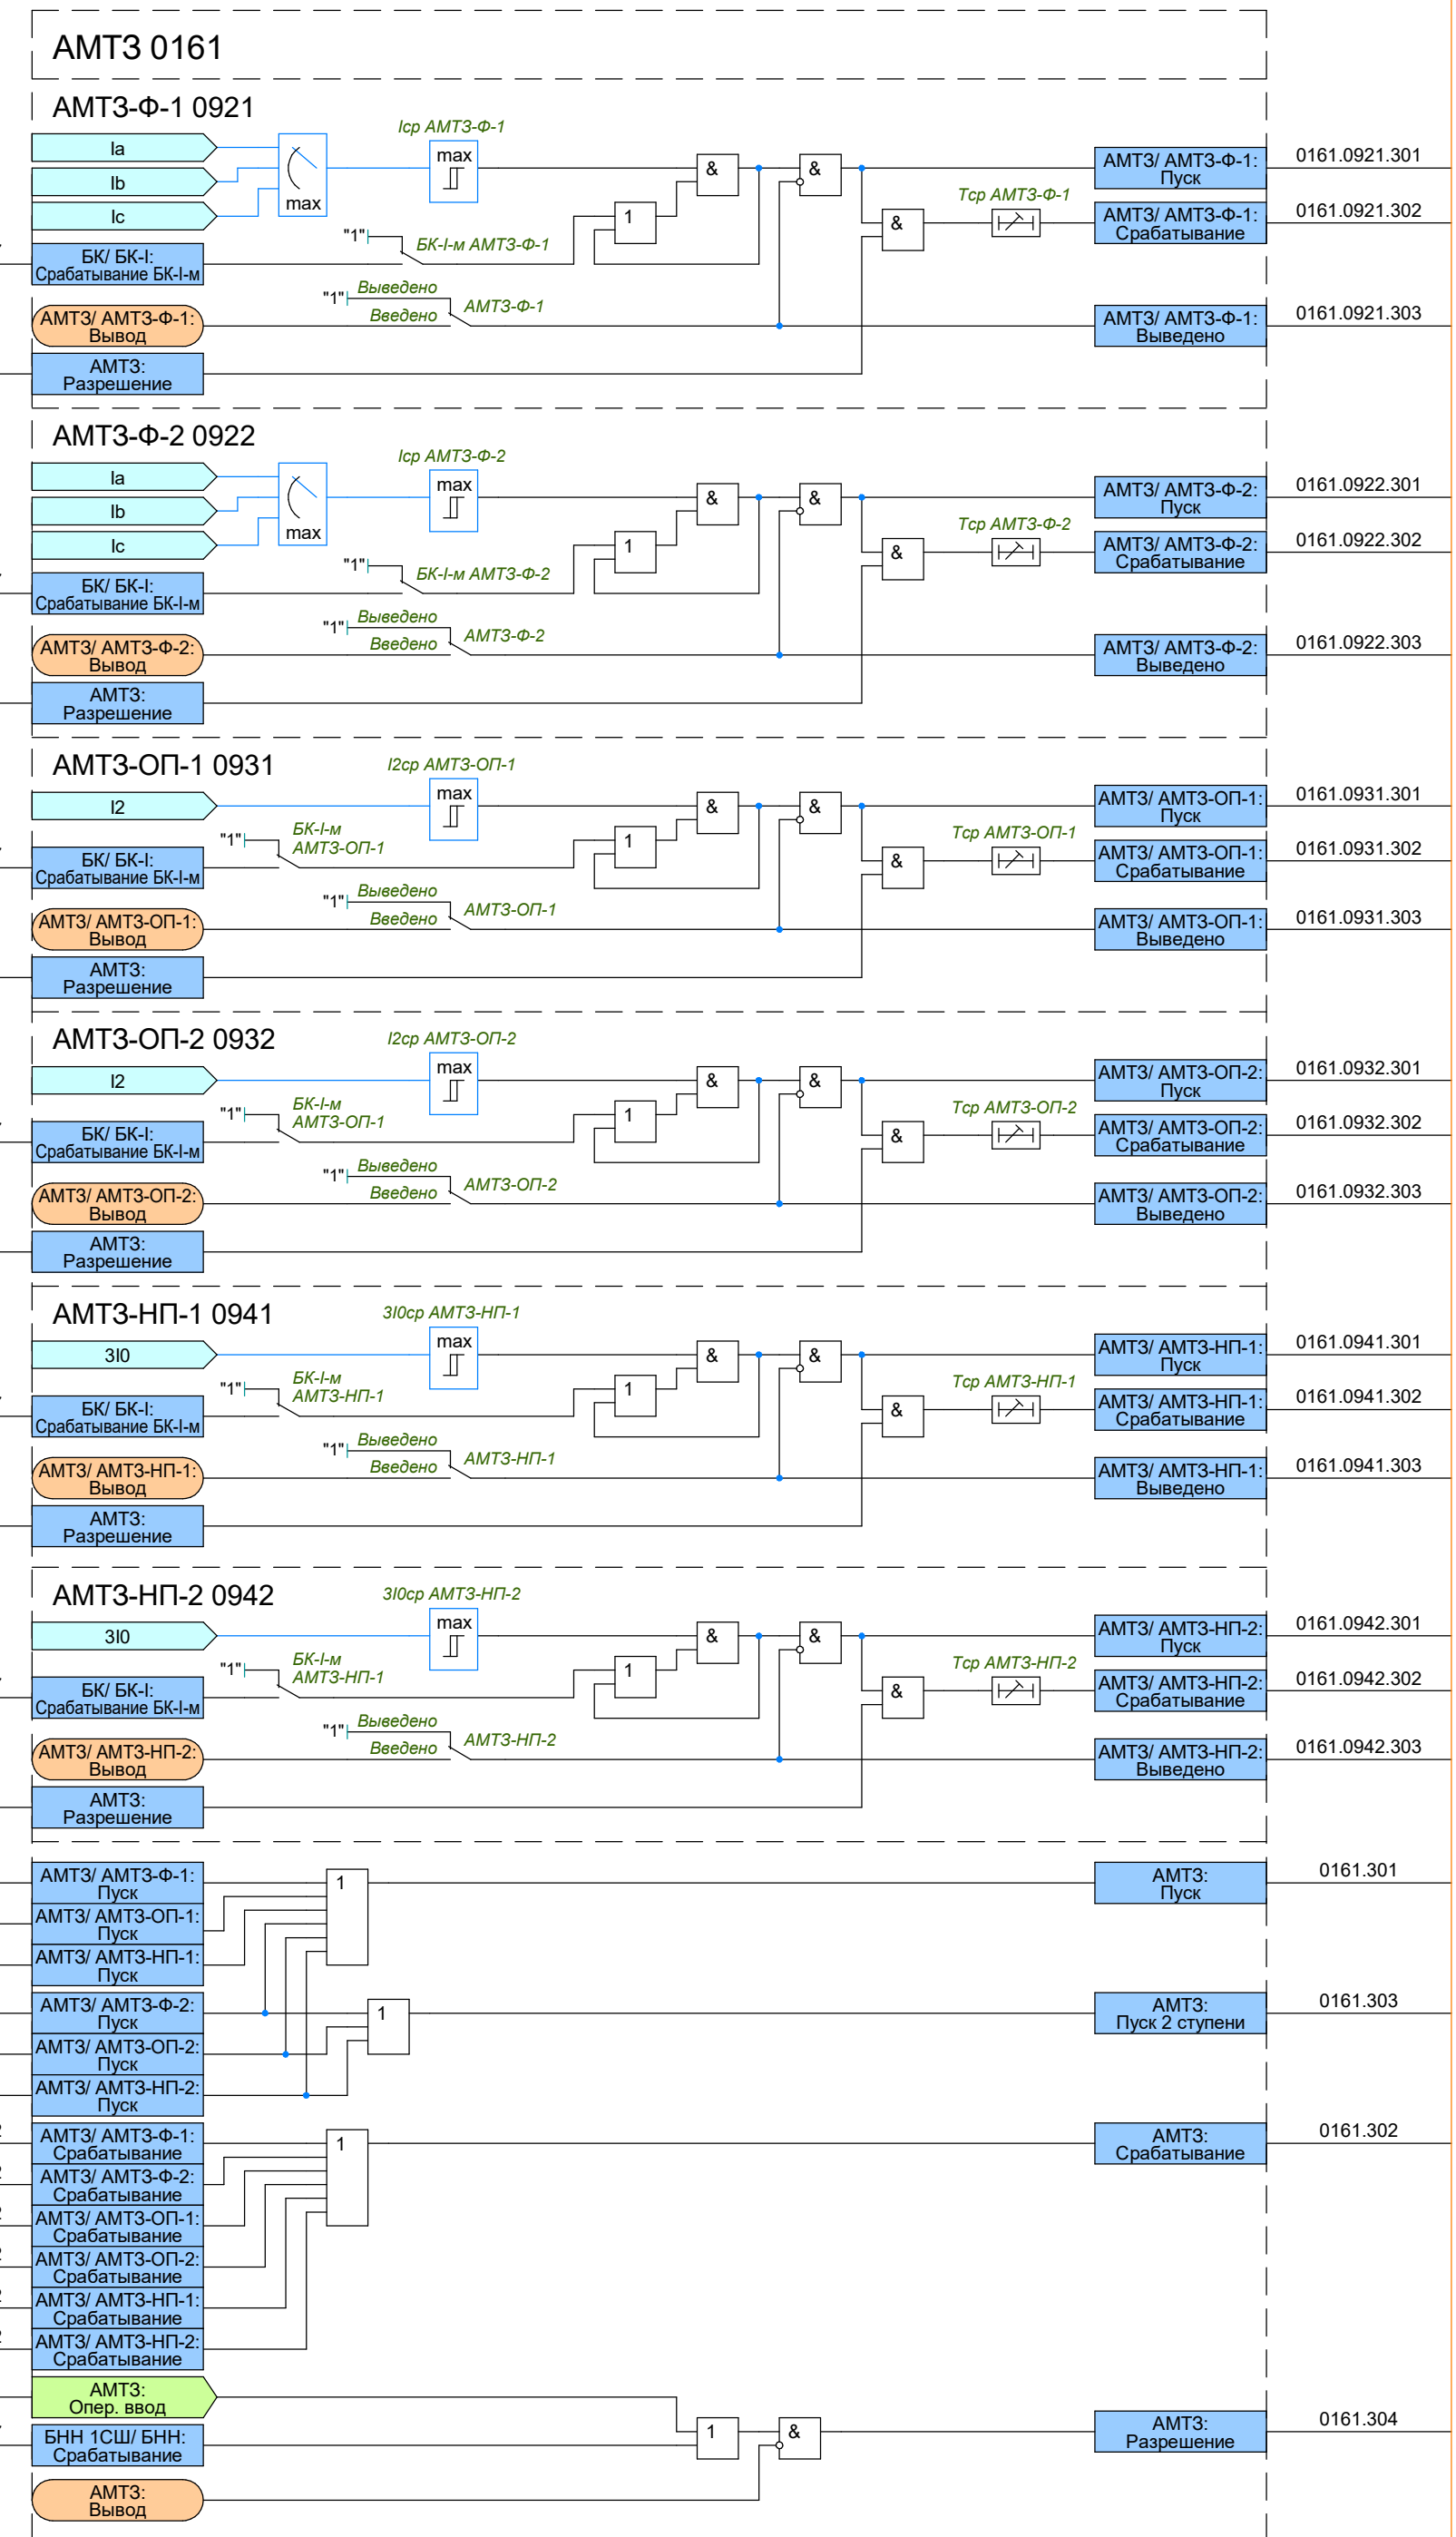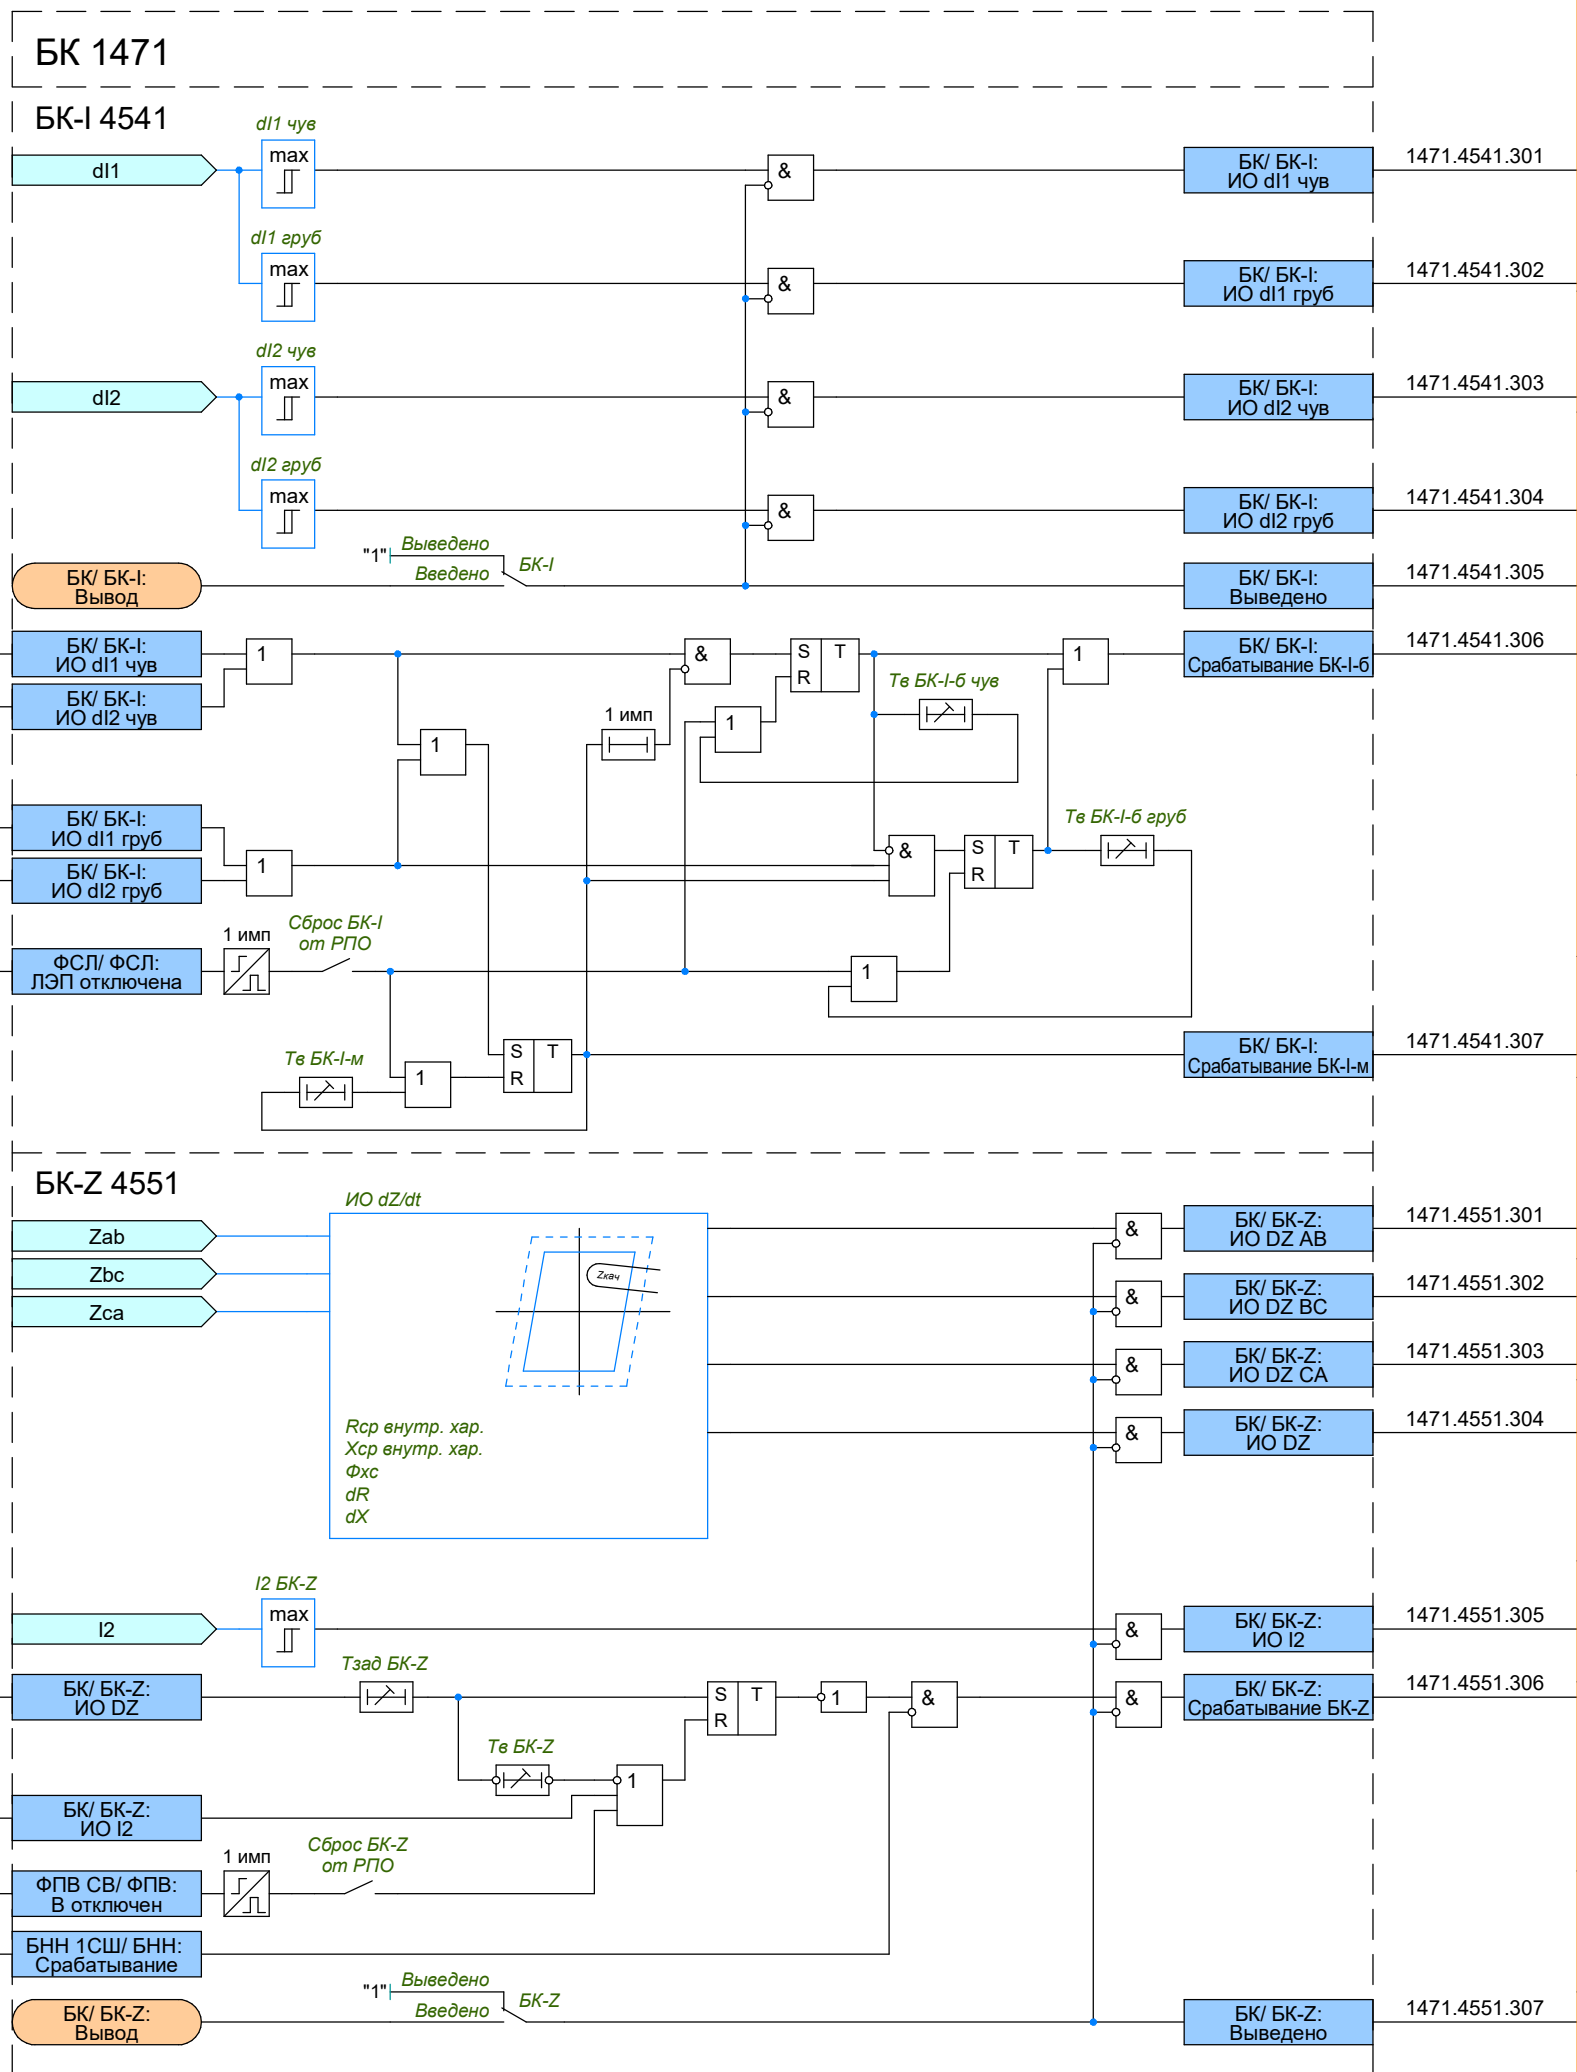

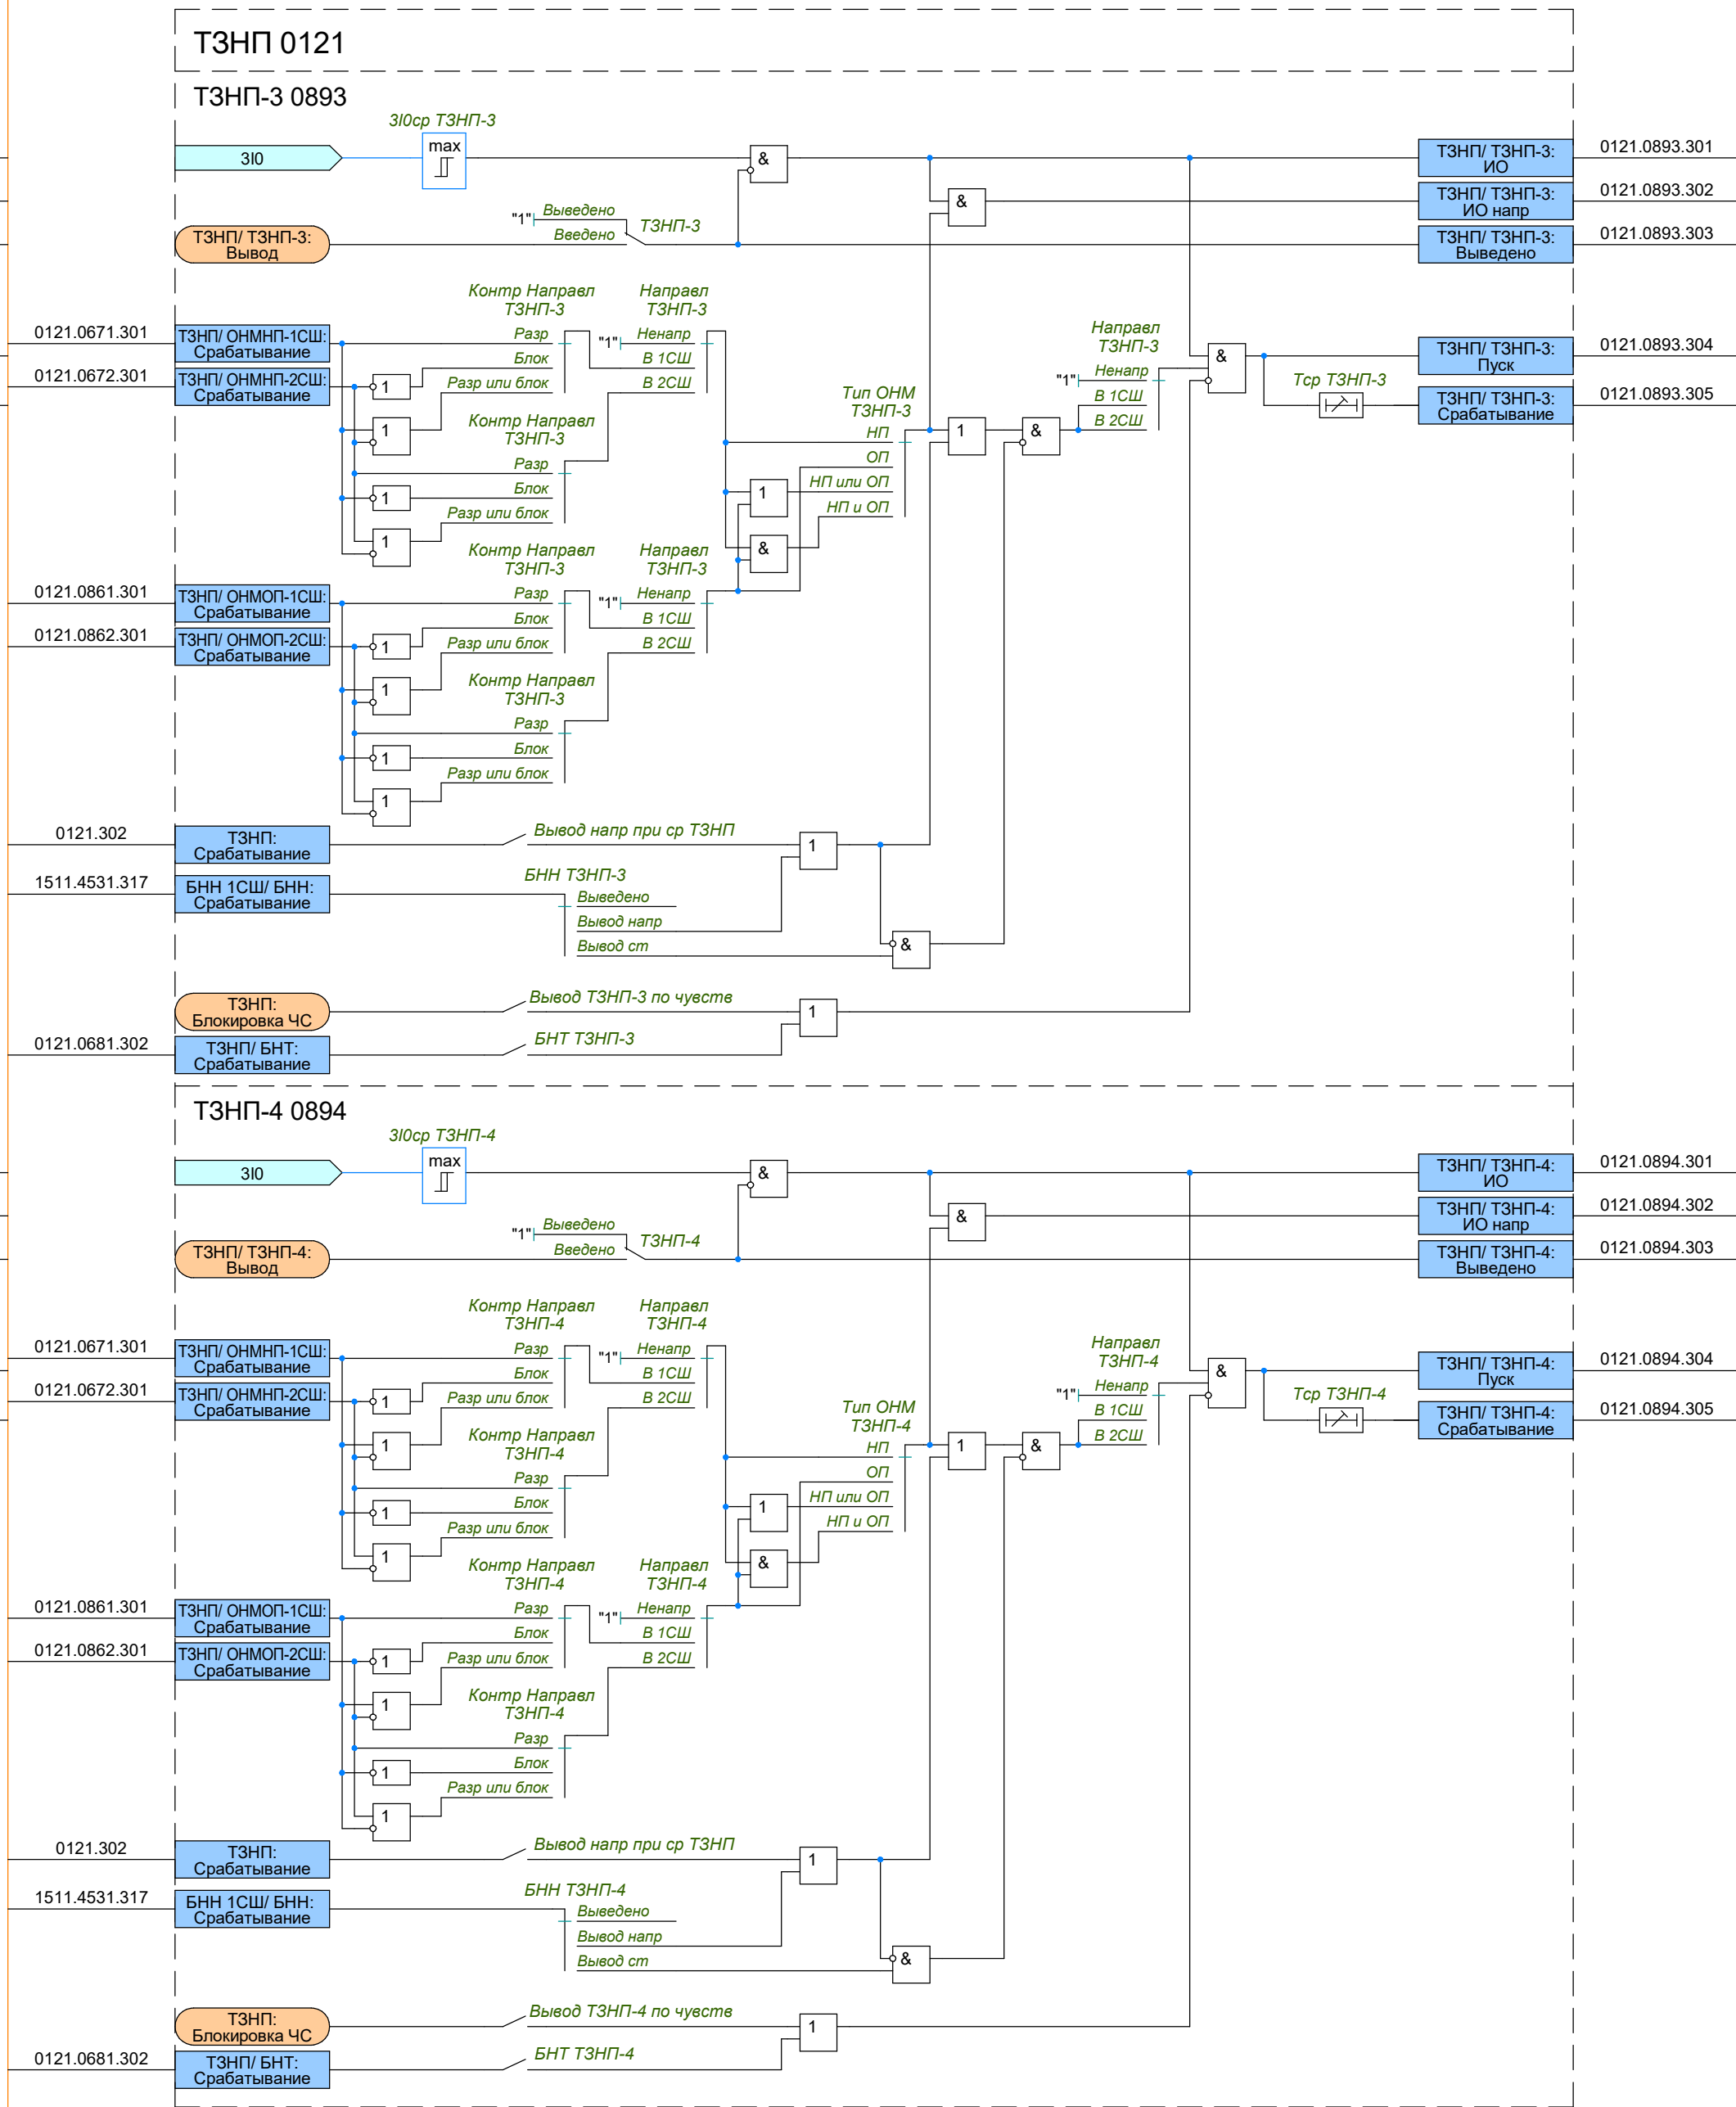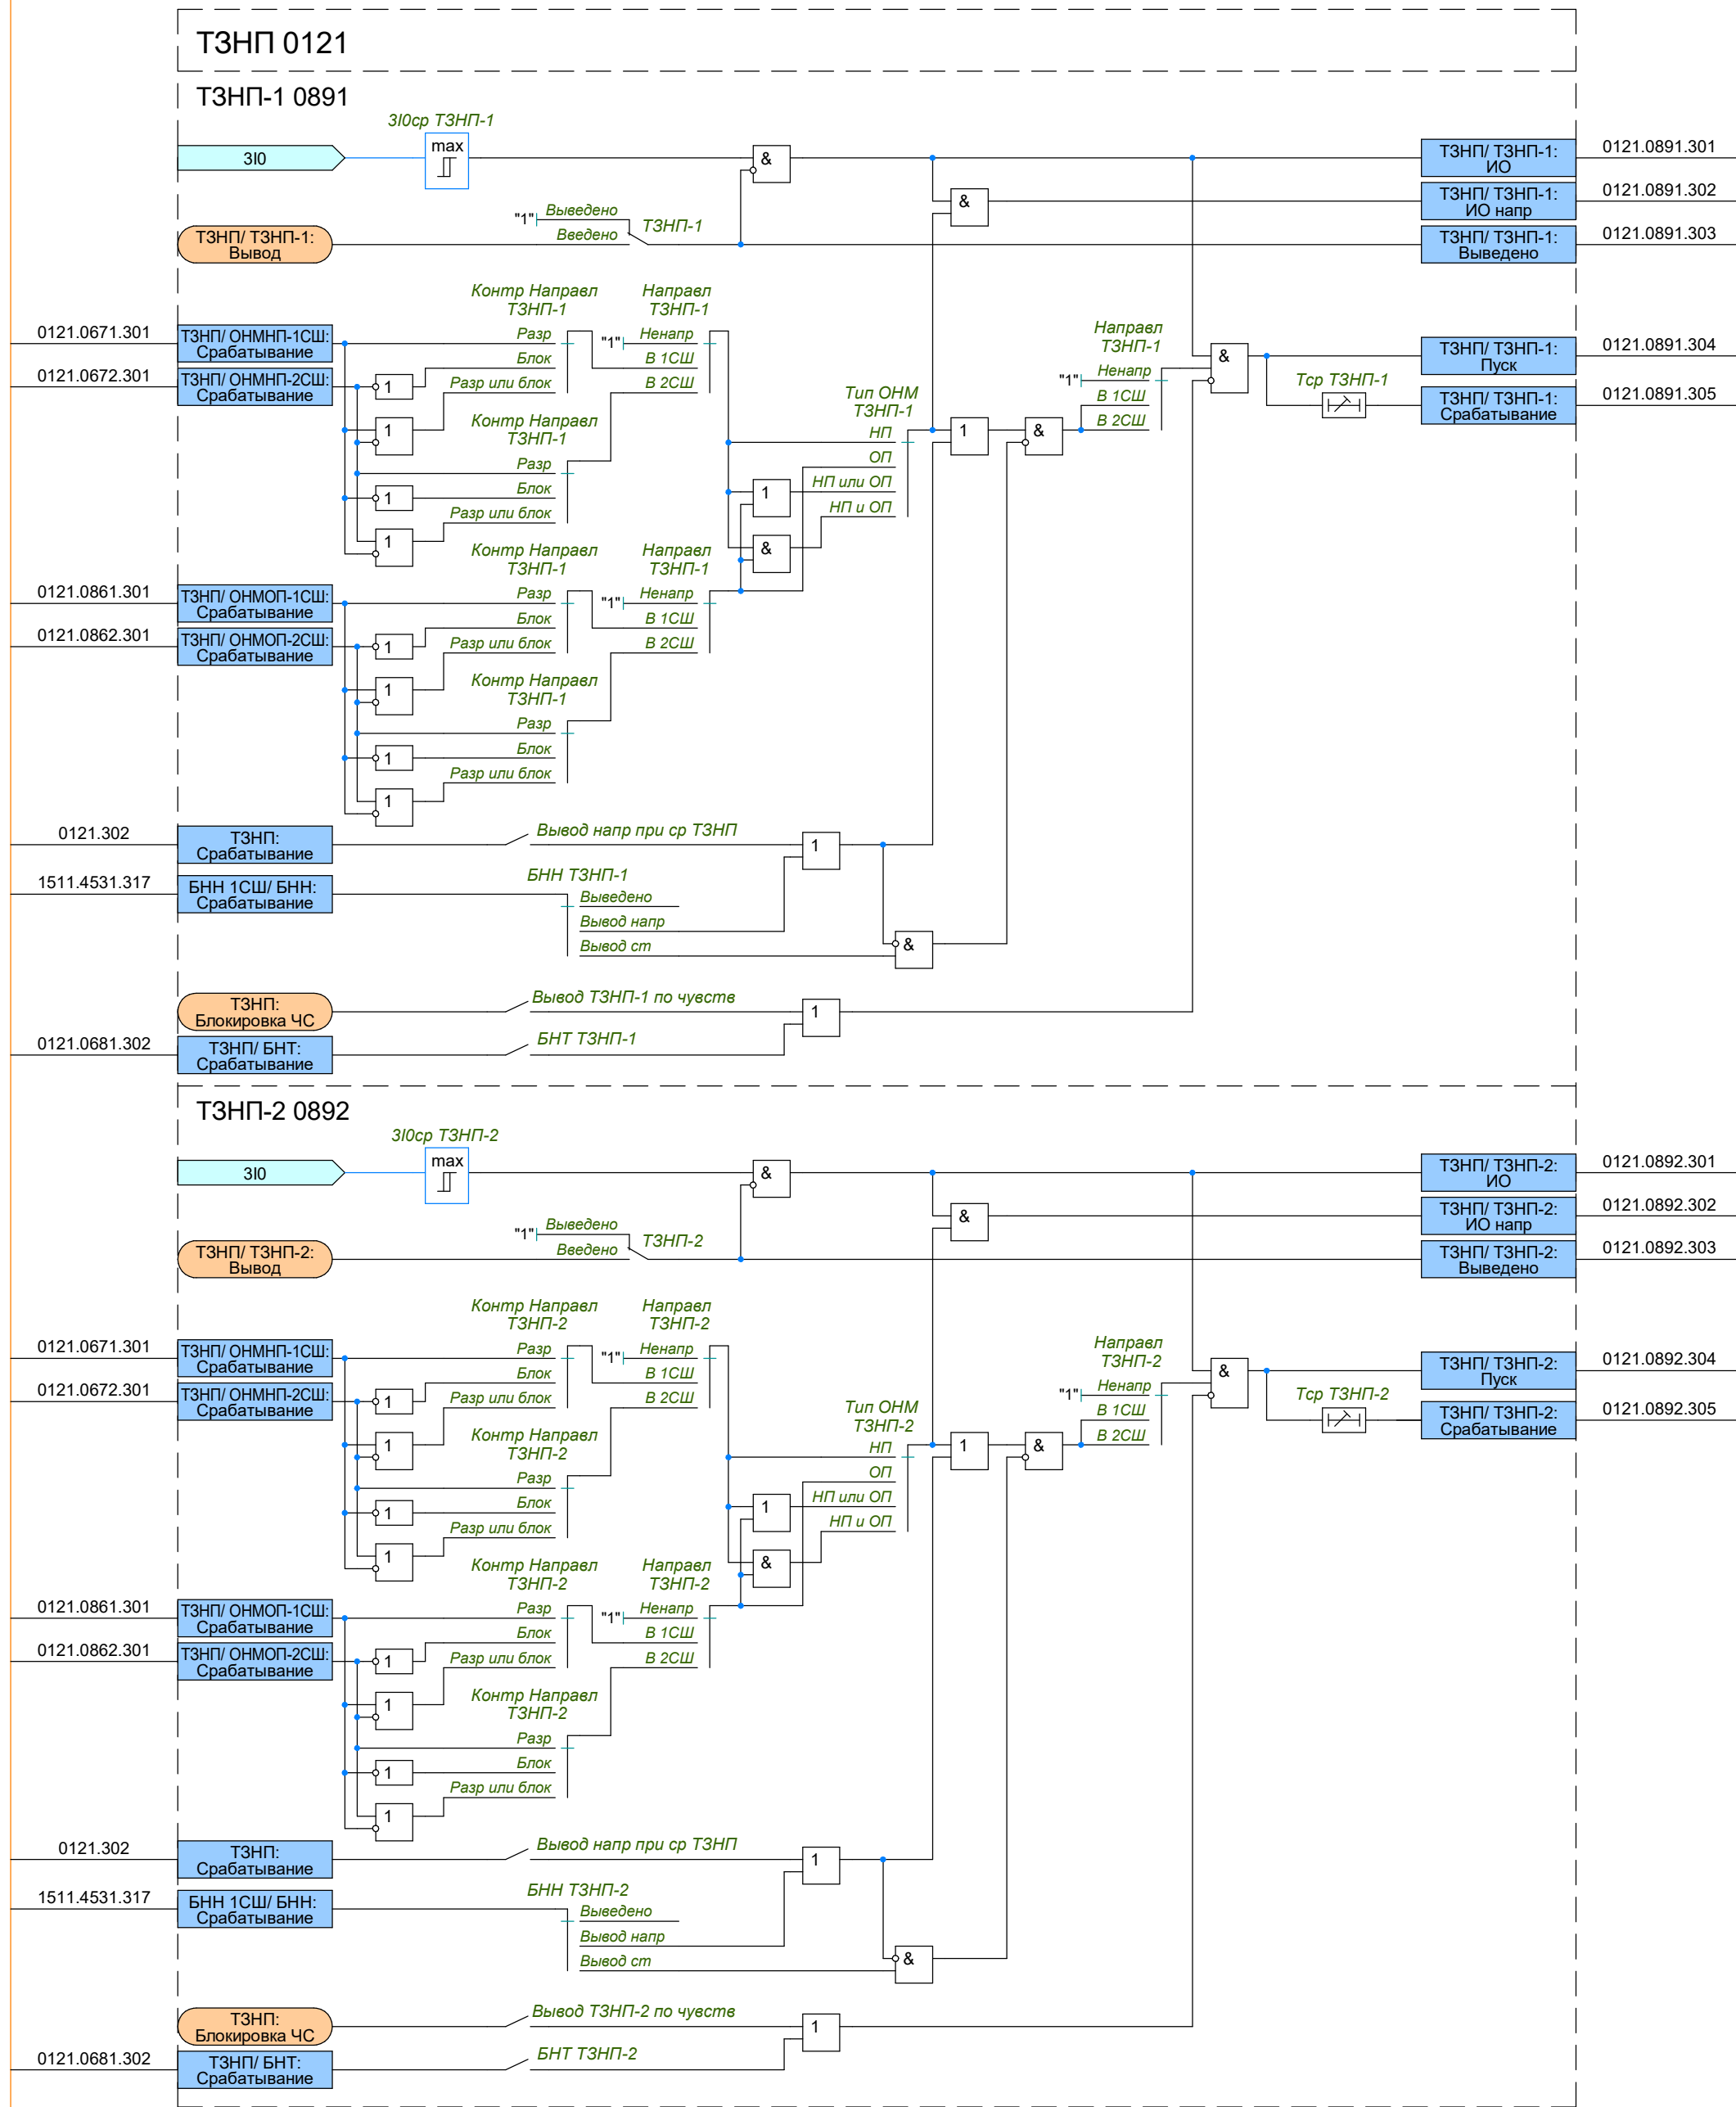


ТЗНП 0121


ОУ1 ТЗНП 0751

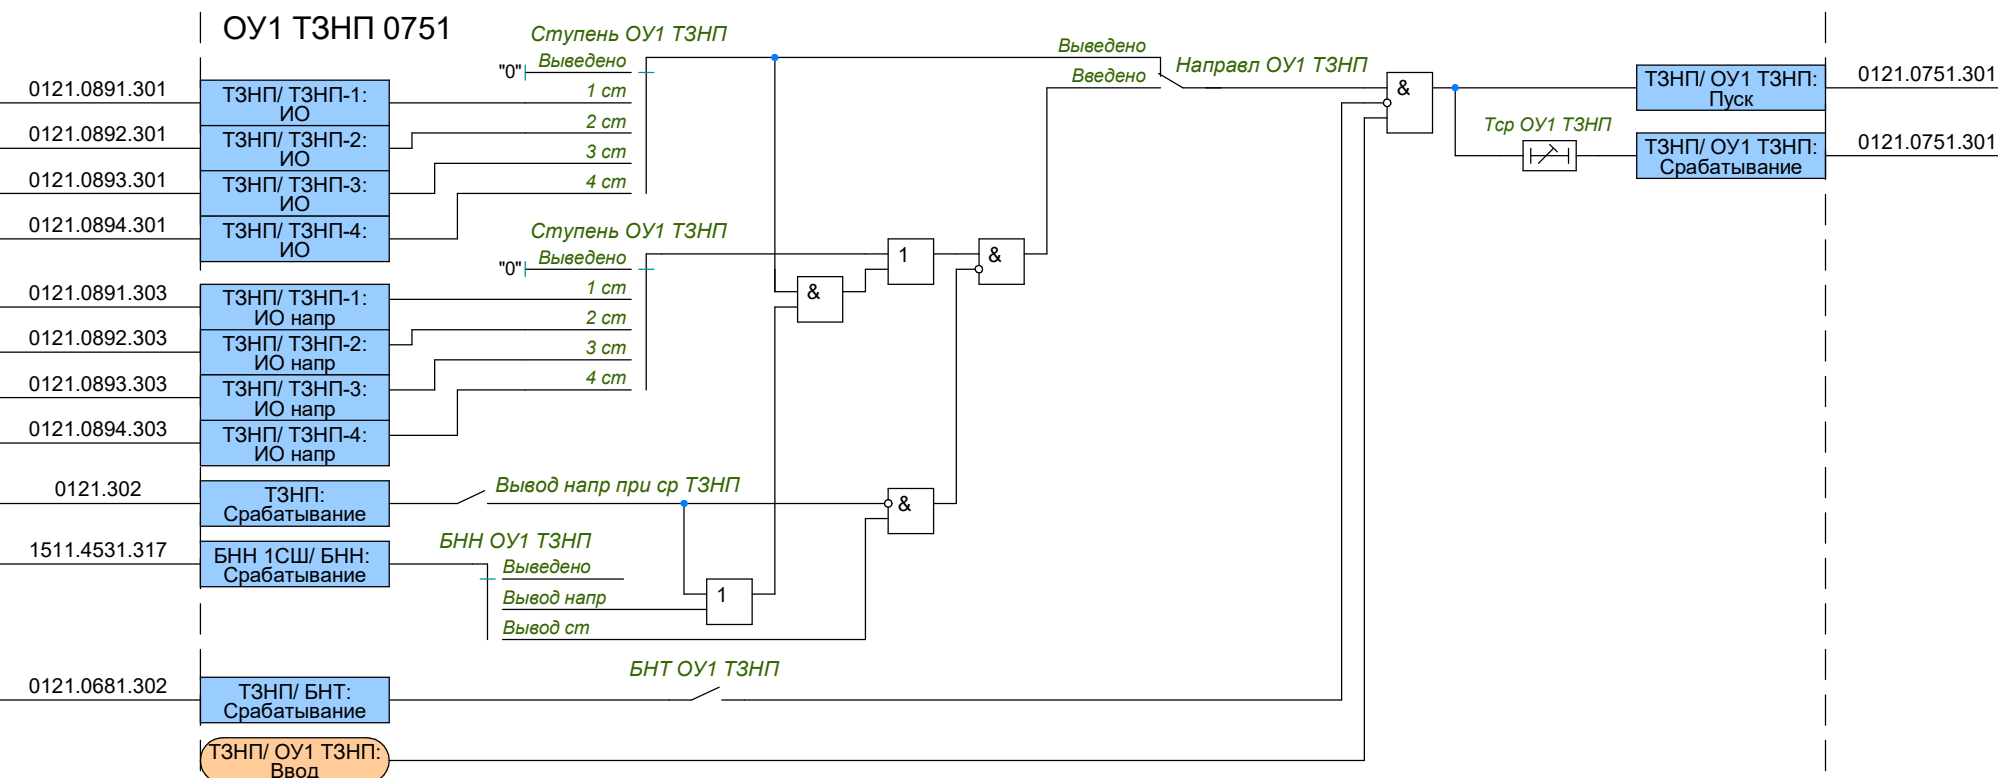

ОУ2 ТЗНП 0752

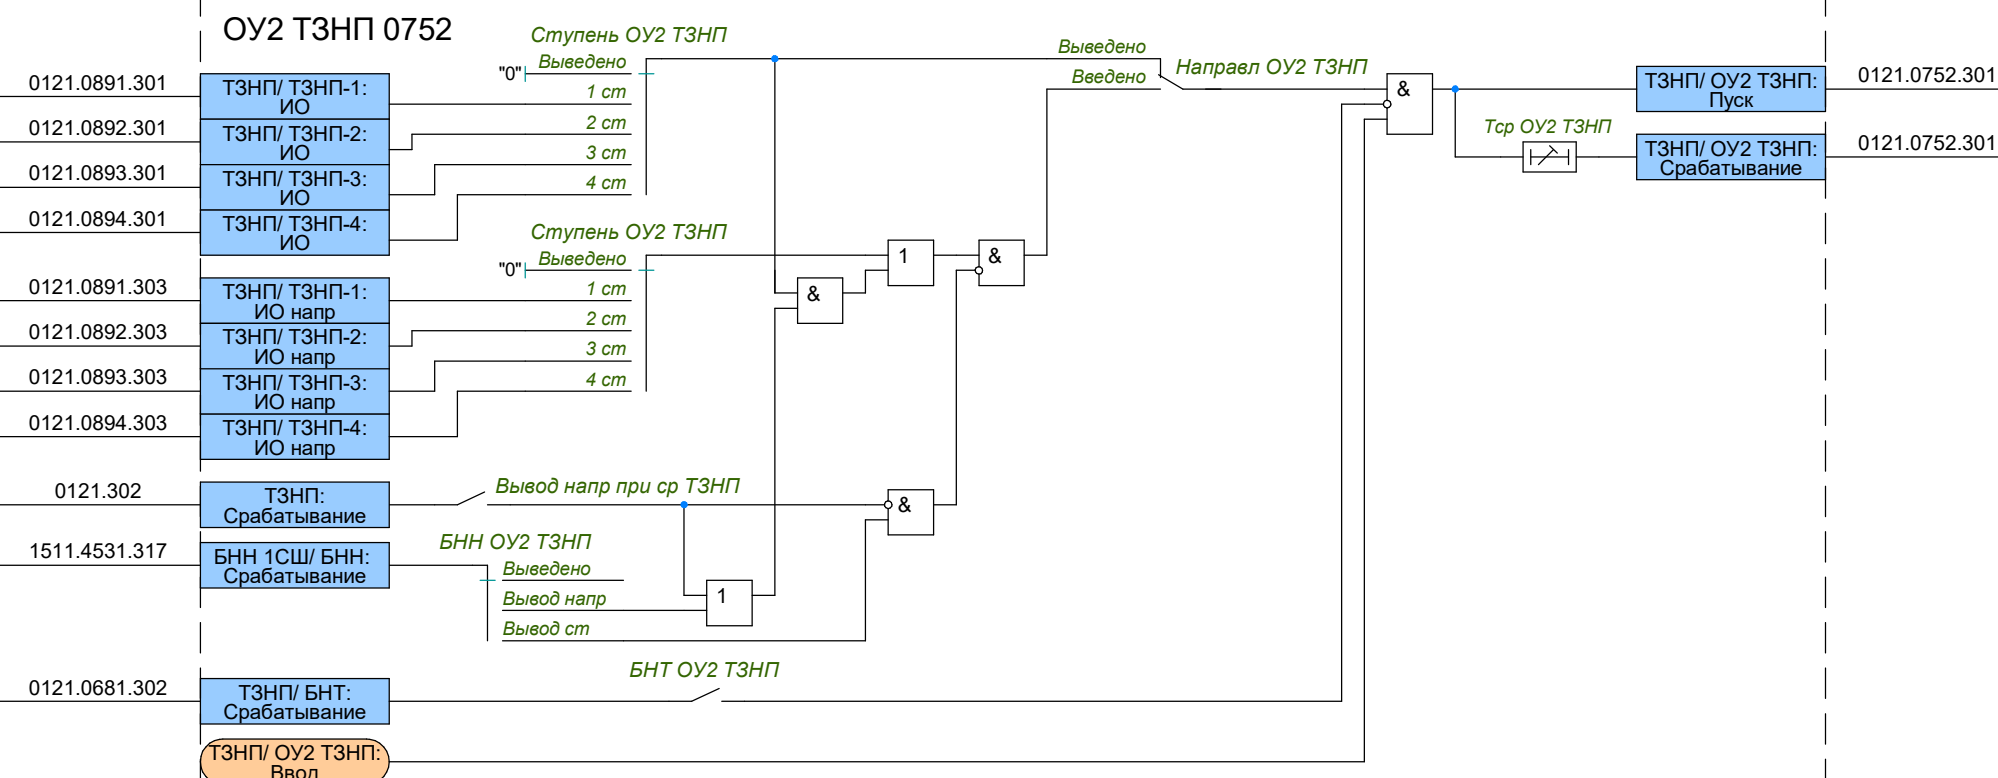


АУ ТЗНП 0541

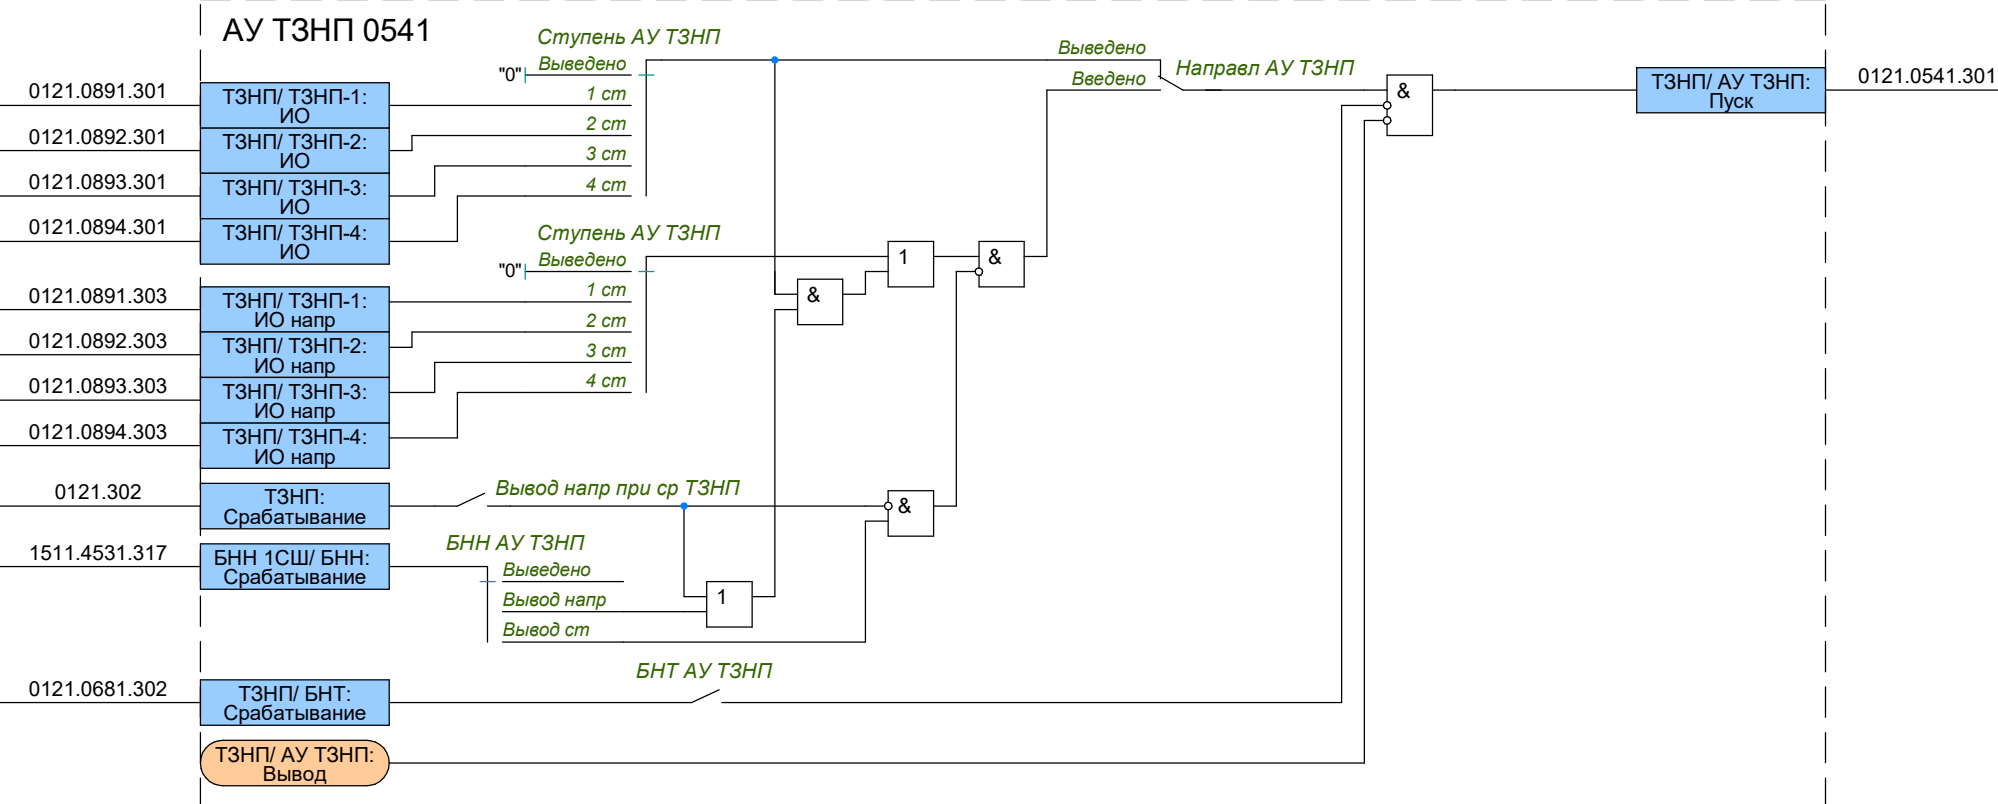


ТЗНП 0121


ОНМНП-1СШ 0671

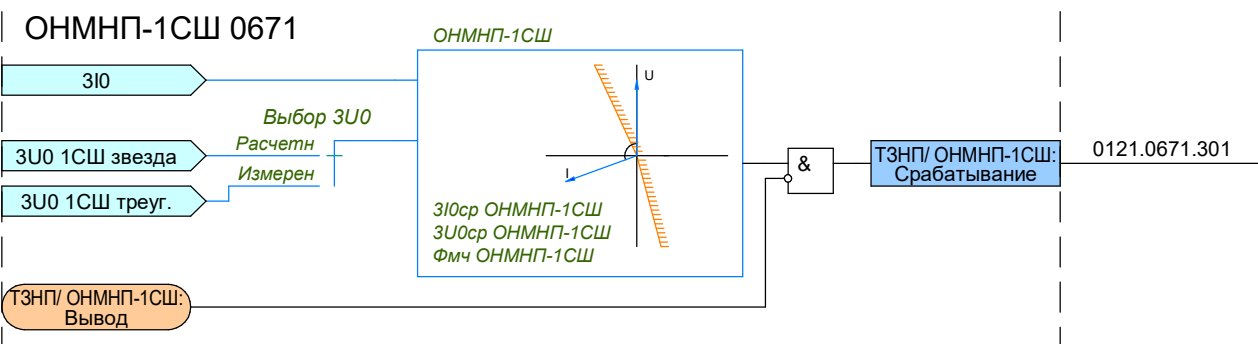


ОНМНП-2СШ 0672

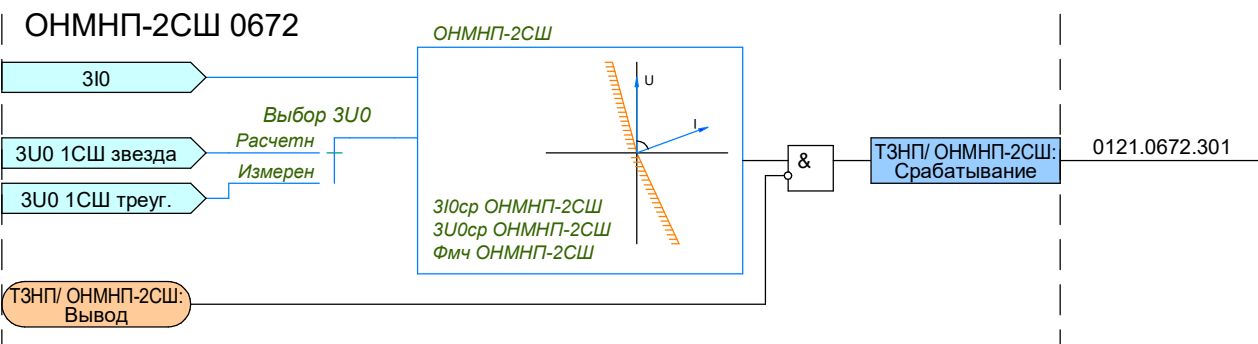



ОНМОП-1СШ 0861

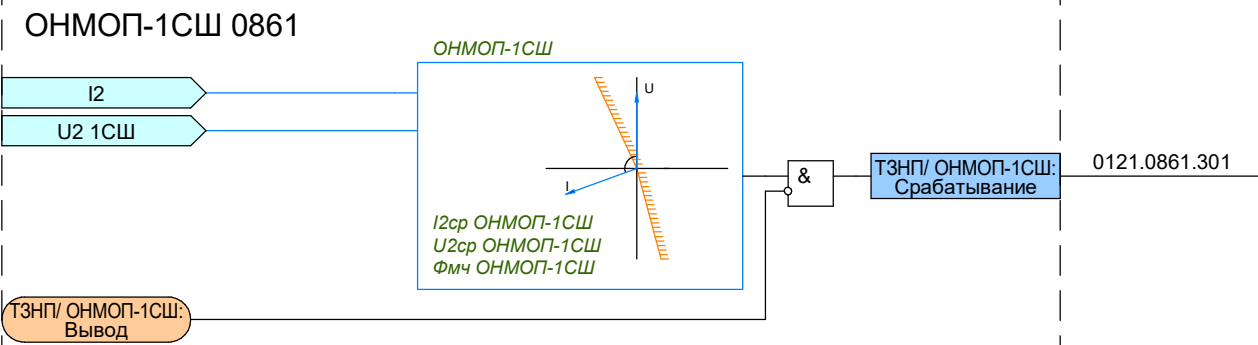

ОНМОП-2СШ 0862

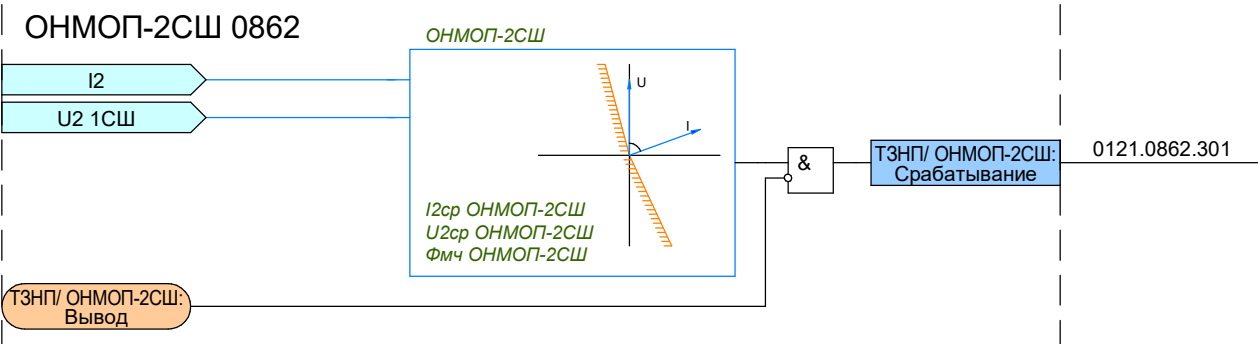


БНТ 0681

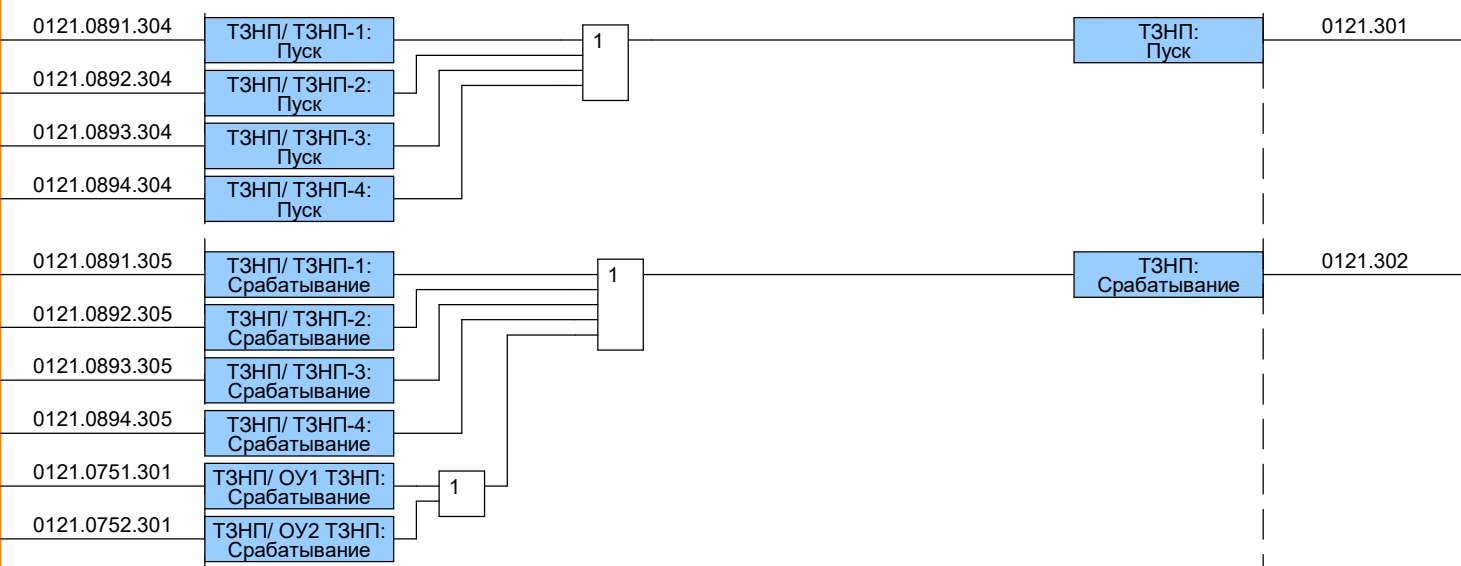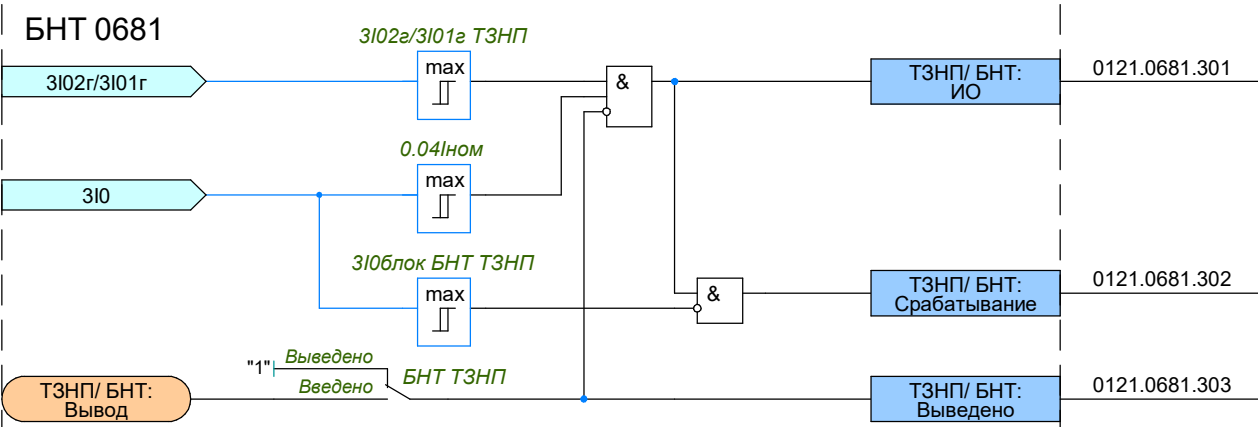


БНН 1СШ 1511


БНН 4531

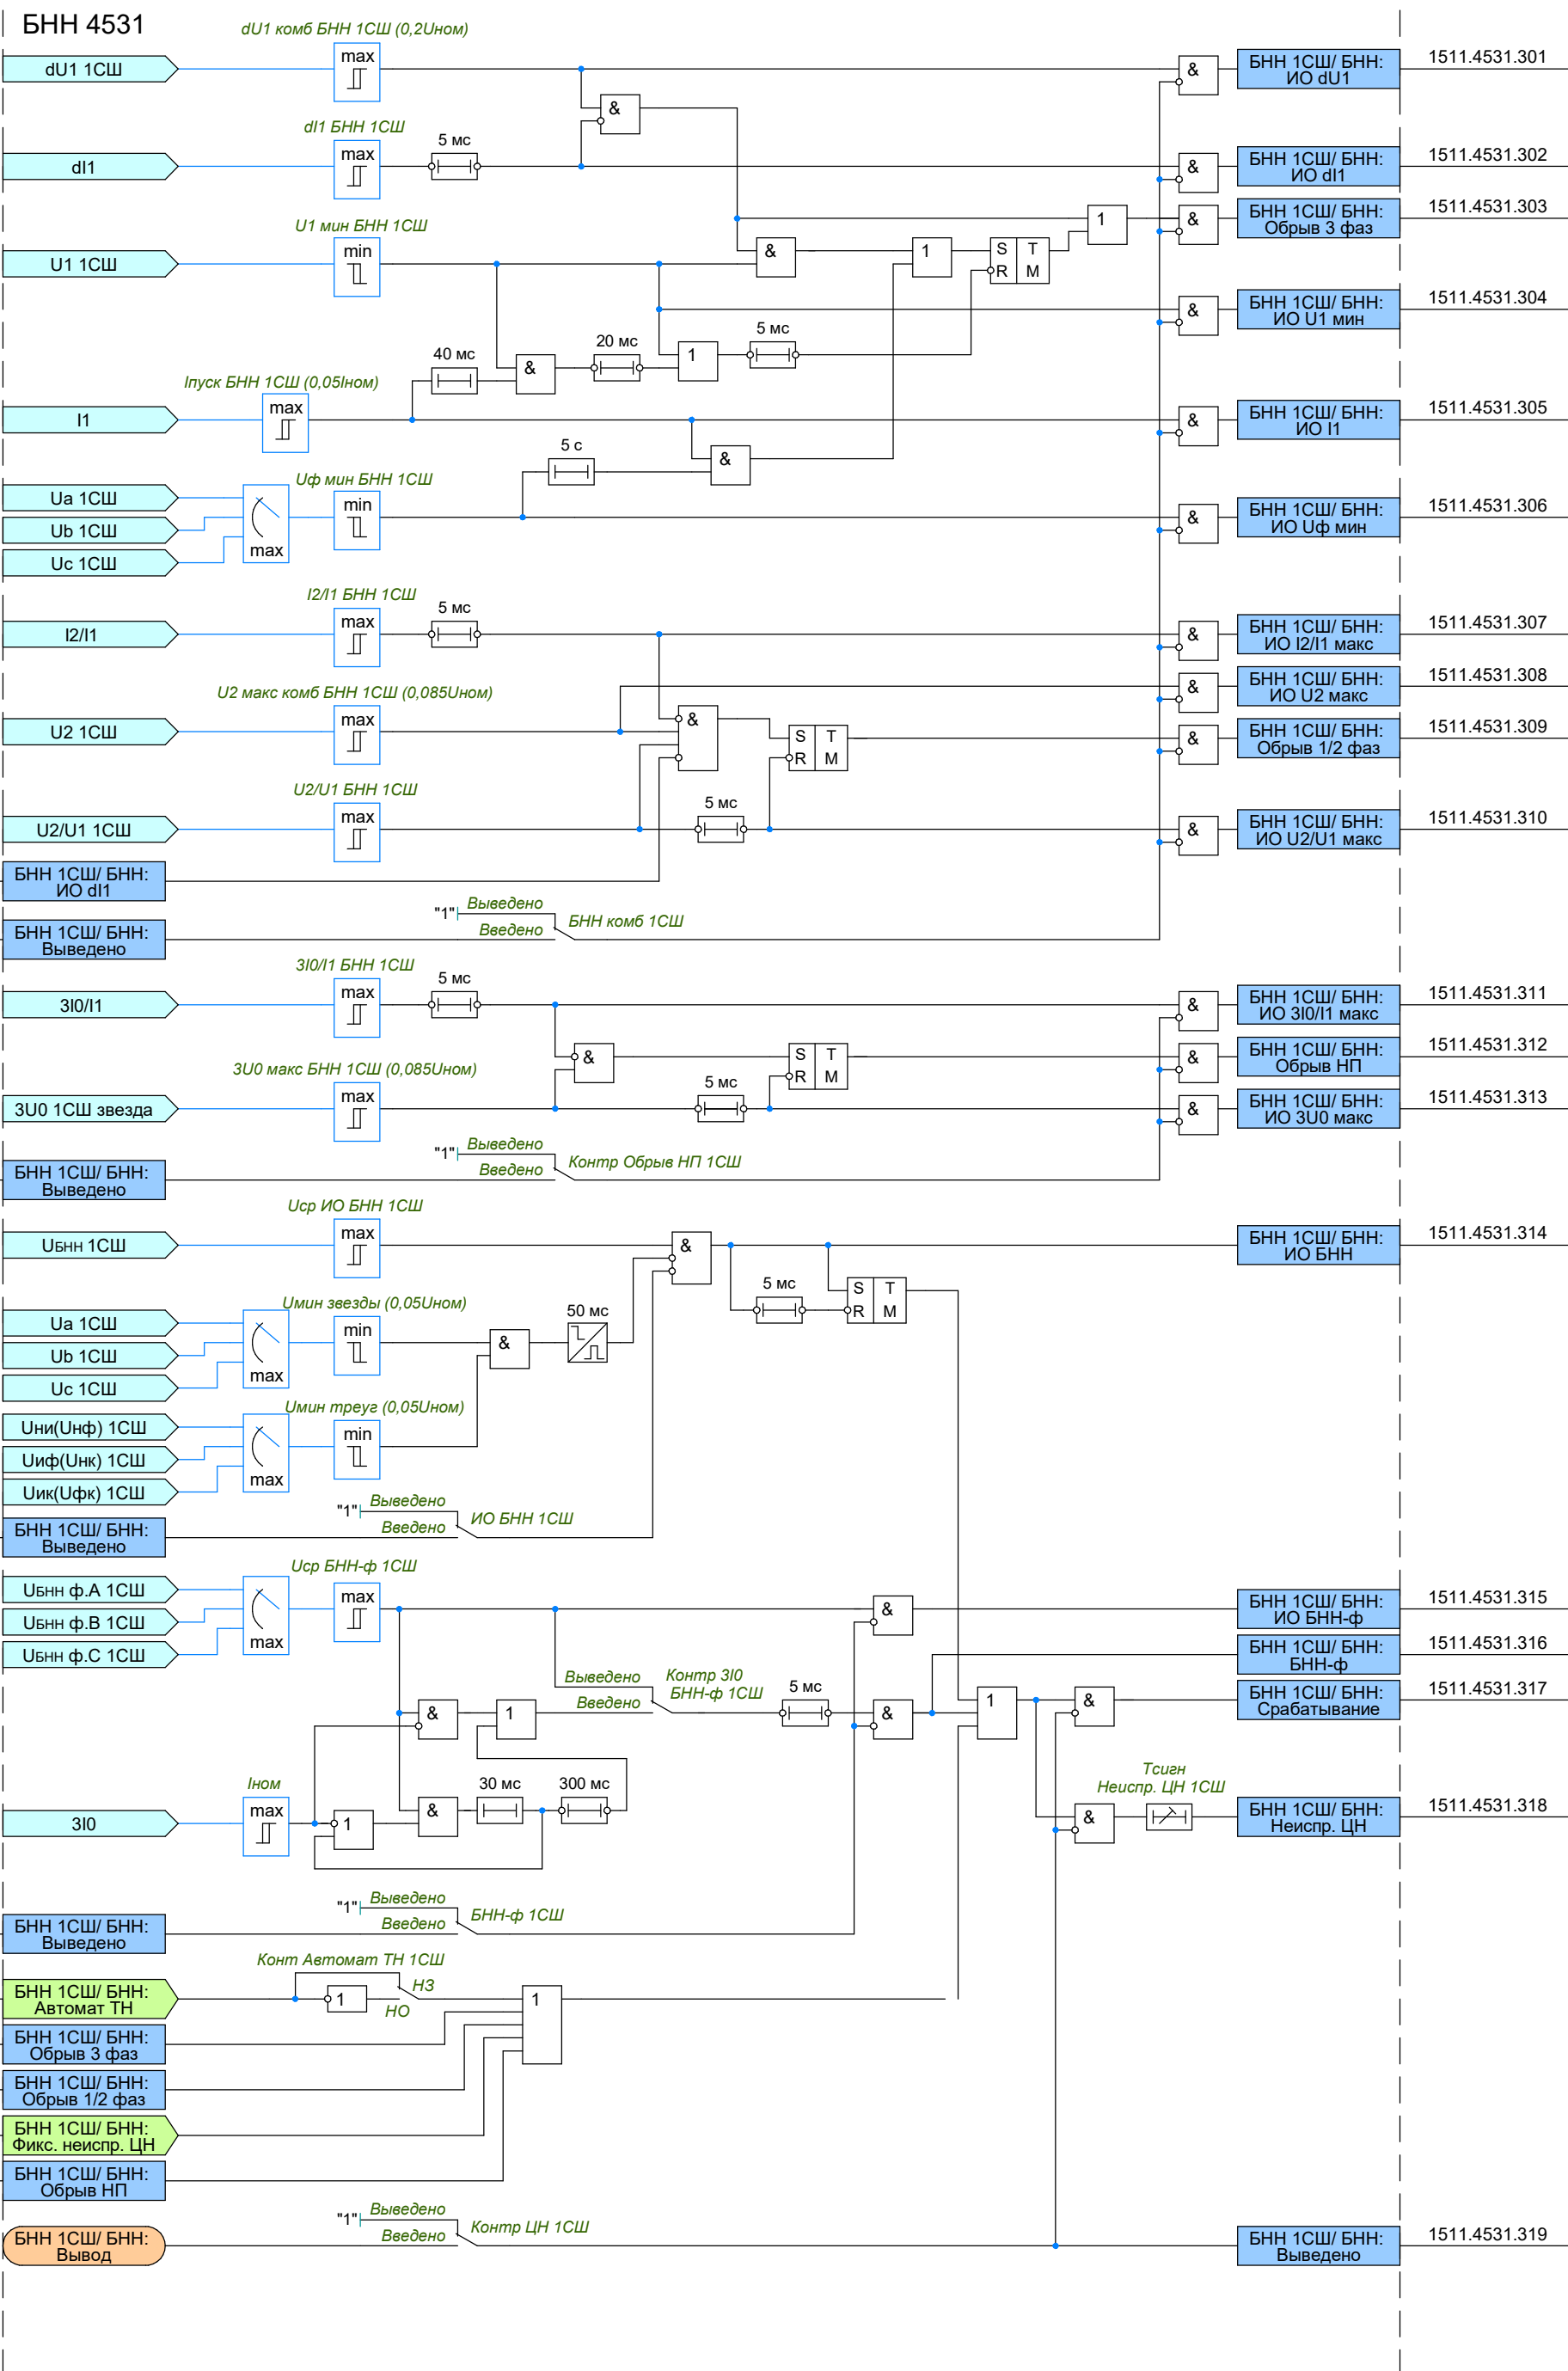

БНН 2СШ 1501


БНН 4571

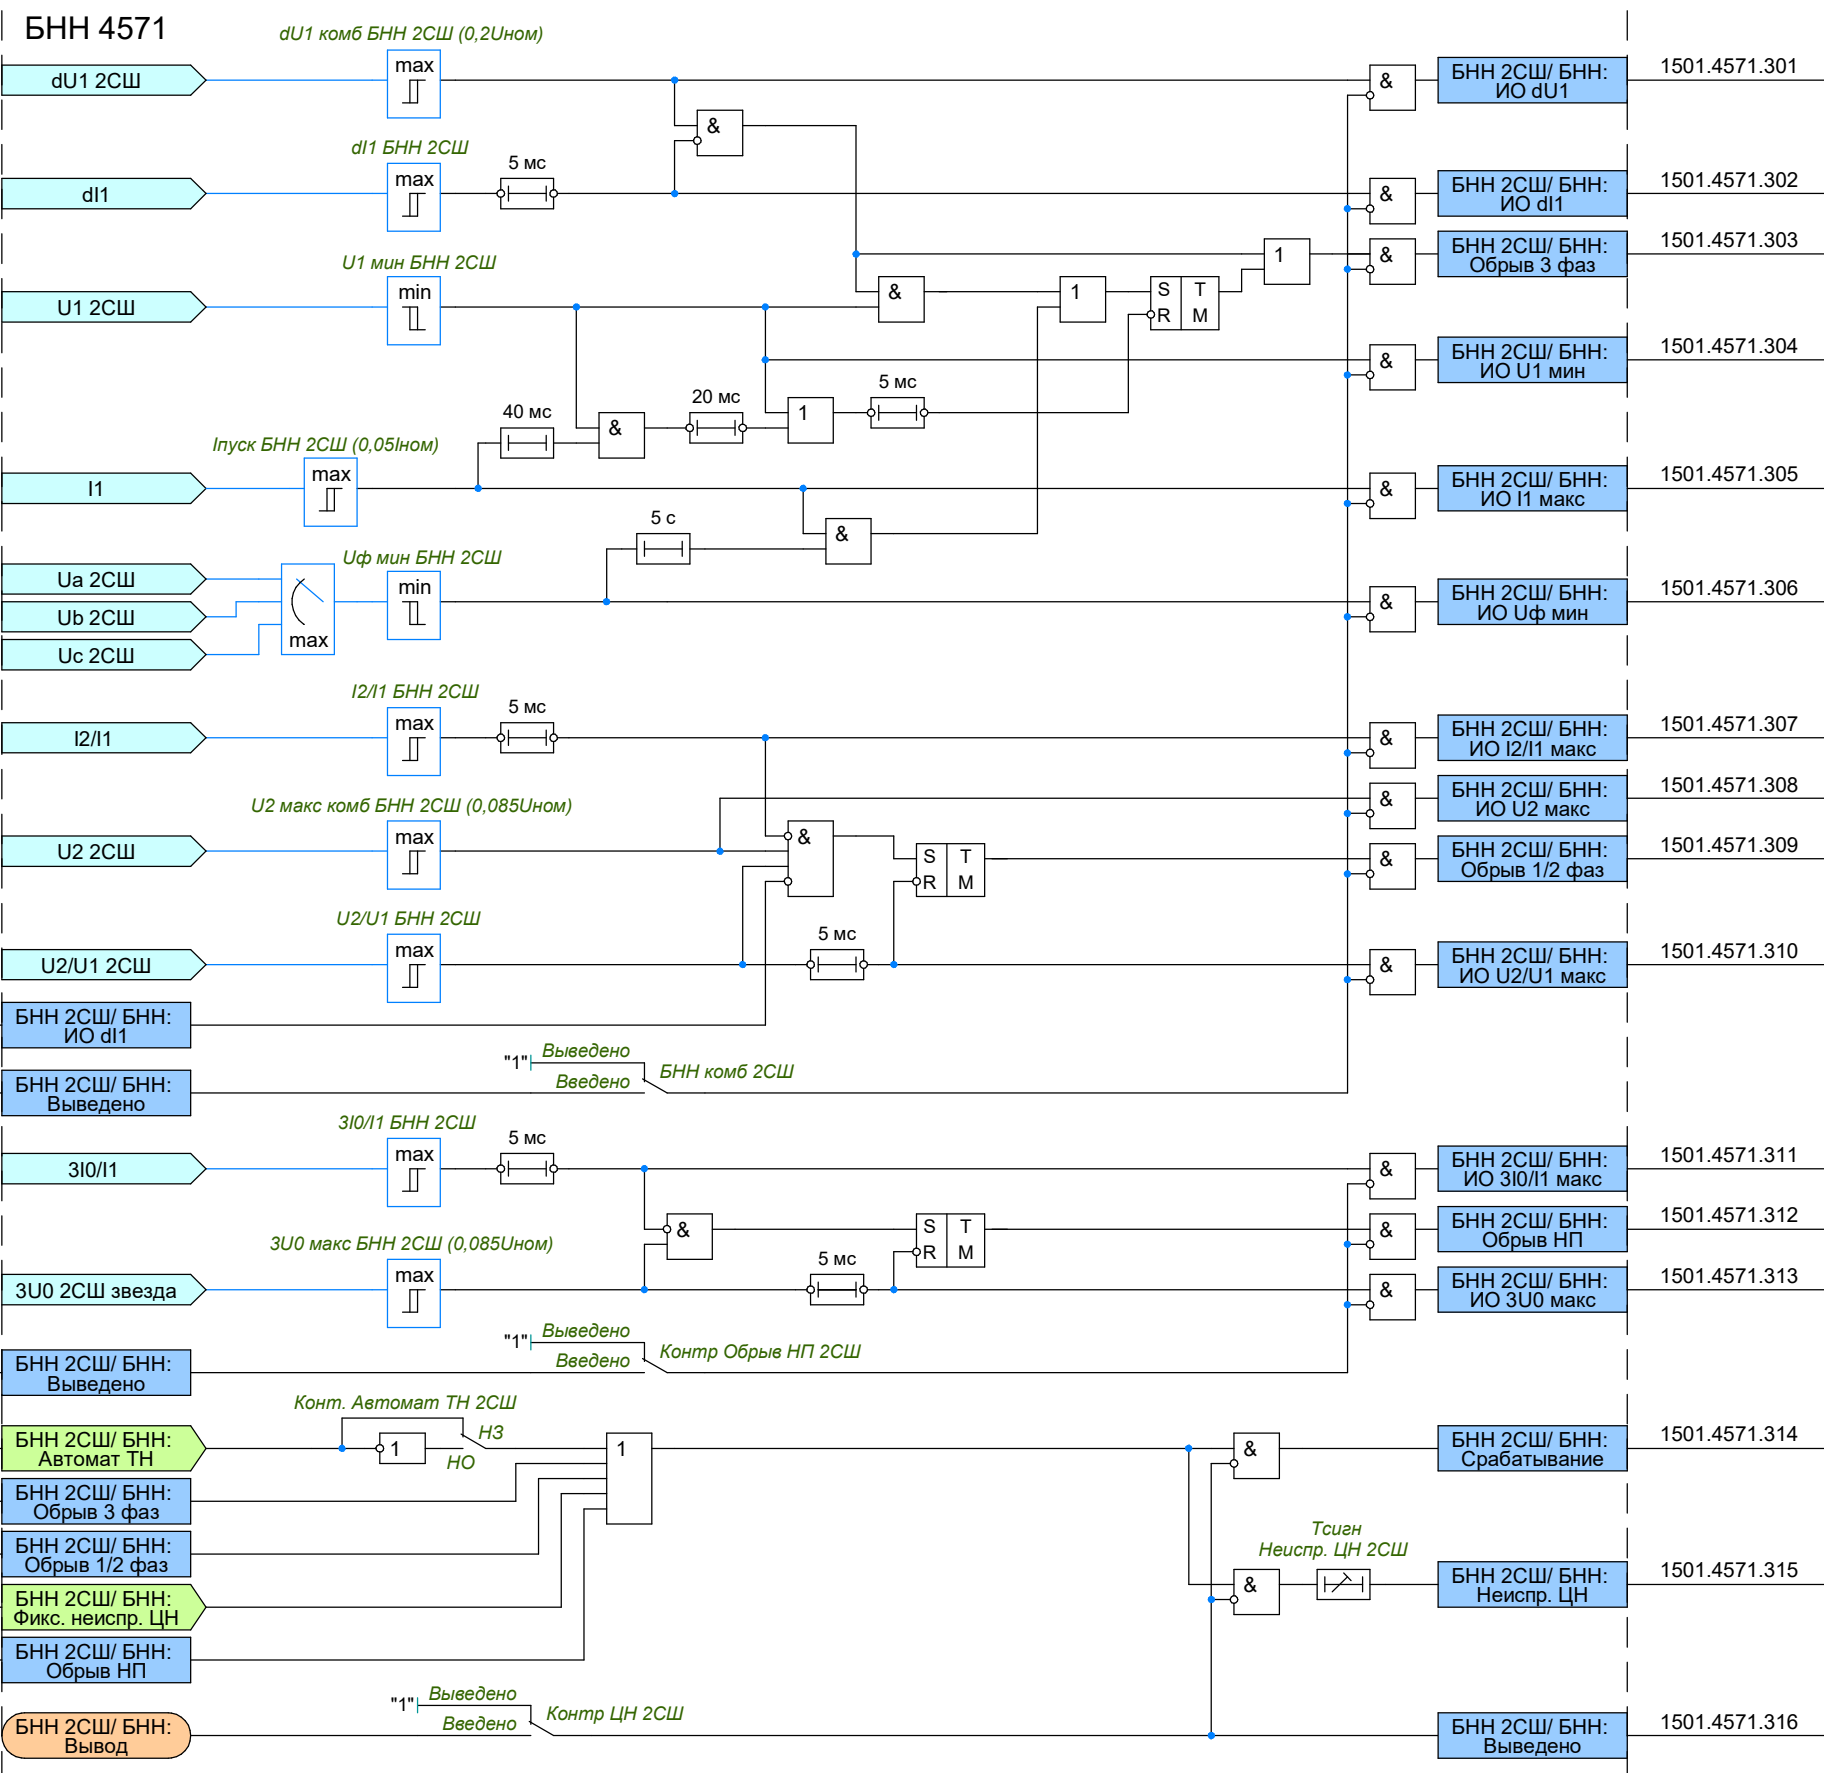

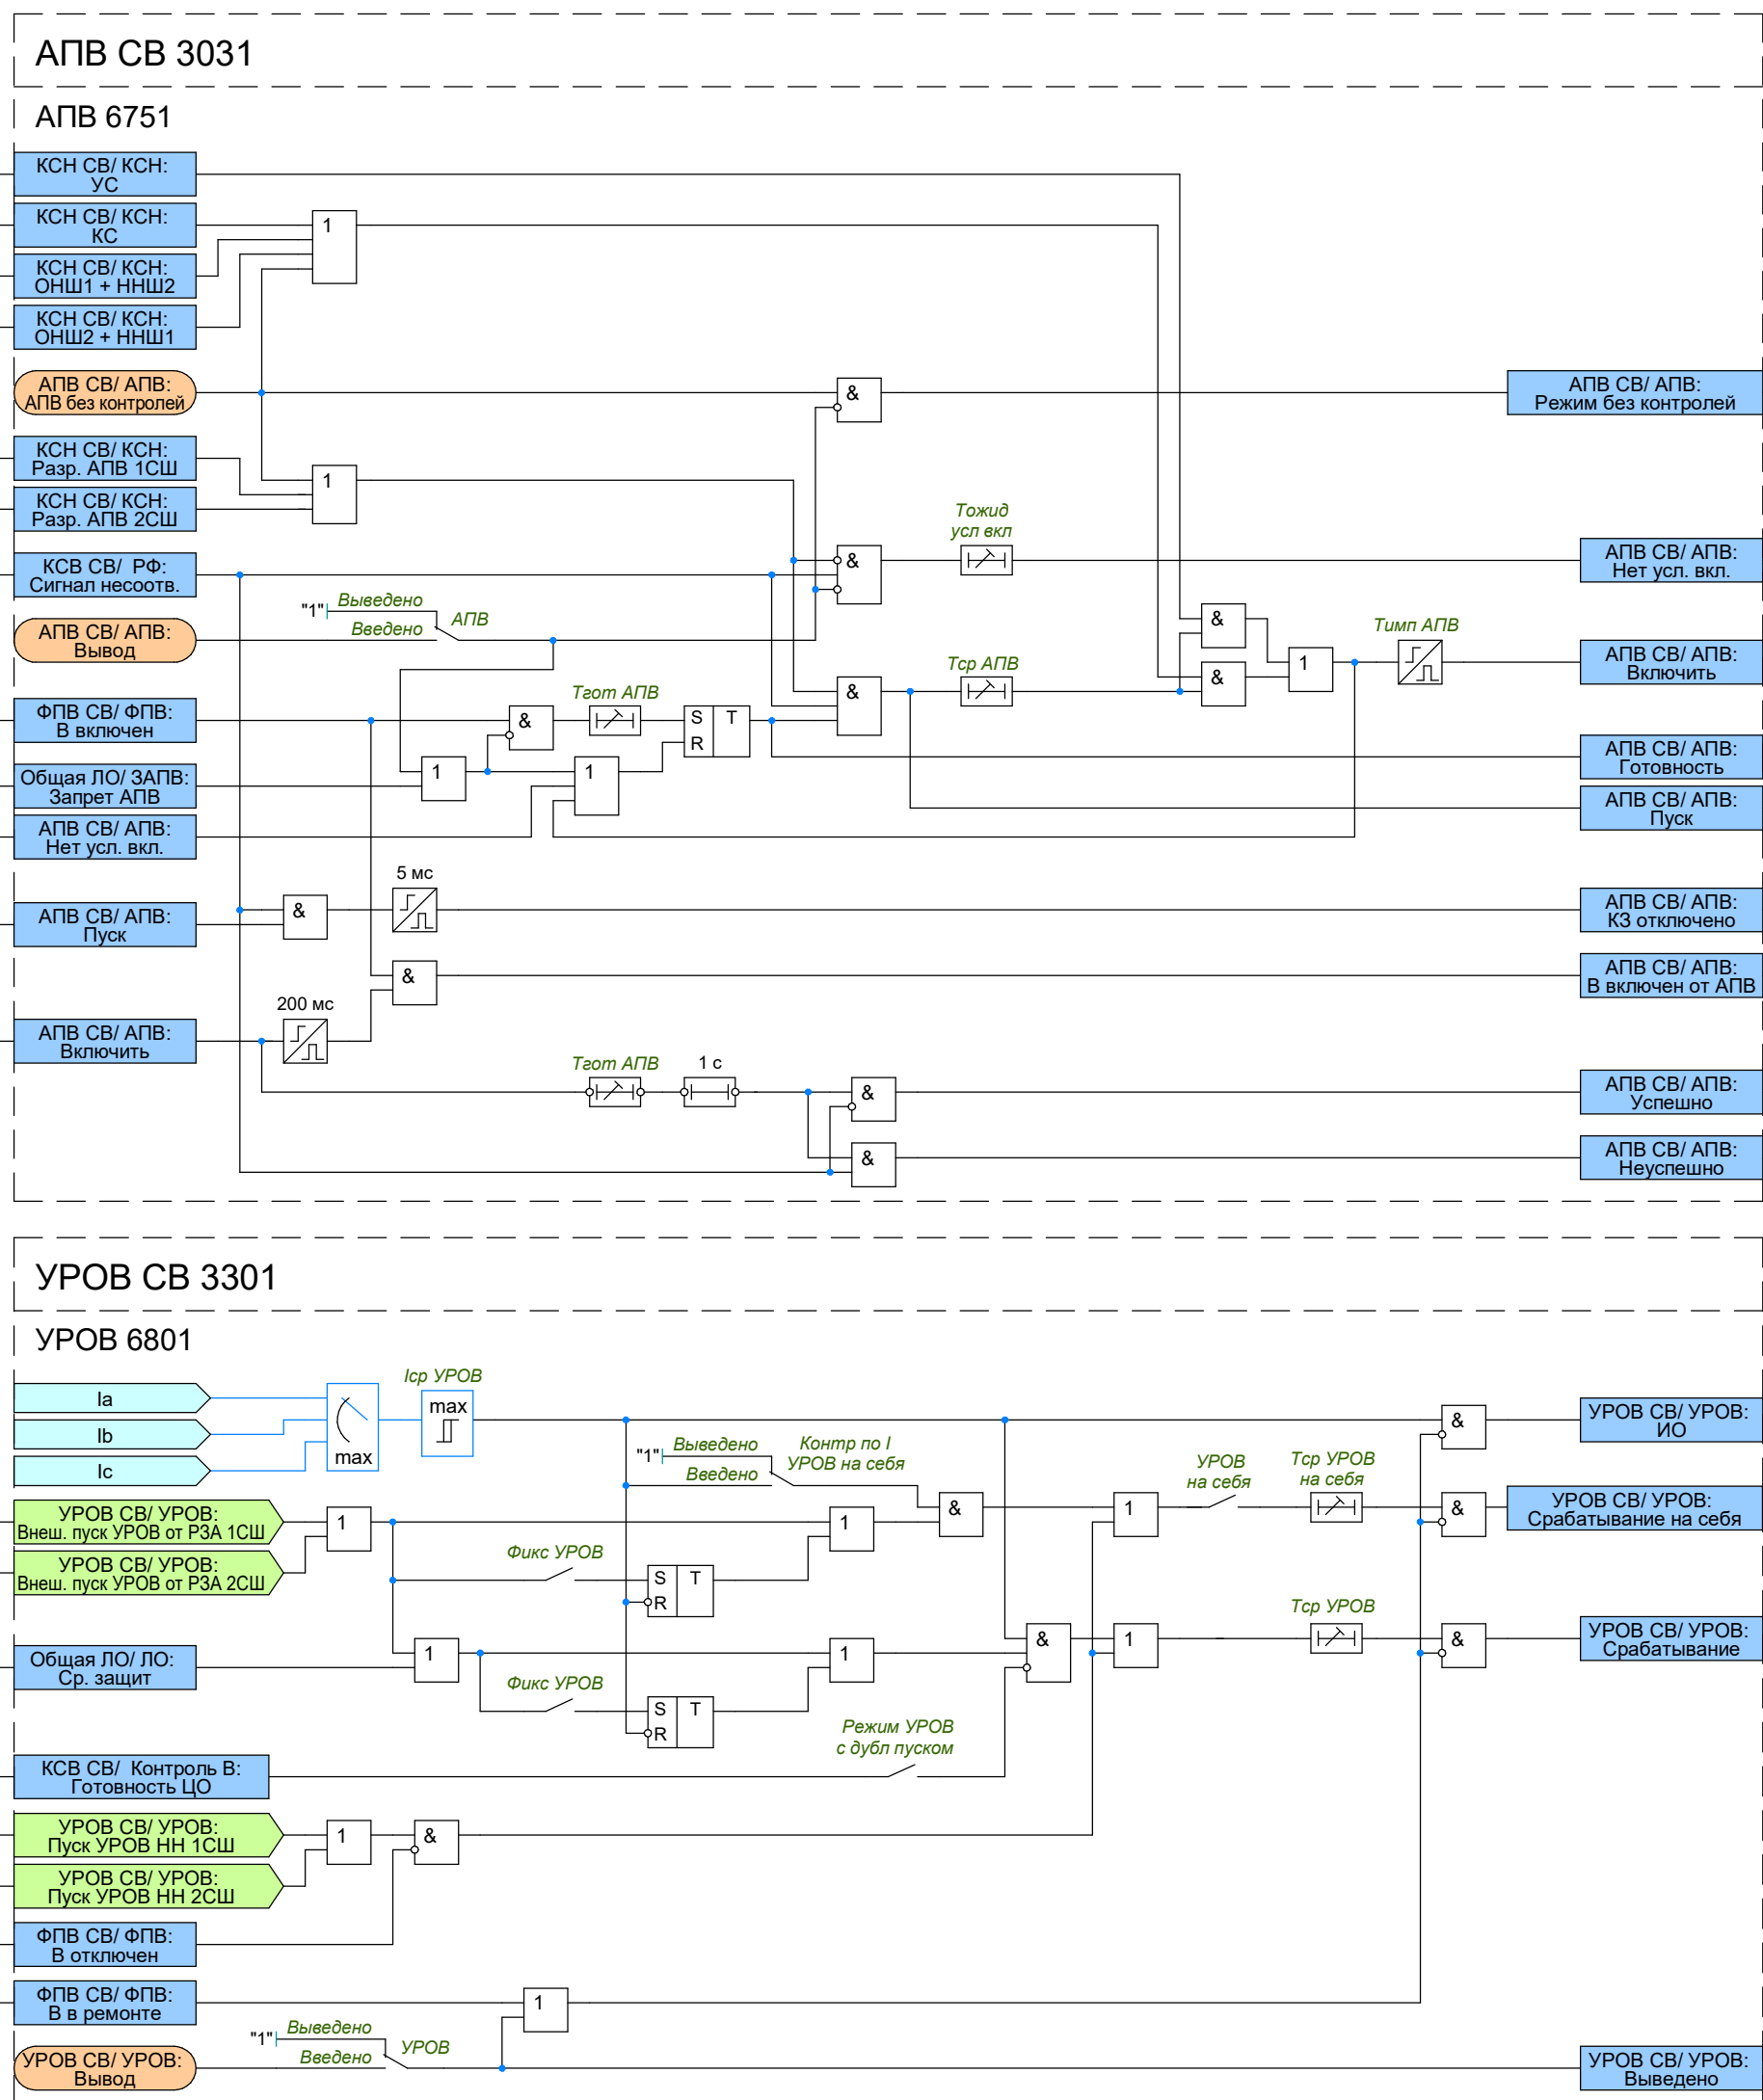


КСВ СВ (Контроль силового выключателя) 3371

Контроль В 6571

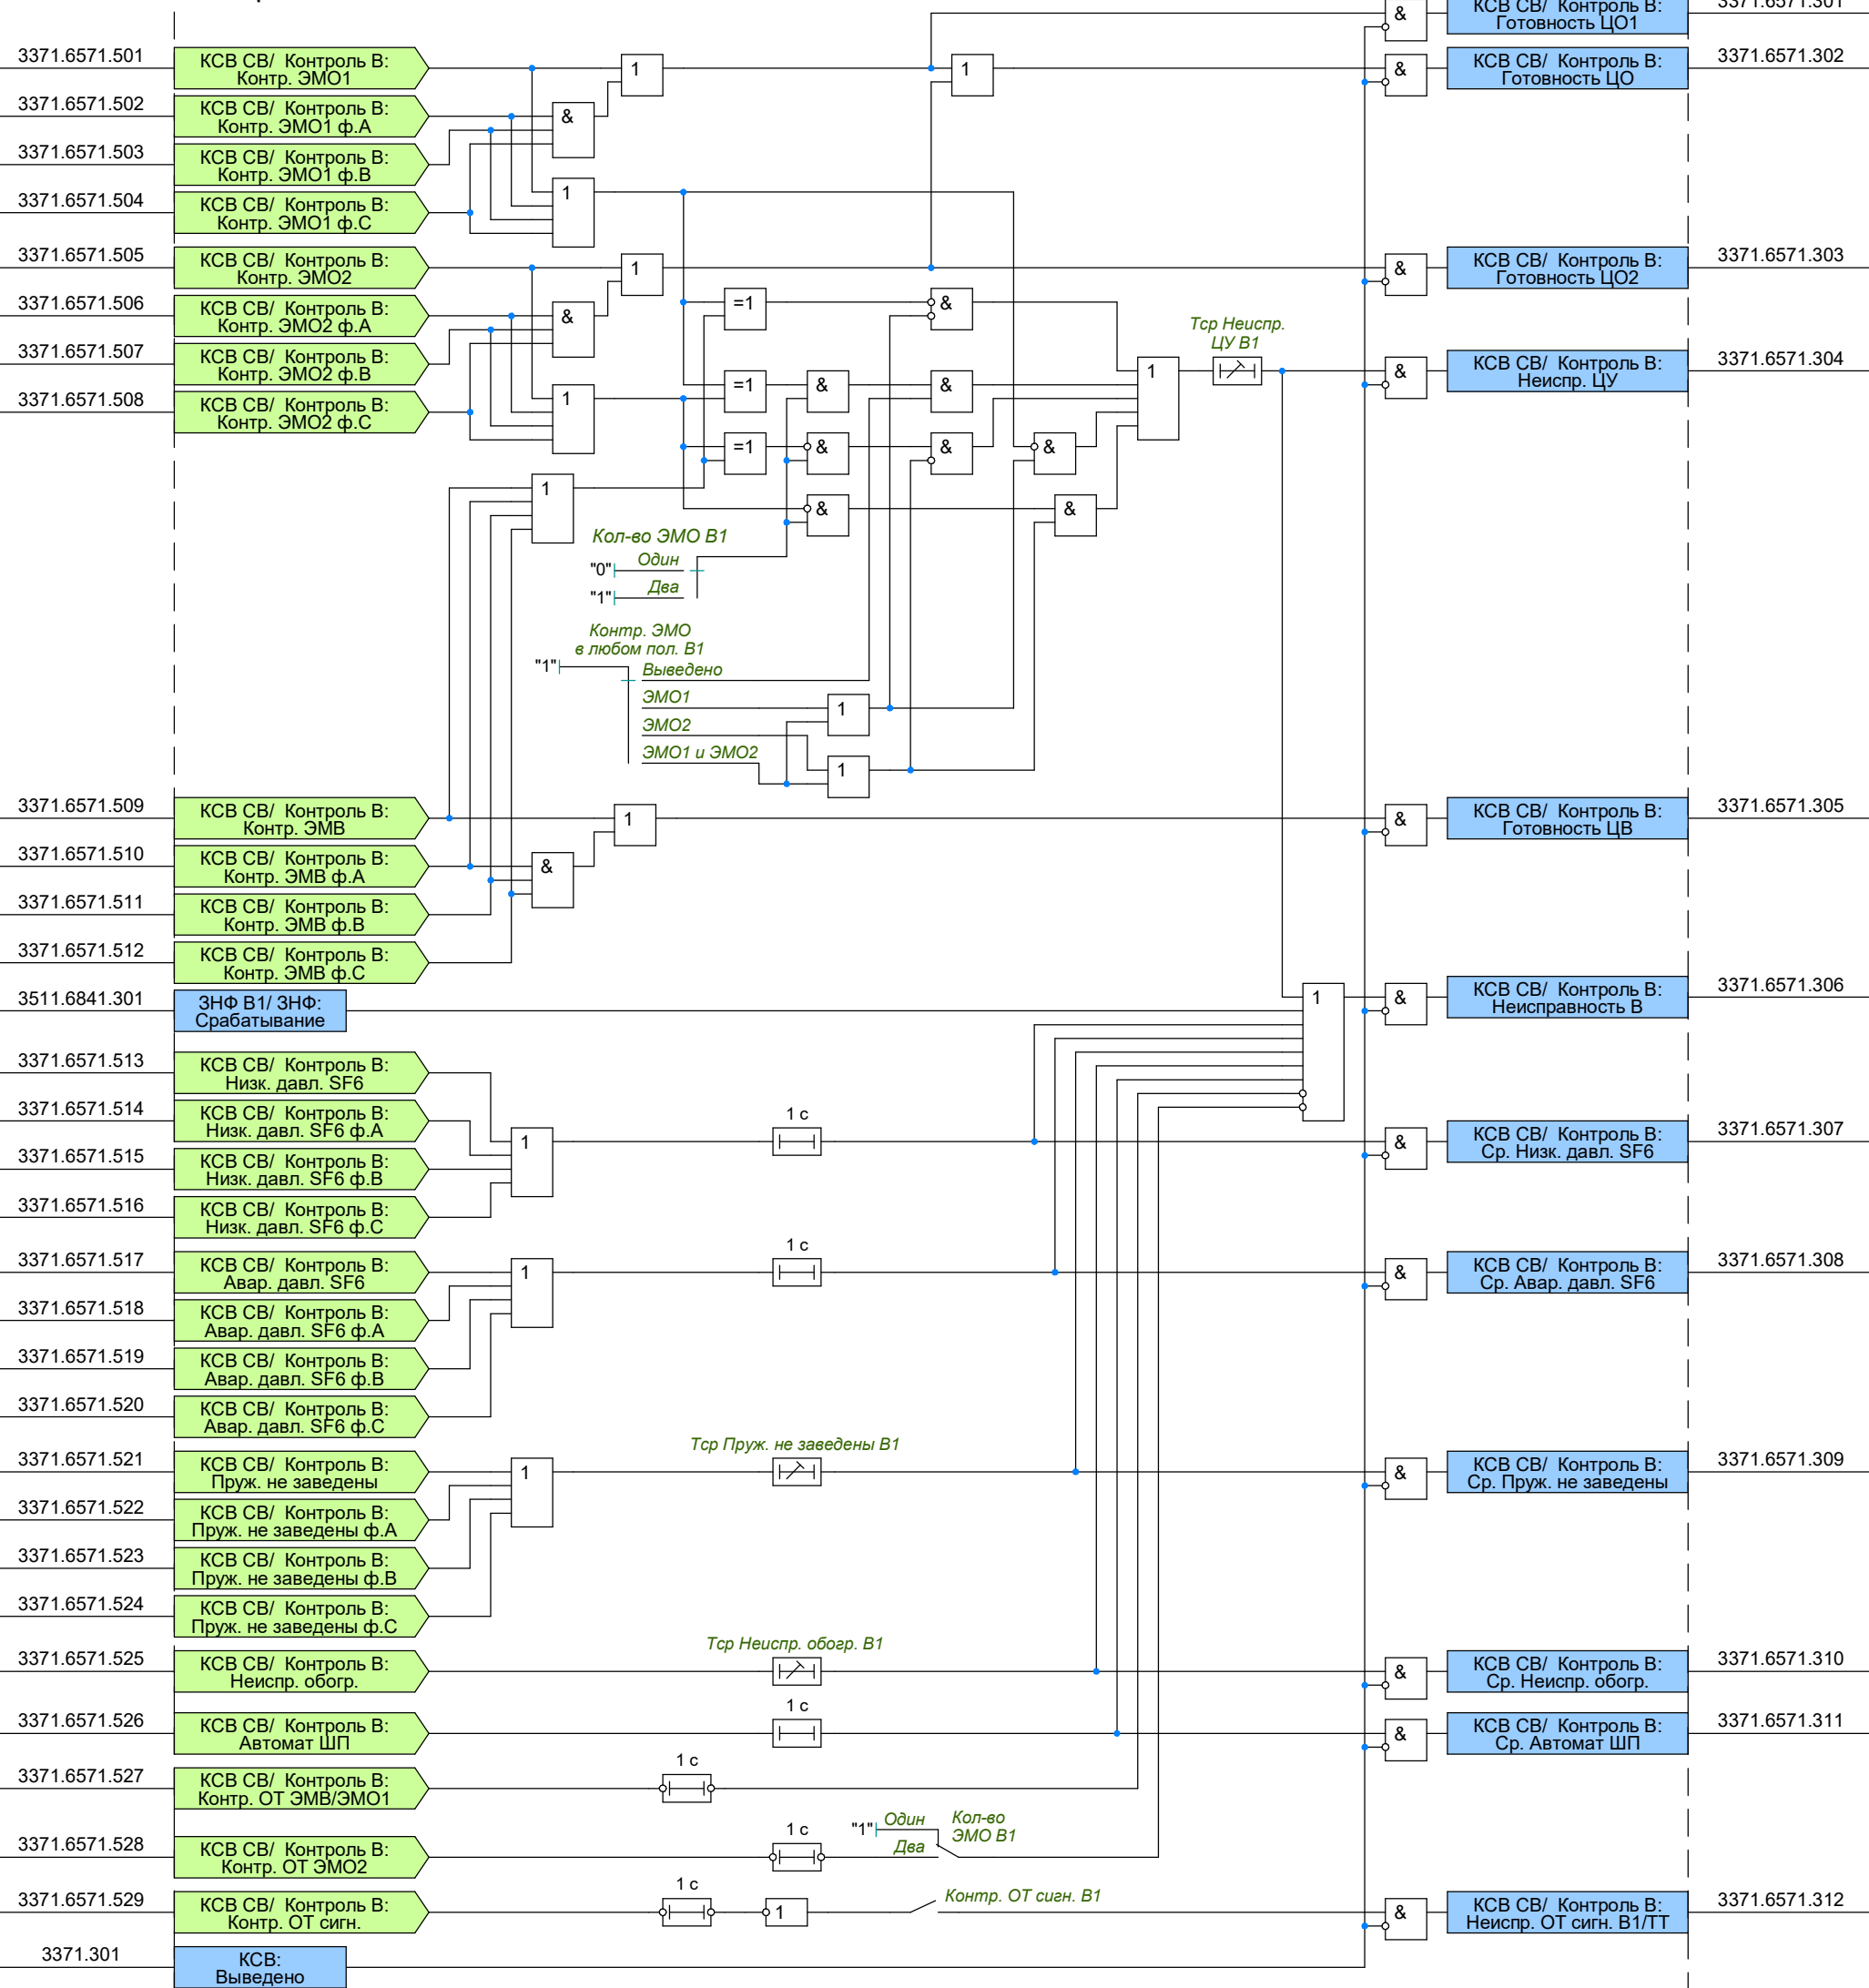


Блокировка управления 6611

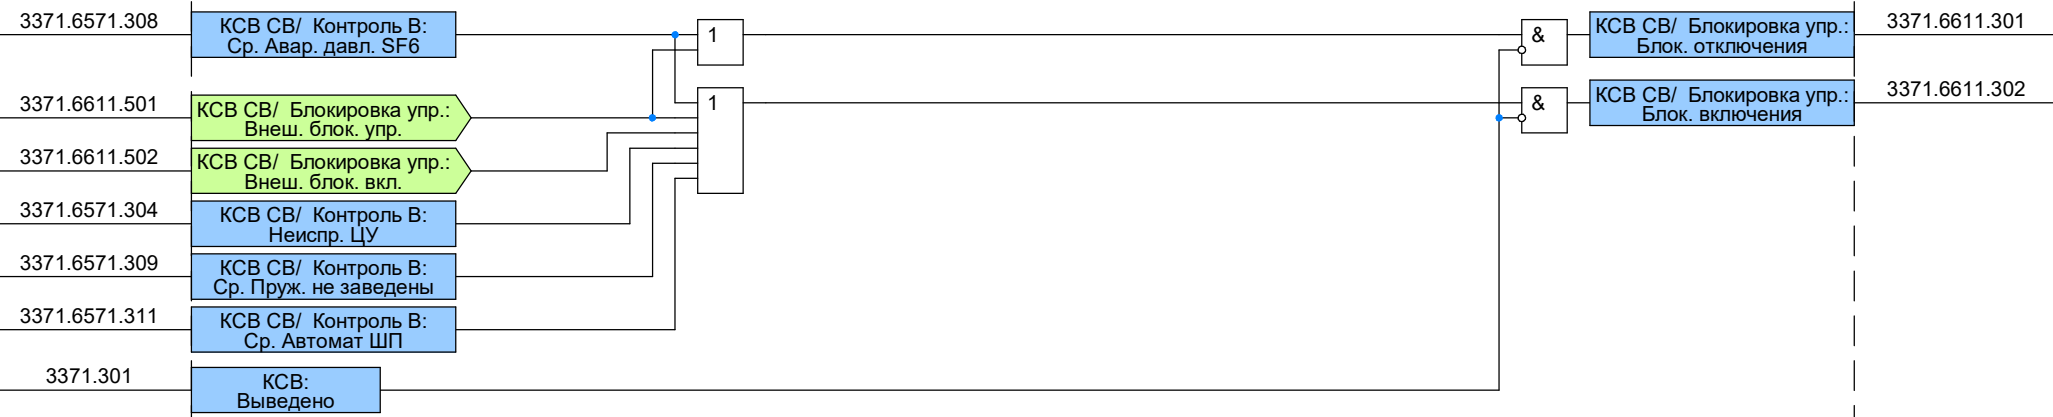


КСВ (Контроль силового выключателя) 3371


Контроль ТТ 6581

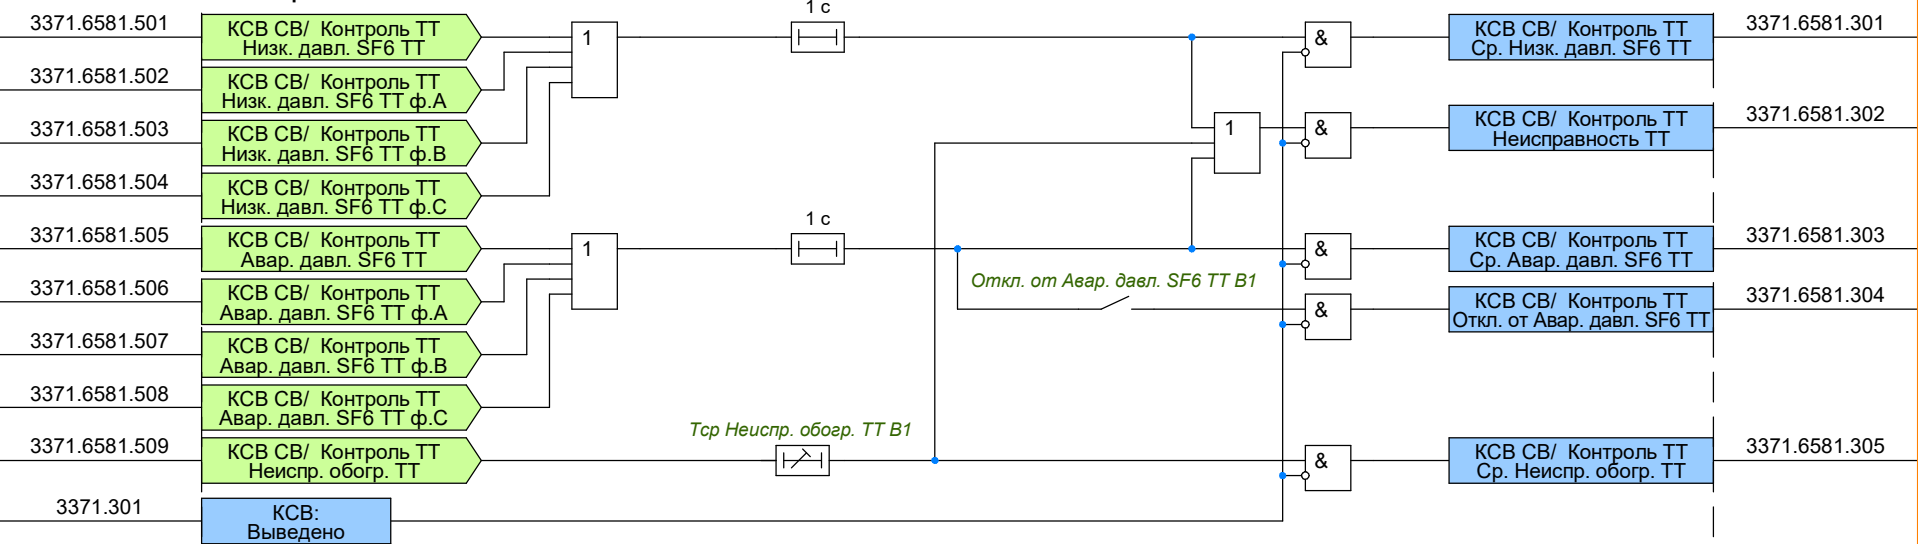

Защита ЭМУ 6601

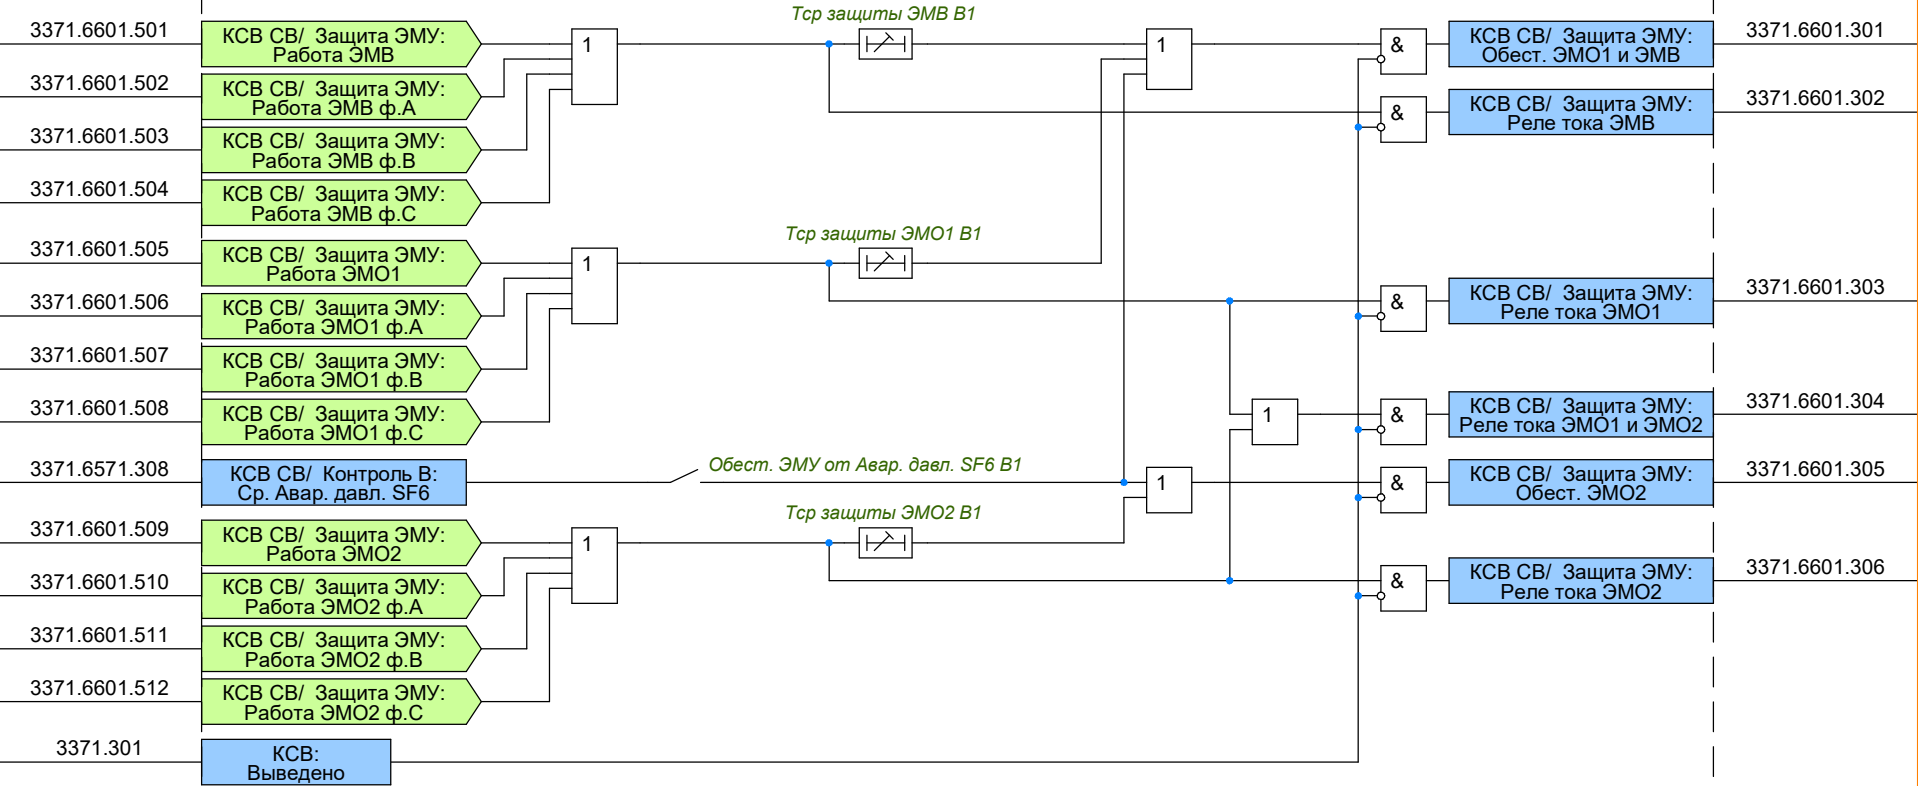


РФ (Реле фиксации) 6621

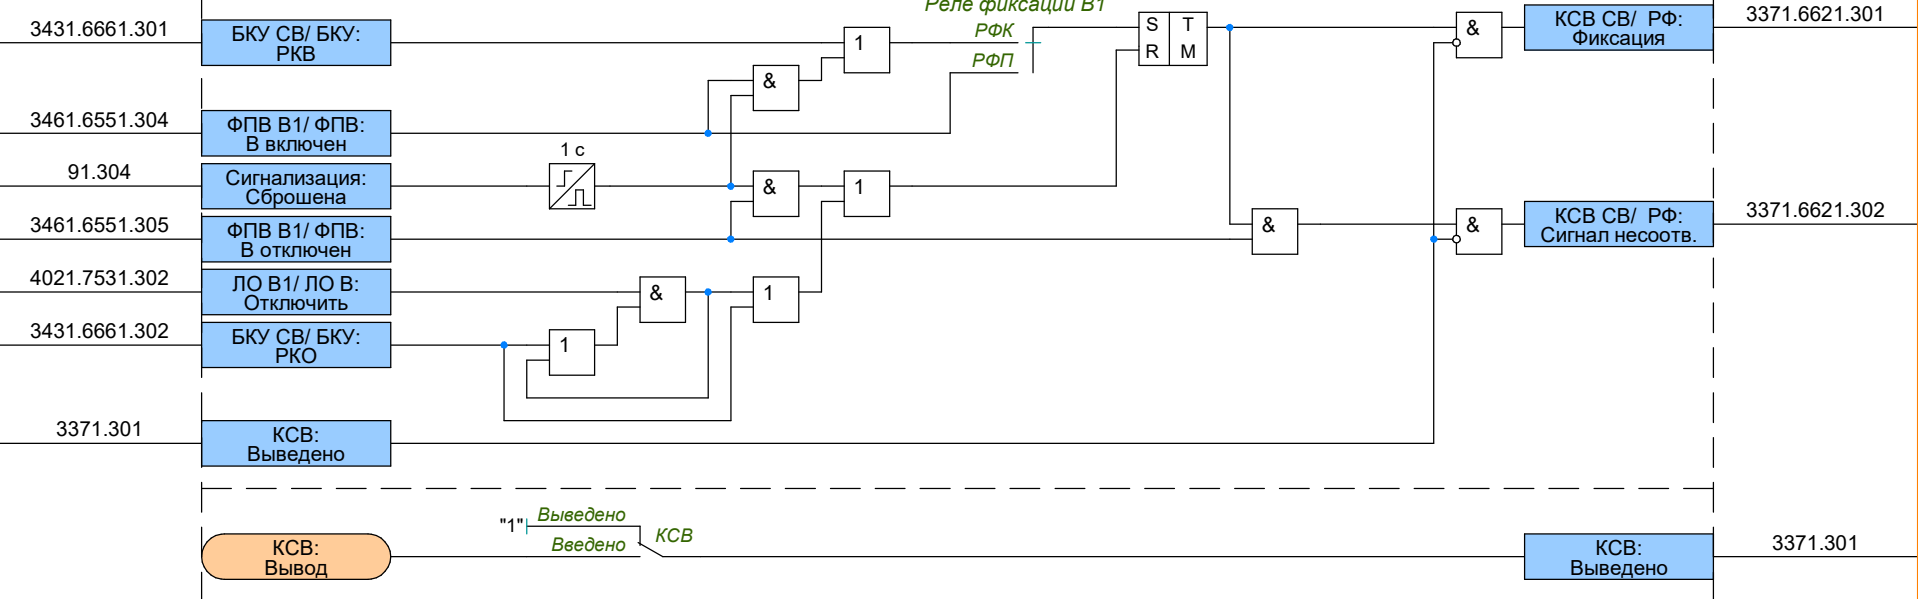


БКУ СВ (Блок команд управления В1) 3431

БКУ 6661

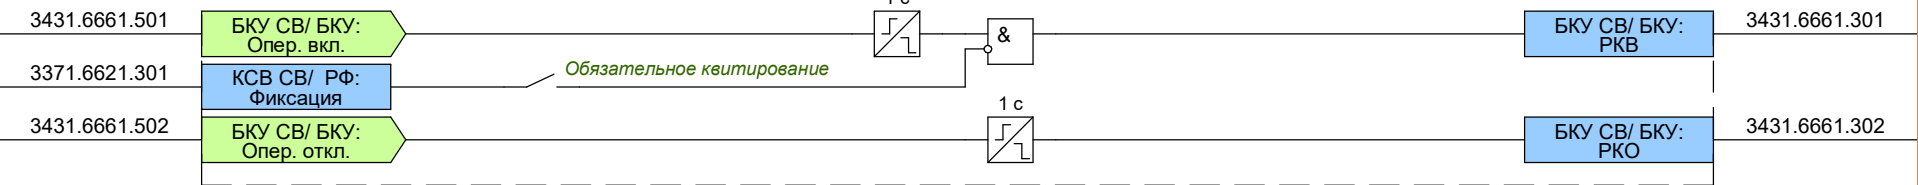


УВ СВ (Управление выключателем) 3561

УВ 6761

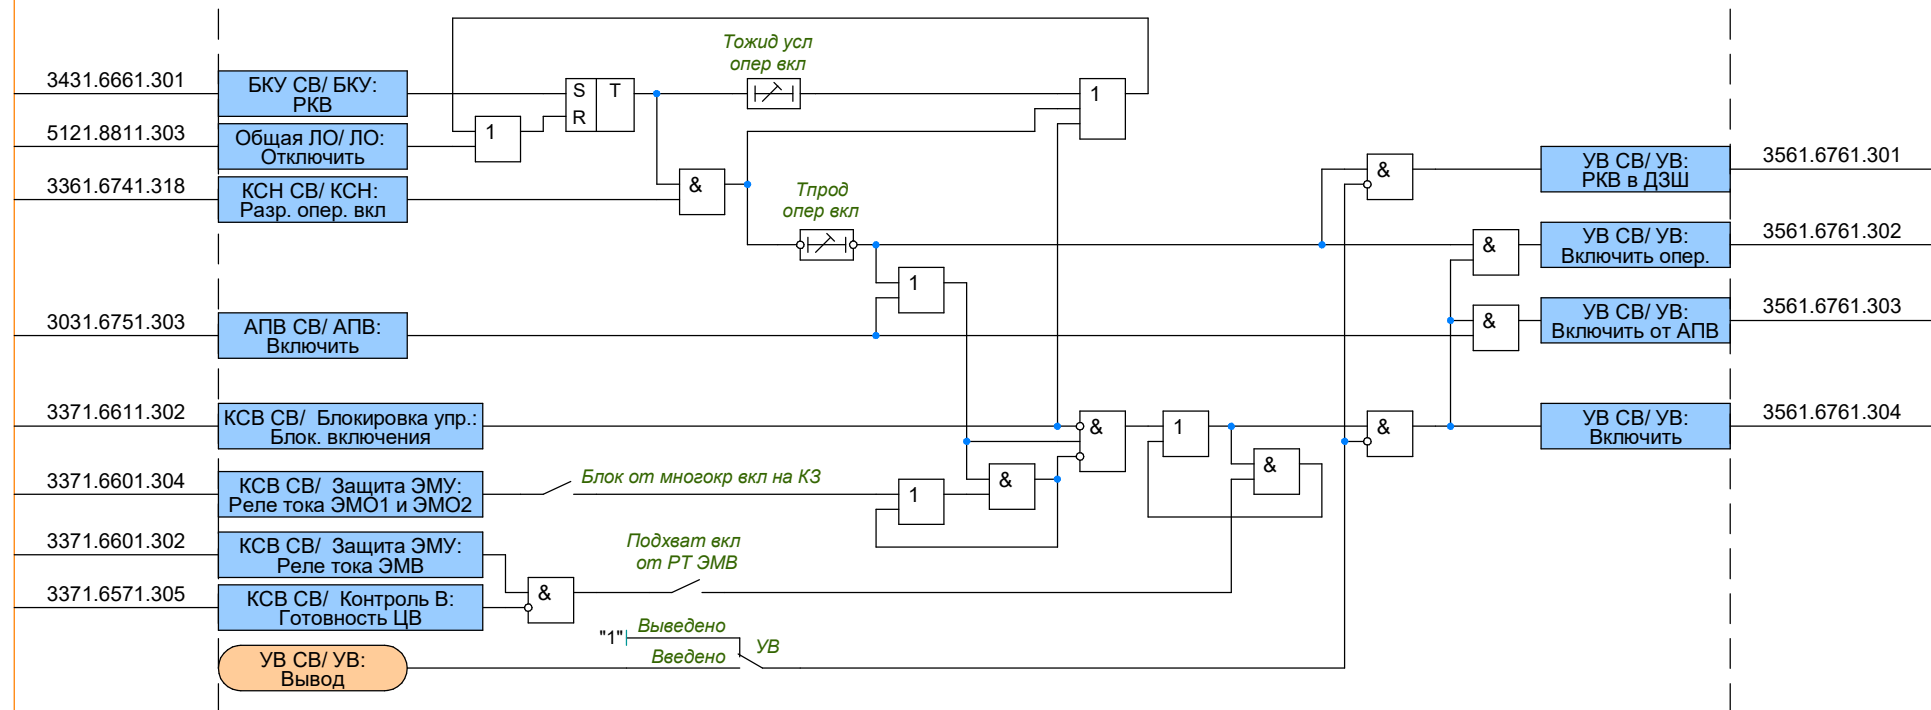


Общая ЛО 5121

ЛО 8811

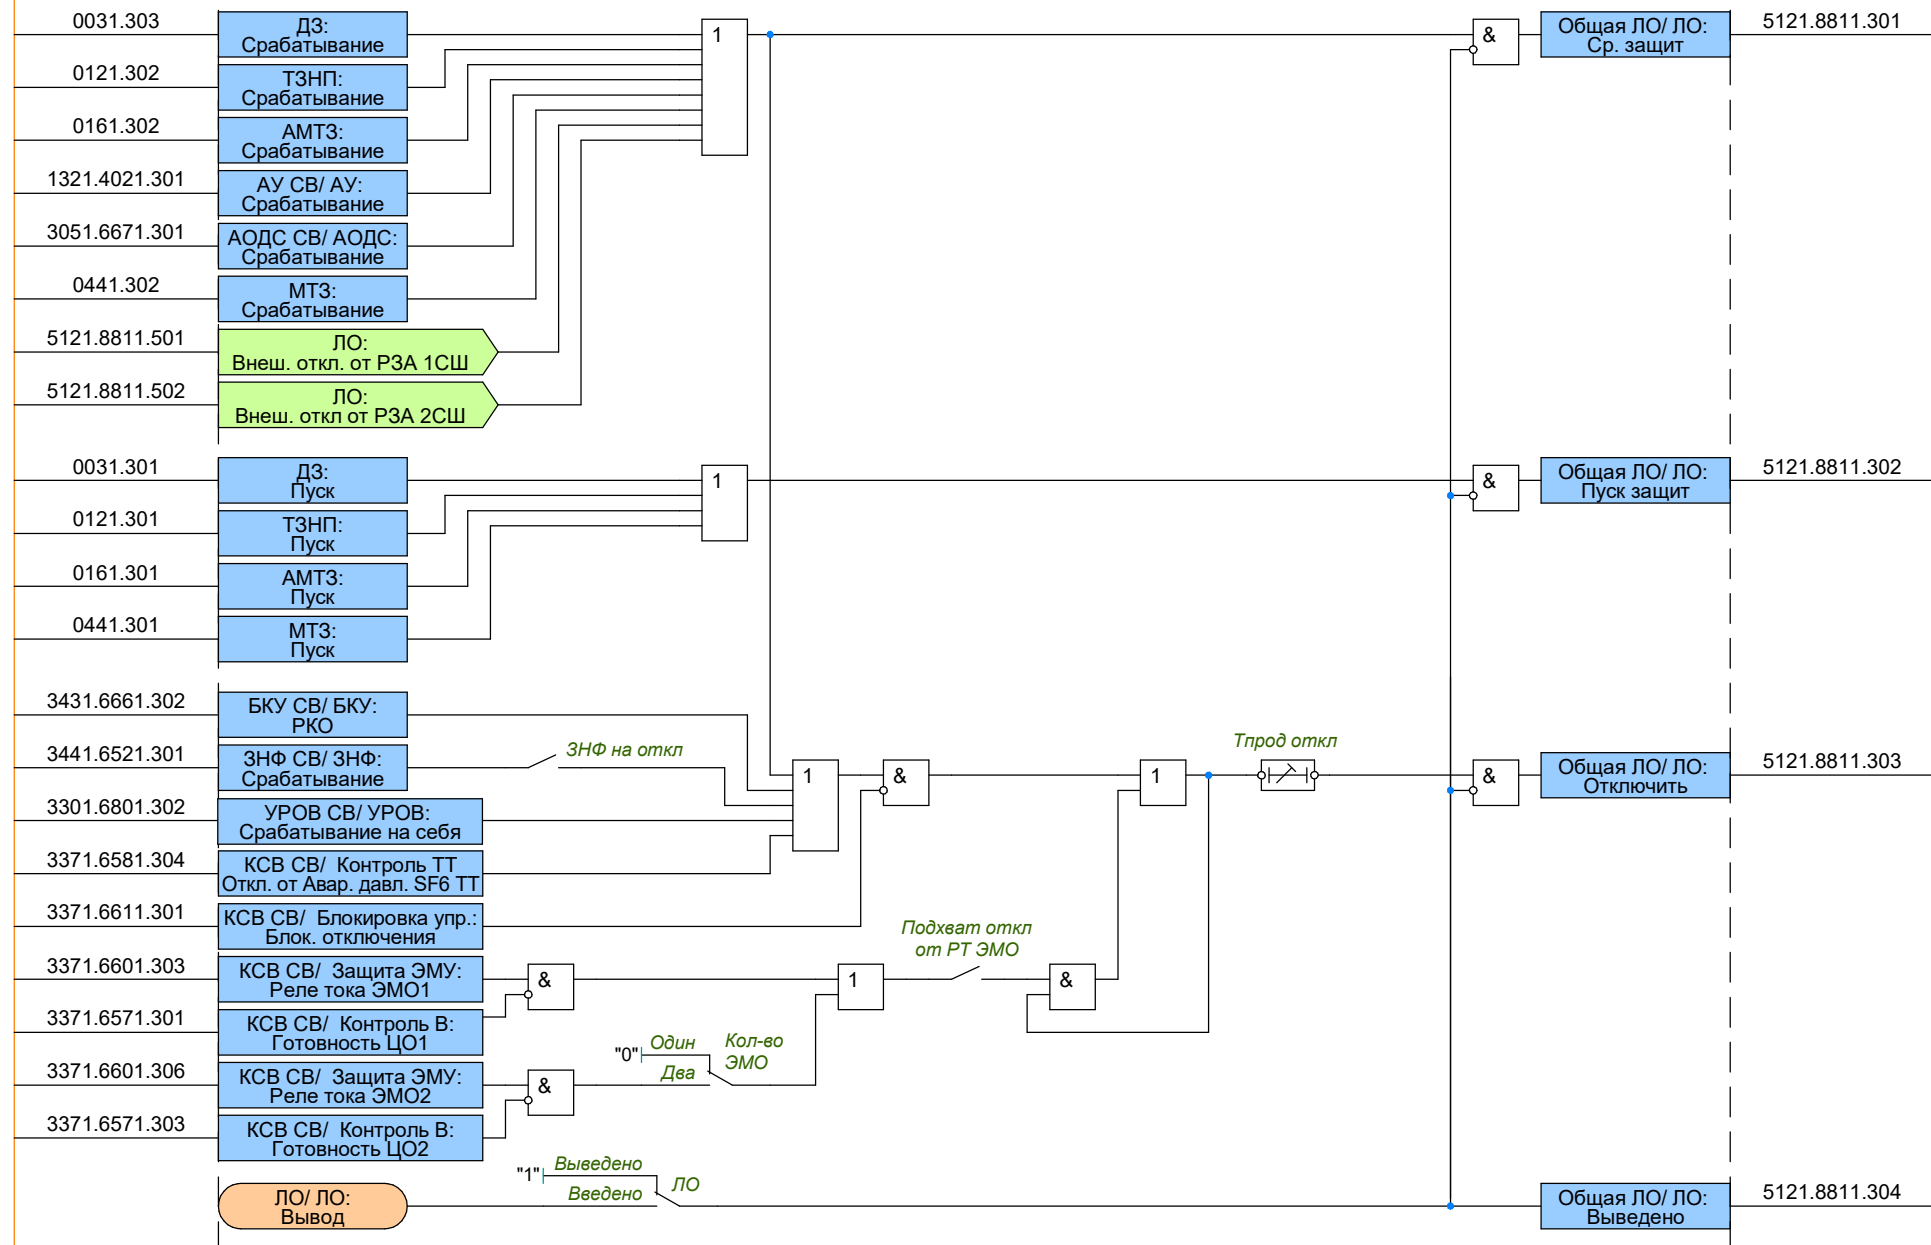


Общая ЛО 5121

ЗАПВ 8821

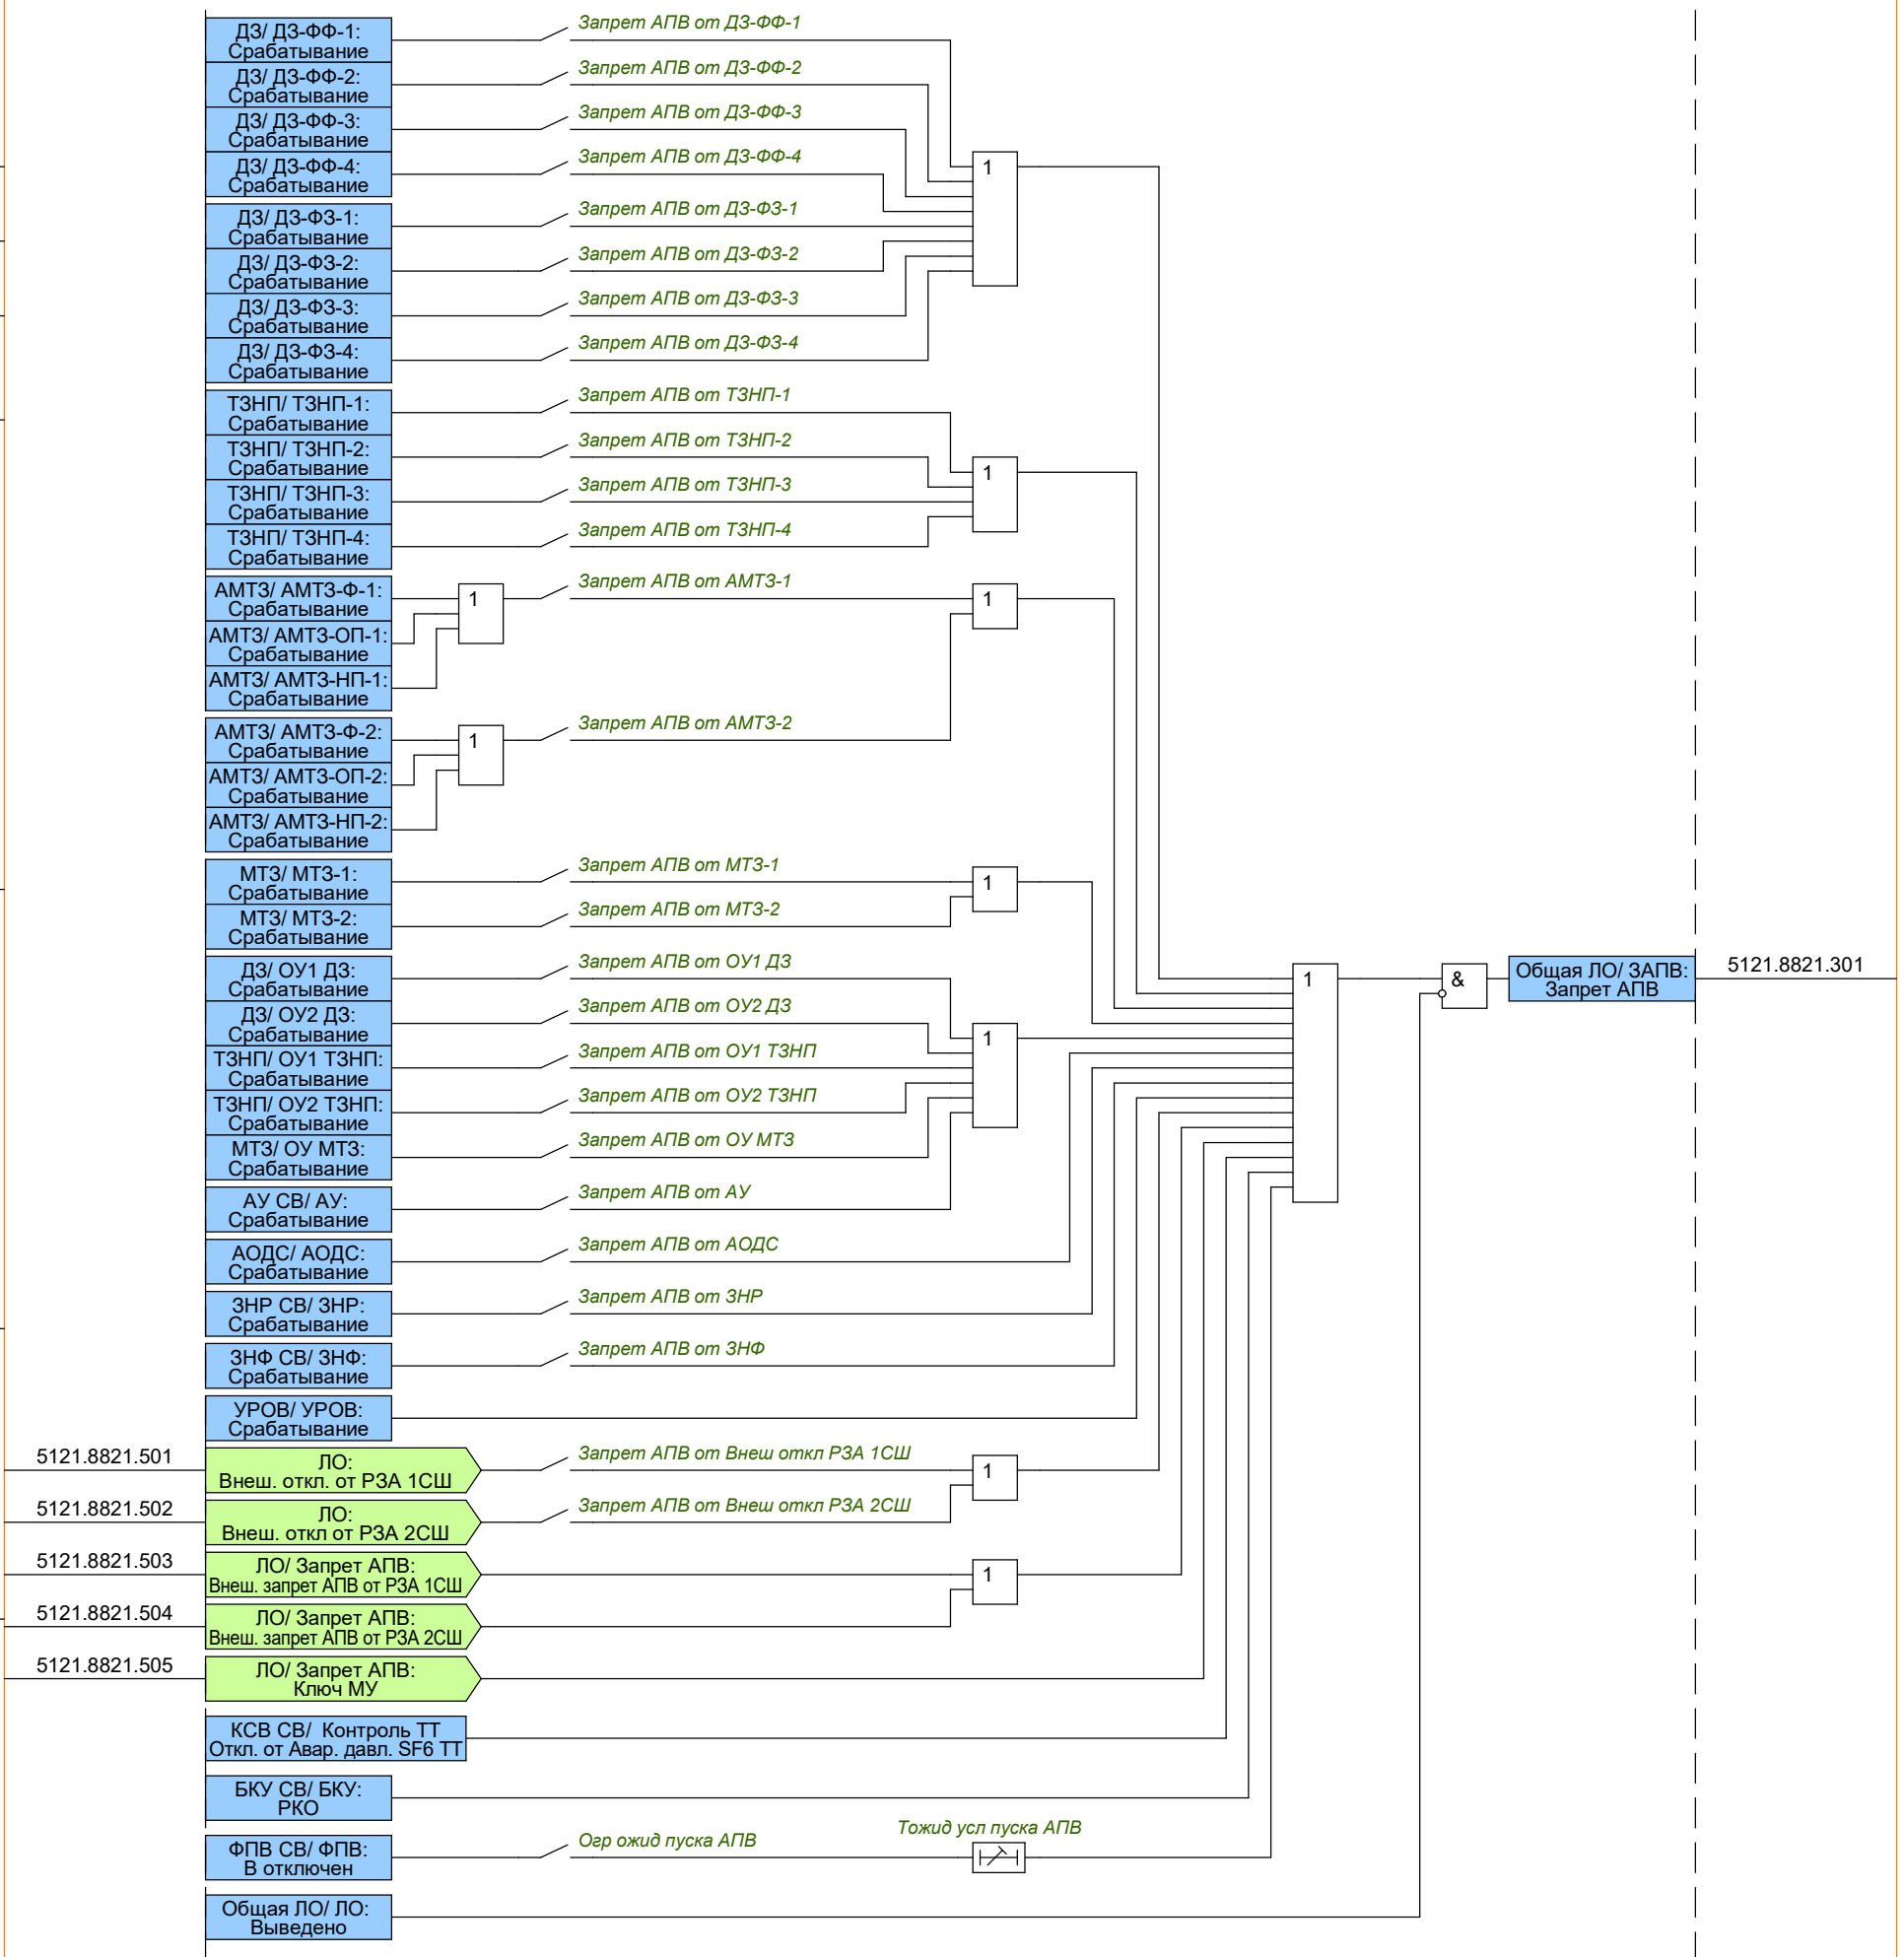


ФПВ СВ (Фиксация положения выключателя) 3461


ФПВ 6551

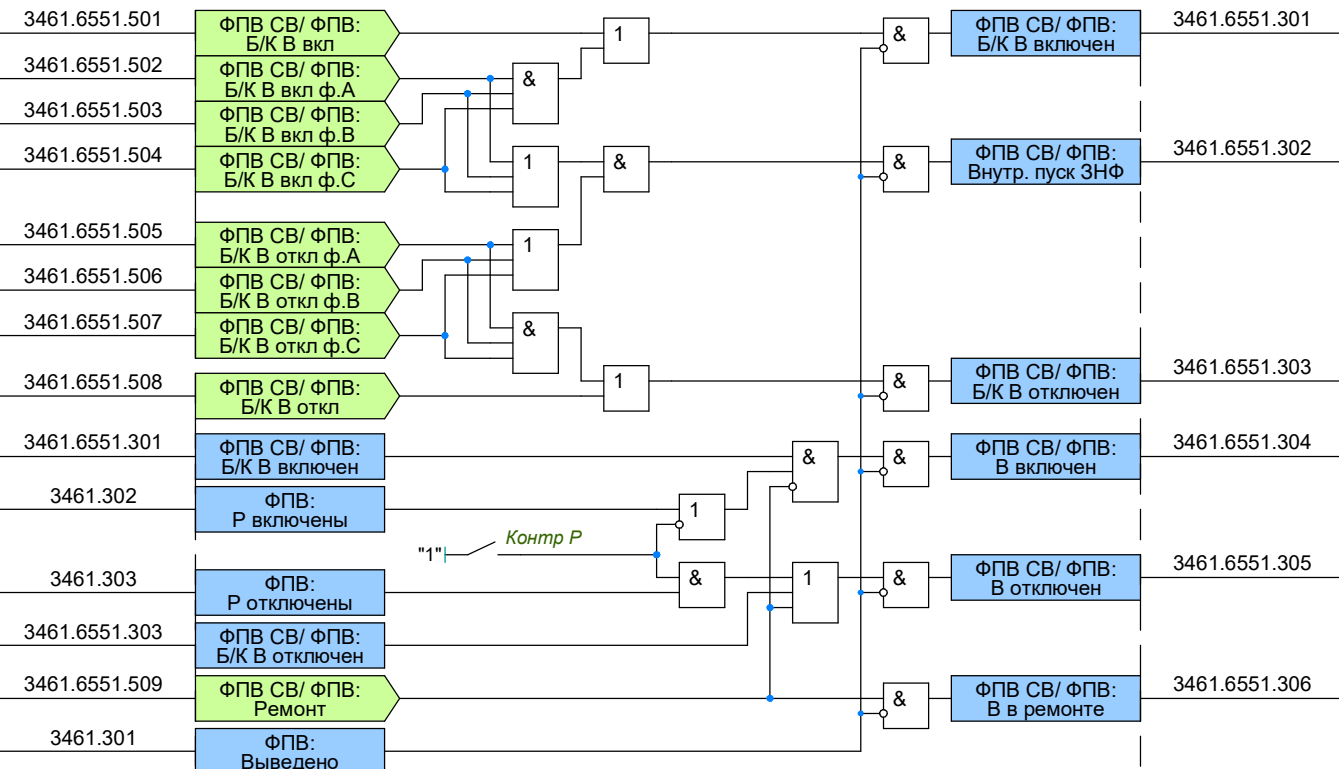


P1 6531

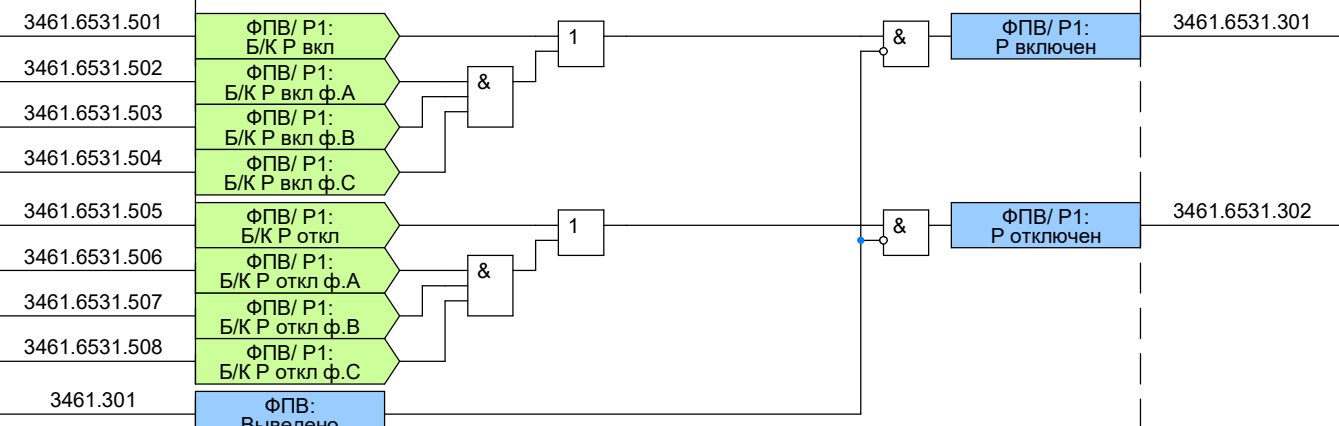

P2 6532

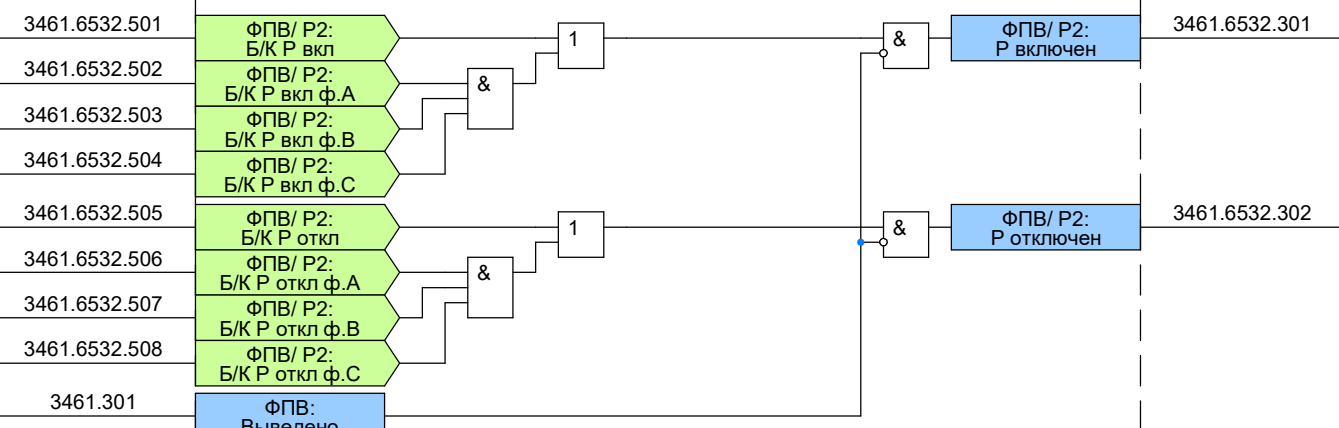


ФПВ: Выведено

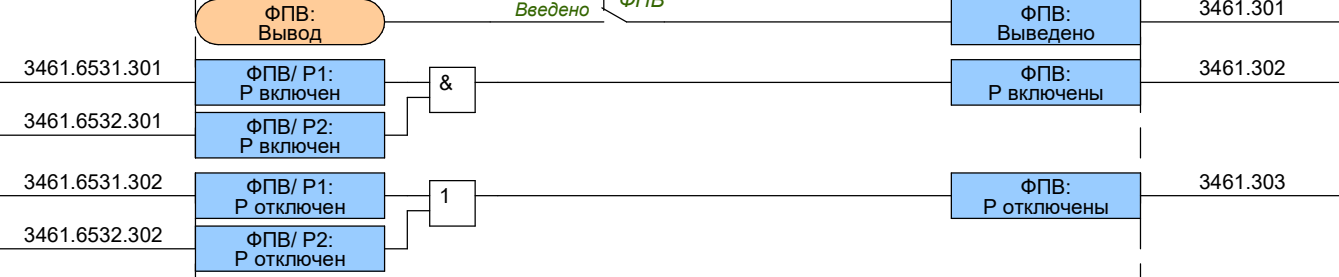


Коммутация

Коммутация

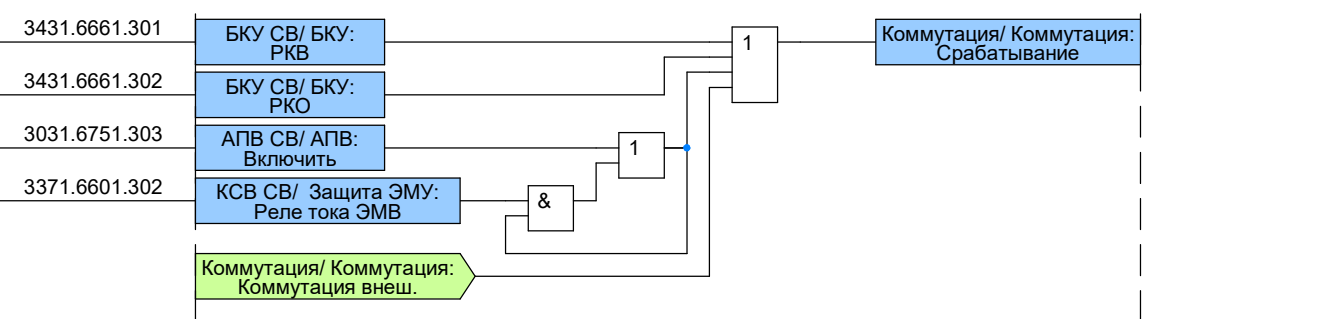

Общая логика

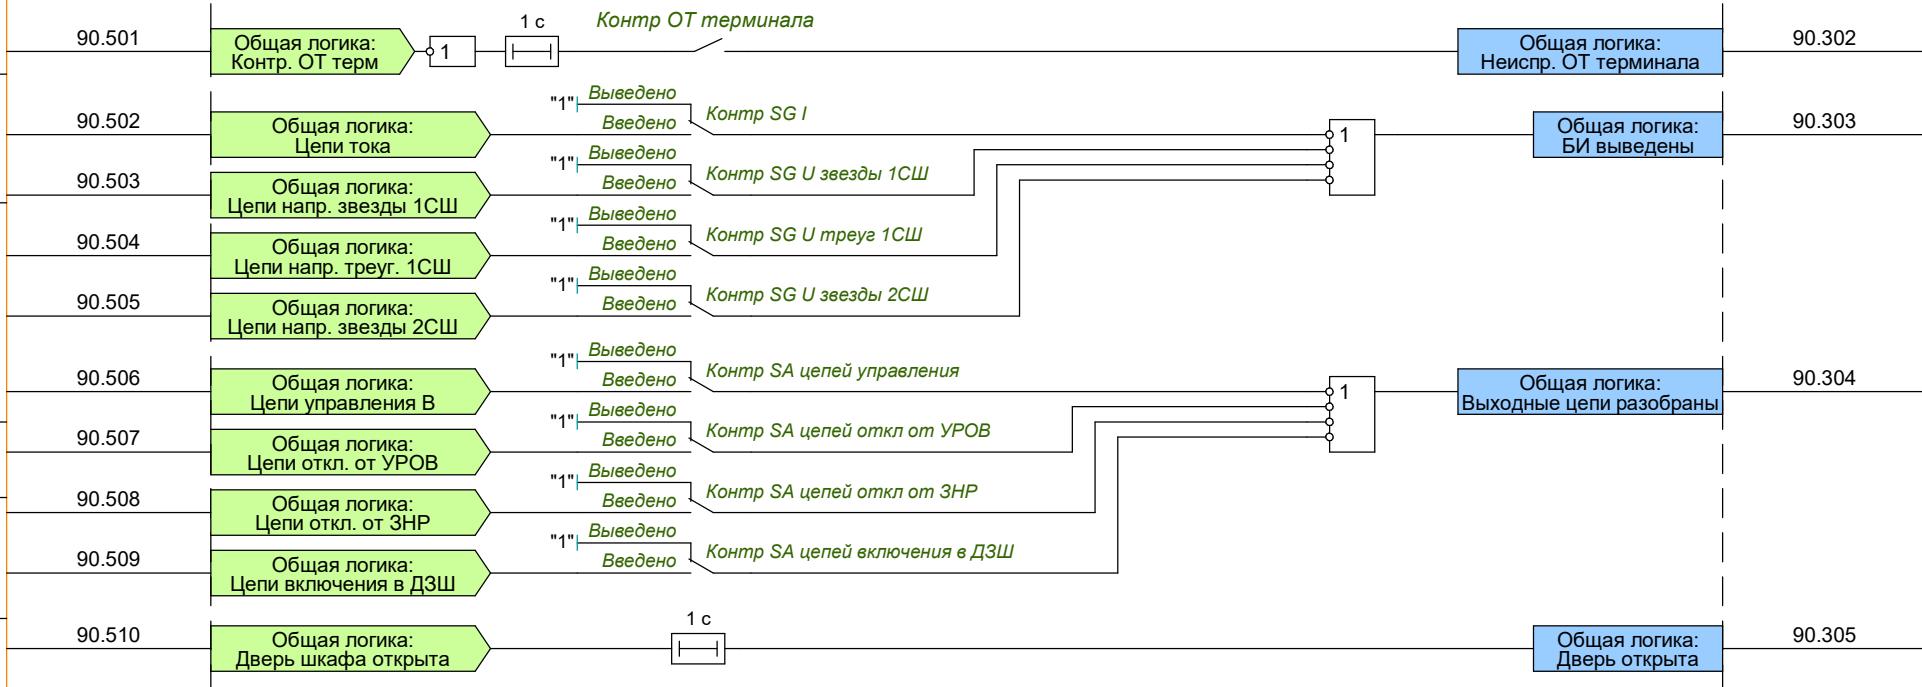

Сигнализация

